แบบขออนุญาต

อาคารพักอาศัยรวม ค.ส.ล. 7 ชั้น

เจ้าของโครงการ

บริษัท ฤทธิกร ลิฟวิ่ง จำกัด

ต.ปลวกแดง อ.ปลวกแดง จังหวัดระยอง

MARCHTEN
ARCHITECTURE / INTERIOR

บริษัท มาร์ชเทน จำกัด
403 ซ.พัฒนาการ 50 สวนหลวง กรุงเทพมหานคร 10250

www.marchtendesign.com
Email:marchtenmanager@gmail.com

04-12-2567

สารบัญแบบสถาปัตยกรรม

แผ่นที่	รายละเอียด	หน้าที่
AR-01	สารบัญแบบ รายการวัสดุ , สัญลักษณ์ประกอบแบบ , สัญลักษณ์อ้างอิง	
AR-02	รายการประกอบแบบ 1	
AR-03	มาตราการเพื่อความปลอดภัยระหว่างการก่อสร้างอาคาร	
AR-04	แบบประกอบผู้พิการ , แผนที่โดยสังเขป	
AP-00	ผังบริเวณ	
AP-01	แบบแปลนพื้นชั้น 1	
AP-02	แบบแปลนพื้นชั้น 2	
AP-03	แบบแปลนพื้นชั้น 3-5	
AP-04	แบบแปลนพื้นชั้น 6	
AP-05	แปลนพื้นห้องใต้หลังคา	
AP-06	แบบแปลนหลังคา	
A-E01	แบบรูปด้าน 1	
A-E02	แบบรูปด้าน 2	
A-E03	แบบรูปด้าน 3	
A-E04	แบบรูปด้าน 4	
A-S01	แบบรูปตัด A	
A-S02	แบบรูปตัด B	
AD-01	แบบขยายบันได (ST-1) , รูปตัด (A) แบบขยายบันได (ST-1)	
AD-02	แบบขยายบันไดหนีไฟ (ST-2)	
AD-03	แบบขยายห้องน้ำ (WC-1),(WC-02),(WC-3)	
AD-04	แบบขยายประตู (1)	
AD-05	แบบขยายประตู (2)	
AD-06	แบบขยายหน้าต่าง	
AD-07	แบบแสดงอุปกรณ์ (1)	
AD-08	แบบแสดงอุปกรณ์ (2)	
AD-09	แบบขยายรางกันตกระเบียง , แปลนขยาย บันไดลิง	
AD-10	แบบขยายบันไดลิง	
A-L01	แบบขยายลิฟท์ (1)	
A-L02	แบบขยายลิฟท์ (2)	
A-L03	แบบขยายลิฟท์ (3)	
A-L04	แบบขยายลิฟท์ (4)	
A-L05	แบบขยายลิฟท์ (5)	
A-L06	แบบขยายลิฟท์ (6)	
A-L07	แบบขยายลิฟท์ (7)	

รายการวัสดุ

งานพื้น

1	พื้น คสล. ทำผิวซีเมนต์ขัดผิวหยาบ
2	พื้น คสล. ปูทับด้วยกระเบื้องแกรนิตโต้ พื้นผิวด้าน ขนาด 60x60 ซม. ระบุรุ่นภายหลัง
3	พื้น คสล.ปรับระดับทำผิวขัดมัน ปูกระเบื้องยาง ระบุรุ่นและชนิดภายหลัง
4	พื้น คสล. ปูทับด้วยกระเบื้องแกรนิตโต้ พื้นผิวด้าน ขนาด 60x60 ซม. ระบุรุ่นภายหลัง
5	พื้นผิวคอนกรีต ค.ส.ล. ทารองพื้นด้วย ARDEX WPM 300 และทาทับผิวกันซึมด้วย ARDEX WPM 950 ของบริษัท ARDEX ติดต่อ คุณตุ๊ก เบอร์ 088-082-8811

งานผนัง

1	ผนังก่ออิฐมวลเบา ฉาบเรียบทาสีรองพื้น TOA สีขาว/ ทาทับด้วยสีทาภายนอก TOA SUPER SHIELD หรือเทียบเท่า
2	ผนังก่ออิฐมวลเบา ฉาบเรียบทาสีรองพื้น TOA สีขาว/ ทาทับด้วยสีทาภายใน TOA SUPER SHIELD หรือเทียบเท่า
3	ผนังก่ออิฐมอญ มอก. ฉาบผิวหน้าลาย กระกระเบื้องแกรนิตโต้ ระบุรุ่น สี ชนิด ภายหลัง

งานฝ้าเพดาน

C0	ฝ้าท้องพื้น ค.ส.ล. ฉาบรอยต่อขัดเรียบ ทาสีรองพื้น TOA สีขาว /ทาทับด้วยสีทาฝ้า TOA SUPER SHIELD
C1	ฝ้าเพดานโครงเคร่าเหล็กชุบสังกะสี SCG เบอร์ 24 กรุยิปซั่มบอร์ดขอบลาด หนา 9 mm. ฉาบรอยต่อขัดเรียบ/ ทาสีรองพื้น TOA สีขาว /ทาทับด้วยสีทาฝ้า TOA SUPER SHIELD
C2	ฝ้าเพดานโครงเคร่าเหล็กชุบสังกะสี SCG เบอร์ 24 กรุยิปซั่มบอร์ดขอบลาด หนา 9 mm. (ทนความชื้น) ฉาบรอยต่อขัดเรียบ/ ทาสีรองพื้น TOA สีขาว /ทาทับด้วยสีทาฝ้า TOA SUPER SHIELD

งานหลังคา

หลังคาโครงเหล็ก ติดตั้งแผ่นหลังคา Metal Sheet ของ Bluescope Steel ลอนมาตรฐาน(ลอน760)
เคลือบอลูซิงค์หนา 0.50 มม. หน้ากว้าง 76 ซม.

หมายเหตุ

รายการใดมีข้อสงสัย ระบุไม่ชัดเจน หรือรายละเอียดไม่เพียงพอ ให้ปรึกษาสถาปนิกหรือวิศวกรผู้รับผิดชอบก่อนดำเนินการก่อสร้างต่อไป ถ้าลักษณะแบบมีการขัดแย้งในส่วนของแบบสถาปัตยกรรมกับแบบในหัวข้ออื่นๆ ให้ยึดแบบสถาปัตยกรรมเป็นหลักในการดำเนินงานต่อ โดยผ่านการอนุมัติจากสถาปนิกหรือวิศวกรผู้รับผิดชอบ

รายการวัสดุและอุปกรณ์ที่ระบุในแบบ ถ้าไม่สามารถหาได้ในท้องตลาดให้ใช้ผลิตภัณฑ์ที่มีคุณภาพเทียบเท่า

สัญลักษณ์วัสดุ

ถมดิน
คอนกรีตเสริมเหล็ก
ผนังฉาบปูนเรียบ
คอนกรีตบล็อค
ผนังก่ออิฐ
อลูมิเนียมหรือเหล็ก
ผนังไม้ไสเรียบ
ไม้ไม่ไส
ยิปซั่มบอร์ด
กรวดล้าง
โครงเคร่าไม้
โครงเคร่าเหล็ก
กระจก

สัญลักษณ์แบบ

A / A-03 — A / A-03 รูปตัด A-A แสดงโนแผ่นที่ A-03

3 A-113 / 2 A-112 / 4 A-114 / 1 A-111 ทิศทางแสดงการมองรูปด้าน ตัวอักษรแสดงในบนแผ่นที่ A-04

SA / A-04 รูปด้าน SA แสดงในบนแผ่นที่ A-04

1 / A-04 แบบขยาย D1 แสดงในบนแผ่นที่ A-04

ห้องนอน 1 / EL.+0.60 | 7 | 1 — แสดงชื่อห้อง; EL. = ELEVATION, CH. = CEILING HEIGHT; แสดงวัสดุผ้าเพดาน; แสดงวัสดุพื้น; แสดงระดับพื้น

EL.+0.20 เส้นแสดงระดับ ระดับ

B — 2 แสดงแนวเสา

1.39 เส้นแสดงระยะจากริมถึงริม

1.39 เส้นแสดงระยะจากกึ่งกลางถึงริม

1.39 เส้นแสดงระยะจากกึ่งกลางถึงกึ่งกลาง

เส้นบอกรายละเอียด

45° เส้นบอกองศา

7 แสดงวัสดุพื้น

7 แสดงวัสดุผนัง

1 แสดงวัสดุผ้า

D3 แสดงชนิดประตู

W1 แสดงชนิดหน้าต่าง

N แสดงทิศเหนือ

PROJECT NUMBER : VC2023-024

PROJECT

MACHI RESIDENCES

อาคารพักอาศัยรวม ค.ส.ล 7 ชั้น

OWNER

บริษัท ฤทธิกร ลิฟวิ่ง จำกัด

ARCHITECT :

อัคคะภัทร์ จิระอารีย์บุตร ส-สถ.3040

403 ซ.พัฒนาการ 50 พัฒนาการ

กรุงเทพมหานคร 10250

INTERIOR DESIGNER :

-

STRUCTURAL ENGINEER :

นายพงษ์ธวิทย์ คฑาวุธเจริญกุล สย.12291

ELECTRICAL ENGINEER :

นายภาคภูมิ คำพิทูรย์ สพก.5587

MECHANICAL ENGINEER :

SANITARY ENGINEER :

นส.อรวรรณ พลตรี สส.134

DRAWING TITLE

สารบัญแบบ ,รายการวัสดุ

DRAWING FOR CONSTRUCTION

DRAW BY :	CHECKER :	REVISION :
Weerayuth L.	Akapatr C.	-

SCALE :

DRAWING NO. A-R01

DATE : 04-12-2024

FILE NAME :

JOB NO.

REVISION	DESCRIPTION

GERNERAL NOTE
DO NOT SCALE DRAWING ALL MEASUREMENT MUST BE CHECKED AT THE SIDE BY THE CONTRACTOR
ALL DESIGN AND DRAWINGS ARE THE PROPERTY OF MARCHTEN CO.,LTD
AND NOT BE USED WITH OUT THEIR WRITTEN PERMISSION

MARCHTEN
ARCHITECTURE / INTERIOR
บริษัท มาร์ชเทน จำกัด
403 ซ.พัฒนาการ 50 สวนหลวง กรุงเทพมหานคร 10250

รายการประกอบแบบ ।

1. การดำเนินการทั่วไป

1.1 ผู้รับจ้างจะต้องทำความเข้าใจกับแบบทั้งหมด ตลอดจนเอกสารประกอบสัญญา ให้เข้าใจถี่ถ้วนเสียก่อนที่จะเริ่มทำการก่อสร้างเพื่อจะสำดับงานได้ถูกต้อง ไม่ผิดพลาด ป้องกันปัญหาที่อาจจะเกิดขึ้น

1.2 รายละเอียดต่างๆและแบบขยายที่ให้ไว้ตามแบบ อาจเปลี่ยนแปลงไปตามความเหมาะสมกับสภาพที่เป็นจริงในงานก่อสร้าง รวมถึงรายการหรือรายละเอียดที่ไม่ได้แสดงไว้ ซึ่งจะได้กำหนดให้ในการก่อสร้างอีกครั้งหนึ่ง ในกรณีที่รูปแบบรายการหรือแบบขยายเกิดการขัดแย้ง หรือไม่สามารถทำตามรูปแบบ รายการหรือแบบขยายได้ ให้ผู้รับจ้างเสนอปัญหาให้ผู้ออกแบบทราบ เพื่อพิจารณาตัดสินตามหลักวิชาช่าง ประโยชน์ใช้สอยความมั่นคงแข็งแรงและความสวยงาม หรือให้ถือว่าส่วนที่ดีกว่าถูกต้องกว่า เลือกวัสดุที่มีคุณภาพดีกว่าครบถ้วนกว่าเป็นเกณฑ์ ซึ่งผู้รับจ้างจะต้องปฏิบัติตามอย่างเคร่งครัด ทั้งนี้ไม่ถือว่าเป็นการเปลี่ยนแปลงรายการก่อสร้างแต่อย่างใด

1.3 วัสดุอุปกรณ์ที่ใช้กับอาคารหลังนี้ผู้รับจ้างจะต้องทำตามที่ระบุในแบบและรายการโดยจะต้องนำหรือทำตัวอย่างมาให้ผู้ออกแบบพิจารณาเห็นชอบเสียก่อน จึงจะนำมาใช้ได้ การขอใช้วัสดุเทียบเท่า ผู้รับจ้างสามารถกระทำได้โดยเสนอต่อผู้ออกแบบพิจารณา พร้อมตัวอย่างและเอกสารประกอบ ในกรณีที่ผู้ออกแบบเห็นว่าวัสดุหรืออุปกรณ์นั้นจำเป็นต้องมีการทดสอบคุณสมบัติเพื่อเป็นข้อมูลเพิ่มเติมในการพิจารณา ผู้รับจ้างจะต้องเป็นผู้ดำเนินการตามที่ผู้ออกแบบแจ้งให้ทราบ โดยมีผู้รับจ้างเป็นผู้ออกค่าใช้จ่ายเองทั้งสิ้น ผู้รับจ้างต้องจัดหาตัวอย่างวัสดุที่ใช้แต่ละชนิด รวมทั้งอุปกรณ์ต่างๆ ที่ใช้ประกอบกันจำนวนไม่น้อยกว่า 2 ตัวอย่าง หรือได้ระบุไว้เป็นอย่างอื่น พร้อมกับรายละเอียดแสดงคุณสมบัติ ของวัสดุอุปกรณ์จากผู้ผลิตส่งให้ผู้ว่าจ้างเพื่อพิจารณาอนุมัติ เมื่อได้รับการอนุมัติแล้วจึงนำไปใช้งานได้ วัสดุอุปกรณ์ที่นำไปใช้งานต้องเป็นของใหม่ปราศจากรอยร้าวหรือตำหนิใดๆ มิขนาดลวดลายสีสรรตรงตามแบบและรายการประกอบแบบผู้รับจ้างต้องรับผิดชอบเวลาที่ใช้เพื่อการพิจารณาอนุมัติวัสดุอุปกรณ์(ไม่น้อยกว่า2 สัปดาห์) ไม่ว่าจะเป็นการขออนุมัติวัสดุอุปกรณ์ตามแบบ หรือวัสดุอุปกรณ์ที่ขอเปลี่ยนแปลงแก้ไขหรือเทียบเท่า กรณีมีเหตุสุดวิสัย ต้องการขอเทียบเท่าวัสดุอุปกรณ์ ผู้รับจ้างต้องหาวัสดุอุปกรณ์ที่มีคุณภาพเทียบเท่าหรือดีกว่าพร้อมรายละเอียดแสดงคุณสมบัติและราคาเปรียบเทียบเสนอผู้ว่าจ้าง เพื่อพิจารณาอนุมัติก่อนแล้วจึงนำไปใช้งานได้

1.4 หนังสือรับรองคุณภาพหรือการติดตั้งวัสดุอุปกรณ์ตามแบบและรายการผู้รับจ้างจะต้องเตรียมไว้เพื่อแสดงต่อผู้ออกแบบได้ทันทีที่ร้องขอในงานแต่ละงวดที่มีการใช้วัสดุอุปกรณ์นั้น ในกรณีที่ผู้รับจ้างไม่สามารถหาหนังสือมารับรองได้ ผู้ว่าจ้างสงวนสิทธิ์ที่จะไม่รับงานในงวดนั้น โดยถือว่าวัสดุหรืออุปกรณ์นั้นไม่ถูกต้องตามแบบและรายการ

1.5 ผู้รับจ้างจะต้องทำและวางแผนการทำงาน (FLOW CHART) แสดงรายละเอียดขั้นตอนวิธีการทำงานและเวลาที่จะใช้ในการก่อสร้าง และเสนอแผนดังกล่าวให้ผู้ออกแบบพิจารณาเห็นชอบก่อนเริ่มทำการก่อสร้าง

2. งานปักผังทำระดับ

2.1 ผู้รับจ้างจะต้องทำการปักผังและทำระดับ ให้ถูกต้องตามที่ปรากฏในผังบริเวณแบบแปลนและรายละเอียดของรูปแบบทุกประการ

2.2 การลดระดับหรือเปลี่ยนระดับพื้นต่างๆ ให้ถือตามที่ระบุในแบบสถาปัตยกรรมเป็นหลัก ดังนั้นก่อนทำการก่อสร้างโครงสร้างต่างๆ จะต้องตรวจสอบกับแบบสถาปัตยกรรมให้ละเอียดเสียก่อน หากพบการขัดแย้งหรือไม่สามารถทำตามแบบได้ให้แจ้งผู้ออกแบบเพื่อพิจารณาแก้ไข

3. งานฐานราก

3.1 ฐานรากเป็นคอนกรีตเสริมเหล็กตามแบบขยายทางวิศวกรรม

3.2 ระดับความลึกของฐานรากเป็นไปตามแบบขยายและรายการประกอบแบบทางวิศวกรรม

4. งานคอนกรีต งานปูน

4.1 งานคอนกรีตและงานปูนทั้งหมด เมื่อถอดแบบแล้วผิวของคอนกรีตจะต้องได้ดั่งได้จากและระดับในทางราบ ส่วนของเสาหรือคานตอนใดที่จะต้องฝังเหล็กหรือน็อต จะต้องจัดวางหรือฝังให้ถูกต้องตามตำแหน่งก่อนทำการเทคอนกรีต ไม้แบบส่วนต่อกัน โดยถูกต้องตามตำแหน่งก่อนทำการเทคอนกรีต โดยจะต้องจัดวางให้เรียบเสมอกันให้เรียบร้อย การยึดและติดตั้งไม้แบบจะต้องทำให้แน่นหนาและมั่นคง

4.2 คอนกรีตส่วนที่กรณีไม่ฉาบปูน (คอนกรีตเปลือยผิว) ไม้แบบจะต้องไสแต่งให้เรียบร้อยได้ขนาด เว้นช่องหรือติดิ้วให้เรียบร้อยแล้วทาน้ำมันกันผิวกระเทาะให้ทั่ว เมื่อถอดแบบแล้วผิวคอนกรีตจะต้องเรียบไม่แตกหักหรือกระเทาะเสียหายและจะต้องได้ดิ้ง ได้จาก หรือเอียงตามรูปแบบทุกประการ

5. งานพื้นอาคาร

5.1 พื้นอาคารเป็นพื้นคอนกรีตเสริมเหล็ก ตามแบบขยายทางวิศวกรรม

5.2 ผิวพื้นในส่วนต่างๆของอาคาร ให้เป็นไปตามรายการพื้นและรายละเอียดประกอบ

6. งานผนัง

6.1 การบุกระเบื้องบุผนัง ถ้าแบบไม่ได้ระบุความสูงของผิวกระเบื้องที่บุ ให้บุกระเบื้องสูง2.00 เมตร เสมอขอบวงกบ

6.1.1 ผนังลอย ให้บุกระเบื้องตลอดความสูงของผนัง

6.2 รายละเอียดผิวผนัง ให้เป็นไปตามรายการผนัง หรือแบบขยาย หรือรายละเอียดตามรูปด้าน

7. งานฝ้าเพดาน

7.1 ฝ้าเพดานโดยทั่วไปเป็นไปตามผังฝ้าเพดาน รายการฝ้าเพดาน

7.2 ให้ติดตั้งแผ่นฉนวนตราช้างกันรังสีความร้อน(ROOF BATT)เหนือฝ้าเพดานใต้หลังคา ตามกรรมวิธีของบริษัทผู้ผลิต

7.3 โครงเคร่าไม้ โครงเคร่าไม้เนื้อแข็ง ใช้ขนาด 1 1/2"x3" ไม่เกิน 0.50x0.75 ม. ทาน้ำยากันปลวก SHELLDRITE STEDFAST 4SC รอบตัว

7.4 หากแบบระบุเป็นฝ้าไม้ระแนง ใช้ไม้สักขนาด 3/4"x4" ยาวตลอดไม่ต้องต่อ ยกเว้นช่วงที่ยาวกว่า 3ม.

7.5 หากแบบระบุเป็นฝ้าเพดาน GYMSUM BOARD ฉาบเรียบให้ใช้โครงเคร่าเหล็กชุบสังกะสีกันสนิม @ 0.40ม.

8. งานหลังคา

หลังคาทั่วไปใช้หลังคาเมทัลชีท แผ่นเหล็กเคลือบสังกะสีโดยกรรมวิธีจุ่มร้อนและเคลือบสี มอก. 2131-2545 มีระบบกันน้ำฝนชิมครบชุด

9. งานบัวปูนปั้นและบัวเชิงผนัง

9.1 งานบัวปูนปั้นภายนอก หากผู้รับจ้างเสนอ เป็น GRC (GLASS FIBRE REINFORCE CONCRETE) ให้ผู้รับจ้างทำ SHOP DRAWING เสนอผู้ออกแบบ เห็นชอบก่อนทำการติดตั้ง ทั้งนี้ความหนาของ GRC ต้องหนาอย่างน้อย 10 ซ.ม.

9.2 บัวเชิงผนังใช้บัวไม้เนื้อแข็ง 1/2"x4" หรือตามแบบ

9.3 การทำบัวเชิงผนัง จะต้องทำทุกส่วนที่พื้นนั้นไปบรรจบ เช่น เสาถ้าอยู่กลางห้อง จะต้องทำบัวโดยรอบถ้าอยู่ริมอาคารทำบัวเฉพาะด้านที่พื้นไปบรรจบ ทั้งนี้รวมถึงผนังและแผงคสล.ด้วย

10. งานวงกบ ประตู หน้าต่าง ช่องแสง

10.1 วงกบเป็นไม้เนื้อมะค่า หรือไม้ตามแบบขยายและรายการประตู หน้าต่าง

10.2 วงกบและบานกรอบอลูมิเนียม เป็น ALUMINIUM NA 1 หนาไม่ต่ำกว่า 1.2 มม. ของเมืองทองหรือเทียบเท่า ขนาดหน้าตัดตามแบบขยายและรายการ(พร้อมรางบานมุ้งลวด) โดยผู้รับจ้างจะต้องเสนอตัวโดยผู้รับจ้างจะต้องเสนอตัวอย่างหน้าตัด แล็ดตาล็อต และวิธีการติดตั้ง ให้พิจารณาก่อนการใช้งาน

11. งานกระจก

11.1 กระจกโดยทั่วไปใช้กระจกใส(CLEAR FLOAT GLASS) ขนาดความหนา 5 มม. สำหรับห้องน้ำใช้กระจกฝ้า ขนาดความหนา 5 มม.หรือตามแบบขยายและรายการประตูหน้าต่าง

11.2 การติดตั้งกระจกติดตาย ลูกฟักกระจก จะต้องอัดด้วย CAULKING COMPOUND ชนิดSILICONE SEALANT

12. งานห้องน้ำ ห้องส้วม

12.1 พื้นห้องน้ำ ห้องส้วมเป็นคสล. หล่อกับที่ผสมน้ำยากันซึม

12.2 รายละเอียดผิวพื้นและผิวผนังห้องน้ำ ห้องส้วม ให้ดูจากรายการพื้นและรายการผนัง

12.3 สุขภัณฑ์ภายในห้องน้ำ ห้องส้วมให้ติดตั้งตามแบบขยายและรายการ

13. งานบันได

บันไดเป็นคอนกรีตเสริมเหล็กตามแบบขยายบันได

13.1 ลูกนอนไม้เนื้อแข็งขนาด 2"x10"

13.2 ราวบันได ตามแบบขยาย

14. งานระบบประปาสุขาภิบาล

ให้ติดตั้งและเดินท่อระบบสุขาภิบาล ตามแบบและรายการประกอบแบบทางสุขาภิบาล กรณีที่ต้องเดินท่อผ่านคาน พื้น หรือโครงสร้าง จะต้องจัดเตรียมผัง SLEEVE ไว้ให้เรียบร้อย

14.1 ติดตั้งประตูน้ำ(STOP VALVE)ก่อนต่อเข้าสุขภัณฑ์ทุกตัว

14.2 ให้ติดตั้งก็อกน้ำล้างพื้น 1 จุดทุกห้องน้ำ

15. งานระบบไฟฟ้า

ให้ติดตั้งเดินสายไฟและอุปกรณ์ ตามมาตรฐานการไฟฟ้านครหลวง

15.1 ให้ติดตั้งและเดินสายระบบไฟฟ้าระบบแสงสว่าง ตามแบบและรายการประกอบแบบทางไฟฟ้ากรณีที่ต้องเดินท่อร้อยสายผ่านคาน พื้น หรือโครงสร้าง จะต้องจัดเตรียมผัง SLEEVE ไว้ให้เรียบร้อย

15.2 การติดตั้งดวงโคมให้ติดตั้งตามแบบที่แสดงในผังไฟฟ้าในกรณีที่ติดตั้งดวงโคมกับฝ้าเพดานจะต้องจัดเคร่าฝ้าให้พอดีกับดวงโคม หรือต้องเพิ่มโครงเคร่าเพื่อความแข็งแรงตามความเหมาะสม

15.3 อุปกรณ์ปลั๊ก สวิทช์ ใช้ของ NATIONAL WIDE SERIES,BTICINO

15.4 สายไฟฟ้า YAZAKI, BANGKOK CABLE หรือเทียบเท่า

15.5 ท่อร้อยสายไฟ ใช้ท่อ PVC CONDUIT(สีเหลือง)

15.6 ตู้ MDB ใช้ SQUARE -D 12 ช่อง

PROJECT NUMBER : VC2023-024

PROJECT

MACHI RESIDENCES

อาคารพักอาศัยรวม ค.ส.ล 7 ชั้น

OWNER

บริษัท ฤทธิกร ลิฟวิ่ง จำกัด

ARCHITECT :

อัคคะภัทร์ จิระอาธิย์บุตร ส-สถ.3040

403 ซ.พัฒนาการ 50 พัฒนาการ

กรุงเทพมหานคร 10250

INTERIOR DESIGNER :

–

STRUCTURAL ENGINEER :

นายพงษ์ธวิทย์ คฑาวุธเจริญกุล สย.12291

ELECTRICAL ENGINEER :

นายภาคภูมิ คำพิทูรย์ สพก.5587

MECHANICAL ENGINEER :

SANITARY ENGINEER :

นส.อรวรรณ พลตรี สส.134

DRAWING TITLE

รายการประกอบแบบ

DRAWING FOR CONSTRUCTION

DRAW BY :	CHECKER :	REVISION :
Weerayuth L.	Akapatr C.	–

SCALE : 1 : 100

DRAWING NO. A-R02

DATE : 04-12-2024

FILE NAME :


JOB NO.

REVISION	DESCRIPTION

GERNERAL NOTE
DO NOT SCALE DRAWING ALL MEASUREMENT MUST BE CHECKED AT THE SIDE BY THE CONTRACTOR
ALL DESIGN AND DRAWINGS ARE THE PROPERTY OF MARCHTEN CO.,LTD
AND NOT BE USED WITH OUT THEIR WRITTEN PERMISSION


MARCHTEN
ARCHITECTURE / INTERIOR
บริษัท มาร์ชเทน จำกัด
403 ซ.พัฒนาการ 50 สวนหลวง กรุงเทพมหานคร 10250

CONSTRUCTION & FIRE EXIT DETAILS

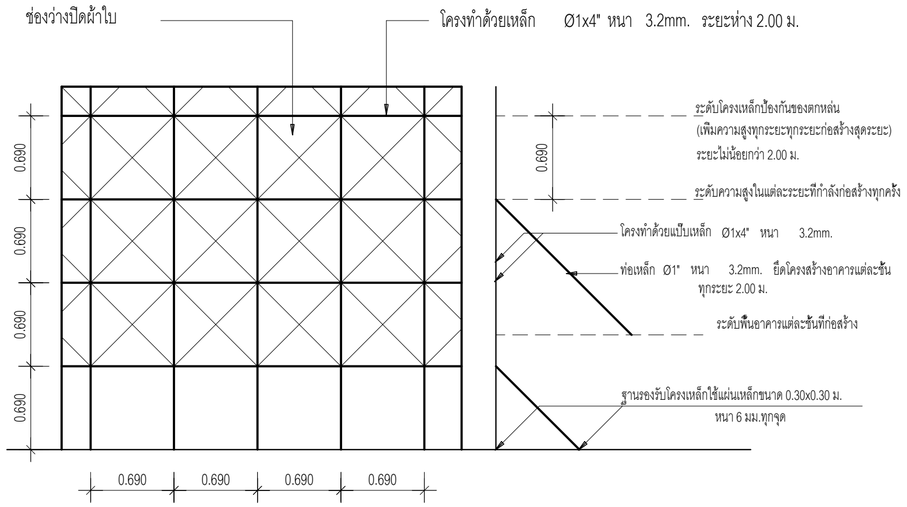

แบบขยายรูปตั้งด้านหน้า

แบบขยายรูปตัด

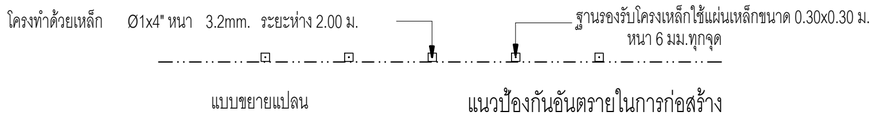

แบบขยายแปลน


แนวป้องกันอันตรายในการก่อสร้าง

มาตราการป้องกันเหตุเดือดร้อนรำคาญในการก่อสร้าง


เพื่อไม่ให้เสียหายและรบกวนบ้านผู้อยู่อาศัยตลอดจนผู้ใช้ถนนใกล้เคียงจึงมีมาตราการดังนี้คือ

1. การทำฐานรากหากใช้เข็มตอกจะต้องมี SHEET PILE กันดินเคลื่อน
2. การลำเลียงหรือขนย้ายวัสดุก่อสร้างรวมทั้งคอนกรีตผสมเสร็จ จะจัดทำในบริเวณก่อสร้างเพื่อมิให้ก่อความเดือดร้อนรำคาญแก่ผู้ใช้ทางเดินเท้าและถนน
3. รถขนดินที่มากมดินในบริเวณก่อสร้างจะต้องไม่มีการบรรทุกเกินน้ำหนัก ซึ่งจะเป็นเหตุให้ถนนชำรุดเสียหาย
4. จะไม่ทำการก่อสร้างหรือกระทำการใดๆในบริเวณที่ได้รับอนุญาตให้ก่อสร้างดัดแปลงรื้อถอน หรือเคลื่อนย้าย ซึ่งก่อให้เกิดเสียงและแสงรบกวนผู้อยู่อาศัยข้างเคียงระหว่าง 22.00 - 6.00 น.
5. จะมีการป้องกันวัสดุร่วงหล่นตามกฎข้างล่าง
6. จะไม่จอดรถขนถ่ายวัสดุบนถนนสาธารณะด้านหน้า SITE
7. การก่อสร้างจะมีกล่องฝึงวัสดุจากที่สูงลงที่ต่ำป้องกันอันตรายกับบุคคลที่เกี่ยวข้องและป้องกันสิ่งของลงสู่บ้านข้างเคียง
8. จะมีรั้วชั่วคราวล้อมรอบ SITE สูง 2.50 ม.
9. จะมีจุดกองวัสดุอยู่เป็นที่เฉพาะภายใน SITE
10. จัดให้มีปล่องทิ้งเศษขยะชั่วคราว
11. ก่อสร้างไม่ทำให้เสียงดังเกิน 75 DB.(A)

มาตราฐานความปลอดภัยในระหว่างการก่อสร้าง

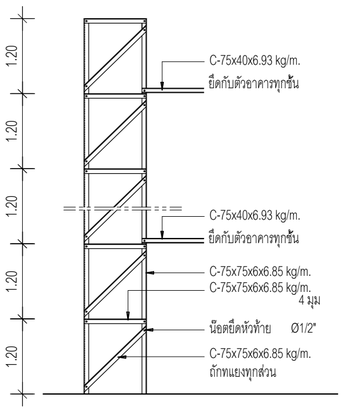

รูปแสดงแนวตั้ง

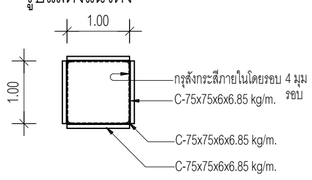


รูปแสดงผัง


มาตราการเพื่อความปลอดภัยระหว่างการก่อสร้างอาคาร

ในระหว่างการก่อสร้างอาคารจะต้องมีมาตราการต่างๆ ในระหว่างการก่อสร้างอาคารจะต้องมีมาตราการต่างๆ ซึ่งอาจจะเกิดได้กับชีวิตและทรัพย์สินของตนเองและผู้ขึนได้อย่างน้อยจะต้องเตรียมการป้องกันโดย

1. ป้องกันการเสียหายซึ่งเกิดจากการสันสะเทือนเนื่องจากการตอกเข็มและการก่อสร้างฐานรากที่อยู่ต่ำกว่าระดับดินเดิม ตอกเข็ม กันดินพัง (SHEET PILES) ซึ่งมีขนาดเพียงพอที่จะรับน้ำหนักของดิน และน้ำหนักของสิ่งก่อสร้าง รวมทั้งน้ำหนักจร บนดินได้เพียงพอ โดยจะออกแบบให้มีมาตราการน้ำหนักสิ่งเหล่านี้ด้วยการค้ำยัน (BRACING) ให้เพียงพอ
2. การป้องกันการเสียหายซึ่งเกิดจากเศษสิ่งของ วัสดุร่วงหล่นลงมาข้างล่าง
   - 2.1 กันรั้วชั่วคราวโดยรอบพื้นที่ ท่จะทำการก่อสร้างอาคาร ห้ามมิให้ผู้ที่มิใช่บุคคลที่ไม่มีกิจธุระเกี่ยวข้องเข้าไปภายในบริเวณ
   - 2.2 ขึงผ้าใบห่างจากอาคารที่ก่อสร้างห่างจากอาคาร 2.00 ม. โดยรอบ ในส่วนที่ระยะห่างไม่ถึง 2.00 ม. ให้สร้างรั้วสูง 2.00 ม.
   - 2.3 คนงานที่เกี่ยวข้องในการปฏิบัติงาน ในบริเวณก่อสร้างให้ปฏิบัติตน ตามประกาศกระทรวงมหาดไทย เรื่อง ความปลอดภัยในการทำงานก่อสร้าง อย่างเคร่งครัด
3. จัดทำประกันภัยสำหรับชีวิตและทรัพย์สินของบุคคล ที่เกี่ยวข้องกับงานก่อสร้าง
4. ด้านชิดแนวเขตป้องกันอันตรายโดยใช้โครงเหล็กแป็บชิดแนวเขตที่ดินและขึงช่องว่างด้วยผ้าใบ
5. ติดตั้งโครงเหล็กบุผ้าใบ ชนิดหนาล้อมรอบตัวอาคารตามความสูงที่ก่อสร้าง ป้องกันวัสดุร่วงหล่นและฝุ่นละออง
6. ไม่กองวัสดุก่อสร้างในที่สาธารณะ

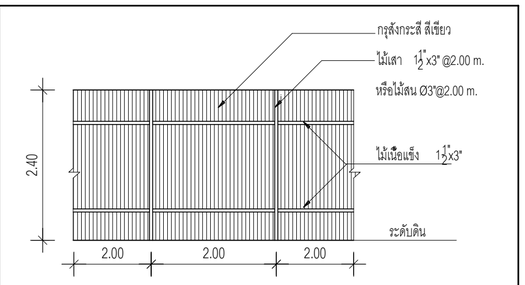

รูปแบบรั้วชั่วคราว

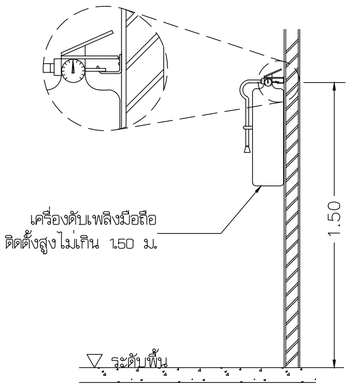


แบบแสดงตำแหน่งเครื่องดับเพลิงมือถือ

ป้ายหนีไฟ เรืองแสง สำรองไฟฉุกเฉิน


เครื่องดับเพลิงแบบมือถือชนิดผงเคมีแห้ง
ให้มีเครื่องดับเพลิงแบบมือถือ ขนาดบรรจุไม่น้อยกว่า 4 กก. (หรือไม่เล็กกว่าขนาด 10 ปอนด์)
โดยติดตั้งให้เครื่องดับเพลิงสูงไม่เกิน 1.5 เมตร วัดจากส่วนบนสุดของตัวเครื่องจากพื้น

ชนิดหรือประเภทของอาคาร	ชนิดของเครื่องดับเพลิง	ขนาดบรรจุไม่น้อยกว่า
1) ห้องแถว ตึกแถว บ้านแถว และบ้านแฝด ที่มีความสูงไม่เกิน 2.00 ม	1) น้ำอัดความดัน	10 ลิตร
	2) กรด – โซดา	10 ลิตร
	3) โฟมเคมี	10 ลิตร
	4) ก๊าซคาร์บอนไดออกไซด์	3 กิโลกรัม
	5) ผงเคมีแห้ง	3 กิโลกรัม
	6) เฮลอน (HALON 1211)	3 กิโลกรัม
2) อาคารอื่น นอกจากอาคาร (1)	1) โฟมเคมี	10 ลิตร
	2) ก๊าซคาร์บอนไดออกไซด์	4 กิโลกรัม
	3) ผงเคมีแห้ง	4 กิโลกรัม
	4) เฮลอน (HALON 1211)	4 กิโลกรัม

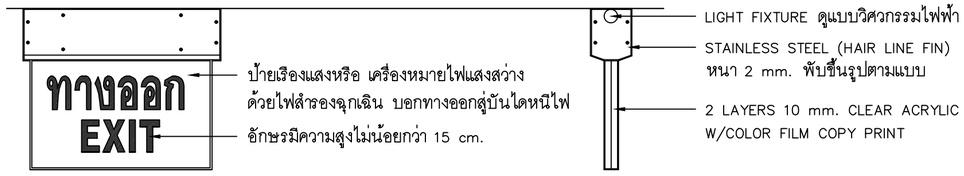

FRONT VIEW SIDE VIEW

แบบขยายป้ายทางออก

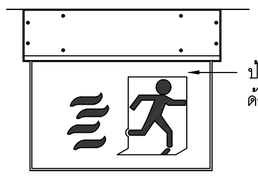

FRONT VIEW แบบขยายป้ายทางหนีไฟ

(หมายเหตุ)

- สำหรับสีในป้าย กำหนดให้ใช้ตามมาตรฐานสากล
- ให้ผู้รับจ้างจัดทำ SHOP DRAWING เสนอก่อนดำเนินการ

PROJECT NUMBER : VC2023-024

PROJECT

MACHI RESIDENCES

อาคารพักอาศัยรวม ค.ส.ล 7 ชั้น

OWNER

บริษัท ฤทธิกร ลิฟวิ่ง จำกัด

ARCHITECT :

อัคคะภัทร์ จิระอารีย์บุตร ส-สถ.3040
403 ซ.พัฒนาการ 50 พัฒนาการ
กรุงเทพมหานคร 10250

INTERIOR DESIGNER :

–

STRUCTURAL ENGINEER :

นายพงษ์ธวิทย์ คฑาวุธเจริญกุล สย.12291

ELECTRICAL ENGINEER :

นายภาคภูมิ คำพิทูรย์ สพก.5587

MECHANICAL ENGINEER :

SANITARY ENGINEER :

นส.อรวรรณ พลตรี สส.134

DRAWING TITLE

มาตราการเพื่อความปลอดภัย
แผนที่โดยสังเขป

DRAWING FOR CONSTRUCTION

DRAW BY :	CHECKER :	REVISION :
Weerayuth L.	Akapatr C.	–


SCALE :	DRAWING NO.
1 : 100	A-R03
DATE : 04–12–2024	
FILE NAME :	JOB NO.

REVISION	DESCRIPTION


GERNERAL NOTE
DO NOT SCALE DRAWING ALL MEASUREMENT MUST BE CHECKED AT THE SIDE BY THE CONTRACTOR
ALL DESIGN AND DRAWINGS ARE THE PROPERTY OF MARCHTEN CO.,LTD
AND NOT BE USED WITH OUT THEIR WRITTEN PERMISSION

MARCHTEN
ARCHITECTURE / INTERIOR


บริษัท มาร์ชเทน จำกัด
403 ซ.พัฒนาการ 50 สวนหลวง กรุงเทพมหานคร 10250

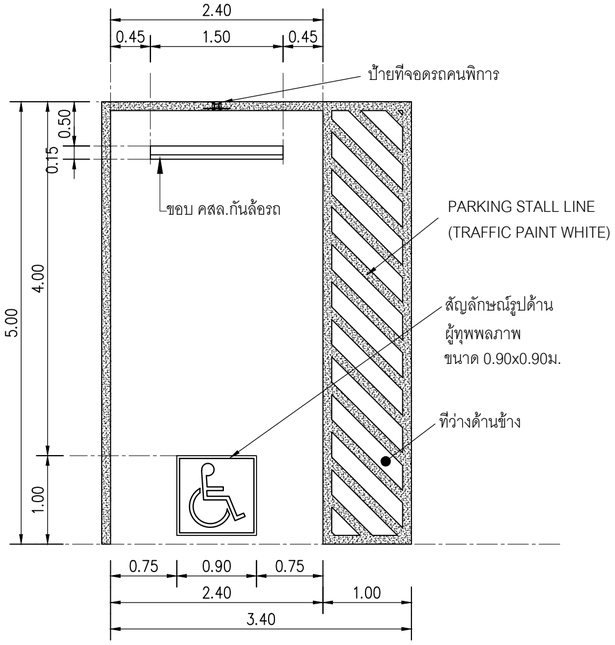

แบบขยาย ที่จอดรถคนพิการ

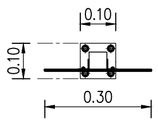

แปลนขยาย ป้ายที่จอดรถคนพิการ

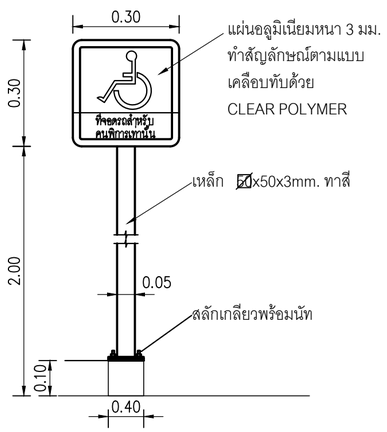

รูปด้านขยาย ป้ายที่จอดรถคนพิการ




สัญลักษณ์ สำหรับคนพิการทางกาย ทางการได้ยินหรือสื่อความหมาย

สัญลักษณ์ สำหรับคนพิการทางกาย ทางการได้ยินหรือสื่อความหมาย

สัญลักษณ์ สำหรับผู้สูงอายุ


สัญลักษณ์ สำหรับคนพิการ ทางกายภาพหรือการเคลื่อนไหว

สัญลักษณ์ สำหรับคนพิการ ทางการมองเห็น

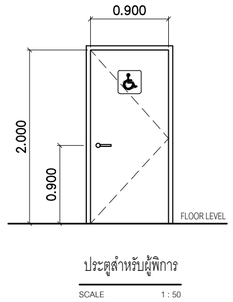


ประตูสำหรับผู้พิการ

SCALE 1 : 50

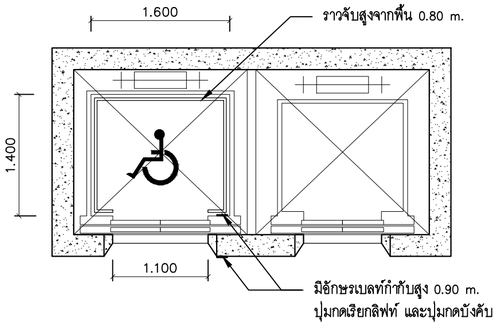


ลิฟท์ สำหรับคนพิการ

SCALE 1 : 50

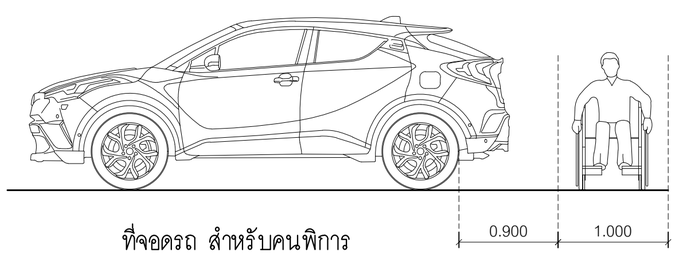

ที่จอดรถ สำหรับคนพิการ

SCALE 1 : 50

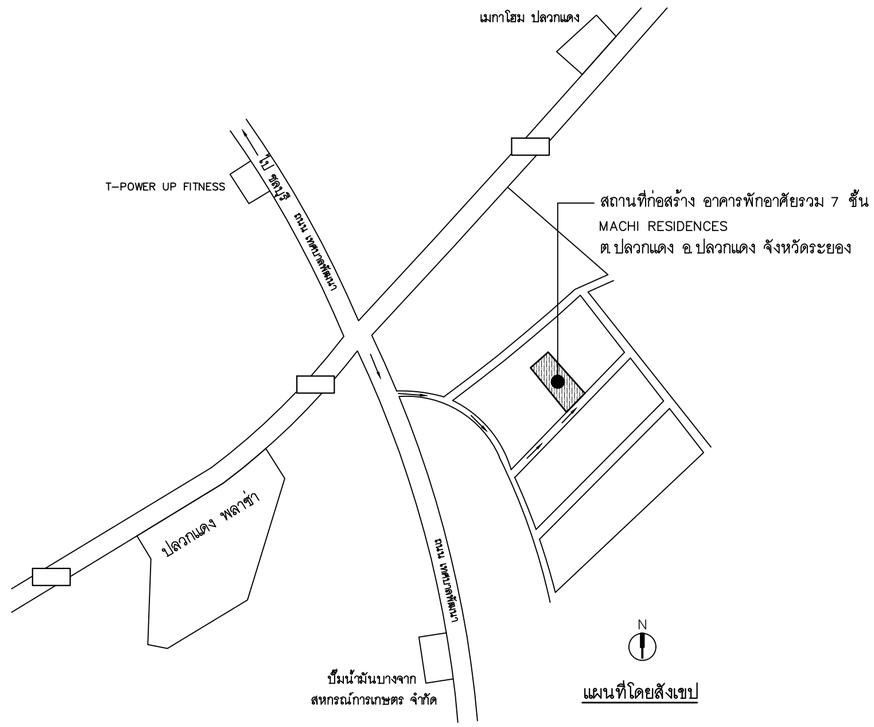

แผนที่โดยสังเขป

PROJECT NUMBER : VC2023-024

PROJECT

MACHI RESIDENCES

อาคารพักอาศัยรวม ค.ส.ล 7 ชั้น

OWNER

บริษัท ฤทธิกร ลิฟวิ่ง จำกัด

ARCHITECT :

อัคคะภัทร์ จิระอารีย์บุตร ส-สถ.3040

403 ซ.พัฒนาการ 50 พัฒนาการ

กรุงเทพมหานคร 10250

INTERIOR DESIGNER :

–

STRUCTURAL ENGINEER :

นายพงษ์ธวิทย์ คทาวุธเจริญกุล สย.12291

ELECTRICAL ENGINEER :

นายภาคภูมิ คำพิทูรย์ สพก.5587

MECHANICAL ENGINEER :

SANITARY ENGINEER :

นส.อรวรรณ พลตรี สส.134

DRAWING TITLE

แบบประกอบผู้พิการ , แผนที่โดยสังเขป

DRAWING FOR CONSTRUCTION

DRAW BY :	CHECKER :	REVISION :
Weerayuth L.	Akapatr C.	–

SCALE :	DRAWING NO.
1 : 100	A-R04
DATE : 04-12-2024	
FILE NAME :	JOB NO.

REVISION	DESCRIPTION

GERNERAL NOTE


DO NOT SCALE DRAWING ALL MEASUREMENT MUST BE CHECKED AT THE SIDE BY THE CONTRACTOR

ALL DESIGN AND DRAWINGS ARE THE PROPERTY OF MARCHTEN CO.,LTD AND NOT BE USED WITH OUT THEIR WRITTEN PERMISSION

MARCHTEN

ARCHITECTURE / INTERIOR

บริษัท มาร์เทน จำกัด
403 ซ.พัฒนาการ 50 สวนหลวง กรุงเทพมหานคร 10250

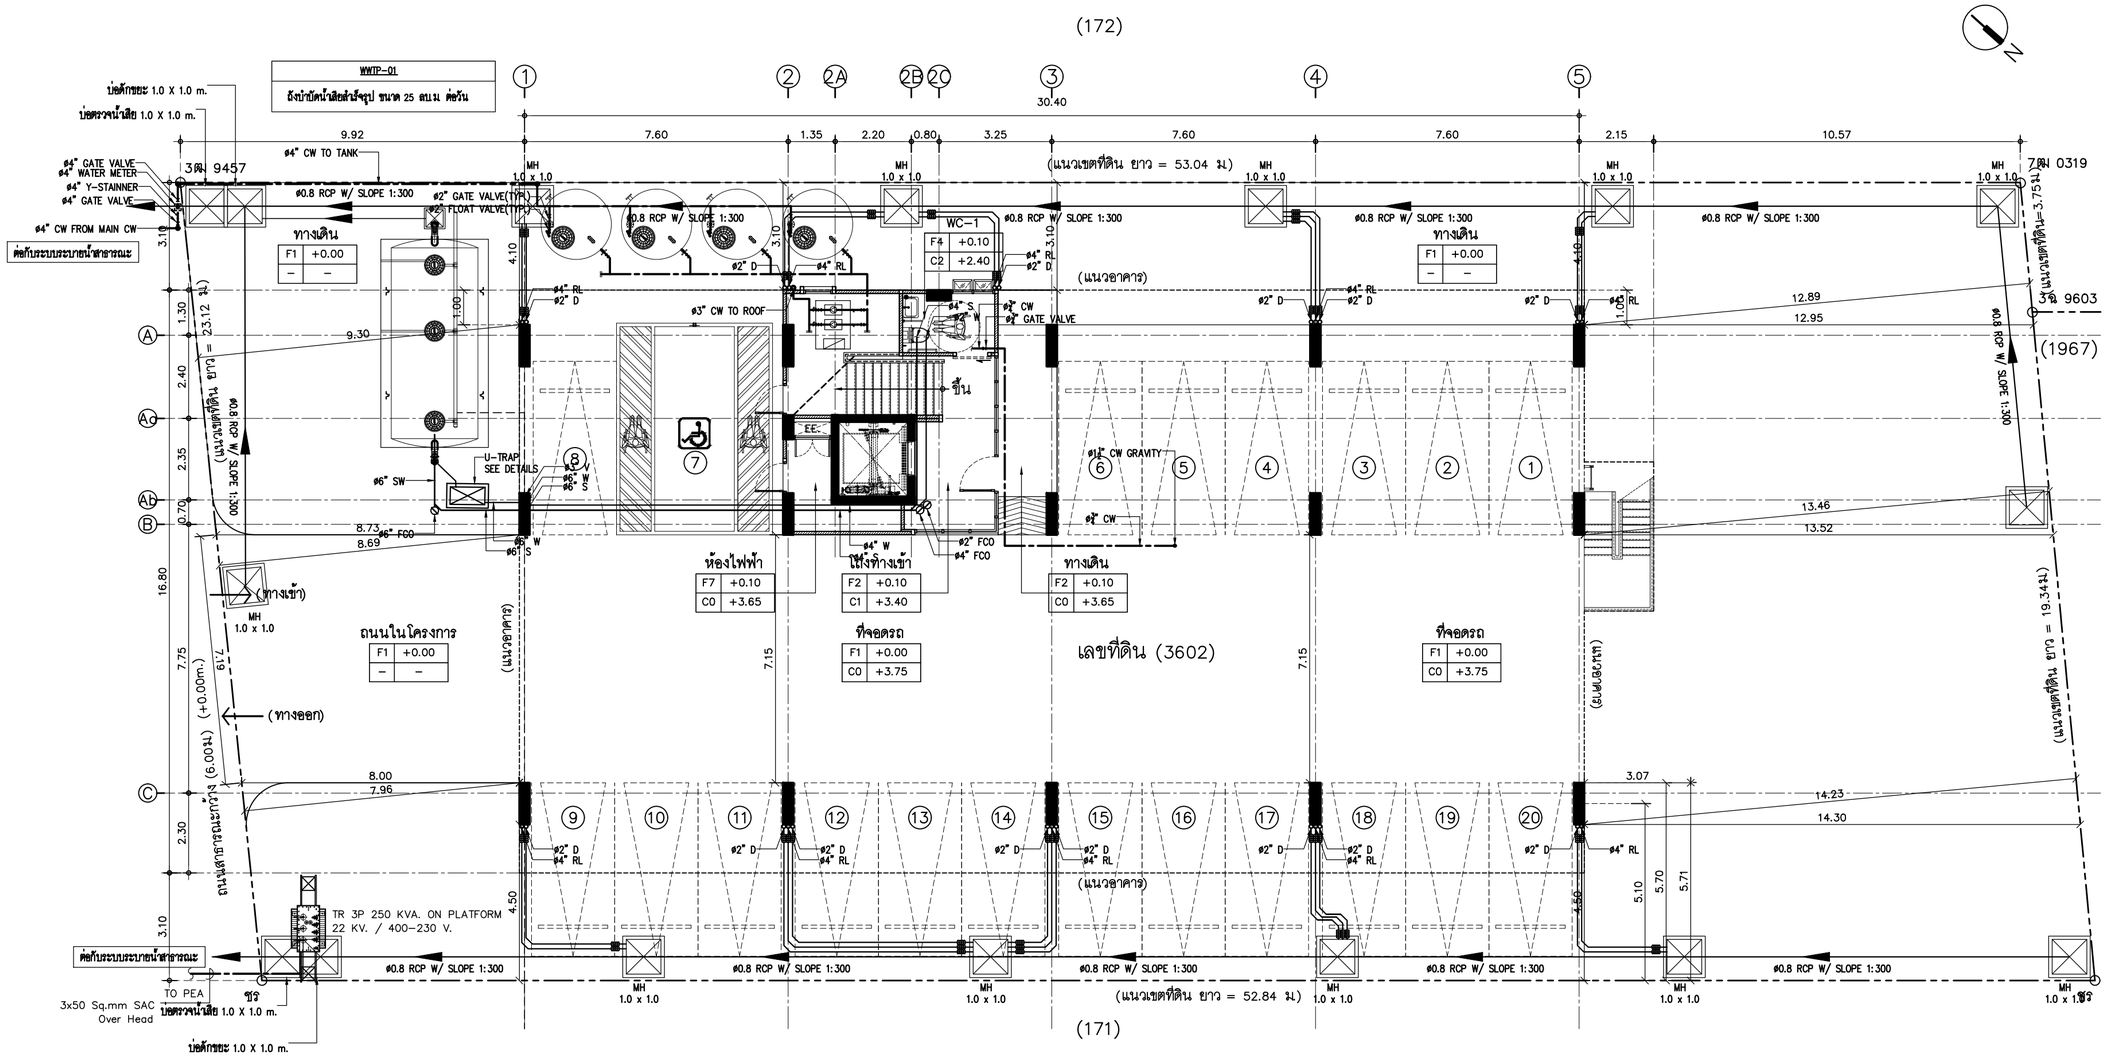

ผังบริเวณ

SCALE 1:125

PROJECT NUMBER : VC2023-024

PROJECT

MACHI RESIDENCES

อาคารพักอาศัยรวม ค.ส.ล 7 ชั้น

OWNER

บริษัท ฤทธิกร ลิฟวิ่ง จำกัด

ARCHITECT :

อัคคะภัทร์ จิระอารีย์บุตร ส-สถ.3040

403 ซ.พัฒนาการ 50 พัฒนาการ

กรุงเทพมหานคร 10250

INTERIOR DESIGNER :

–

STRUCTURAL ENGINEER :

นายพงษ์ธวิทย์ คฑาวุธเจริญกุล สย.12291

ELECTRICAL ENGINEER :

นายภาคภูมิ คำพิทูรย์ สพก.5587

MECHANICAL ENGINEER :

SANITARY ENGINEER :

นส.อรวรรณ พลตรี สส.134

DRAWING TITLE

ผังบริเวณ

DRAWING FOR CONSTRUCTION

DRAW BY :	CHECKER :	REVISION :
Weerayuth L.	Akapatr C.	–

SCALE : 1 : 100

DRAWING NO. A-P00

DATE : 04-12-2024

FILE NAME :

JOB NO.


REVISION	DESCRIPTION

GERNERAL NOTE

DO NOT SCALE DRAWING ALL MEASUREMENT MUST BE CHECKED AT THE SIDE BY THE CONTRACTOR

ALL DESIGN AND DRAWINGS ARE THE PROPERTY OF MARCHTEN CO.,LTD AND NOT BE USED WITH OUT THEIR WRITTEN PERMISSION

MARCHTEN
ARCHITECTURE / INTERIOR
บริษัท มาร์ชเทน จำกัด
403 ซ.พัฒนาการ 50 สวนหลวง กรุงเทพมหานคร 10250

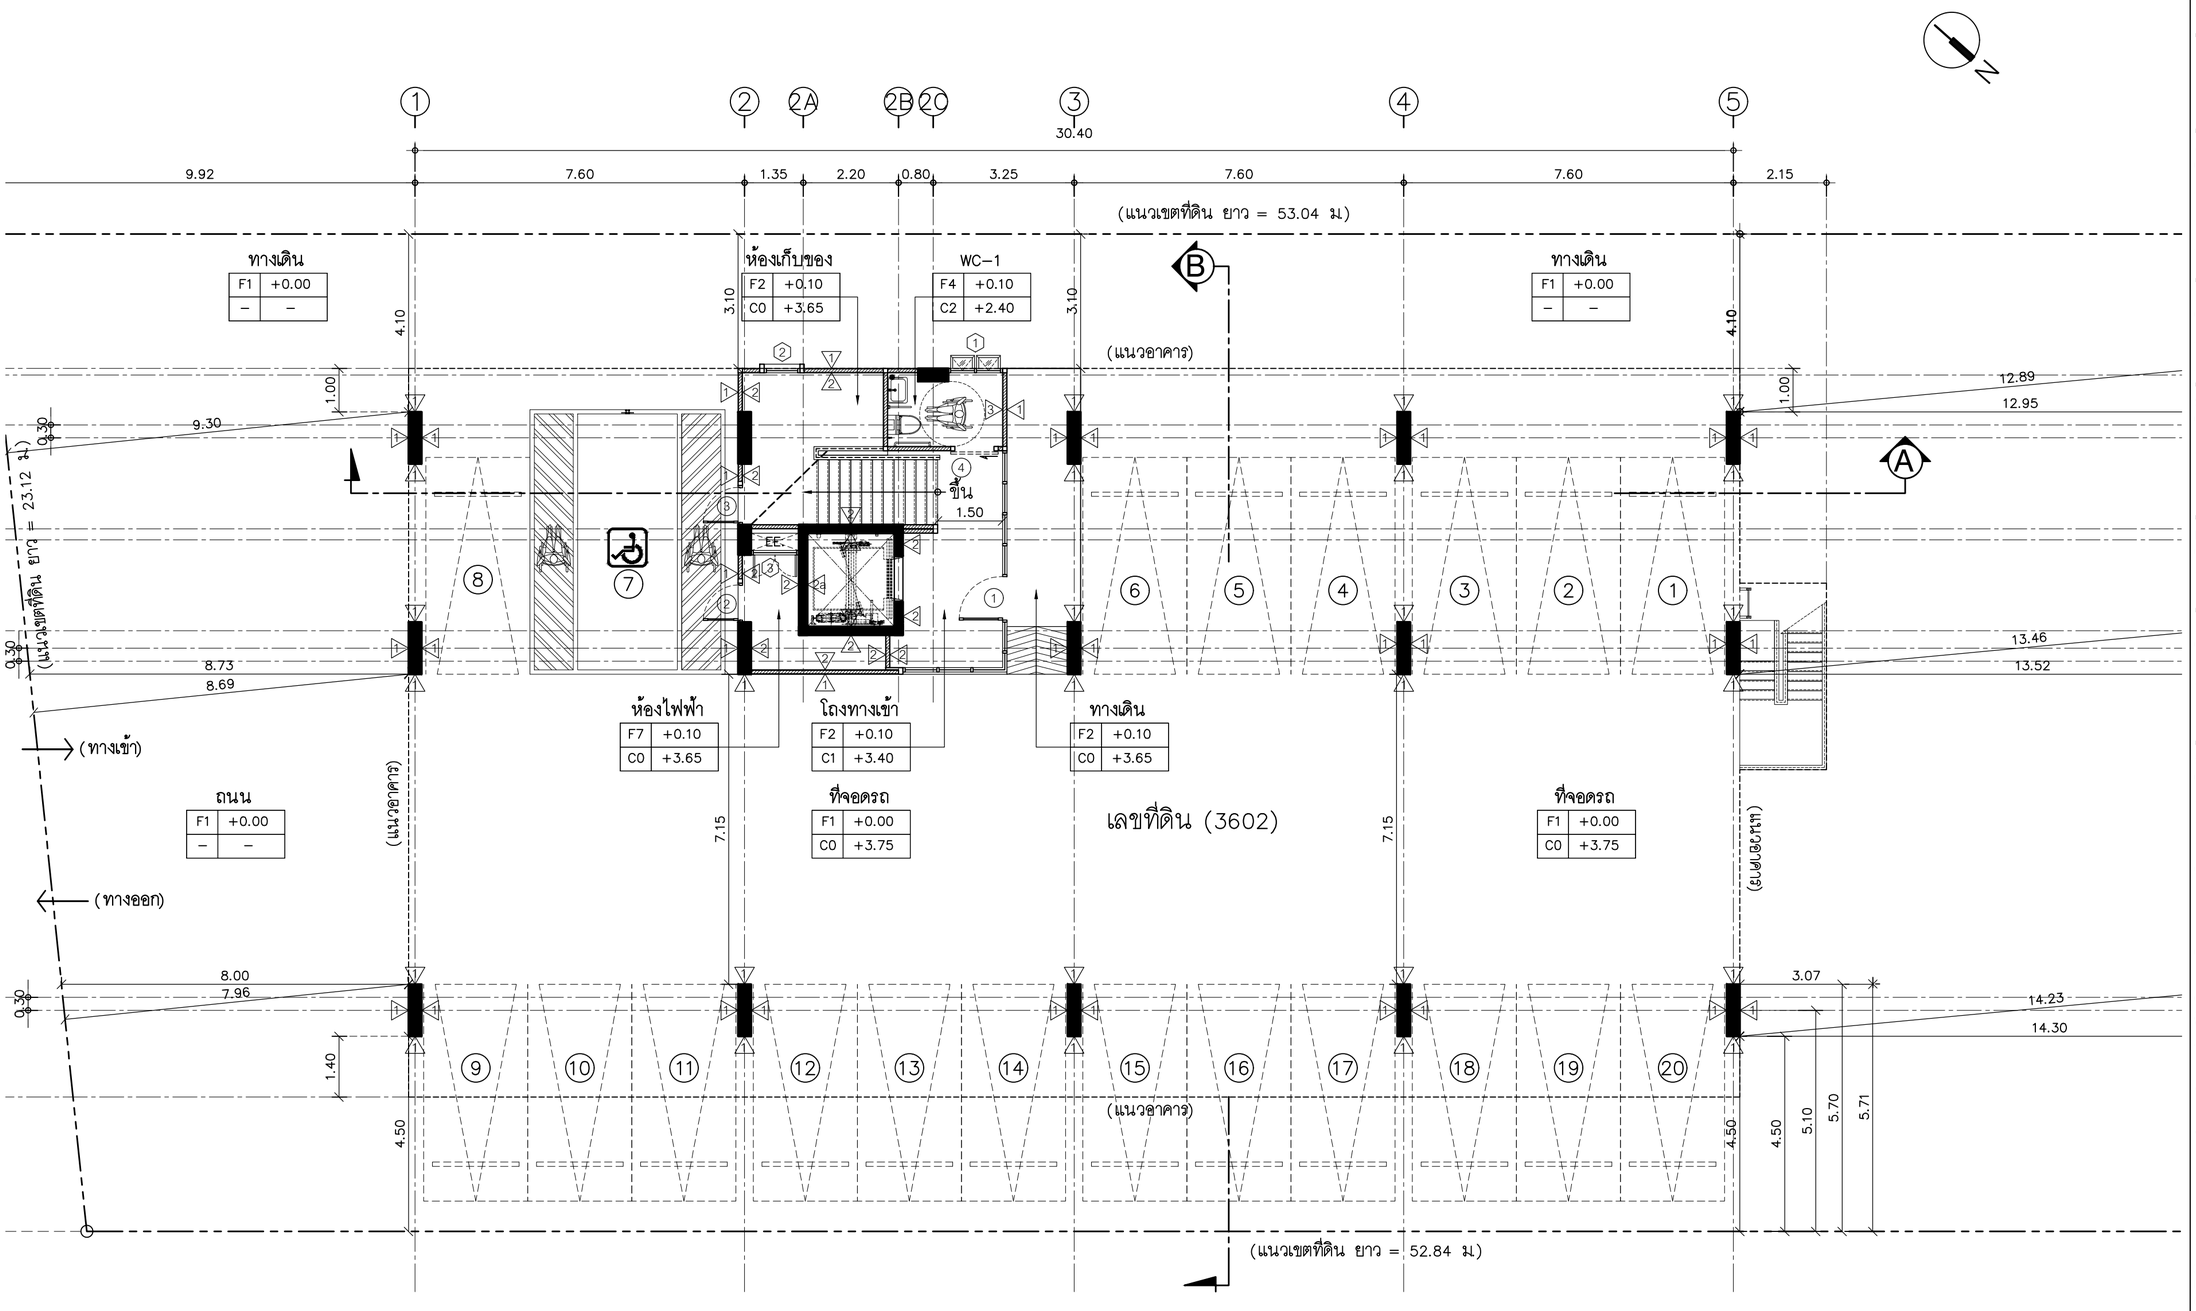

แปลนพื้นชั้น (1)

SCALE 1:100

พื้นที่ดิน = 1,217 ตร.ม (3 งาน 04 ตารางวา)
พื้นที่อาคารชั้น (1)–(7) = 525.00 ตร.ม x7 ชั้น = 3,675 ตร.ม

PROJECT NUMBER : VC2023–024

PROJECT

MACHI RESIDENCES

อาคารพักอาศัยรวม ค.ส.ล 7 ชั้น

OWNER

บริษัท ฤทธิกร ลิฟวิ่ง จำกัด

ARCHITECT :

อัคคะภัทร์ จิระอารีย์บุตร ส–สถ.3040

403 ซ.พัฒนาการ 50 พัฒนาการ

กรุงเทพมหานคร 10250

INTERIOR DESIGNER :

–

STRUCTURAL ENGINEER :

นายพงษ์ธวิทย์ คทาวุธเจริญกุล สย.12291

ELECTRICAL ENGINEER :

นายภาคภูมิ คำพิทูรย์ สพก.5587

MECHANICAL ENGINEER :

SANITARY ENGINEER :

นส.อรวรรณ พลตรี สส.134

DRAWING TITLE

แปลนพื้นชั้น (1)

DRAWING FOR CONSTRUCTION

DRAW BY :	CHECKER :	REVISION :
Weerayuth L.	Akapatr C.	–

SCALE : 1 : 100

DRAWING NO. A-P01

DATE : 04–12–2024

FILE NAME :

JOB NO.

REVISION	DESCRIPTION

GERNERAL NOTE

DO NOT SCALE DRAWING ALL MEASUREMENT MUST BE CHECKED AT THE SIDE BY THE CONTRACTOR


ALL DESIGN AND DRAWINGS ARE THE PROPERTY OF MARCHTEN CO.,LTD AND NOT BE USED WITH OUT THEIR WRITTEN PERMISSION

MARCHTEN

ARCHITECTURE / INTERIOR

บริษัท มาร์ชเทน จำกัด

403 ซ.พัฒนาการ 50 สวนหลวง กรุงเทพมหานคร 10250

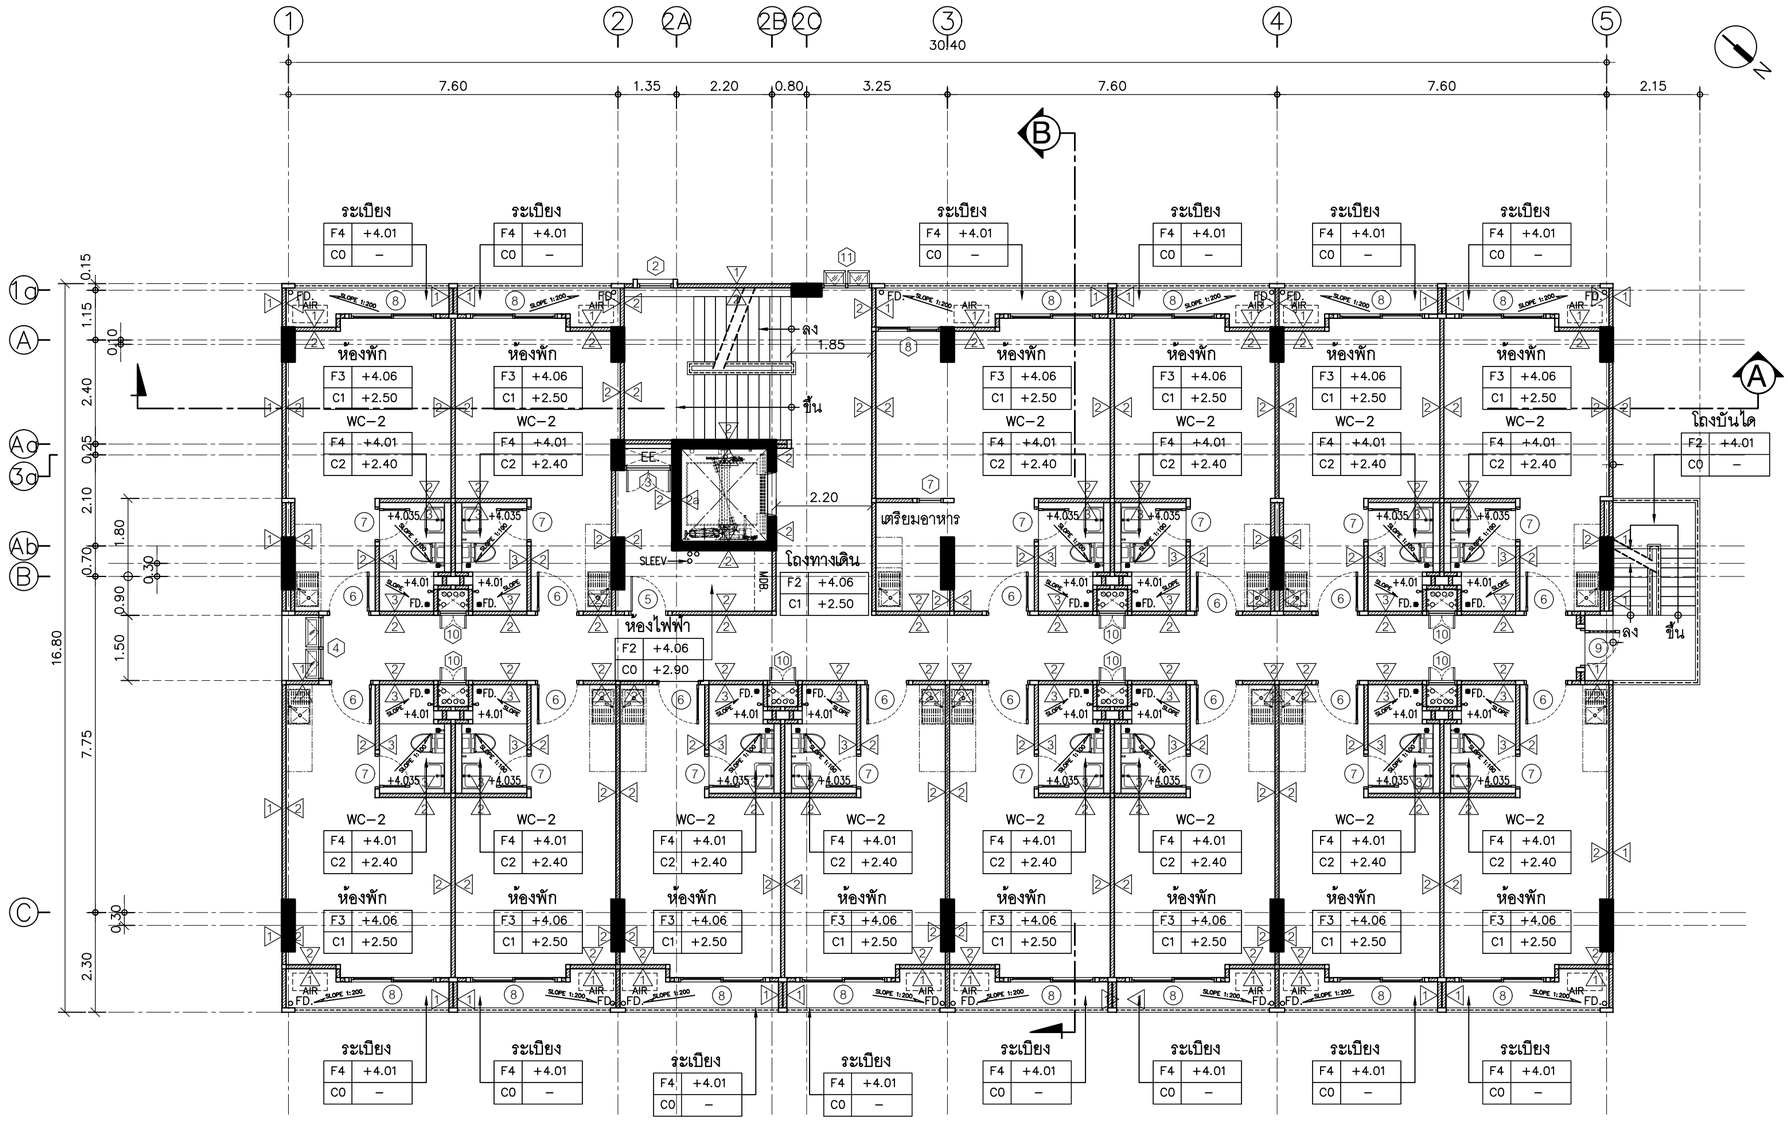



แปลนพื้นชั้น (2)

SCALE 1:100

PROJECT NUMBER : VC2023-024

PROJECT

MACHI RESIDENCES

อาคารพักอาศัยรวม ค.ส.ล 7 ชั้น

OWNER

บริษัท ฤทธิกร ลิฟวิ่ง จำกัด

ARCHITECT :

อัคคะภัทร์ จิระอารีย์บุตร ส-สถ.3040

403 ซ.พัฒนาการ 50 พัฒนาการ

กรุงเทพมหานคร 10250

INTERIOR DESIGNER :

–

STRUCTURAL ENGINEER :

นายพงษ์ธวิทย์ คฑาวุธเจริญกุล สย.12291

ELECTRICAL ENGINEER :

นายภาคภูมิ คำพิทูรย์ สพก.5587

MECHANICAL ENGINEER :

SANITARY ENGINEER :

นส.อรวรรณ พลตรี สส.134

DRAWING TITLE

แปลนพื้นชั้น (2)

DRAWING FOR CONSTRUCTION

DRAW BY :	CHECKER :	REVISION :
Weerayuth L.	Akapatr C.	–

SCALE :	DRAWING NO.
1 : 100	A-P02
DATE : 04-12-2024	
FILE NAME :	JOB NO.

REVISION	DESCRIPTION

GERNERAL NOTE


DO NOT SCALE DRAWING ALL MEASUREMENT MUST BE CHECKED AT THE SIDE BY THE CONTRACTOR

ALL DESIGN AND DRAWINGS ARE THE PROPERTY OF MARCHTEN CO.,LTD AND NOT BE USED WITH OUT THEIR WRITTEN PERMISSION

MARCHTEN

ARCHITECTURE / INTERIOR

บริษัท มาร์ชเทน จำกัด
403 ซ.พัฒนาการ 50 สวนหลวง กรุงเทพมหานคร 10250

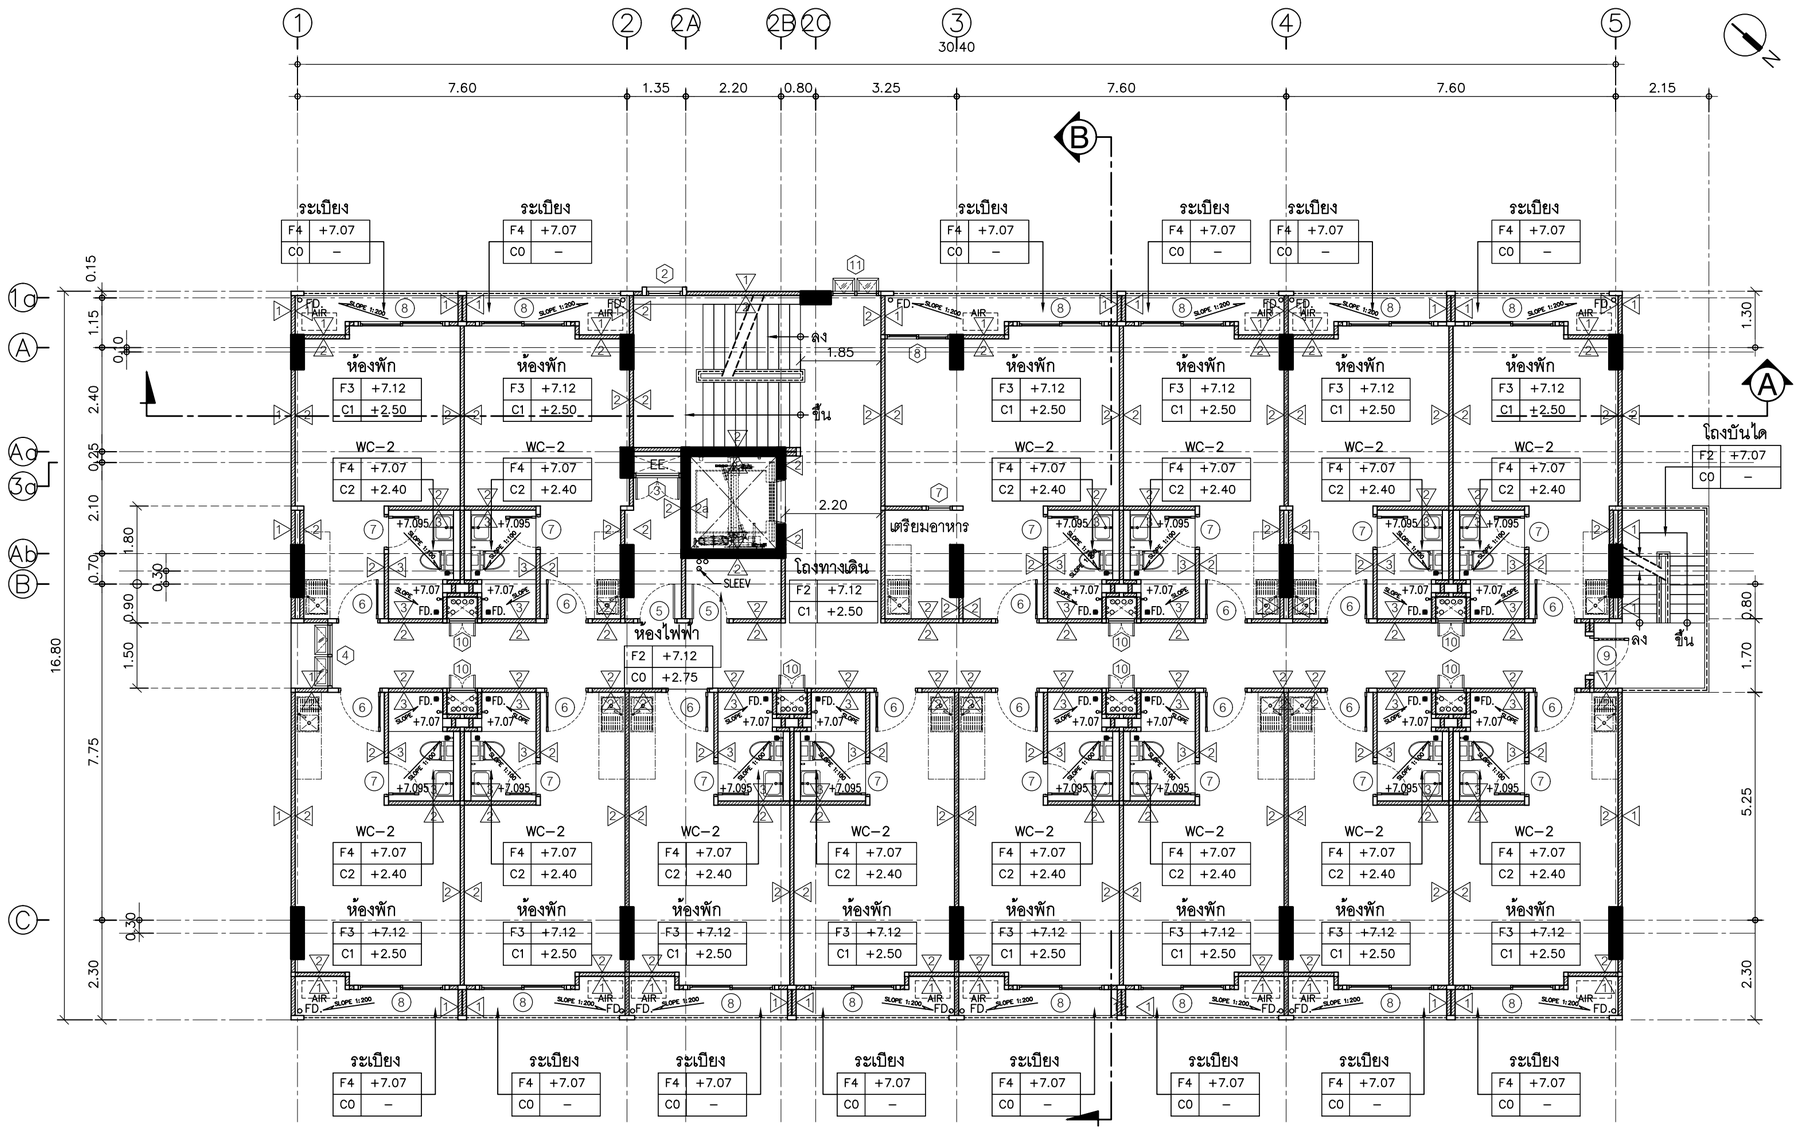

แปลนพื้นชั้น (3)–(5)

SCALE 1:100

PROJECT NUMBER : VC2023–024

PROJECT

MACHI RESIDENCES

อาคารพักอาศัยรวม ค.ส.ล 7 ชั้น

OWNER

บริษัท ฤทธิกร ลิฟวิ่ง จำกัด

ARCHITECT :

อัคคะภัทร์ จิระอารีย์บุตร ส–สถ.3040

403 ซ.พัฒนาการ 50 พัฒนาการ

กรุงเทพมหานคร 10250

INTERIOR DESIGNER :

–

STRUCTURAL ENGINEER :

นายพงษ์ธวิทย์ คฑาวุธเจริญกุล สย.12291

ELECTRICAL ENGINEER :

นายภาคภูมิ คำพิทูรย์ สพก.5587

MECHANICAL ENGINEER :

SANITARY ENGINEER :

นส.อรวรรณ พลตรี สส.134

DRAWING TITLE

แปลนพื้นชั้น (3)–(5)

DRAWING FOR CONSTRUCTION

DRAW BY :	CHECKER :	REVISION :
Weerayuth L.	Akapatr C.	–

SCALE :	DRAWING NO.
1 : 100	A-P03
DATE : 04–12–2024	
FILE NAME :	JOB NO.


REVISION	DESCRIPTION

GERNERAL NOTE

DO NOT SCALE DRAWING ALL MEASUREMENT MUST BE CHECKED AT THE SIDE BY THE CONTRACTOR

ALL DESIGN AND DRAWINGS ARE THE PROPERTY OF MARCHTEN CO.,LTD AND NOT BE USED WITH OUT THEIR WRITTEN PERMISSION

MARCHTEN
ARCHITECTURE / INTERIOR
บริษัท มาร์ชเทน จำกัด
403 ซ.พัฒนาการ 50 สวนหลวง กรุงเทพมหานคร 10250

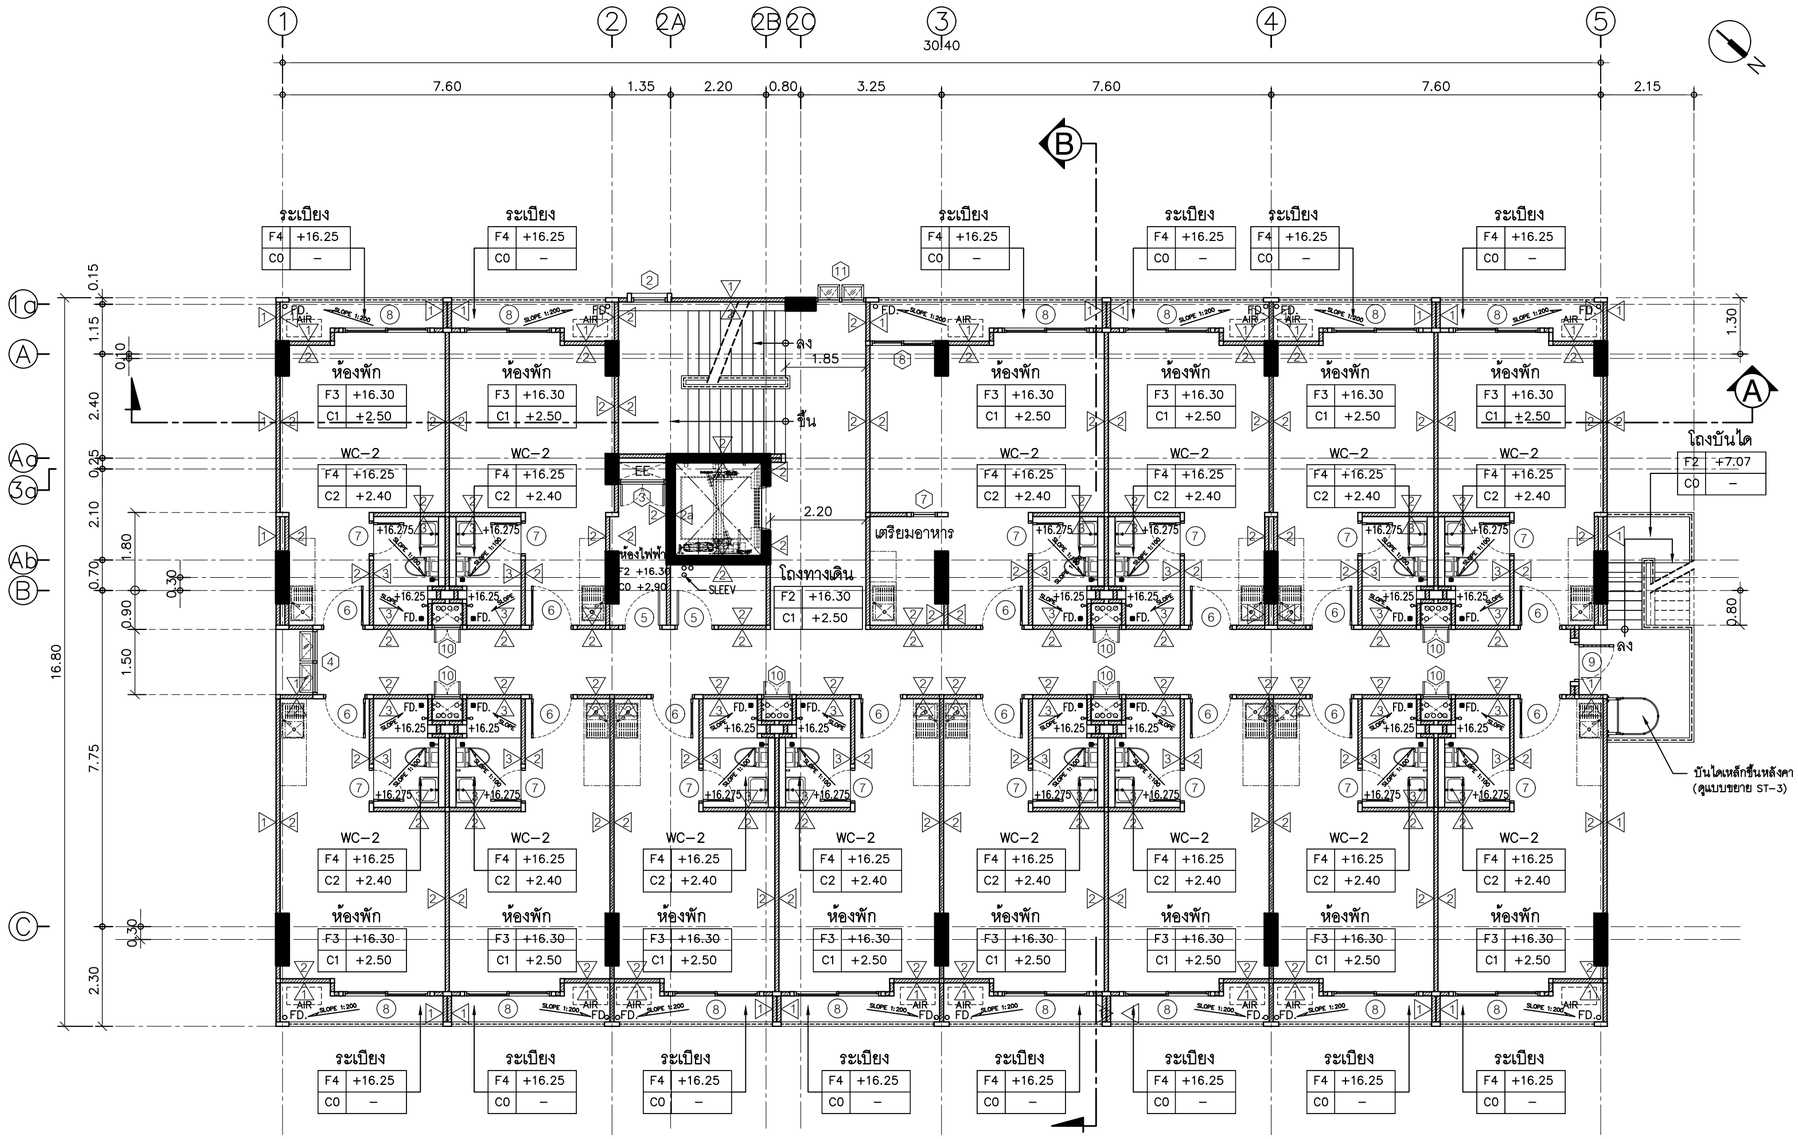

แปลนพื้นชั้น (6)

SCALE 1:100

PROJECT NUMBER : VC2023-024

PROJECT

MACHI RESIDENCES

อาคารพักอาศัยรวม ค.ส.ล 7 ชั้น

OWNER

บริษัท ฤทธิกร ลิฟวิ่ง จำกัด

ARCHITECT :

อัคคะภัทร์ จิระอารีย์บุตร ส-สถ.3040

403 ซ.พัฒนาการ 50 พัฒนาการ

กรุงเทพมหานคร 10250

INTERIOR DESIGNER :

–

STRUCTURAL ENGINEER :

นายพงษ์ธวิทย์ คทาวุธเจริญกุล สย.12291

ELECTRICAL ENGINEER :

นายภาคภูมิ คำพิทูรย์ สพก.5587

MECHANICAL ENGINEER :

SANITARY ENGINEER :

นส.อรวรรณ พลตรี สส.134

DRAWING TITLE

แปลนพื้นชั้น (6)

DRAWING FOR CONSTRUCTION

DRAW BY :	CHECKER :	REVISION :
Weerayuth L.	Akapatr C.	–

SCALE :	DRAWING NO.
1 : 100	A-P04
DATE : 04-12-2024	
FILE NAME :	JOB NO.

REVISION	DESCRIPTION


GERNERAL NOTE

DO NOT SCALE DRAWING ALL MEASUREMENT MUST BE CHECKED AT THE SIDE BY THE CONTRACTOR

ALL DESIGN AND DRAWINGS ARE THE PROPERTY OF MARCHTEN CO.,LTD AND NOT BE USED WITH OUT THEIR WRITTEN PERMISSION

MARCHTEN
ARCHITECTURE / INTERIOR

บริษัท มาร์ชเทน จำกัด
403 ซ.พัฒนาการ 50 สวนหลวง กรุงเทพมหานคร 10250

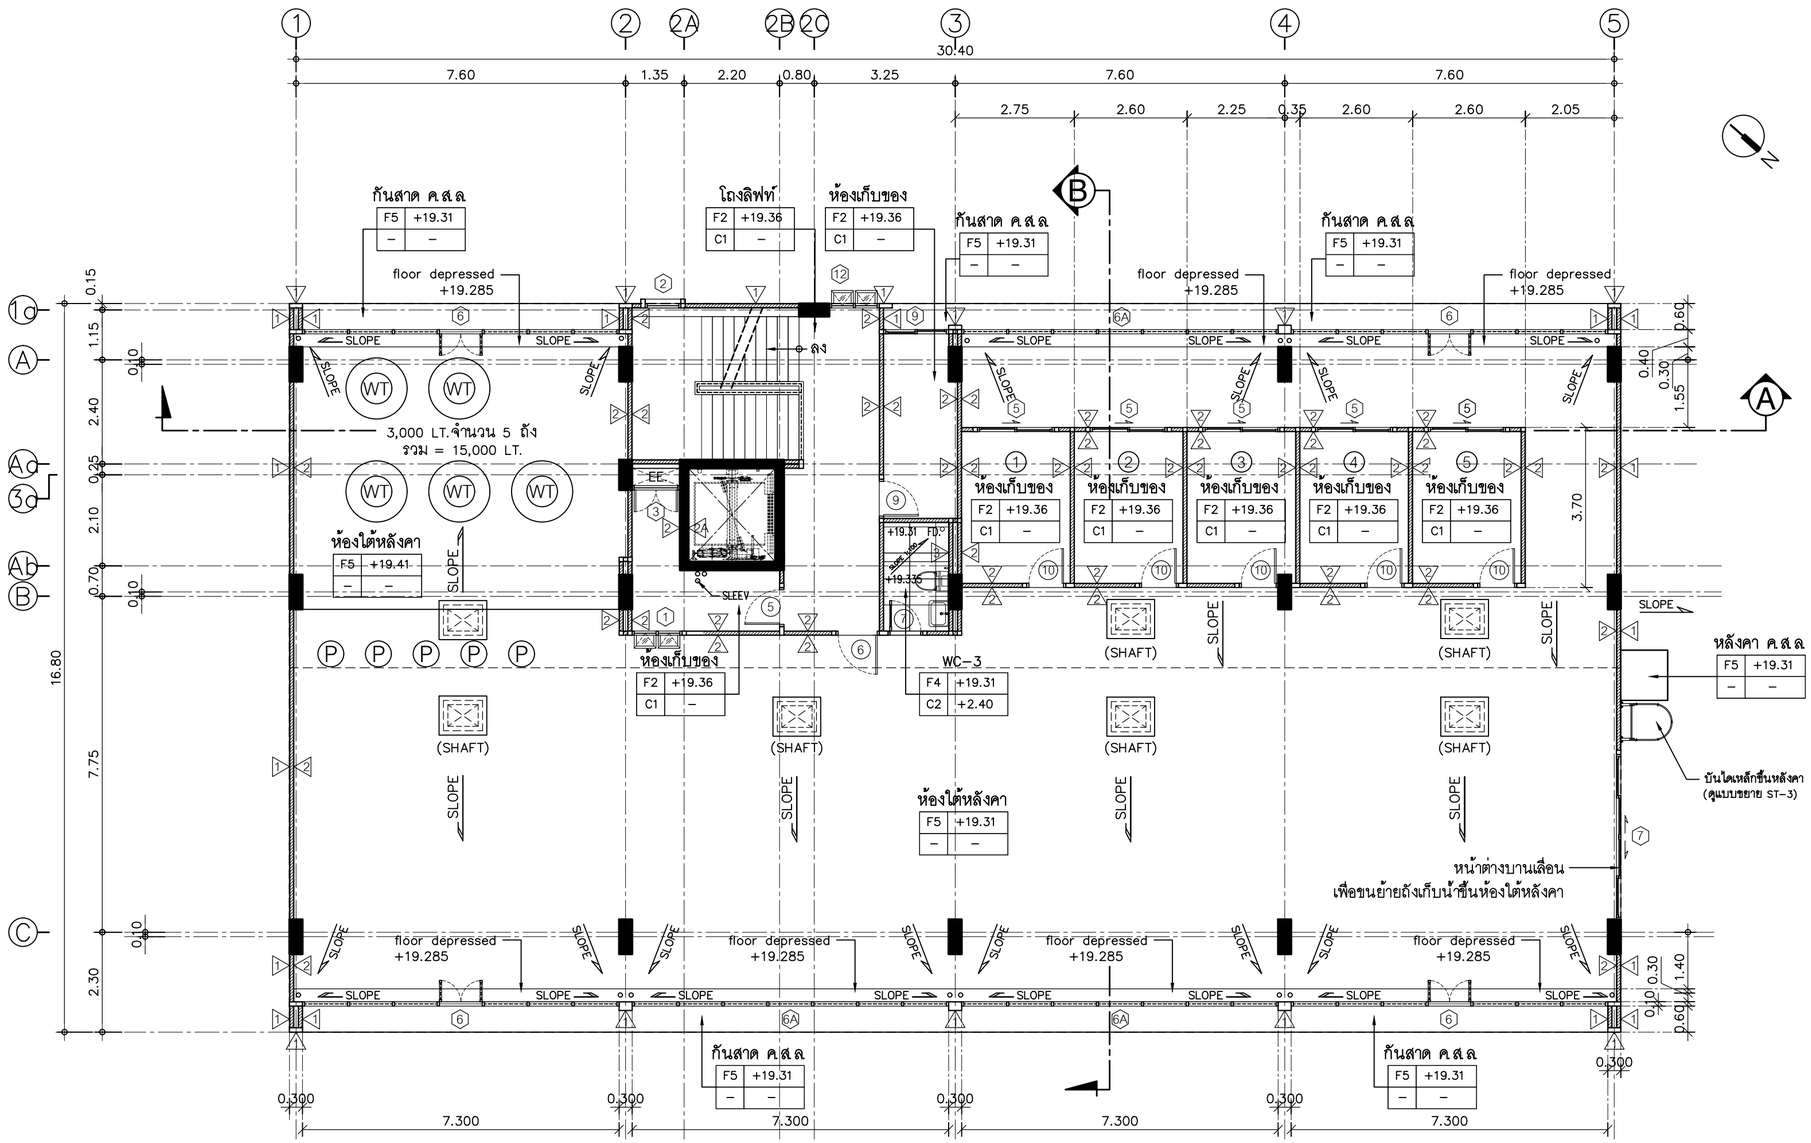

แปลนพื้นห้องใต้หลังคา


SCALE 1:100

PROJECT NUMBER : VC2023-024	
PROJECT	MACHI RESIDENCES อาคารพักอาศัยรวม คสล 7 ชั้น
OWNER	บริษัท ฤทธิกร ลิฟวิ่ง จำกัด
ARCHITECT :	อัคคะภัทร์ จิระอารีย์บุตร ส-สถ.3040 403 ซ.พัฒนาการ 50 พัฒนาการ กรุงเทพมหานคร 10250
INTERIOR DESIGNER :	–
STRUCTURAL ENGINEER :	นายพงษ์ธวิทย์ คฑาวุธเจริญกุล สย.12291
ELECTRICAL ENGINEER :	นายภาคภูมิ คำพิทูรย์ สพก.5587
MECHANICAL ENGINEER :	
SANITARY ENGINEER :	นส.อรวรรณ พลตรี สส.134
DRAWING TITLE	แปลนพื้นห้องใต้หลังคา
DRAWING FOR CONSTRUCTION	
DRAW BY : Weerayuth L.	CHECKER : Akapatr C.
REVISION : –	
SCALE : 1 : 100	DRAWING NO. A-P05
DATE : 04-12-2024	
FILE NAME :	JOB NO.

REVISION	DESCRIPTION

GERNERAL NOTE
DO NOT SCALE DRAWING ALL MEASUREMENT MUST BE CHECKED AT THE SIDE BY THE CONTRACTOR
ALL DESIGN AND DRAWINGS ARE THE PROPERTY OF MARCHTEN CO.,LTD AND NOT BE USED WITH OUT THEIR WRITTEN PERMISSION

MARCHTEN
ARCHITECTURE / INTERIOR
บริษัท มาร์ชเทน จำกัด
403 ซ.พัฒนาการ 50 สวนหลวง กรุงเทพมหานคร 10250

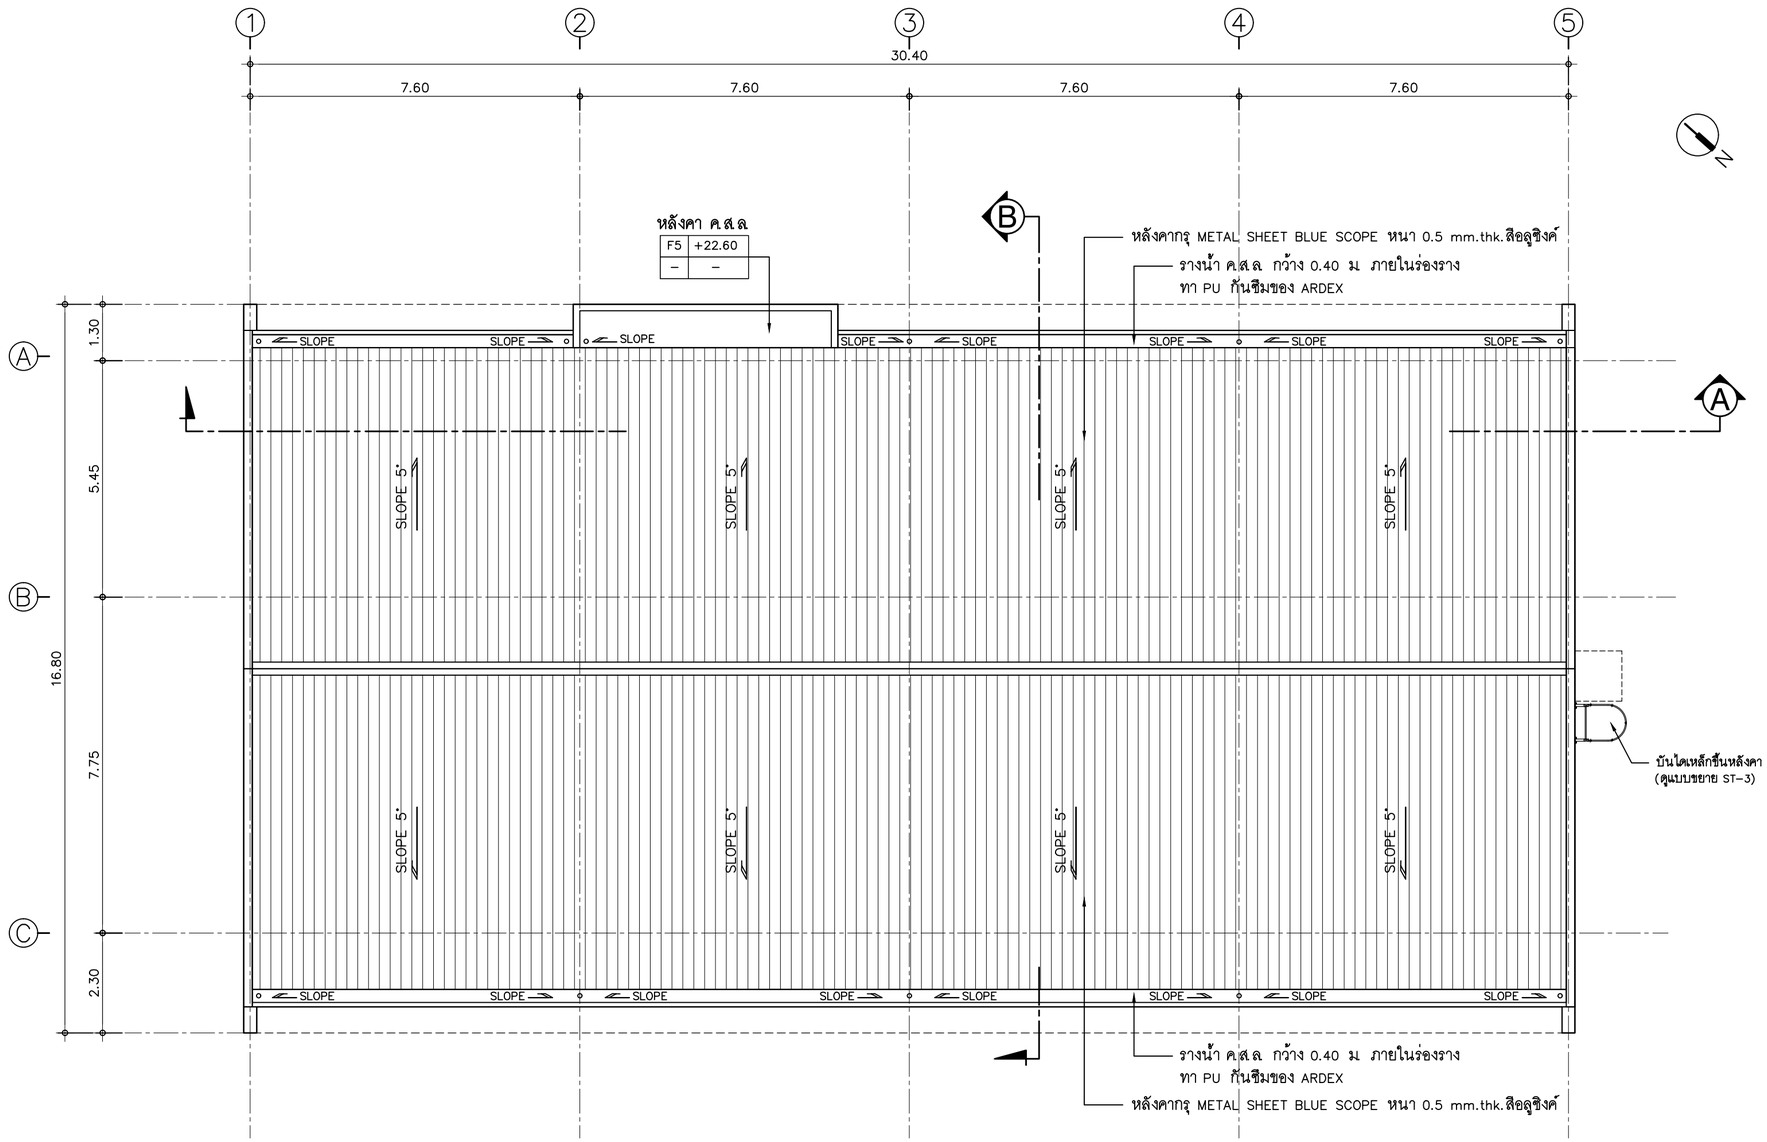



แปลนหลังคา

SCALE 1:100

PROJECT NUMBER : VC2023-024

PROJECT

MACHI RESIDENCES

อาคารพักอาศัยรวม ค.ส.ล 7 ชั้น

OWNER

บริษัท ฤทธิกร ลิฟวิ่ง จำกัด

ARCHITECT :

อัคคะภัทร์ จิระอารีย์บุตร ส-สถ.3040

403 ซ.พัฒนาการ 50 พัฒนาการ

กรุงเทพมหานคร 10250

INTERIOR DESIGNER :

–

STRUCTURAL ENGINEER :

นายพงษ์ธวิทย์ คฑาวุธเจริญกุล สย.12291

ELECTRICAL ENGINEER :

นายภาคภูมิ คำพิทูรย์ สฟก.5587

MECHANICAL ENGINEER :

SANITARY ENGINEER :

นส.อรวรรณ พลตรี สส.134

DRAWING TITLE

แปลนหลังคา

DRAWING FOR CONSTRUCTION

DRAW BY :	CHECKER :	REVISION :
Weerayuth L.	Akapatr C.	–

SCALE :	DRAWING NO.
1 : 100	A-P06
DATE : 04-12-2024	
FILE NAME :	JOB NO.

REVISION	DESCRIPTION

GERNERAL NOTE

DO NOT SCALE DRAWING ALL MEASUREMENT MUST BE CHECKED AT THE SIDE BY THE CONTRACTOR


ALL DESIGN AND DRAWINGS ARE THE PROPERTY OF MARCHTEN CO.,LTD AND NOT BE USED WITH OUT THEIR WRITTEN PERMISSION

MARCHTEN

ARCHITECTURE / INTERIOR

บริษัท มาร์ชเทน จำกัด

403 ซ.พัฒนาการ 50 สวนหลวง กรุงเทพมหานคร 10250

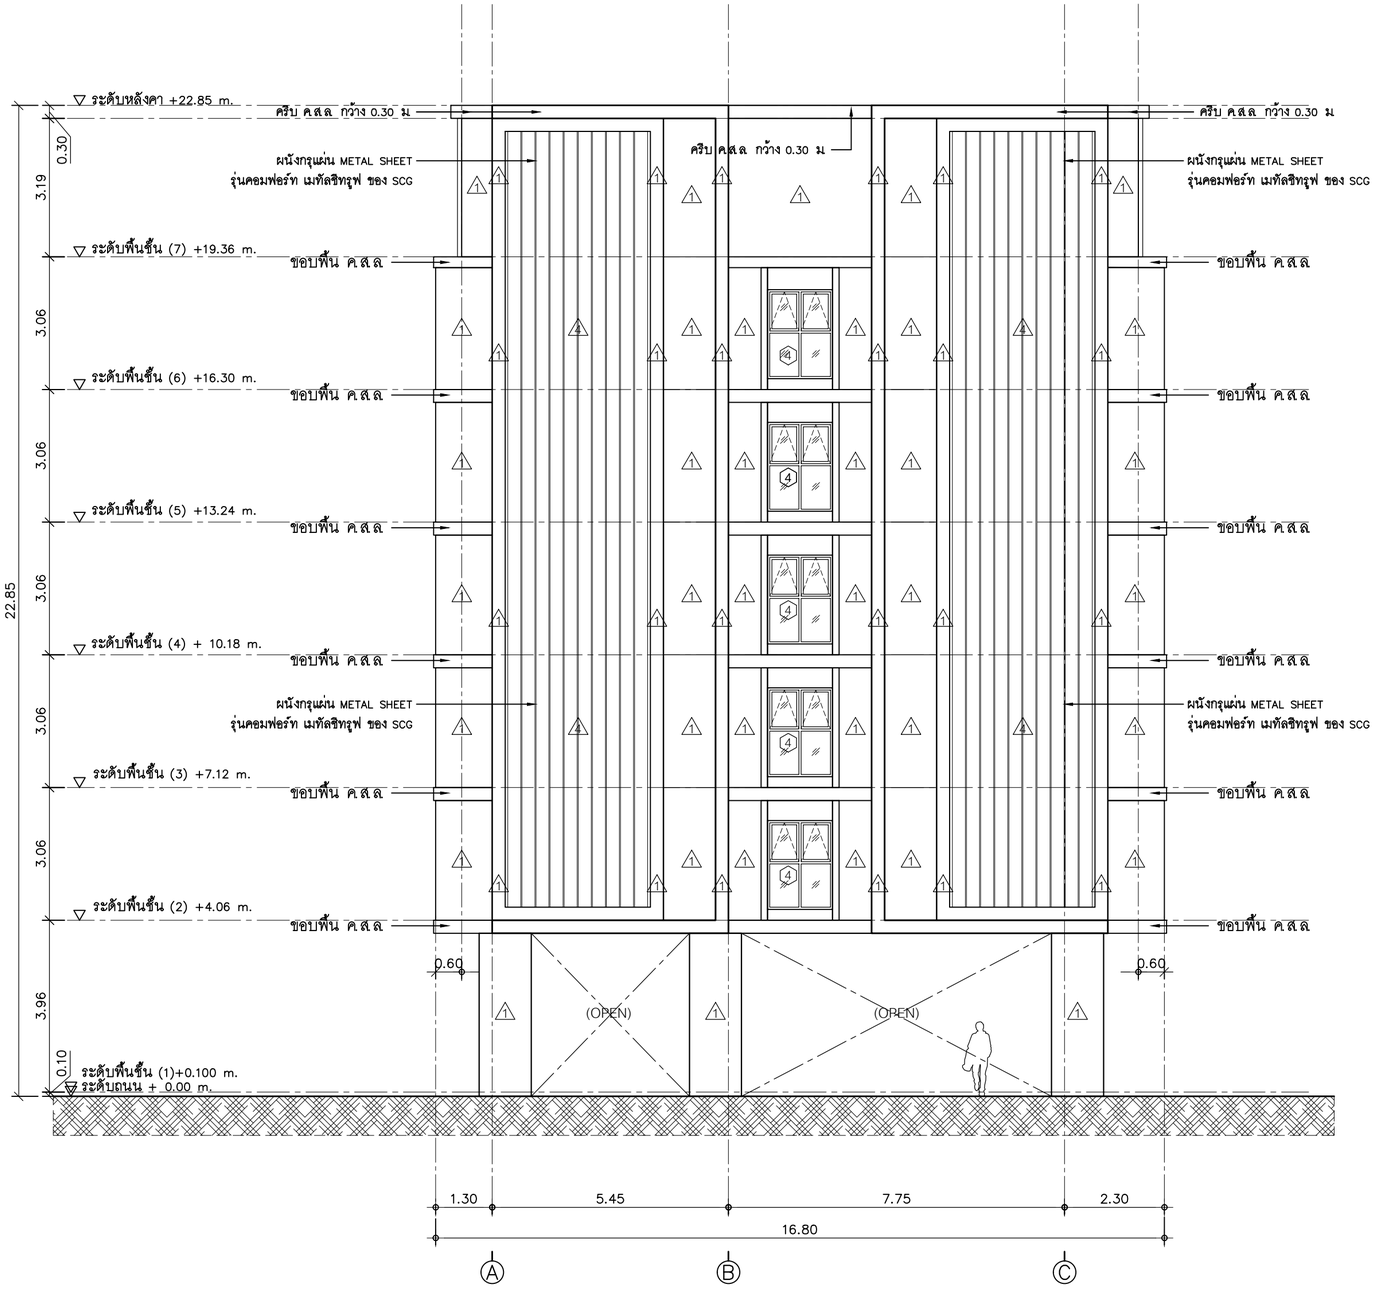

รูปด้าน (1)

SCALE 1:100

PROJECT NUMBER : VC2023-024

PROJECT

MACHI RESIDENCES

อาคารพักอาศัยรวม คสล 7 ชั้น

OWNER

บริษัท ฤทธิกร ลิฟวิ่ง จำกัด

ARCHITECT :

อัคคะภัทร์ จิระอารีย์บุตร ส-สถ.3040

403 ซ.พัฒนาการ 50 พัฒนาการ

กรุงเทพมหานคร 10250

INTERIOR DESIGNER :

–

STRUCTURAL ENGINEER :

นายพงษ์ธวิทย์ คทาวุธเจริญกุล สย.12291

ELECTRICAL ENGINEER :

นายภาคภูมิ คำพิทูรย์ สพก.5587

MECHANICAL ENGINEER :

SANITARY ENGINEER :

นส.อรวรรณ พลตรี สส.134

DRAWING TITLE

รูปด้าน (1)

DRAWING FOR CONSTRUCTION

DRAW BY :	CHECKER :	REVISION :
Weerayuth L.	Akapatr C.	–

SCALE :	DRAWING NO.
1 : 100	A-E01
DATE : 04-12-2024	
FILE NAME :	JOB NO.

REVISION	DESCRIPTION

GERNERAL NOTE

DO NOT SCALE DRAWING ALL MEASUREMENT MUST BE CHECKED AT THE SIDE BY THE CONTRACTOR

ALL DESIGN AND DRAWINGS ARE THE PROPERTY OF MARCHTEN CO.,LTD AND NOT BE USED WITH OUT THEIR WRITTEN PERMISSION

MARCHTEN

ARCHITECTURE / INTERIOR

บริษัท มาร์เทน จำกัด

403 ซ.พัฒนาการ 50 สวนหลวง กรุงเทพมหานคร 10250



รูปด้าน (2)

SCALE 1:100

PROJECT NUMBER : VC2023-024

PROJECT

MACHI RESIDENCES

อาคารพักอาศัยรวม คสล 7 ชั้น

OWNER

บริษัท ฤทธิกร ลิฟวิ่ง จำกัด

ARCHITECT :

อัคคะภัทร์ จิระอารีย์บุตร ส-สถ.3040

403 ซ.พัฒนาการ 50 พัฒนาการ

กรุงเทพมหานคร 10250

INTERIOR DESIGNER :

–

STRUCTURAL ENGINEER :

นายพงษ์ธวิทย์ คทาวุธเจริญกุล สย.12291

ELECTRICAL ENGINEER :

นายภาคภูมิ คำพิทูรย์ สฟก.5587

MECHANICAL ENGINEER :

SANITARY ENGINEER :

นส.อรวรรณ พลตรี สส.134

DRAWING TITLE

รูปด้าน (2)

DRAWING FOR CONSTRUCTION

DRAW BY :	CHECKER :	REVISION :
Weerayuth L.	Akapatr C.	–

SCALE :	DRAWING NO.
1 : 100	A-E02
DATE : 04-12-2024	
FILE NAME :	JOB NO.

REVISION	DESCRIPTION

GERNERAL NOTE

DO NOT SCALE DRAWING ALL MEASUREMENT MUST BE CHECKED AT THE SIDE BY THE CONTRACTOR


ALL DESIGN AND DRAWINGS ARE THE PROPERTY OF MARCHTEN CO.,LTD AND NOT BE USED WITH OUT THEIR WRITTEN PERMISSION

MARCHTEN

ARCHITECTURE / INTERIOR

บริษัท มาร์ชเทน จำกัด

403 ซ.พัฒนาการ 50 สวนหลวง กรุงเทพมหานคร 10250

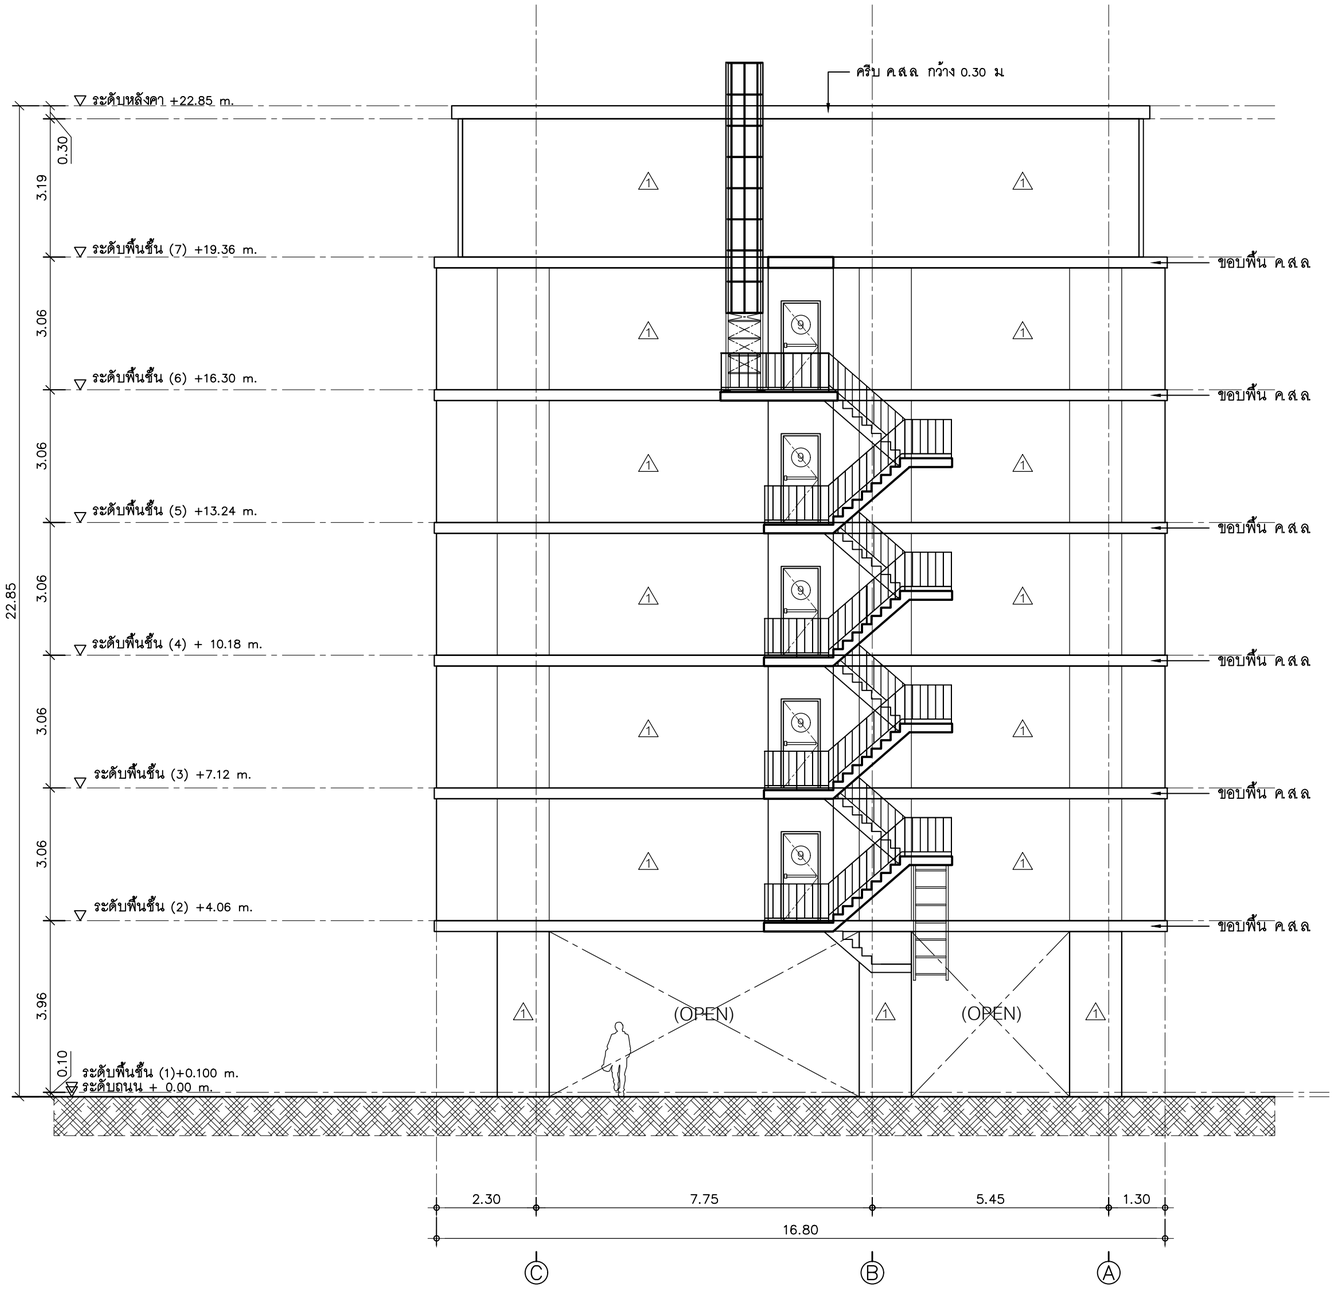

รูปด้าน (3)

SCALE 1:100

PROJECT NUMBER : VC2023-024

PROJECT

MACHI RESIDENCES

อาคารพักอาศัยรวม คสล 7 ชั้น

OWNER

บริษัท ฤทธิกร ลิฟวิ่ง จำกัด

ARCHITECT :

อัคคะภัทร์ จิระอารีย์บุตร ส-สถ.3040

403 ซ.พัฒนาการ 50 พัฒนาการ

กรุงเทพมหานคร 10250

INTERIOR DESIGNER :

–

STRUCTURAL ENGINEER :

นายพงษ์ธวิทย์ คทาวุธเจริญกุล สย.12291

ELECTRICAL ENGINEER :

นายภาคภูมิ คำพิทูรย์ สพก.5587

MECHANICAL ENGINEER :

SANITARY ENGINEER :

นส.อรวรรณ พลตรี สส.134

DRAWING TITLE

รูปด้าน (3)

DRAWING FOR CONSTRUCTION

DRAW BY :	CHECKER :	REVISION :
Weerayuth L.	Akapatr C.	–

SCALE :	DRAWING NO.
1 : 100	A-E03
DATE : 04-12-2024	
FILE NAME :	JOB NO.

REVISION	DESCRIPTION

GERNERAL NOTE

DO NOT SCALE DRAWING ALL MEASUREMENT MUST BE CHECKED AT THE SIDE BY THE CONTRACTOR


ALL DESIGN AND DRAWINGS ARE THE PROPERTY OF MARCHTEN CO.,LTD AND NOT BE USED WITH OUT THEIR WRITTEN PERMISSION

MARCHTEN

ARCHITECTURE / INTERIOR

บริษัท มาร์ชเทน จำกัด

403 ซ.พัฒนาการ 50 สวนหลวง กรุงเทพมหานคร 10250

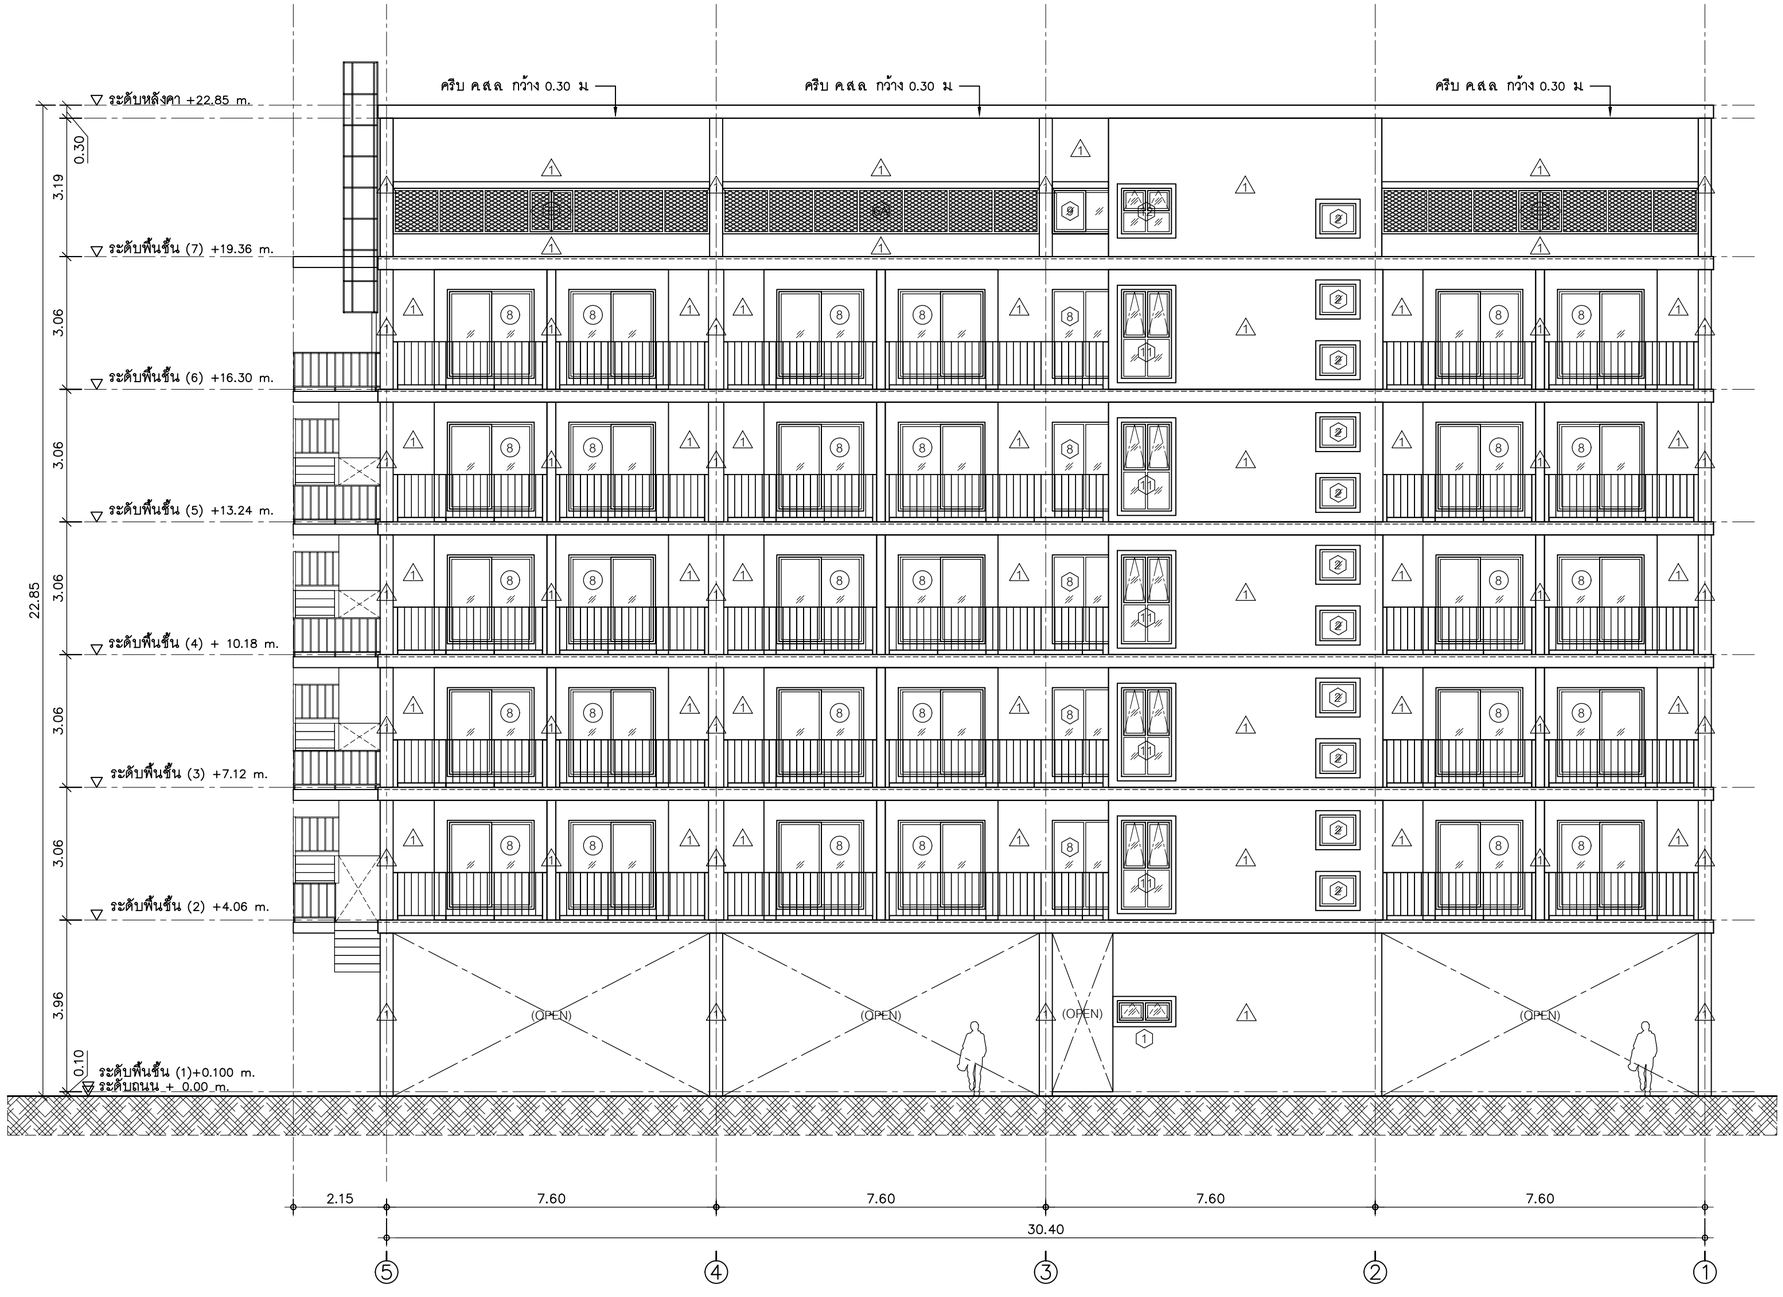

รูปด้าน (4)

SCALE 1:100

PROJECT NUMBER : VC2023-024

PROJECT

MACHI RESIDENCES

อาคารพักอาศัยรวม คสล 7 ชั้น

OWNER

บริษัท ฤทธิกร ลิฟวิ่ง จำกัด

ARCHITECT :

อัคคะภัทร์ จิระอารีย์บุตร ส-สถ.3040

403 ซ.พัฒนาการ 50 พัฒนาการ

กรุงเทพมหานคร 10250

INTERIOR DESIGNER :

–

STRUCTURAL ENGINEER :

นายพงษ์ธวิทย์ คทาวุธเจริญกุล สย.12291

ELECTRICAL ENGINEER :

นายภาคภูมิ คำพิทูรย์ สพก.5587

MECHANICAL ENGINEER :

SANITARY ENGINEER :

นส.อรวรรณ พลตรี สส.134

DRAWING TITLE

รูปด้าน (4)

DRAWING FOR CONSTRUCTION

DRAW BY :	CHECKER :	REVISION :
Weerayuth L.	Akapatr C.	–

SCALE :	DRAWING NO.
1 : 100	A-E04
DATE : 04-12-2024	
FILE NAME :	JOB NO.

REVISION	DESCRIPTION

GERNERAL NOTE


DO NOT SCALE DRAWING ALL MEASUREMENT MUST BE CHECKED AT THE SIDE BY THE CONTRACTOR

ALL DESIGN AND DRAWINGS ARE THE PROPERTY OF MARCHTEN CO.,LTD AND NOT BE USED WITH OUT THEIR WRITTEN PERMISSION

MARCHTEN

ARCHITECTURE / INTERIOR

บริษัท มาร์ชเทน จำกัด
403 ซ.พัฒนาการ 50 สวนหลวง กรุงเทพมหานคร 10250

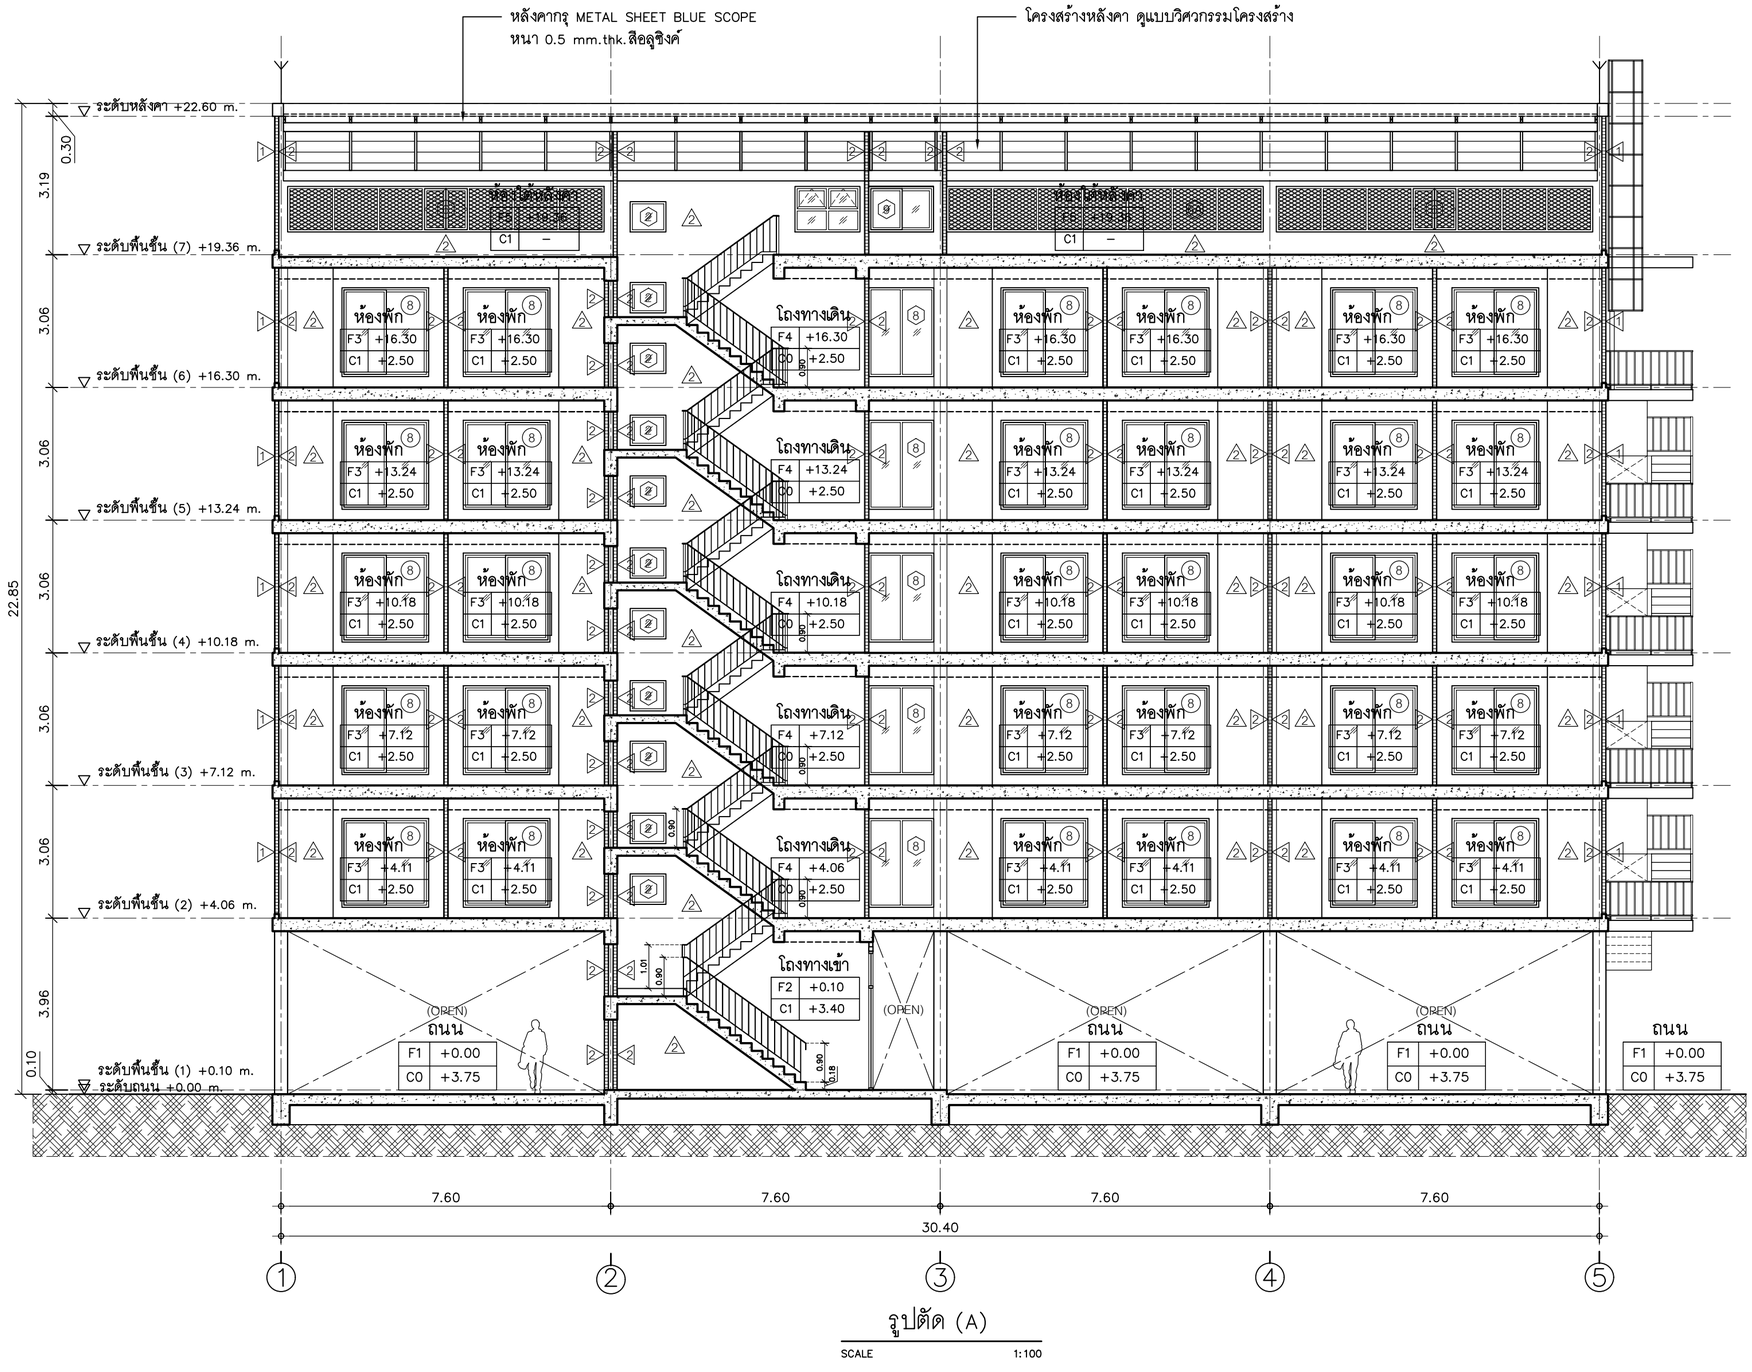

รูปตัด (A)

SCALE 1:100

PROJECT NUMBER : VC2023-024

PROJECT

MACHI RESIDENCES

อาคารพักอาศัยรวม ค.ส.ล 7 ชั้น

OWNER

บริษัท ฤทธิกร ลิฟวิ่ง จำกัด

ARCHITECT :

อัคคะภัทร์ จิระอารีย์บุตร ส-สถ.3040

403 ซ.พัฒนาการ 50 พัฒนาการ

กรุงเทพมหานคร 10250

INTERIOR DESIGNER :

–

STRUCTURAL ENGINEER :

นายพงษ์ธวิทย์ คทาวุธเจริญกุล สย.12291

ELECTRICAL ENGINEER :

นายภาคภูมิ คำพิทูรย์ สพก.5587

MECHANICAL ENGINEER :

SANITARY ENGINEER :

นส.อรวรรณ พลตรี สส.134

DRAWING TITLE

รูปตัด (A)

DRAWING FOR CONSTRUCTION

DRAW BY :	CHECKER :	REVISION :
Weerayuth L.	Akapatr C.	–

SCALE : 1 : 100

DRAWING NO. A-S01

DATE : 04-12-2024

FILE NAME :

JOB NO.


REVISION	DESCRIPTION

GERNERAL NOTE

DO NOT SCALE DRAWING ALL MEASUREMENT MUST BE CHECKED AT THE SIDE BY THE CONTRACTOR

ALL DESIGN AND DRAWINGS ARE THE PROPERTY OF MARCHTEN CO.,LTD AND NOT BE USED WITH OUT THEIR WRITTEN PERMISSION

MARCHTEN
ARCHITECTURE / INTERIOR
บริษัท มาร์ชเทน จำกัด
403 ซ.พัฒนาการ 50 สวนหลวง กรุงเทพมหานคร 10250

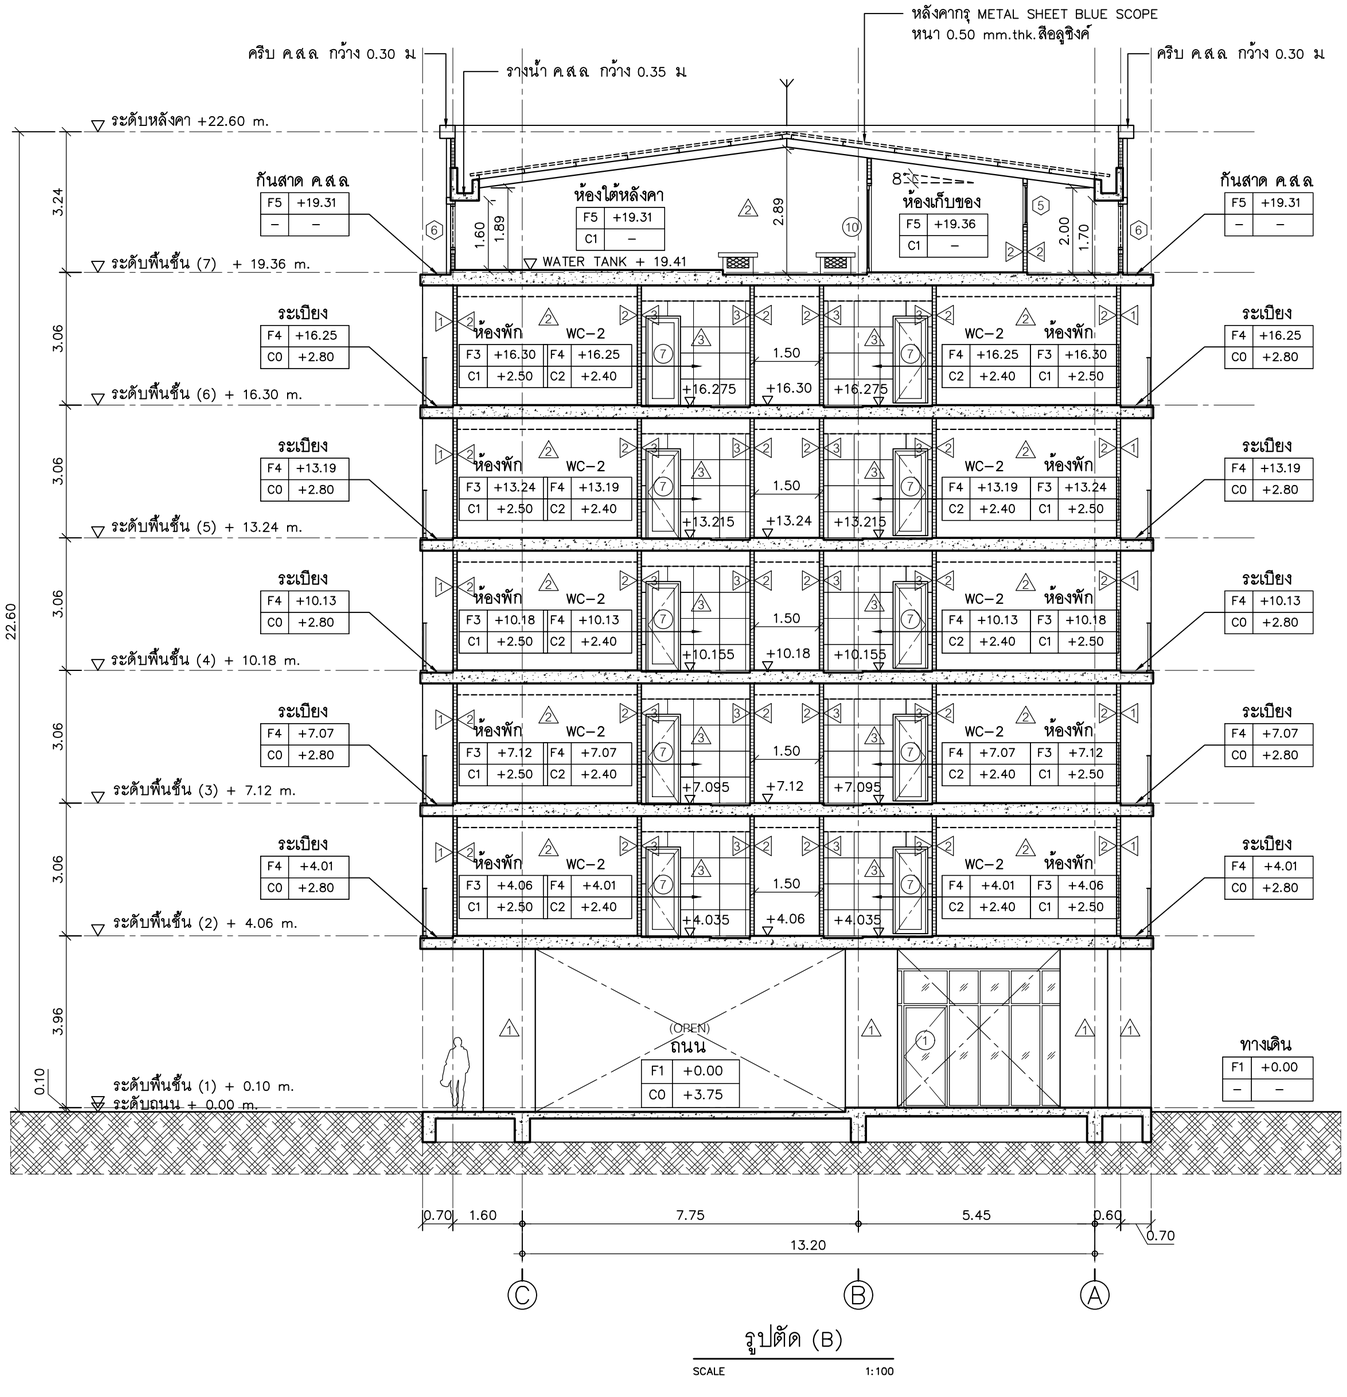

รูปตัด (B)

SCALE 1:100

PROJECT NUMBER : VC2023-024

PROJECT

MACHI RESIDENCES
อาคารพักอาศัยรวม คสล 7 ชั้น

OWNER

บริษัท ฤทธิกร ลิฟวิ่ง จำกัด

ARCHITECT :

อัคคะภัทร์ จิระอารีย์บุตร ส–สถ.3040
403 ซ.พัฒนาการ 50 พัฒนาการ
กรุงเทพมหานคร 10250

INTERIOR DESIGNER :

–

STRUCTURAL ENGINEER :

นายพงษ์ธวิทย์ คทาวุธเจริญกุล สย.12291

ELECTRICAL ENGINEER :

นายภาคภูมิ คำพิทูรย์ สฟก.5587

MECHANICAL ENGINEER :

SANITARY ENGINEER :

นส.อรวรรณ พลตรี สส.134

DRAWING TITLE

รูปตัด (B)

DRAWING FOR CONSTRUCTION


DRAW BY :	CHECKER :	REVISION :
Weerayuth L.	Akapatr C.	–

SCALE :	DRAWING NO.
1 : 100	A-S02
DATE : 04–12–2024	
FILE NAME :	JOB NO.

REVISION	DESCRIPTION


GERNERAL NOTE
DO NOT SCALE DRAWING ALL MEASUREMENT MUST BE CHECKED AT THE SIDE BY THE CONTRACTOR
ALL DESIGN AND DRAWINGS ARE THE PROPERTY OF MARCHTEN CO.,LTD AND NOT BE USED WITH OUT THEIR WRITTEN PERMISSION

MARCHTEN
ARCHITECTURE / INTERIOR
บริษัท มาร์ชเทน จำกัด
403 ซ.พัฒนาการ 50 สวนหลวง กรุงเทพมหานคร 10250

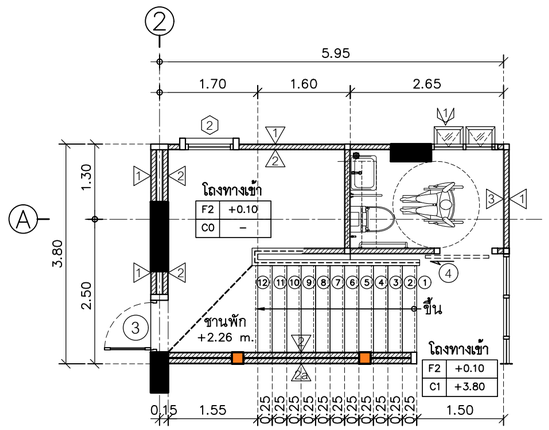


แปลนชั้น (1)–(2)

SCALE (ST–1) บันไดหลัก 1:75

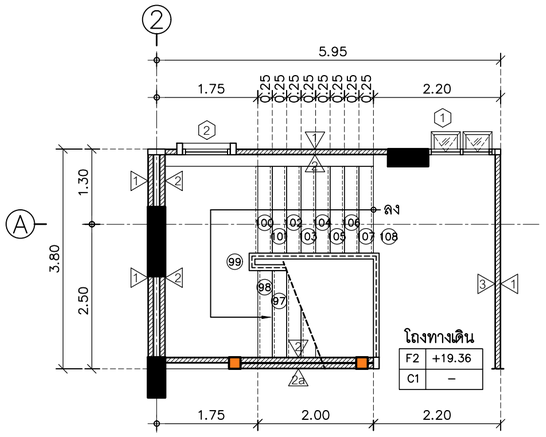


แปลนชั้น (7)

SCALE (ST–1) บันไดหลัก 1:75

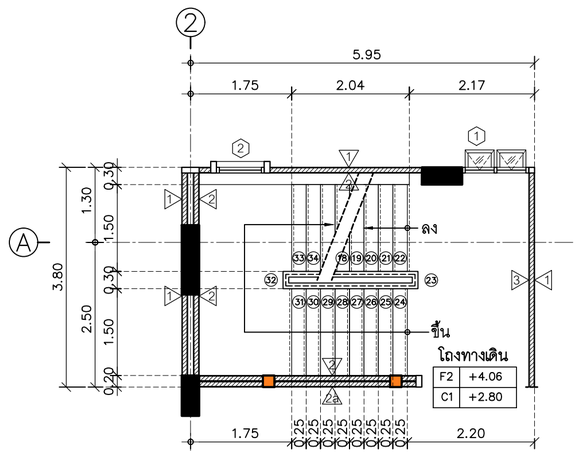

แปลนชั้น (2)–(6)


SCALE (ST–1) บันไดหลัก 1:75

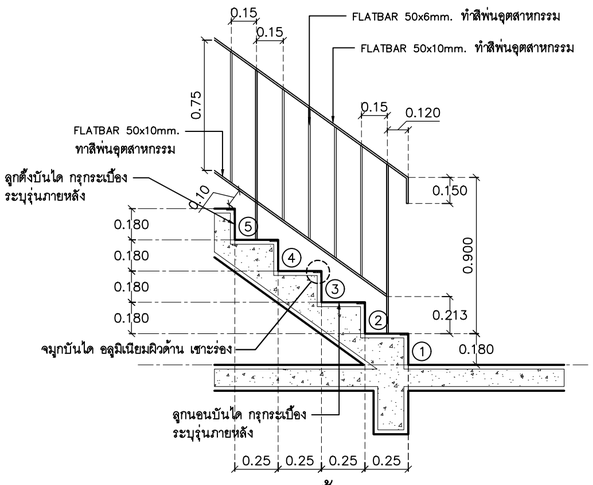

แบบขยายลูกตั้ง – ลูกนอน

SCALE 1:25

บันได (ST–1)

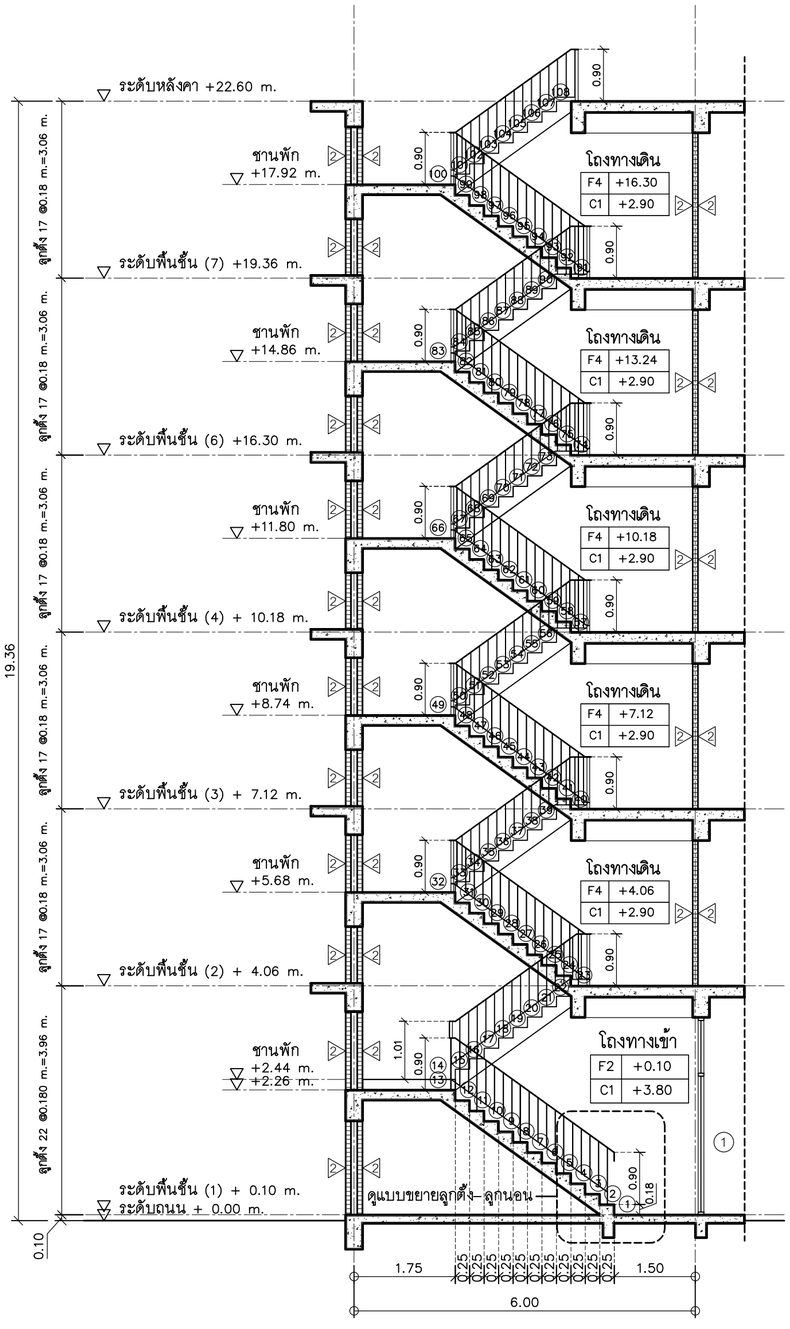

รูปตัด (A)

SCALE 1:75

แบบขยายบันได (ST–1)

PROJECT NUMBER : VC2023–024

PROJECT

MACHI RESIDENCES

อาคารพักอาศัยรวม ค.ส.ล 7 ชั้น

OWNER

บริษัท ฤทธิกร ลิฟวิ่ง จำกัด

ARCHITECT :

อัคคะภัทร์ จิระอารีย์บุตร ส–สถ.3040

403 ซ.พัฒนาการ 50 พัฒนาการ

กรุงเทพมหานคร 10250

INTERIOR DESIGNER :

–

STRUCTURAL ENGINEER :

นายพงษ์ธวิทย์ คทาวุธเจริญกุล สย.12291

ELECTRICAL ENGINEER :

นายภาคภูมิ คำพิทูรย์ สฟก.5587

MECHANICAL ENGINEER :

SANITARY ENGINEER :

นส.อรวรรณ พลตรี สส.134

DRAWING TITLE

แบบขยายบันได (ST–1)

DRAWING FOR CONSTRUCTION

DRAW BY :	CHECKER :	REVISION :
Weerayuth L.	Akapatr C.	–

SCALE : 1 : 100

DRAWING NO. A-D01

DATE : 04–12–2024

FILE NAME :


JOB NO.

REVISION	DESCRIPTION

GERNERAL NOTE
DO NOT SCALE DRAWING ALL MEASUREMENT MUST BE CHECKED AT THE SIDE BY THE CONTRACTOR
ALL DESIGN AND DRAWINGS ARE THE PROPERTY OF MARCHTEN CO.,LTD AND NOT BE USED WITH OUT THEIR WRITTEN PERMISSION


MARCHTEN
ARCHITECTURE / INTERIOR

บริษัท มาร์ชเทน จำกัด
403 ซ.พัฒนาการ 50 สวนหลวง กรุงเทพมหานคร 10250

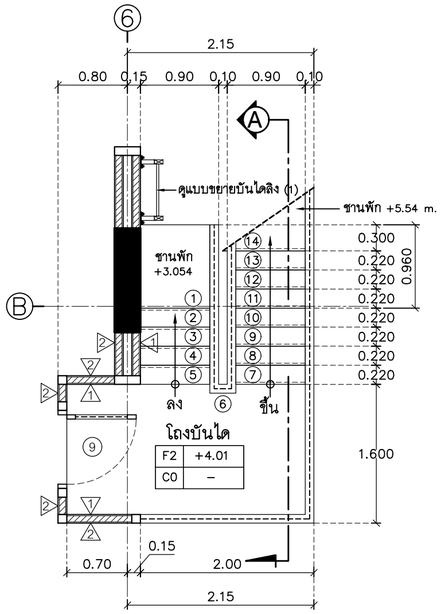


แปลนชั้น (2)–(3)

SCALE (ST–2) บันไดหนีไฟ 1:50

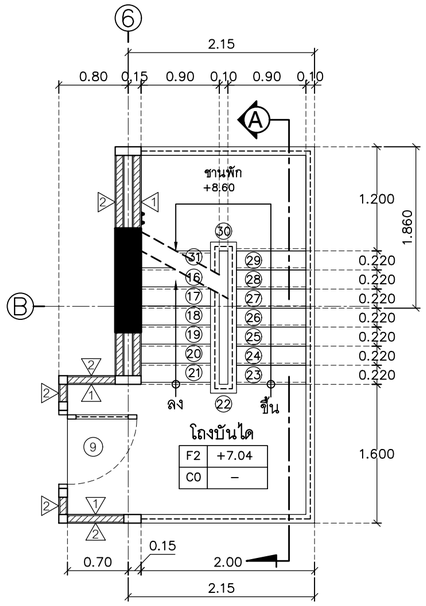


แปลนชั้น (3)–(5)

SCALE (ST–2) บันไดหนีไฟ 1:50

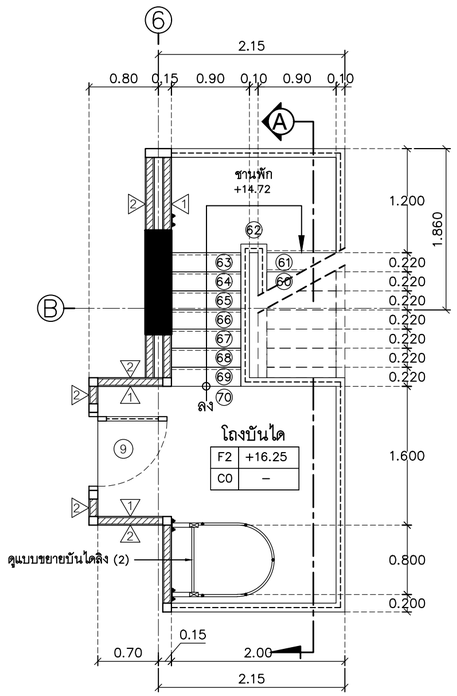


แปลนชั้น (6)

SCALE (ST–2) บันไดหนีไฟ 1:50

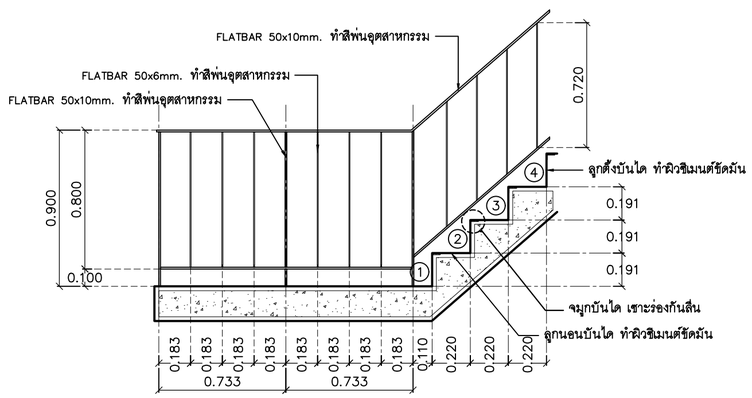

แบบขยายลูกตั้ง – ลูกนอน

SCALE บันไดหนีไฟ (ST–2) 1:25

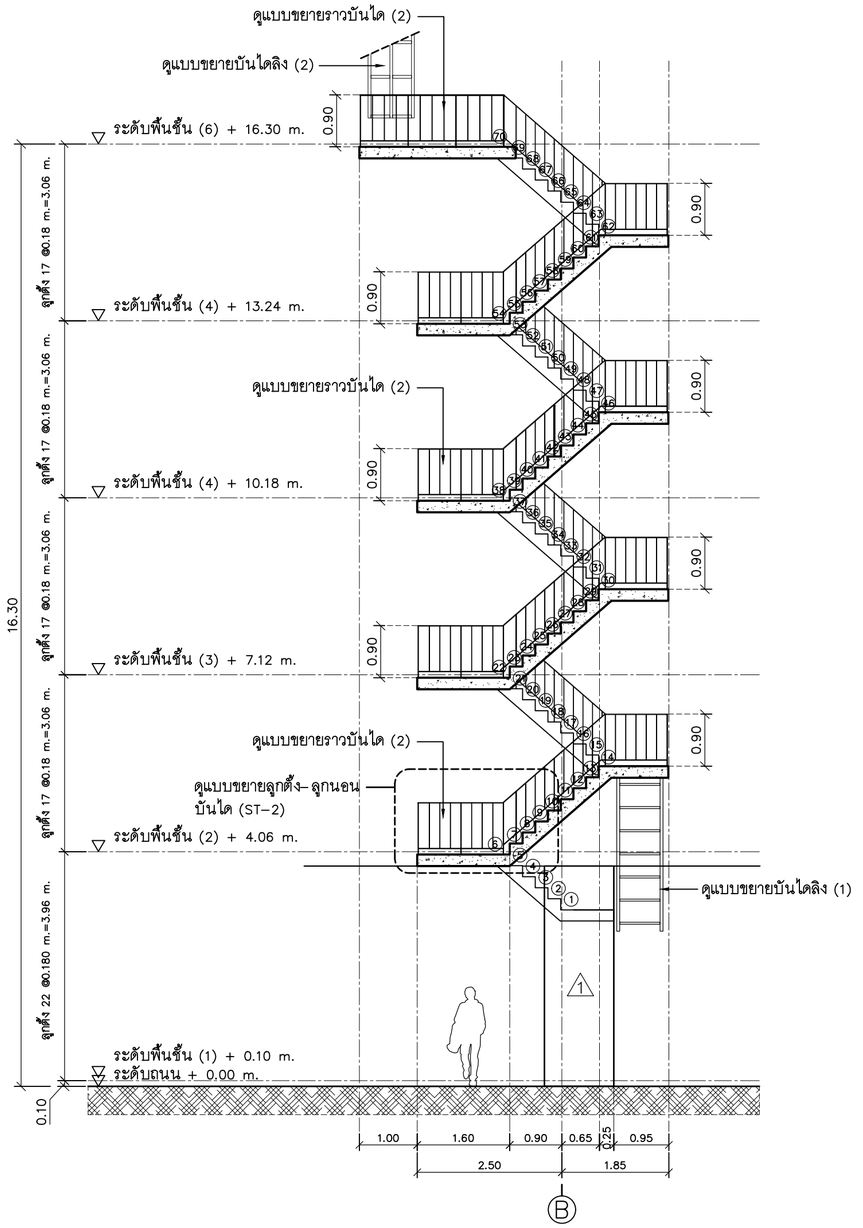

รูปตัด (A)

SCALE (ST–2) บันไดหนีไฟ 1:75

PROJECT NUMBER : VC2023–024

PROJECT

MACHI RESIDENCES

อาคารพักอาศัยรวม ค.ส.ล 7 ชั้น

OWNER

บริษัท ฤทธิกร ลิฟวิ่ง จำกัด

ARCHITECT :

อัคคะภัทร์ จิระอารีย์บุตร ส–สถ.3040

403 ซ.พัฒนาการ 50 พัฒนาการ

กรุงเทพมหานคร 10250

INTERIOR DESIGNER :

–

STRUCTURAL ENGINEER :

นายพงษ์ธวิทย์ คฑาวุธเจริญกุล สย.12291

ELECTRICAL ENGINEER :

นายภาคภูมิ คำพิทูรย์ สพก.5587

MECHANICAL ENGINEER :

SANITARY ENGINEER :

นส.อรวรรณ พลตรี สส.134

DRAWING TITLE

(ST–2) บันไดหนีไฟ

DRAWING FOR CONSTRUCTION

DRAW BY :	CHECKER :	REVISION :
Weerayuth L.	Akapatr C.	–

SCALE :	DRAWING NO.
1 : 100	A-D02
DATE : 04–12–2024	
FILE NAME :	JOB NO.

REVISION	DESCRIPTION

GERNERAL NOTE

DO NOT SCALE DRAWING ALL MEASUREMENT MUST BE CHECKED AT THE SIDE BY THE CONTRACTOR


ALL DESIGN AND DRAWINGS ARE THE PROPERTY OF MARCHTEN CO.,LTD AND NOT BE USED WITH OUT THEIR WRITTEN PERMISSION

MARCHTEN

ARCHITECTURE / INTERIOR

บริษัท มาร์เทน จำกัด

403 ซ.พัฒนาการ 50 สวนหลวง กรุงเทพมหานคร 10250

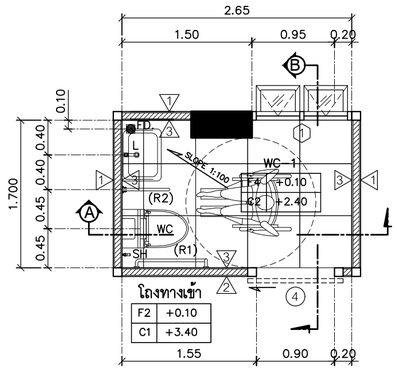

แปลนห้องน้ำ (WC-1)


SCALE 1:50

รายการประกอบแบบขยายห้องน้ำ

สัญลักษณ์	ความหมาย	ติดตั้งสูง/ ม.
WC.-1	โถส้วมชนิดนั่งราบ	-
L	อ่างล้างหน้า	0.80
T	ที่ใส่กระดาษชำระ	0.60
M	กระจกเงา	-
F.D.	รูระบายน้ำที่พื้น พร้อมตะแกรงกันผง Dia. 3"	


สัญลักษณ์	ความหมาย	ติดตั้งสูง/ ม.
(R1)	ราวจับทรงตัว รูปตัว L สูงจากพื้น 0.70 m.	
(R2)	ราวจับทรงตัวแบบพับเก็บได้ แนวดิ่ง	
SH.	สายชำระ	0.45
R	ราวแขวนผ้า	

หมายเหตุ สุขภัณฑ์ ทั้งหมดใช้ของ COTTO ระบุรุ่นและสีภายหลัง

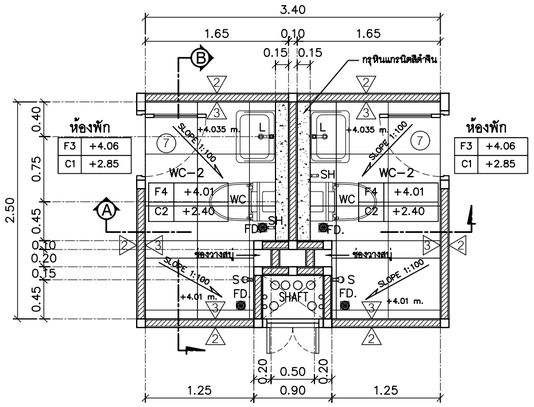


แปลนห้องน้ำ (WC-2)

SCALE 1:50

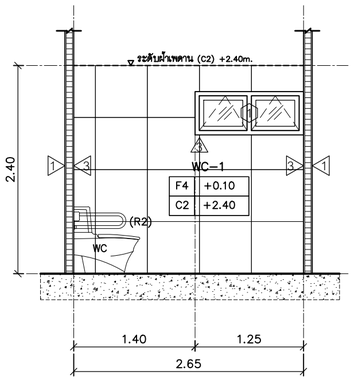


รูปตัด (A) ห้องน้ำ (WC-1)

SCALE 1:50

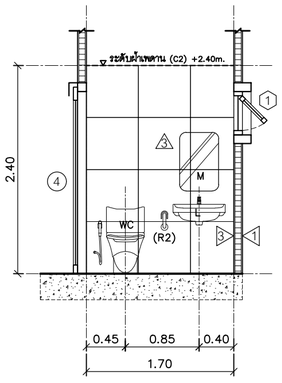


รูปตัด (B) ห้องน้ำ (WC-1)

SCALE 1:50

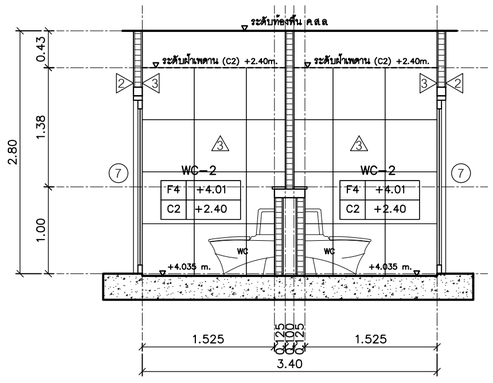


รูปตัด (A) ห้องน้ำ (WC-2)

SCALE 1:50

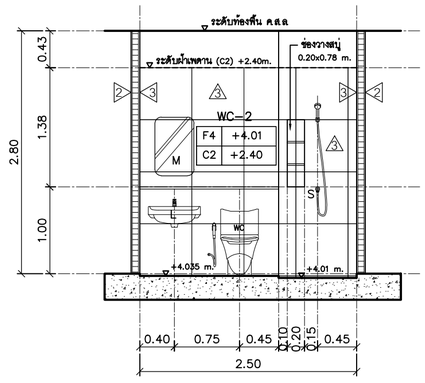


รูปตัด (B) ห้องน้ำ (WC-2)

SCALE 1:50

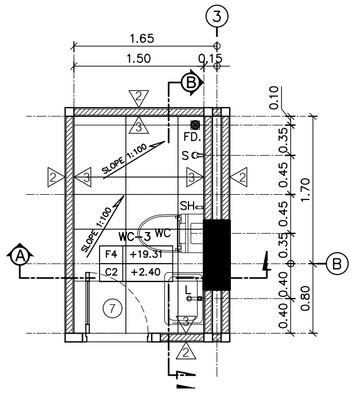


แปลนห้องน้ำ (WC-3)

SCALE 1:50

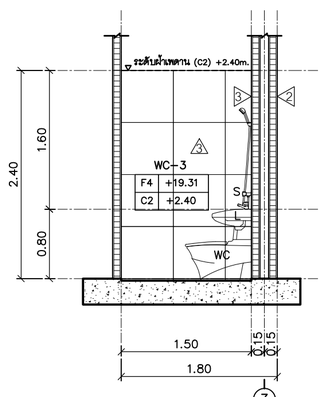

รูปตัด (A) ห้องน้ำ (WC-3)

SCALE 1:50

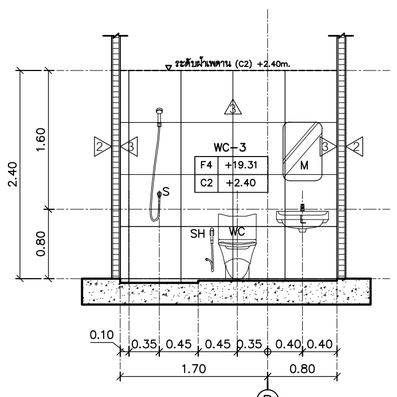

รูปตัด (B) ห้องน้ำ (WC-3)

SCALE 1:50

PROJECT NUMBER : VC2023-024

PROJECT

MACHI RESIDENCES

อาคารพักอาศัยรวม ค.ส.ล 7 ชั้น

OWNER

บริษัท ฤทธิกร ลิฟวิ่ง จำกัด

ARCHITECT :

อัคคะภัทร์ จิระอารีย์บุตร ส-สถ.3040

403 ซ.พัฒนาการ 50 พัฒนาการ

กรุงเทพมหานคร 10250

INTERIOR DESIGNER :

–

STRUCTURAL ENGINEER :

นายพงษ์ธวิทย์ คฑาวุธเจริญกุล สย.12291

ELECTRICAL ENGINEER :

นายภาคภูมิ คำพิทูรย์ สพก.5587

MECHANICAL ENGINEER :

SANITARY ENGINEER :

นส.อรวรรณ พลตรี สส.134

DRAWING TITLE

แบบขยาย (WC-01,02,03)

DRAWING FOR CONSTRUCTION

DRAW BY :	CHECKER :	REVISION :
Weerayuth L.	Akapatr C.	–


SCALE :	DRAWING NO.
1 : 100	A-D03
DATE : 04-12-2024	
FILE NAME :	JOB NO.

REVISION	DESCRIPTION


GERNERAL NOTE
DO NOT SCALE DRAWING ALL MEASUREMENT MUST BE CHECKED AT THE SIDE BY THE CONTRACTOR
ALL DESIGN AND DRAWINGS ARE THE PROPERTY OF MARCHTEN CO.,LTD AND NOT BE USED WITH OUT THEIR WRITTEN PERMISSION

MARCHTEN
ARCHITECTURE / INTERIOR


บริษัท มาร์ชเทน จำกัด
403 ซ.พัฒนาการ 50 สวนหลวง กรุงเทพมหานคร 10250

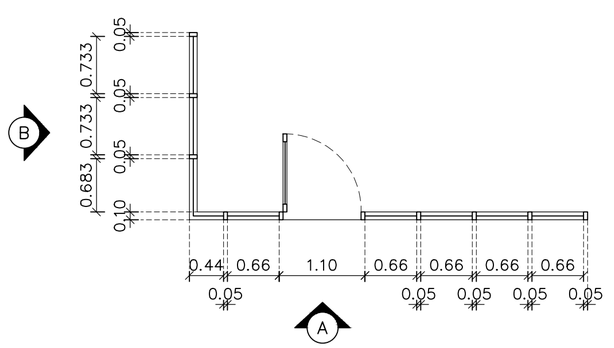

1

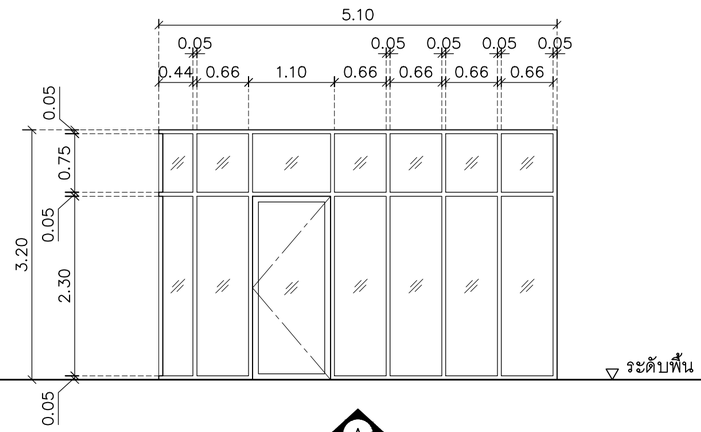


A

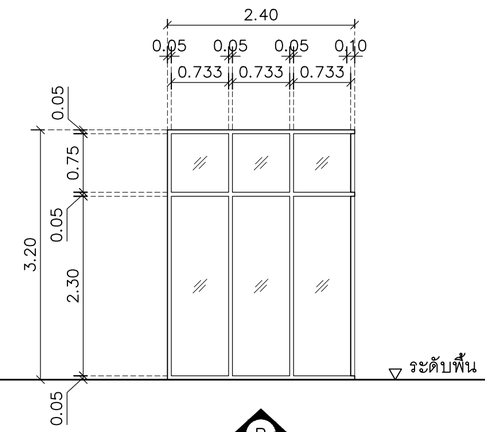


B

ลักษณะ	ประตูบานเปิดเดี่ยว		
ตำแหน่ง	ทางเข้าโถงชั้น (1)		
วงกบ	ALUMINIUM สีดำ หนา 1.5 mm.		
กรอบบาน	ALUMINIUM สีดำ หนา 1.5 mm.		
ลูกฟัก	กระจกใส หนา 6 มม		
ช่องแสง	–		
อุปกรณ์	HAFELE		

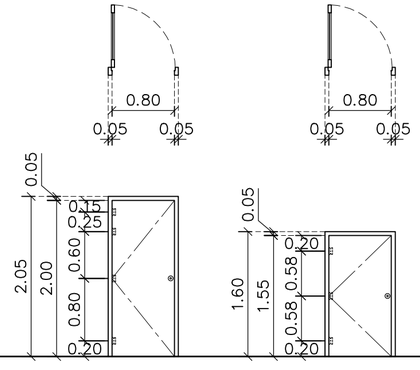


2 3

ลักษณะ	ประตูบานเปิดเดี่ยว
ตำแหน่ง	ประตูห้องไฟฟ้าชั้น (1)/ห้องเก็บของชั้น (1)
วงกบ	ไม้เนื้อแข็ง ขนาด 2”x4”
กรอบบาน	UPVC.
ลูกฟัก	–
ช่องแสง	–
อุปกรณ์	HAFELE ติดตั้งตามมาตรฐานผู้ผลิต

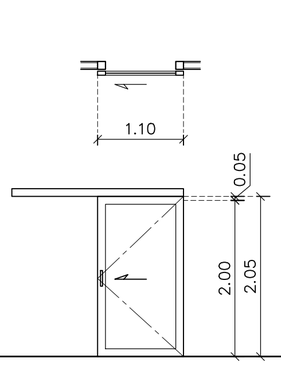


4

ลักษณะ	ประตูบานเลื่อนเดี่ยว
ตำแหน่ง	ประตูเข้าห้องน้ำผู้พิการ
วงกบ	–
กรอบบาน	ไม้เนื้อแข็ง
ลูกฟัก	–
ช่องแสง	–
อุปกรณ์	HAFELE ติดตั้งตามมาตรฐานผู้ผลิต

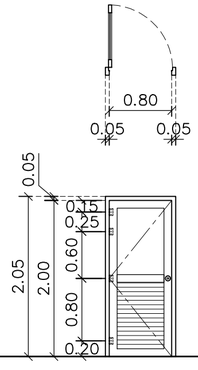


5

ลักษณะ	ประตูบานเปิดเดี่ยว
ตำแหน่ง	ประตูเข้าห้องไฟฟ้า
วงกบ	ไม้เนื้อแข็ง ขนาด 2”x4”
กรอบบาน	ไม้เนื้อแข็ง
ลูกฟัก	เกร็ดไม้เนื้อแข็ง
ช่องแสง	–
อุปกรณ์	HAFELE ติดตั้งตามมาตรฐานผู้ผลิต

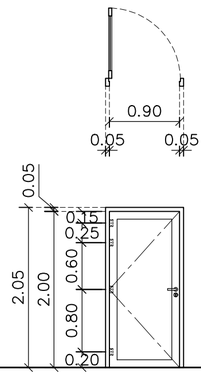

6

ลักษณะ	ประตูบานเปิดเดี่ยว
ตำแหน่ง	ประตูเข้าห้องพัก
วงกบ	UPVC ขนาด 2”x4”
กรอบบาน	UPVC
ลูกฟัก	–
ช่องแสง	–
อุปกรณ์	HAFELE ติดตั้งตามมาตรฐานผู้ผลิต

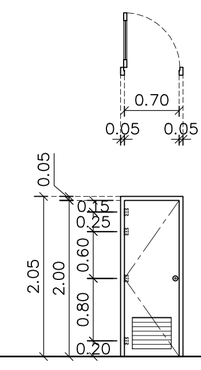

7

ลักษณะ	ประตูบานเปิดเดี่ยว
ตำแหน่ง	ห้องน้ำภายในห้องพัก
วงกบ	UPVC ขนาด 2”x4”
กรอบบาน	UPVC
ลูกฟัก	–
ช่องแสง	–
อุปกรณ์	HAFELE ติดตั้งตามมาตรฐานผู้ผลิต

PROJECT NUMBER : VC2023-024

PROJECT

MACHI RESIDENCES

อาคารพักอาศัยรวม ค.ส.ล 7 ชั้น

OWNER

บริษัท ฤทธิกร ลิฟวิ่ง จำกัด

ARCHITECT :

อัคคะภัทร์ จิระอารีย์บุตร ส-สถ.3040

403 ซ.พัฒนาการ 50 พัฒนาการ

กรุงเทพมหานคร 10250

INTERIOR DESIGNER :

–

STRUCTURAL ENGINEER :

นายพงษ์ธวิทย์ คทาวุธเจริญกุล สย.12291

ELECTRICAL ENGINEER :

นายภาคภูมิ คำพิทูรย์ สฟก.5587

MECHANICAL ENGINEER :

SANITARY ENGINEER :

นส.อรวรรณ พลตรี สส.134

DRAWING TITLE

แบบขยายประตู (1)

DRAWING FOR CONSTRUCTION

DRAW BY :	CHECKER :	REVISION :
Weerayuth L.	Akapatr C.	–

SCALE : 1 : 100	DRAWING NO. A-D04
DATE : 04-12-2024	
FILE NAME :	JOB NO.

REVISION	DESCRIPTION

GERNERAL NOTE

DO NOT SCALE DRAWING ALL MEASUREMENT MUST BE CHECKED AT THE SIDE BY THE CONTRACTOR


ALL DESIGN AND DRAWINGS ARE THE PROPERTY OF MARCHTEN CO.,LTD AND NOT BE USED WITH OUT THEIR WRITTEN PERMISSION

MARCHTEN

ARCHITECTURE / INTERIOR


บริษัท มาร์ชเทน จำกัด

403 ซ.พัฒนาการ 50 สวนหลวง กรุงเทพมหานคร 10250

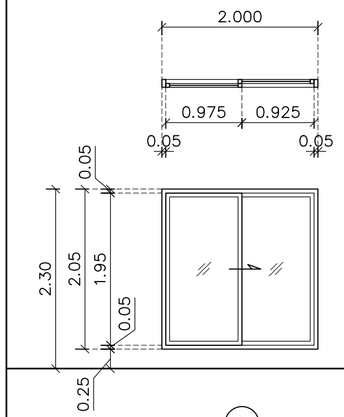


8

ลักษณะ	ประตูบานเลื่อน
ตำแหน่ง	ระเบียงห้องพัก
วงกบ	ALUMINIUM สีดำ หนา 1.5 mm.
กรอบบาน	ALUMINIUM สีดำ หนา 1.2 mm.
ลูกฟัก	–
ช่องแสง	กระจกใส หนา 6 มม
อุปกรณ์	HAFELE ติดตั้งตามมาตรฐานผู้ผลิต

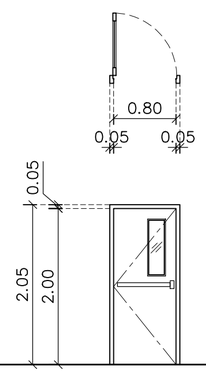


9

ลักษณะ	ประตูหนีไฟ บานเลื่อนเดี่ยว
ตำแหน่ง	บันไดหนีไฟ
วงกบ	เหล็ก
กรอบบาน	เหล็ก
ลูกฟัก	–
ช่องแสง	กระจกนิรภัย
อุปกรณ์	ติดตั้งตามมาตรฐานผู้ผลิต
ทนไฟความร้อน 1,000 องศา ไม่น้อยกว่า 3 ชั่วโมง	

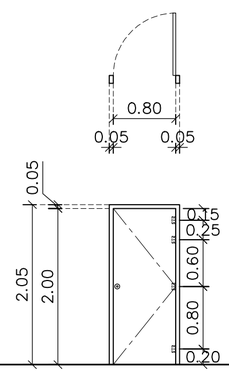


10

ลักษณะ	ประตูบานเปิดเดี่ยว
ตำแหน่ง	ห้องเก็บของ
วงกบ	ไม้เนื้อแข็ง ขนาด 2"x4"
กรอบบาน	ไม้อัด
ลูกฟัก	–
ช่องแสง	–
อุปกรณ์	HAFELE ติดตั้งตามมาตรฐานผู้ผลิต

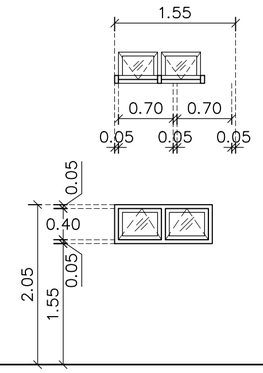


1

ลักษณะ	หน้าต่างบานกระทุ้ง
ตำแหน่ง	ห้องน้ำผู้พิการ
วงกบ	ALUMINIUM สีดำ หนา 1.5 mm.
กรอบบาน	ALUMINIUM สีดำ หนา 1.2 mm.
ลูกฟัก	–
ช่องแสง	กระจกผิวพ่นทรายหนา 6 มม
อุปกรณ์	HAFELE ติดตั้งตามมาตรฐานผู้ผลิต

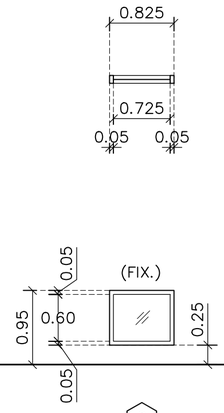


2

ลักษณะ	บานช่องแสงกระจกติดตาย
ตำแหน่ง	ชานพักบันไดหลัก
วงกบ	ALUMINIUM สีดำ หนา 1.5 mm.
กรอบบาน	ALUMINIUM สีดำ หนา 1.2 mm.
ลูกฟัก	–
ช่องแสง	กระจกใส หนา 6 มม
อุปกรณ์	HAFELE ติดตั้งตามมาตรฐานผู้ผลิต

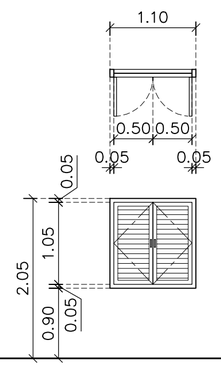


3

ลักษณะ	หน้าต่างบานเปิดคู่
ตำแหน่ง	ห้องไฟฟ้า
วงกบ	ALUMINIUM สีดำ หนา 1.5 mm.
กรอบบาน	ALUMINIUM สีดำ หนา 1.5 mm.
ลูกฟัก	เกร็ดระบายอากศ 2" สีดำ
ช่องแสง	–
อุปกรณ์	HAFELE ติดตั้งตามมาตรฐานผู้ผลิต

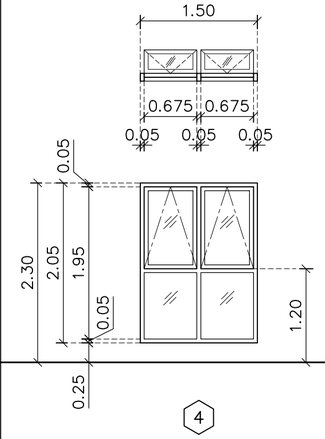


4

ลักษณะ	หน้าต่างบานกระทุ้ง + ช่องแสงกระจกติดตาย
ตำแหน่ง	โถงทางเดิน
วงกบ	ALUMINIUM สีดำ หนา 1.5 mm.
กรอบบาน	ALUMINIUM สีดำ หนา 1.5 mm.
ลูกฟัก	กระจกใส หนา 6 มม
ช่องแสง	–
อุปกรณ์	ติดตั้งตามมาตรฐานผู้ผลิต

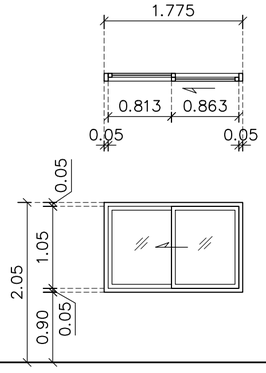


5

ลักษณะ	หน้าต่างบานเลื่อนสลับ
ตำแหน่ง	ห้องเก็บของ
วงกบ	ALUMINIUM สีดำ หนา 1.5 mm.
กรอบบาน	ALUMINIUM สีดำ หนา 1.5 mm.
ลูกฟัก	กระจกใส หนา 6 มม
ช่องแสง	–
อุปกรณ์	ติดตั้งตามมาตรฐานผู้ผลิต

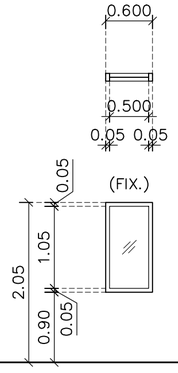

7

ลักษณะ	บานช่องแสงกระจกติดตาย
ตำแหน่ง	ห้องเตรียมอาหาร
วงกบ	ALUMINIUM สีดำ หนา 1.5 mm.
กรอบบาน	ALUMINIUM สีดำ หนา 1.5 mm.
ลูกฟัก	กระจกใส หนา 6 มม
ช่องแสง	–
อุปกรณ์	ติดตั้งตามมาตรฐานผู้ผลิต

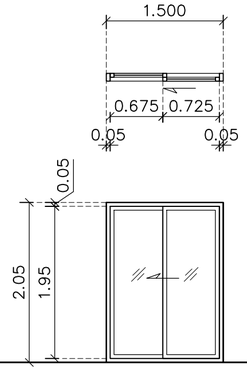

8

ลักษณะ	หน้าต่างบานเลื่อนสลับ
ตำแหน่ง	ระเบียงห้องพัก
วงกบ	ALUMINIUM สีดำ หนา 1.5 mm.
กรอบบาน	ALUMINIUM สีดำ หนา 1.5 mm.
ลูกฟัก	กระจกใส หนา 6 มม
ช่องแสง	–
อุปกรณ์	ติดตั้งตามมาตรฐานผู้ผลิต

PROJECT NUMBER : VC2023-024

PROJECT

MACHI RESIDENCES

อาคารพักอาศัยรวม ค.ส.ล 7 ชั้น

OWNER

บริษัท ฤทธิกร ลิฟวิ่ง จำกัด

ARCHITECT :

อัคคะภัทร์ จิระอารีย์บุตร ส-สถ.3040
403 ซ.พัฒนาการ 50 พัฒนาการ
กรุงเทพมหานคร 10250

INTERIOR DESIGNER :

–

STRUCTURAL ENGINEER :

นายพงษ์ธวิทย์ คฑาวุธเจริญกุล สย.12291

ELECTRICAL ENGINEER :

นายภาคภูมิ คำพิทูรย์ สพก.5587

MECHANICAL ENGINEER :

SANITARY ENGINEER :

นส.อรวรรณ พลตรี สส.134

DRAWING TITLE

แบบขยายประตู (2)

DRAWING FOR CONSTRUCTION

DRAW BY :	CHECKER :	REVISION :
Weerayuth L.	Akapatr C.	–

SCALE : 1 : 100

DRAWING NO. A-D05

DATE : 04-12-2024

FILE NAME :


JOB NO.

REVISION	DESCRIPTION

GERNERAL NOTE
DO NOT SCALE DRAWING ALL MEASUREMENT MUST BE CHECKED AT THE SIDE BY THE CONTRACTOR
ALL DESIGN AND DRAWINGS ARE THE PROPERTY OF MARCHTEN CO.,LTD
AND NOT BE USED WITH OUT THEIR WRITTEN PERMISSION


MARCHTEN
ARCHITECTURE / INTERIOR

บริษัท มาร์ชเทน จำกัด
403 ซ.พัฒนาการ 50 สวนหลวง กรุงเทพมหานคร 10250

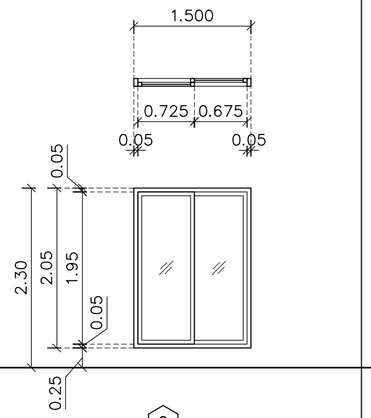


9

ลักษณะ	ประตูบานเลื่อน
ตำแหน่ง	ระเบียงห้องพัก
วงกบ	ALUMINIUM สีดำ หนา 1.5 mm.
กรอบบาน	ALUMINIUM สีดำ หนา 1.2 mm.
ลูกฟัก	–
ช่องแสง	กระจกใส หนา 6 มม
อุปกรณ์	HAFELE ติดตั้งตามมาตรฐานผู้ผลิต

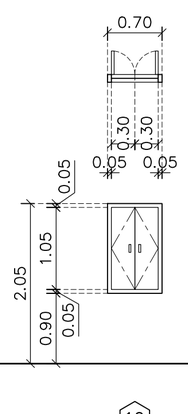


10

ลักษณะ	หน้าต่างบานเปิดคู่
ตำแหน่ง	โถงทางเดิน
วงกบ	UPVC
กรอบบาน	บานไม้อัด
ลูกฟัก	–
ช่องแสง	กระจกนิรภัย
อุปกรณ์	ติดตั้งตามมาตรฐานผู้ผลิต

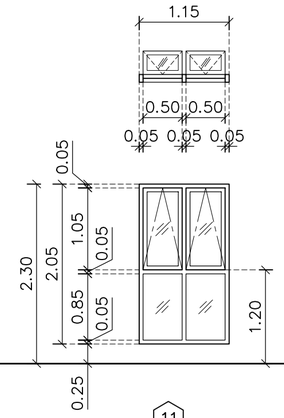

11


ลักษณะ	หน้าต่างบานกระทุ้ง + ช่องแสงกระจกติดตาย
ตำแหน่ง	โถงบันไดหลัก
วงกบ	ALUMINIUM สีดำ หนา 1.5 mm.
กรอบบาน	ALUMINIUM สีดำ หนา 1.2 mm.
ลูกฟัก	–
ช่องแสง	–
อุปกรณ์	HAFELE ติดตั้งตามมาตรฐานผู้ผลิต

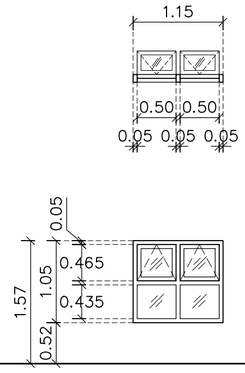

12


ลักษณะ	หน้าต่างบานกระทุ้ง
ตำแหน่ง	ห้องใต้หลังคา
วงกบ	ALUMINIUM สีดำ หนา 1.5 mm.
กรอบบาน	ALUMINIUM สีดำ หนา 1.2 mm.
ลูกฟัก	–
ช่องแสง	กระจกผิวพ่นทรายหนา 6 มม
อุปกรณ์	HAFELE ติดตั้งตามมาตรฐานผู้ผลิต

ลักษณะ	–
ตำแหน่ง	–
วงกบ	–
กรอบบาน	–
ลูกฟัก	–
ช่องแสง	–
อุปกรณ์	–

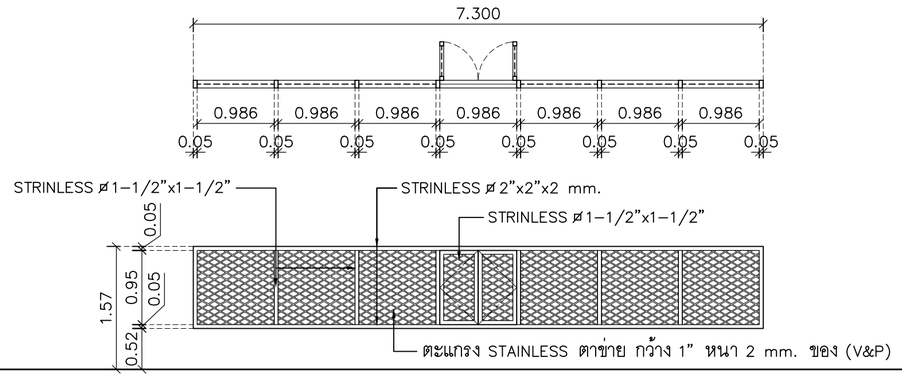

6

ลักษณะ	หน้าต่างบานเปิดคู่ + บานช่องตะข่ายระบายอากาศ
ตำแหน่ง	ชั้นใต้หลังคา
วงกบ	STRINLESS 1"x2"
กรอบบาน	STRINLESS 1"x2"
ลูกฟัก	–
ช่องแสง	ตะแกรง STAINLESS
อุปกรณ์	HAFELE ติดตั้งตามมาตรฐานผู้ผลิต

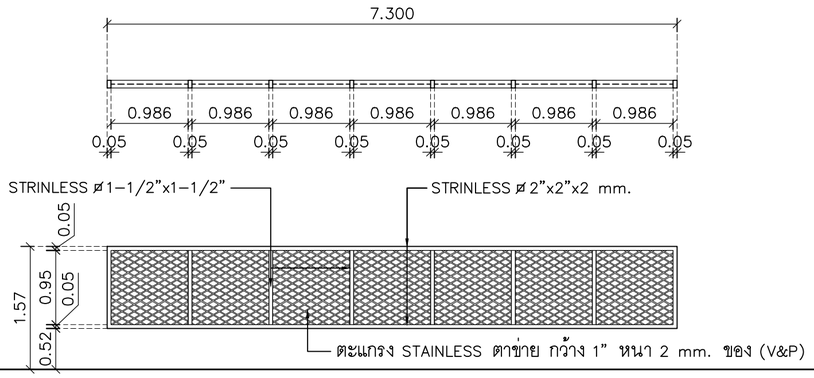

6A

ลักษณะ	บานช่องตะข่ายระบายอากาศ
ตำแหน่ง	ชั้นใต้หลังคา
วงกบ	STRINLESS 1"x2"
กรอบบาน	STRINLESS 1"x2"
ลูกฟัก	–
ช่องแสง	ตะแกรง STAINLESS
อุปกรณ์	–

PROJECT NUMBER : VC2023-024

PROJECT

MACHI RESIDENCES

อาคารพักอาศัยรวม ค.ส.ล 7 ชั้น

OWNER

บริษัท ฤทธิกร ลิฟวิ่ง จำกัด

ARCHITECT :

อัคคะภัทร์ จิระอารีย์บุตร ส-สถ.3040

403 ซ.พัฒนาการ 50 พัฒนาการ

กรุงเทพมหานคร 10250

INTERIOR DESIGNER :

–

STRUCTURAL ENGINEER :

นายพงษ์ธวิทย์ คฑาวุธเจริญกุล สย.12291

ELECTRICAL ENGINEER :

นายภาคภูมิ คำพิทูรย์ สพก.5587

MECHANICAL ENGINEER :

SANITARY ENGINEER :

นส.อรวรรณ พลตรี สส.134

DRAWING TITLE

แบบขยายหน้าต่าง

DRAWING FOR CONSTRUCTION

DRAW BY :	CHECKER :	REVISION :
Weerayuth L.	Akapatr C.	–

SCALE : 1 : 100

DRAWING NO. A-D06

DATE : 04–12–2024

FILE NAME :


JOB NO.


REVISION	DESCRIPTION


GERNERAL NOTE
DO NOT SCALE DRAWING ALL MEASUREMENT MUST BE CHECKED AT THE SIDE BY THE CONTRACTOR
ALL DESIGN AND DRAWINGS ARE THE PROPERTY OF MARCHTEN CO.,LTD AND NOT BE USED WITH OUT THEIR WRITTEN PERMISSION

MARCHTEN
ARCHITECTURE / INTERIOR

บริษัท มาร์ชเทน จำกัด
403 ซ.พัฒนาการ 50 สวนหลวง กรุงเทพมหานคร 10250

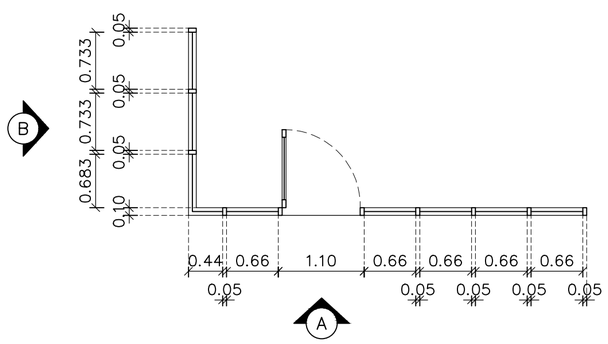


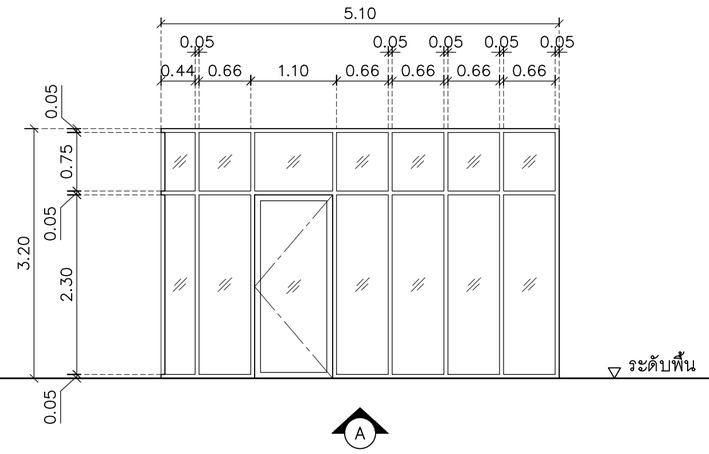

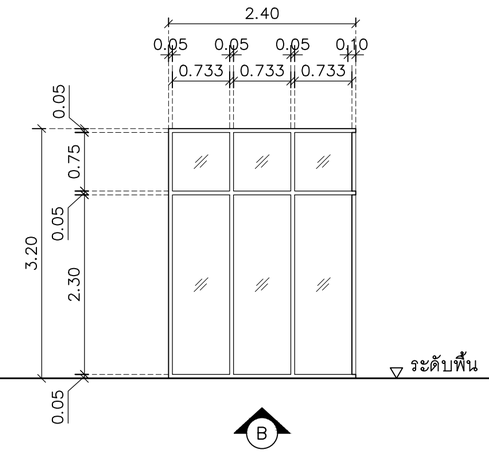

แบบแสดงอุปกรณ์ (1)

อุปกรณ์	อุปกรณ์ HAFELE
1)	มือจับ สีดำ 903.92.559 PC HDL SET ST.ST.GRA. BLA
2)	อุปกรณ์ล๊อค สีดำ 911.25.100 MORT.LOCK PC R55/24 BLACK
3)	ชุดกุญแจล๊อค สีดำ 916.80.776 SA MK KW1 DOUB PC W/THUM BLM 35/35
4)	DOOR CLOSER สีดำ 931.84.070 DCL 51 BLACK MATT W HOLD OPEN W/O COVER

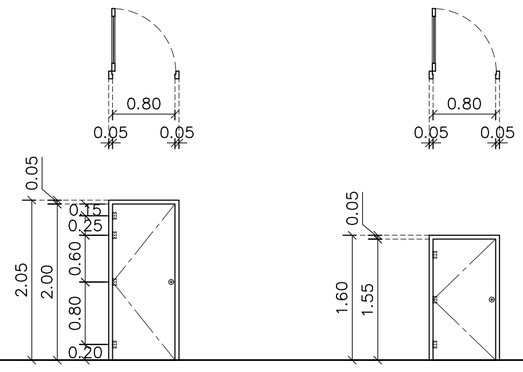


แบบแสดงอุปกรณ์ (2)


อุปกรณ์	อุปกรณ์ HAFELE
1)	มือจับ สีดำ 903.92.559 PC HDL SET ST.ST.GRA. BLA
2)	อุปกรณ์ล๊อค สีดำ 911.25.100 MORT.LOCK PC R55/24 BLACK
3)	ชุดกุญแจล๊อค สีดำ 916.80.776 SA MK KW1 DOUB PC W/THUM BLM 35/35
4)	DOOR STOPPER สีดำ 937.55.143 DOOR STOPPER STST.BLACK

แบบแสดงอุปกรณ์ (3)

อุปกรณ์	อุปกรณ์ HAFELE
1)	940.83.005 D-LI11 80-P FITT.W/O S.CL
2)	ราง 940.43.932 R. TRACK ALU CLEAR ANO 3000MM
3)	มือจับ 903.07.910 PULL HANDLE ST.ST.MATT32X300MM
4)	LOCK 911.26.590 SLID.MORTISE LOCK WC STST55/20
5)	ชุดล๊อค 902.53.204 WC ROUND STST.MATT 35-45MM

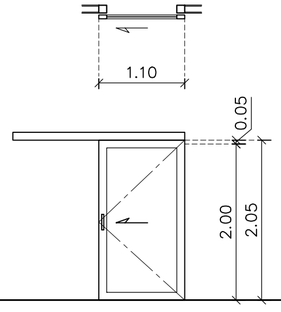

แบบแสดงอุปกรณ์ (4)

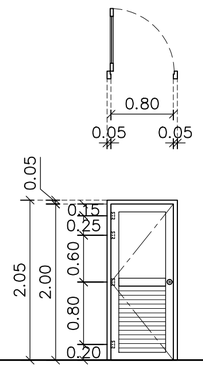

(5)

อุปกรณ์	อุปกรณ์ HAFELE
1)	มือจับ 903.92.556 PC HANDLE SET 8 ST.ST.MATT
2)	อุปกรณ์ล๊อค 911.02.153 MORT.LOCK PC ST.ST.LH/RH 24MM
3)	ชุดกุญแจล๊อค 916.80.762 SA MK KW1 PC SNP 30/30 W/R THM
4)	บานพับ 926.98.040 BUTT HING.STST.SATIN102X76X3MM

PROJECT NUMBER : VC2023-024

PROJECT

MACHI RESIDENCES

อาคารพักอาศัยรวม ค.ส.ล 7 ชั้น

OWNER

บริษัท ฤทธิกร ลิฟวิ่ง จำกัด

ARCHITECT :

อัคคะภัทร์ จิระอารีย์บุตร ส-สถ.3040

403 ซ.พัฒนาการ 50 พัฒนาการ

กรุงเทพมหานคร 10250

INTERIOR DESIGNER :

-

STRUCTURAL ENGINEER :

นายพงษ์ธวิทย์ คฑาวุธเจริญกุล สย.12291

ELECTRICAL ENGINEER :

นายภาคภูมิ คำพิทูรย์ สพก.5587

MECHANICAL ENGINEER :

SANITARY ENGINEER :

นส.อรวรรณ พลตรี สส.134

DRAWING TITLE

แบบแสดงอุปกรณ์ (1)

DRAWING FOR CONSTRUCTION

DRAW BY :	CHECKER :	REVISION :
Weerayuth L.	Akapatr C.	-

SCALE : 1 : 100

DATE : 04-12-2024

DRAWING NO. A-D07

FILE NAME :


JOB NO.

REVISION	DESCRIPTION

GERNERAL NOTE
DO NOT SCALE DRAWING ALL MEASUREMENT MUST BE CHECKED AT THE SIDE BY THE CONTRACTOR
ALL DESIGN AND DRAWINGS ARE THE PROPERTY OF MARCHTEN CO.,LTD AND NOT BE USED WITH OUT THEIR WRITTEN PERMISSION


MARCHTEN
ARCHITECTURE / INTERIOR

บริษัท มาร์ชเทน จำกัด
403 ซ.พัฒนาการ 50 สวนหลวง กรุงเทพมหานคร 10250

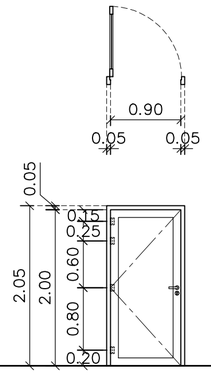


แบบแสดงอุปกรณ์ (6)

อุปกรณ์	อุปกรณ์ HAFELE
1)	มือจับ 903.92.556 PC HANDLE SET 8 ST.ST.MATT
2)	อุปกรณ์ล็อค 911.02.153 MORT.LOCK PC ST.ST.LH/RH 24MM
3)	ชุดกุญแจล็อค 916.80.762 SA MK KW1 PC SNP 30/30 W/R THM
4)	บานพับ 926.98.040 BUTT HING.STST.SATIN102X76X3MM
5)	DOOR STOPPER ST.ST. SATIN 937.55.140
6)	DR.VIEW W/CAP 180 DEG BR.NI.S 959.00.134

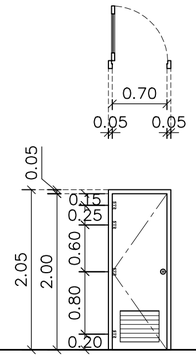


แบบแสดงอุปกรณ์ (7)

อุปกรณ์	อุปกรณ์ HAFELE
1)	มือจับ 903.92.556 PC HANDLE SET 8 ST.ST.MATT
2)	อุปกรณ์ล็อค 911.02.153 MORT.LOCK PC ST.ST.LH/RH 24MM
3)	ชุดกุญแจล็อค 916.95.406 DBL.PC.W/WC FUNC.60MM NI.PL.MA
4)	บานพับ 926.98.040 BUTT HING.STST.SATIN102X76X3MM
5)	WALL DOOR BUFFER STST.MAT.90MM 937.12.800

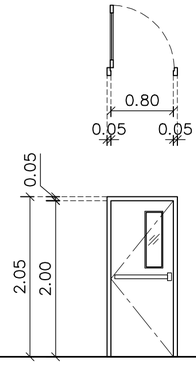


แบบแสดงอุปกรณ์ (9)

อุปกรณ์	อุปกรณ์ HAFELE
1)	มือจับ 911.30.162 SA MK KW1 PANIC LEV.SNP
2)	ชุดผลักเปิด PANIC EXIT DEVICE ST.ST. 911.56.036
3)	DOOR CLOSER TS2000 NVBC F SILV. 931.16.699

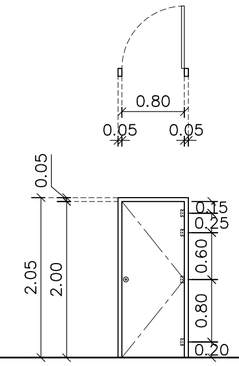

แบบแสดงอุปกรณ์ (10)

อุปกรณ์	อุปกรณ์ HAFELE
1)	มือจับ 903.92.556 PC HANDLE SET 8 ST.ST.MATT
2)	อุปกรณ์ล็อค 911.02.153 MORT.LOCK PC ST.ST.LH/RH 24MM
3)	ชุดกุญแจล็อค 916.80.762 SA MK KW1 PC SNP 30/30 W/R THM
4)	บานพับ 926.98.040 BUTT HING.STST.SATIN102X76X3MM
5)	DOOR STOPPER ST.ST. SATIN 937.55.140

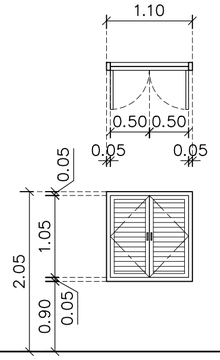

แบบแสดงอุปกรณ์ (3)

อุปกรณ์	อุปกรณ์ HAFELE
1)	มือจับ 152.52.051 FLUSH HANDLE ST.ST.MATT 140/45MM
2)	อุปกรณ์ล็อค 911.62.357 ENGINEERING BOLT SET STST.MATT

PROJECT NUMBER : VC2023-024

PROJECT

MACHI RESIDENCES

อาคารพักอาศัยรวม ค.ส.ล 7 ชั้น

OWNER

บริษัท ฤทธิกร ลิฟวิ่ง จำกัด

ARCHITECT :

อัคคะภัทร์ จิระอารีย์บุตร ส-สถ.3040

403 ซ.พัฒนาการ 50 พัฒนาการ

กรุงเทพมหานคร 10250

INTERIOR DESIGNER :

–

STRUCTURAL ENGINEER :

นายพงษ์ธวิทย์ คฑาวุธเจริญกุล สย.12291

ELECTRICAL ENGINEER :

นายภาคภูมิ คำพิทูรย์ สฟก.5587

MECHANICAL ENGINEER :

SANITARY ENGINEER :

นส.อรวรรณ พลตรี สส.134

DRAWING TITLE

แบบแสดงอุปกรณ์ (2)

DRAWING FOR CONSTRUCTION

DRAW BY :	CHECKER :	REVISION :
Weerayuth L.	Akapatr C.	–

SCALE : 1 : 100

DATE : 04-12-2024

DRAWING NO. A-D08

FILE NAME :

JOB NO.

REVISION	DESCRIPTION

GERNERAL NOTE


DO NOT SCALE DRAWING ALL MEASUREMENT MUST BE CHECKED AT THE SIDE BY THE CONTRACTOR

ALL DESIGN AND DRAWINGS ARE THE PROPERTY OF MARCHTEN CO.,LTD AND NOT BE USED WITH OUT THEIR WRITTEN PERMISSION

MARCHTEN


ARCHITECTURE / INTERIOR

บริษัท มาร์ชเทน จำกัด
403 ซ.พัฒนาการ 50 สวนหลวง กรุงเทพมหานคร 10250

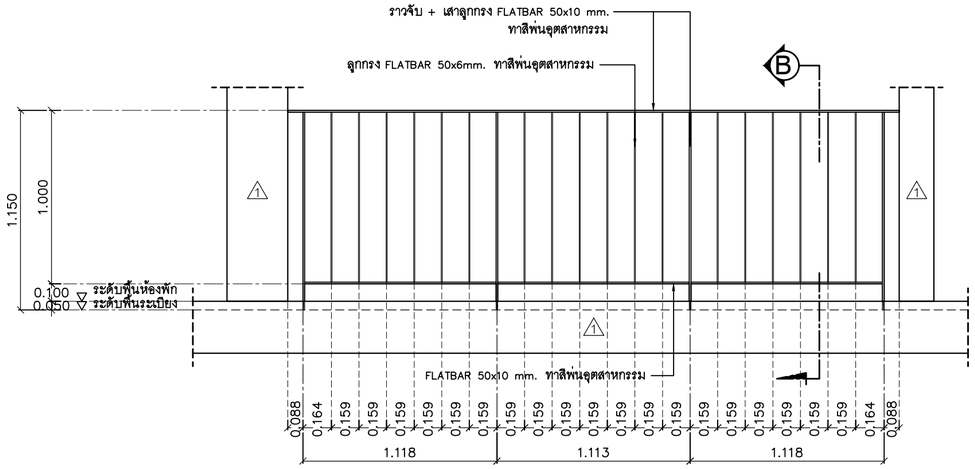


แบบขยายราวกันตกระเบียง

SCALE 1:25

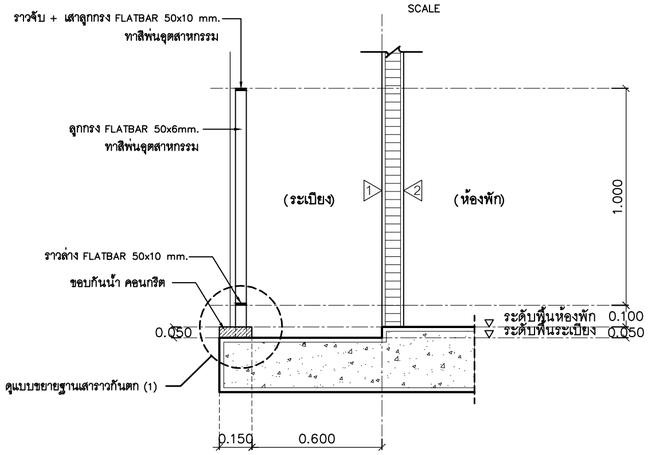


รูปตัด (A) ขยายราวกันตกระเบียง

SCALE 1:20

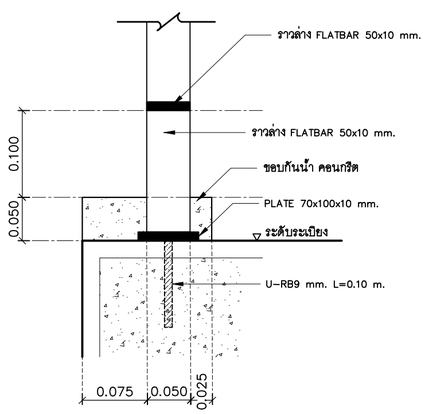


แบบขยายฐานเสาราวกันตก (1)

SCALE 1:5

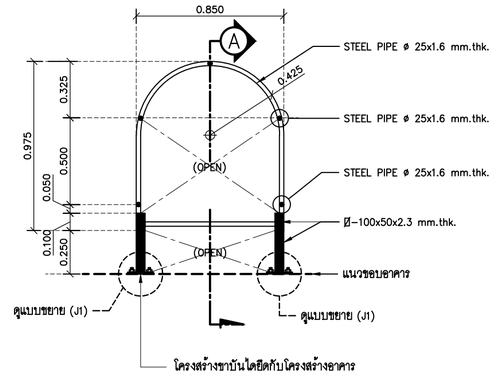


แปลนขยาย บันไดลิง

SCALE 1:25

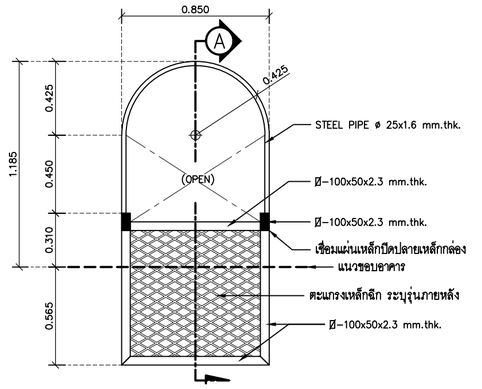

แปลนขยาย บันไดลิง

SCALE 1:25

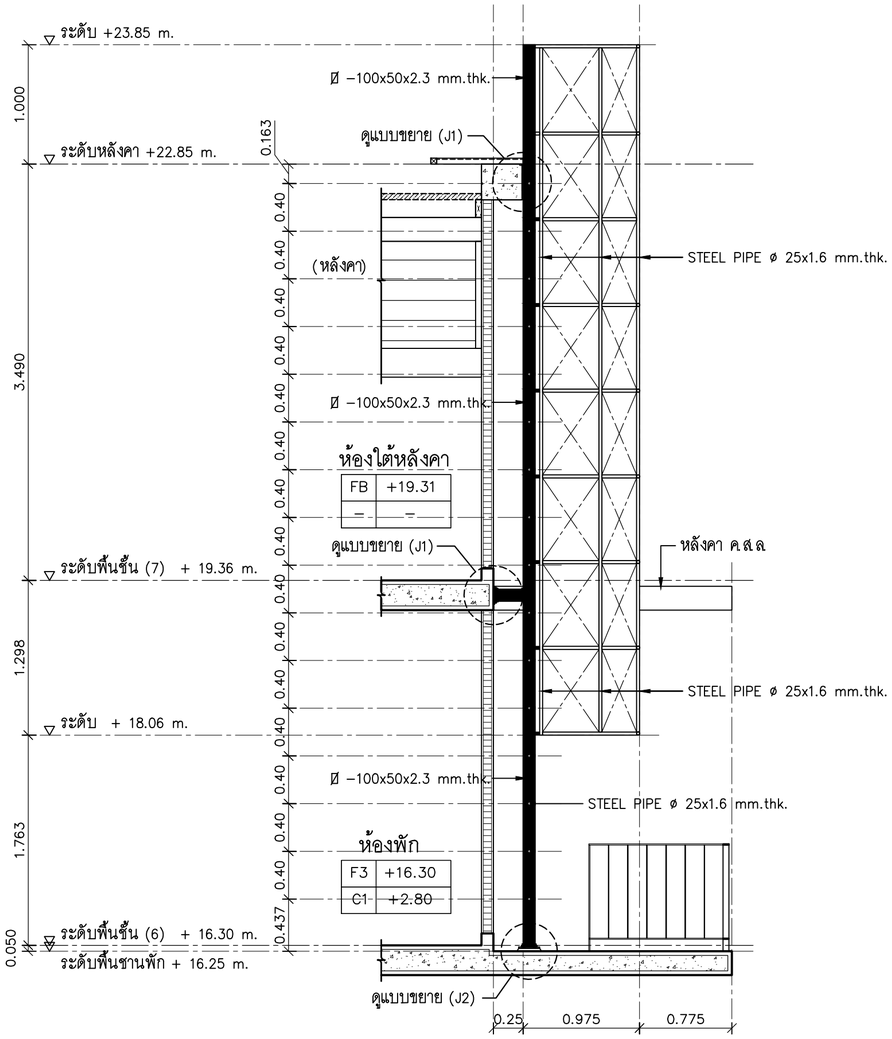

รูปตัด (A) บันไดลิง

SCALE 1:25

PROJECT NUMBER : VC2023-024

PROJECT

MACHI RESIDENCES

อาคารพักอาศัยรวม ค.ส.ล 7 ชั้น

OWNER

บริษัท ฤทธิกร ลิฟวิ่ง จำกัด

ARCHITECT :

อัคคะภัทร์ จิระอารีย์บุตร ส-สถ.3040

403 ซ.พัฒนาการ 50 พัฒนาการ

กรุงเทพมหานคร 10250

INTERIOR DESIGNER :

–

STRUCTURAL ENGINEER :

นายพงษ์ธวิทย์ คฑาวุธเจริญกุล สย.12291

ELECTRICAL ENGINEER :

นายภาคภูมิ คำพิทูรย์ สพก.5587

MECHANICAL ENGINEER :

SANITARY ENGINEER :

นส.อรวรรณ พลตรี สส.134

DRAWING TITLE

แบบขยายราวกันตก

แบบขยายบันไดลิง

DRAWING FOR CONSTRUCTION

DRAW BY :	CHECKER :	REVISION :
Weerayuth L.	Akapatr C.	–

SCALE :	DRAWING NO.
1 : 100	A-D09
DATE : 04-12-2024	
FILE NAME :	JOB NO.

REVISION	DESCRIPTION

GERNERAL NOTE

DO NOT SCALE DRAWING ALL MEASUREMENT MUST BE CHECKED AT THE SIDE BY THE CONTRACTOR


ALL DESIGN AND DRAWINGS ARE THE PROPERTY OF MARCHTEN CO.,LTD AND NOT BE USED WITH OUT THEIR WRITTEN PERMISSION

MARCHTEN

ARCHITECTURE / INTERIOR


บริษัท มาร์ชเทน จำกัด

403 ซ.พัฒนาการ 50 สวนหลวง กรุงเทพมหานคร 10250

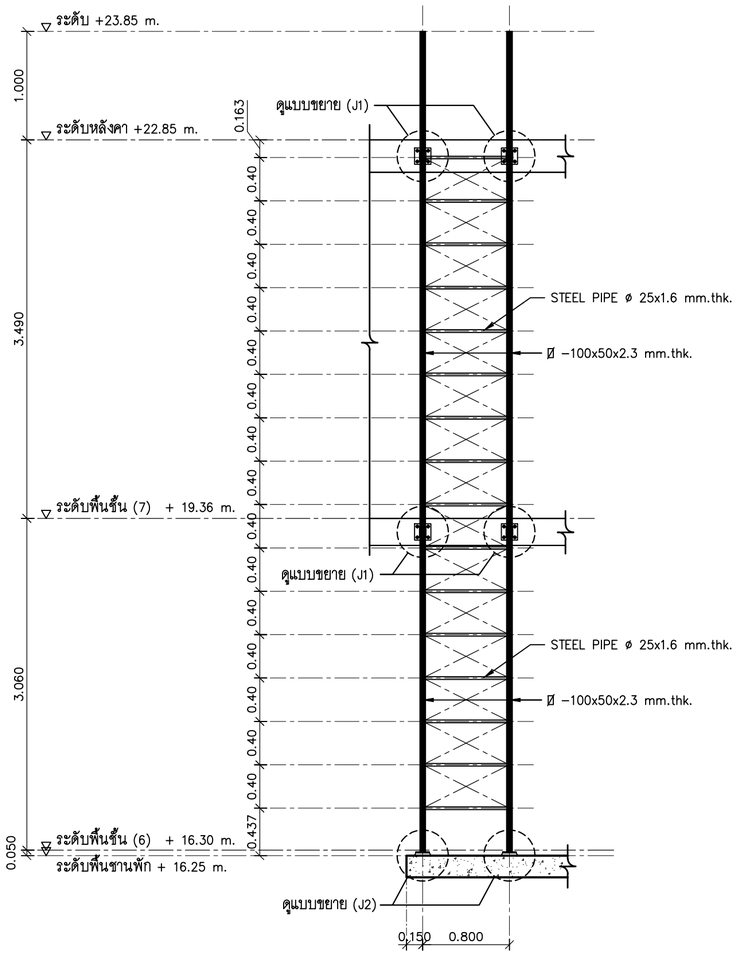


รูปด้าน (1) บันไดลิง

SCALE (ขยายลูกนอนบันได) 1:25

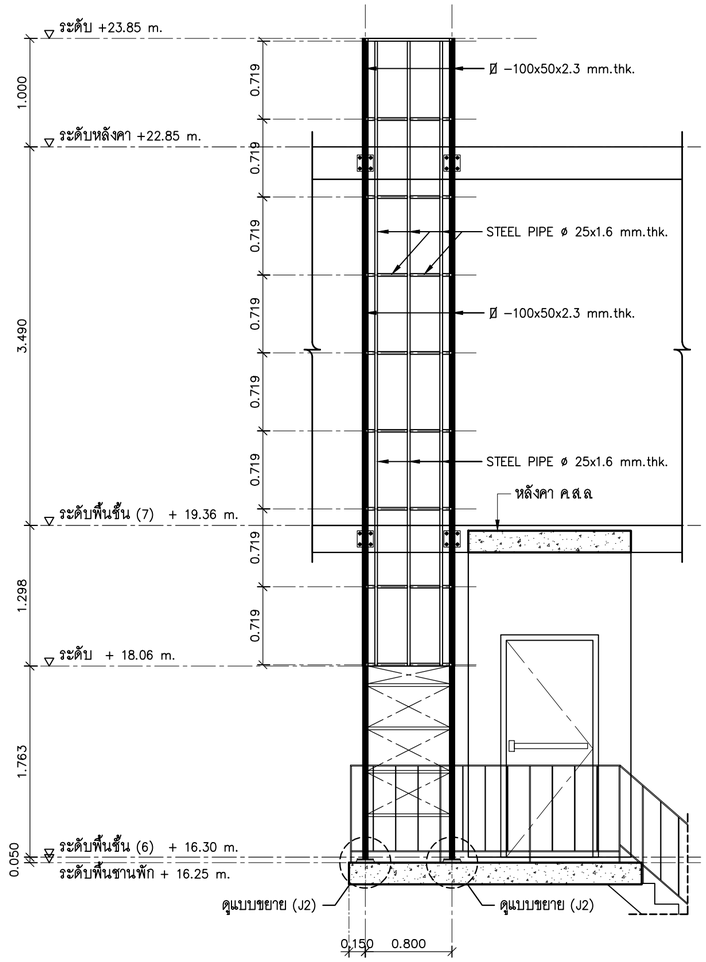


รูปด้าน (2) บันไดลิง

SCALE (ขยายแผงกันตกบันได) 1:25

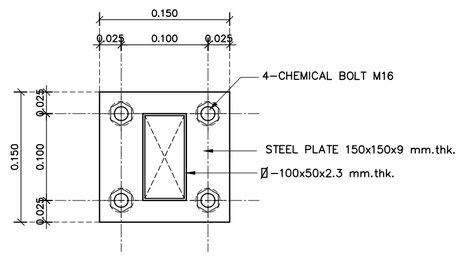

แปลนขยาย (J1),(J2)

SCALE 1:5

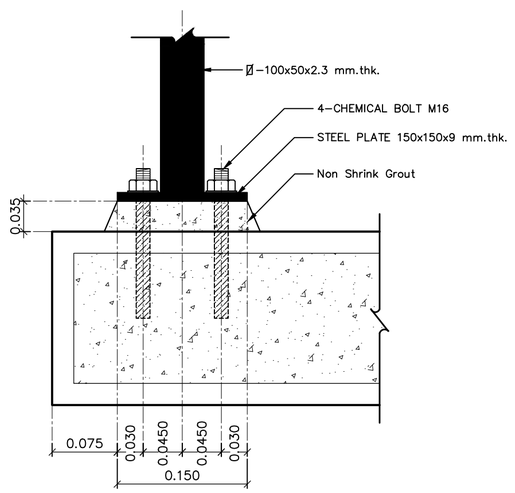

แบบขยายฐานเสาบันได (J2)

SCALE 1:5

PROJECT NUMBER : VC2023-024

PROJECT

MACHI RESIDENCES

อาคารพักอาศัยรวม ค.ส.ล 7 ชั้น

OWNER

บริษัท ฤทธิกร ลิฟวิ่ง จำกัด

ARCHITECT :

อัคคะภัทร์ จิระอารีย์บุตร ส-สถ.3040

403 ซ.พัฒนาการ 50 พัฒนาการ

กรุงเทพมหานคร 10250

INTERIOR DESIGNER :

-

STRUCTURAL ENGINEER :

นายพงษ์อวิทย์ คฑาวุธเจริญกุล สย.12291

ELECTRICAL ENGINEER :

นายภาคภูมิ คำพิทูรย์ สฟก.5587

MECHANICAL ENGINEER :

SANITARY ENGINEER :

นส.อรวรรณ พลตรี สส.134

DRAWING TITLE

แบบขยายบันไดลิง

DRAWING FOR CONSTRUCTION

DRAW BY :	CHECKER :	REVISION :
Weerayuth L.	Akapatr C.	-

SCALE :	DRAWING NO.
1 : 100	A-D10
DATE : 04-12-2024	
FILE NAME :	JOB NO.

REVISION	DESCRIPTION

GERNERAL NOTE

DO NOT SCALE DRAWING ALL MEASUREMENT MUST BE CHECKED AT THE SIDE BY THE CONTRACTOR


ALL DESIGN AND DRAWINGS ARE THE PROPERTY OF MARCHTEN CO.,LTD AND NOT BE USED WITH OUT THEIR WRITTEN PERMISSION

MARCHTEN


ARCHITECTURE / INTERIOR

บริษัท มาร์ชเทน จำกัด


403 ซ.พัฒนาการ 50 สวนหลวง กรุงเทพมหานคร 10250

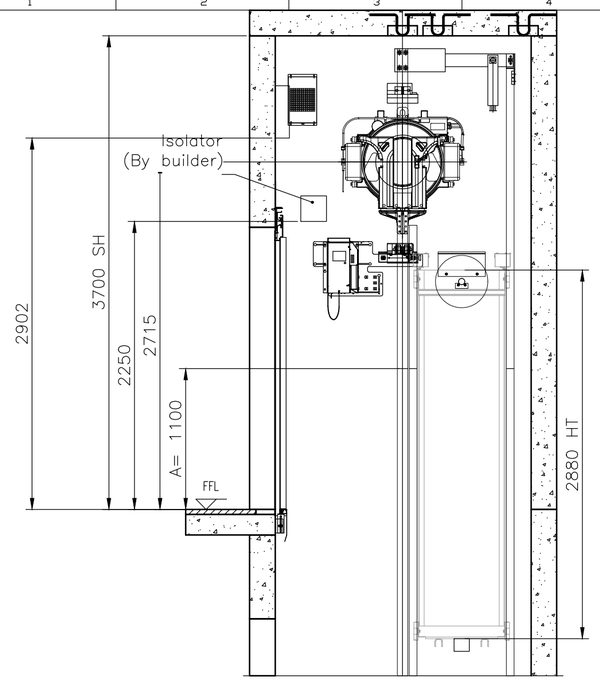


TOP CLEARANCES L1_24_7
SECTION A-A (CAR CAGE AT BOTTOM)
Scale 1:20

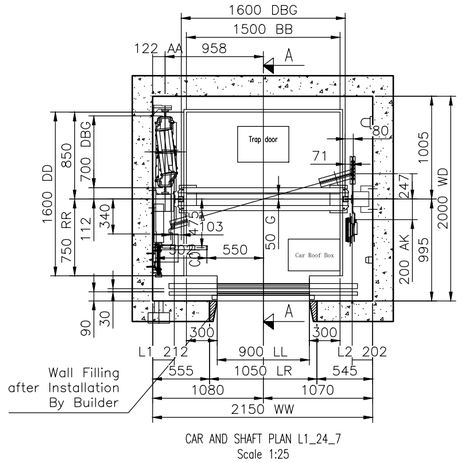


CAR AND SHAFT PLAN L1_24_7
Scale 1:25

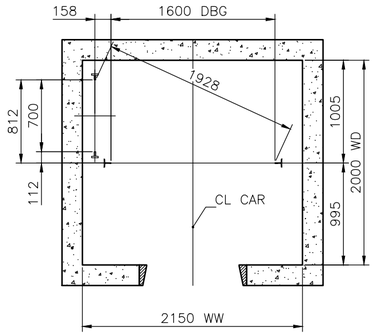


GUIDES L1_24_7
Scale 1:25

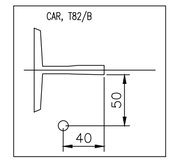


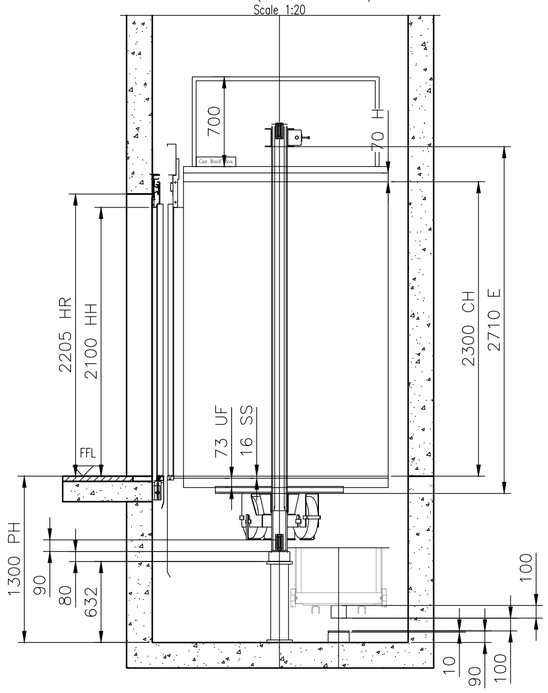


PIT CLEARANCES L1_24_7
SECTION A-A (CAR CAGE AT BOTTOM)
Scale 1:20

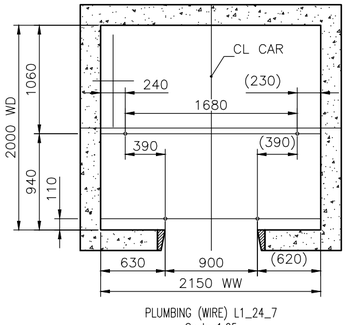

PLUMBING (WIRE) L1_24_7
Scale 1:25

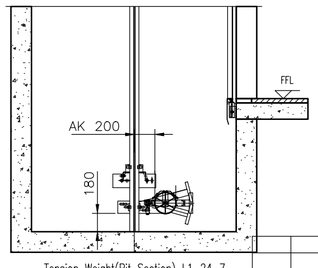

Tension Weight(Pit Section) L1_24_7
Scale 1:25

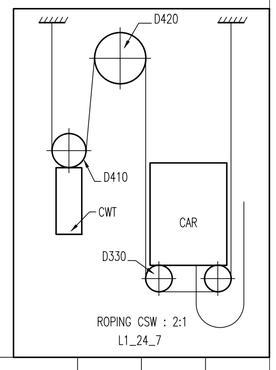

ROPING CSW : 2:1
L1_24_7

NOTE: Ladder needs to be supplied locally to access car roof from car inside after car installation. Refer to platform AM.

FOR REFERENCE ONLY

Version	Date	Description	Designed by	Checked by	Approved by
–	2024-02-21	First issue	Nuttiya Nimitsumawong		

KONE Elevators Co. Ltd.
No.88 Middle GuCheng Road
Phaholyothin
10900
Bangkok

Project name: 7 Floors Khun Keng
Site address:
Drawing title: INSTALLATION LAYOUT
Equipment number(s): L1_24_7
FL ref. number: T-0007184627
Drg no: T-0007184627-010-I-1-1
Issue: –
Page: 1 (1)

CAMOS R23.1 M006387071 KONE E MonoSpace (23.1)

© KONE Corporation

PROJECT NUMBER : VC2023-024

PROJECT
MACHI RESIDENCES
อาคารพักอาศัยรวม ค.ส.ล 7 ชั้น

OWNER
บริษัท ฤทธิกร ลิฟวิ่ง จำกัด

ARCHITECT :
อัคคะภัทร์ จิระอารีย์บุตร ส-สถ.3040
403 ซ.พัฒนาการ 50 พัฒนาการ
กรุงเทพมหานคร 10250

INTERIOR DESIGNER :
–

STRUCTURAL ENGINEER :
นายพงษ์ธวิทย์ คฑาวุธเจริญกุล สย.12291

ELECTRICAL ENGINEER :
นายภาคภูมิ คำพิทูรย์ สพก.5587

MECHANICAL ENGINEER :

SANITARY ENGINEER :
นส.อรวรรณ พลตรี สีส.134

DRAWING TITLE
แบบขยายลิฟท์ (1)

DRAWING FOR CONSTRUCTION


DRAW BY :	CHECKER :	REVISION :
Weerayuth L.	Akapatr C.	–

SCALE : 1 : 100
DRAWING NO. A-L01
DATE : 04-12-2024
FILE NAME :
JOB NO.


REVISION	DESCRIPTION

GERNERAL NOTE
DO NOT SCALE DRAWING ALL MEASUREMENT MUST BE CHECKED AT THE SIDE BY THE CONTRACTOR
ALL DESIGN AND DRAWINGS ARE THE PROPERTY OF MARCHTEN CO.,LTD
AND NOT BE USED WITH OUT THEIR WRITTEN PERMISSION

MARCHTEN
ARCHITECTURE / INTERIOR
บริษัท มาร์ชเทน จำกัด
403 ซ.พัฒนาการ 50 สวนหลวง กรุงเทพมหานคร 10250

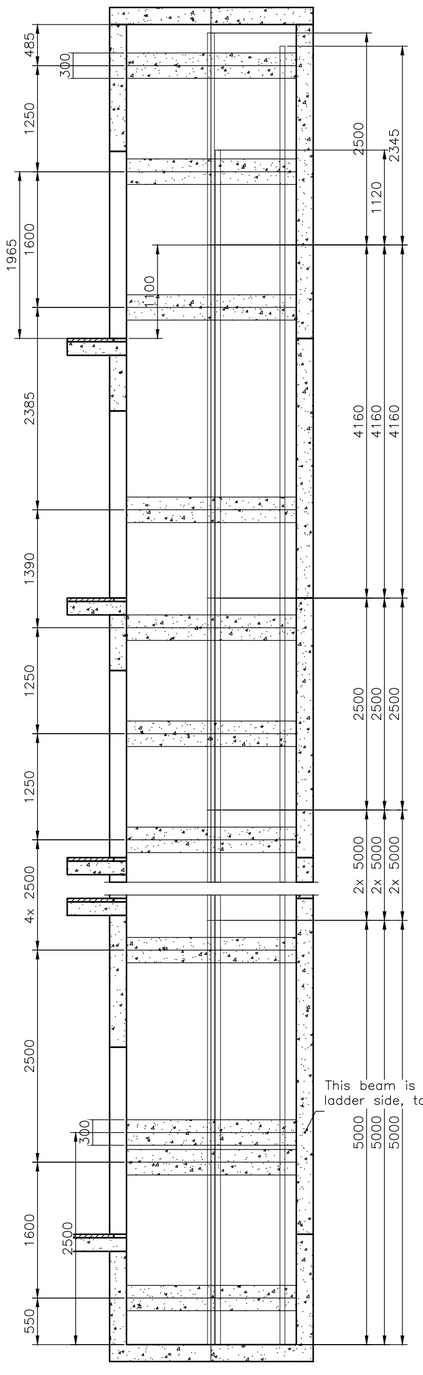


GUIDE RAIL AND DIVIDING BEAM L1_24_7
Scale 1:30

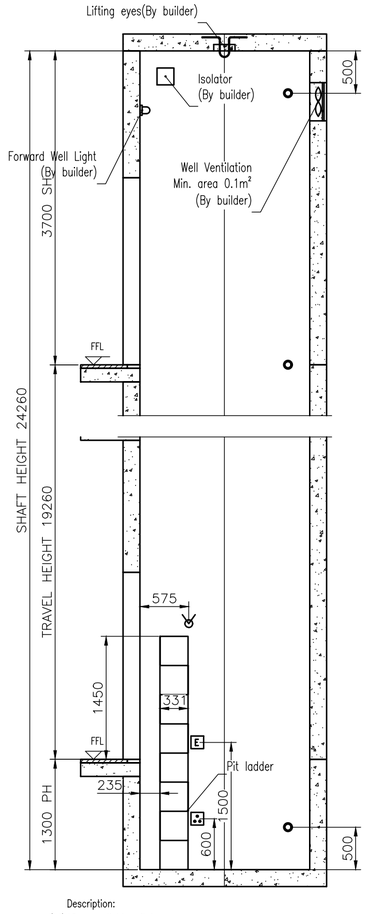



Description:
- *2 ways light switch
- E Emergency Stop
- *Water Proof Socket
- *Well Light

LIFT WELL ACCESSORIES L1_24_7
Scale 1:30

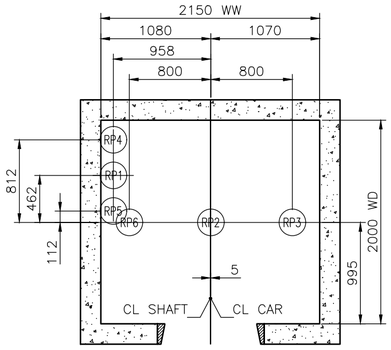


FORCES ON PIT
Scale 1:25

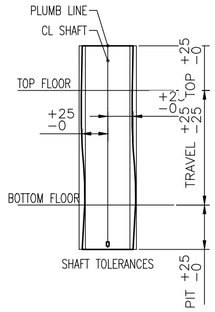

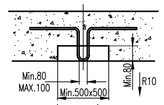

Lifting eyes(By builder)
R10 – CAPACITY 15KN L1_24_7
R9 – CAPACITY 20KN
ONLY AS DIMENSIONAL REFERENCE
LIFTING EYE STRENGTH IS UNDER BUILDER RESPONSIBILITY

LIFTING EYES CAPACITY MUST BE CERTIFIED BY BUILDER ACCORDING TO LOCAL REQUIREMENTS

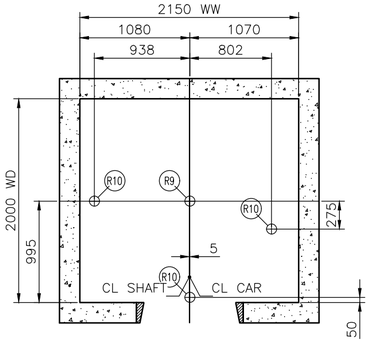

LIFTING EYE PLACEMENT
Scale 1:25

Guide Rail Force
ELEVATOR NUMBER(S): L1_24_7

Load	Value(kN)	Value(kN)	Value(kN)	Value(kN)
Fx car	1.68	–	–	–
Fy car	2.62	–	–	–
Fx cwt	0.19	–	–	–
Fy cwt	0.89	–	–	–

Note:

=- Fx applies to two fixings (per guide) but in opposite directions.
=- Fy applies to one fixing (per guide) at a time.

MAXIMUM REACTION LOADS ON PIT FLOOR

	L1_24_7			
Load	Value (kN)	Value (kN)	Value (kN)	Value (kN)
RP1	71			
RP2	90			
RP3	34			
RP4	22			
RP5	7			
RP6	50			

Note:

Reaction loads RP1–RP6 on the pit bottom are not simultaneous

Version	Date	Description	Designed by	Checked by	Approved by
–	2024-02-21	First issue	Nutliya Nimitsumawong		

KONE Elevators Co. Ltd.
No.88 Middle GuCheng Road
Phaholyothin
10900
Bangkok

Project name: 7 Floors Khun Keng
Site address:
Drawing title: LAYOUT FOR BUILDER
Equipment number(s): L1_24_7
FL ref. number: T-0007184627
Drg no: T-0007184627-010-B-1-1
Issue: –
Page: 1 (2)

FOR REFERENCE ONLY

CAMOS R23.1 M006387071 KONE E MonoSpace (23.1)

© KONE Corporation

PROJECT NUMBER : VC2023-024

PROJECT
MACHI RESIDENCES
อาคารพักอาศัยรวม ค.ส.ล 7 ชั้น

OWNER
บริษัท ฤทธิกร ลิฟวิ่ง จำกัด

ARCHITECT :
อัคคะศักร์ จิระอารีย์บุตร ส–สถ.3040
403 ซ.พัฒนาการ 50 พัฒนาการ
กรุงเทพมหานคร 10250

INTERIOR DESIGNER :
–

STRUCTURAL ENGINEER :
นายพงษ์ธวิทย์ คฑาวุธเจริญกุล สย.12291

ELECTRICAL ENGINEER :
นายภาคภูมิ คำพิทูรย์ สพก.5587

MECHANICAL ENGINEER :

SANITARY ENGINEER :
นส.อรวรรณ พลตรี สส.134

DRAWING TITLE
แบบขยายลิฟท์ (2)


DRAWING FOR CONSTRUCTION

DRAW BY : Weerayuth L.
CHECKER : Akapatr C.
REVISION : –
SCALE : 1 : 100
DRAWING NO. A-L02
DATE : 04–12–2024
FILE NAME :
JOB NO.


REVISION	DESCRIPTION

GERNERAL NOTE
DO NOT SCALE DRAWING ALL MEASUREMENT MUST BE CHECKED AT THE SIDE BY THE CONTRACTOR
ALL DESIGN AND DRAWINGS ARE THE PROPERTY OF MARCHTEN CO.,LTD
AND NOT BE USED WITH OUT THEIR WRITTEN PERMISSION

MARCHTEN
ARCHITECTURE / INTERIOR
บริษัท มาร์ชเทน จำกัด
403 ซ.พัฒนาการ 50 สวนหลวง กรุงเทพมหานคร 10250

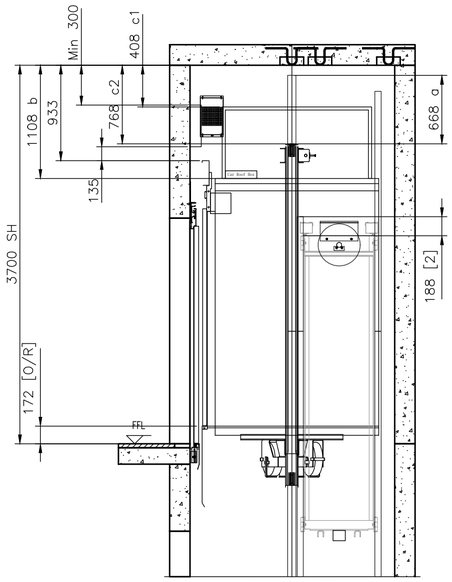

TOP CLEARANCES
(BUFFER COMPRESSED): L1_24_7
Scale 1:25

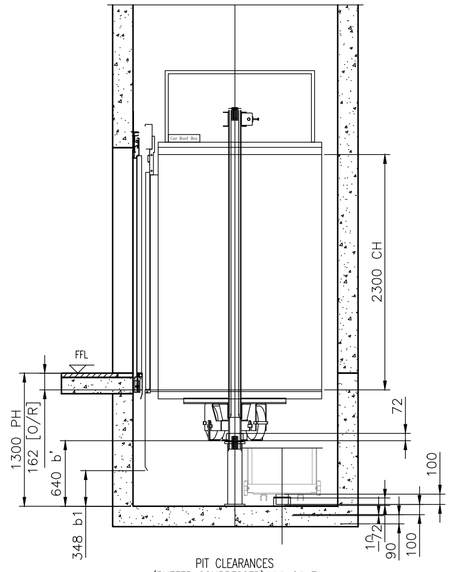

PIT CLEARANCES
(BUFFER COMPRESSED): L1_24_7

Scale 1:25

HEADROOM & PIT DIMENSIONS Follow by EN81						
CLAUSE (EN)	L1_24_7					
	ACTUAL	MINIMUM	ACTUAL	MINIMUM	ACTUAL	MINIMUM
5.7.1.1(a)	668	135				
5.7.1.1(b)	1108	1035				
5.7.1.1(c1)	408	335				
5.7.1.1(c2)	768	135				
5.7.1.2(2)	188	135				
5.7.3.3(b')	640	500				
5.7.3.3(b1)	348	100				

Layout approved with/without comments:

–

–

Date: Signature/stamp:

Version	Date	Description	Designed by	Checked by	Approved by
–	2024-02-21	First issue	Natliya Nimitsumawong		

KONE Elevators Co. Ltd.
No.88 Middle GuCheng Road
Phaholyothin
10900
Bangkok

Project name: 7 Floors Khun Keng
Site address:
Drawing title: LAYOUT FOR AUTHORITY APPROVAL
Equipment number(s): L1_24_7
FI ref. number: T-0007184627
Drg no: T-0007184627-010-A-1-1
Cust no:
Issue: –
Page: 1 (1)

FOR REFERENCE ONLY

CAMOS R23.1 M006387071 KONE E MonoSpace (23.1)

© KONE Corporation

PROJECT NUMBER : VC2023-024

PROJECT

MACHI RESIDENCES
อาคารพักอาศัยรวม ค.ส.ล 7 ชั้น

OWNER

บริษัท ฤทธิกร ลิฟวิ่ง จำกัด

ARCHITECT :
อัคคะภัทร์ จิระอารีย์บุตร ส-สถ.3040
403 ซ.พัฒนาการ 50 พัฒนาการ
กรุงเทพมหานคร 10250

INTERIOR DESIGNER :
–

STRUCTURAL ENGINEER :
นายพงษ์ธวิทย์ คฑาวุธเจริญกุล สย.12291

ELECTRICAL ENGINEER :
นายภาคภูมิ คำพิทูรย์ สพก.5587

MECHANICAL ENGINEER :

SANITARY ENGINEER :
นส.อรวรรณ พลตรี สส.134

DRAWING TITLE

แบบขยายลิฟท์ (3)

DRAWING FOR CONSTRUCTION

DRAW BY :	CHECKER :	REVISION :
Weerayuth L.	Akapatr C.	–

SCALE : 1 : 100

DRAWING NO. A-L03

DATE : 04-12-2024


FILE NAME :

JOB NO.


REVISION	DESCRIPTION

GERNERAL NOTE
DO NOT SCALE DRAWING ALL MEASUREMENT MUST BE CHECKED AT THE SIDE BY THE CONTRACTOR
ALL DESIGN AND DRAWINGS ARE THE PROPERTY OF MARCHTEN CO.,LTD
AND NOT BE USED WITH OUT THEIR WRITTEN PERMISSION


MARCHTEN
ARCHITECTURE / INTERIOR
บริษัท มาร์ชเทน จำกัด
403 ซ.พัฒนาการ 50 สวนหลวง กรุงเทพมหานคร 10250

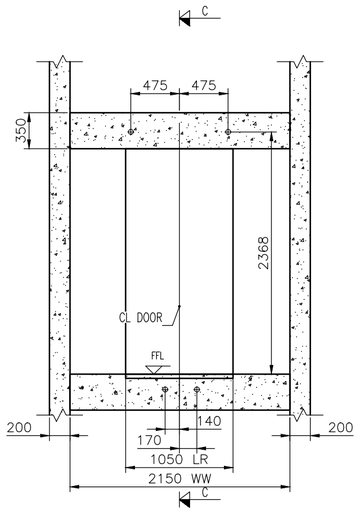

L1_24_7
VIEW FROM WELL, STRUCTURAL OPENING
Scale 1:25

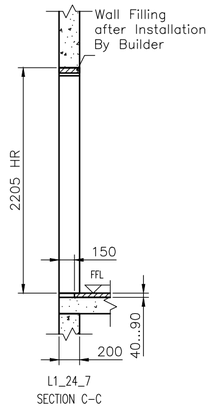

L1_24_7
SECTION C-C

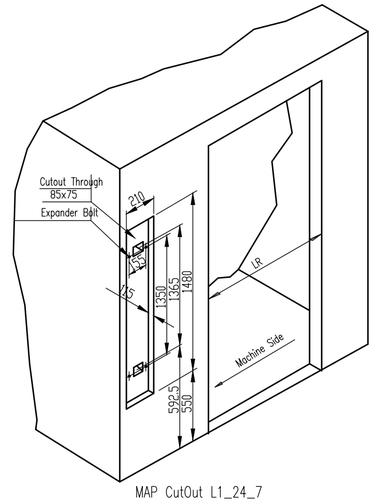


MAP CutOut L1_24_7

Landing Call And Hall Lantern L1_24_7	KDS220		
	SHAPE	A LANDING NO	C LANDING NO
LCI4 Landing Call Indicator (Without key)		1	–
LCI5 Landing Call Indicator (Without key)		2–6	–
LCI6 Landing Call Indicator (Without key)		7	–


Floor NO	Service Floor A	Service Floor C	Floor Mark	Floor Distance (mm)
7	X	N	7	
6	X	N	6	3060
5	X	N	5	3060
4	X	N	4	3060
3	X	N	3	3060
2	X	N	2	3060
1	M	N	1	3960

L1_24_7


LEGEND:
M MAIN FLOOR E EMERGENCY DOOR
X SERVED FLOOR N NON-SERVED FLOOR

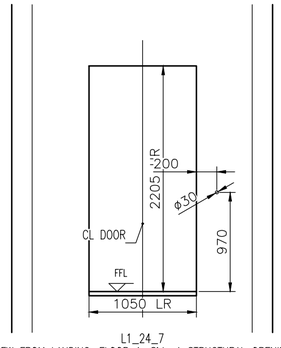


L1_24_7
VIEW FROM LANDING, FLOOR 1, Side A STRUCTURAL OPENING
Scale 1:25

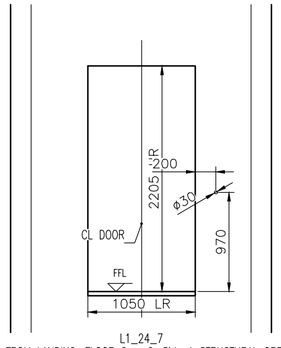


L1_24_7
VIEW FROM LANDING, FLOOR 2 – 6, Side A STRUCTURAL OPENING
Scale 1:25

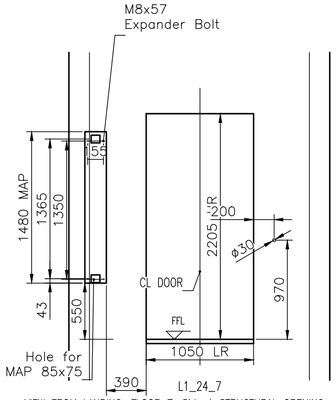


L1_24_7
VIEW FROM LANDING, FLOOR 7, Side A STRUCTURAL OPENING
Scale 1:25

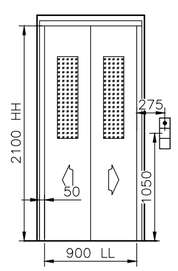

L1_24_7
FOR LANDING CALL
FLOOR 1, Side A
Scale 1:25

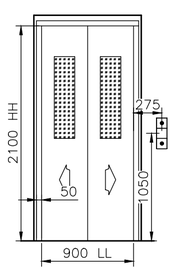

L1_24_7
FOR LANDING CALL
FLOOR 2 – 6, Side A
Scale 1:25

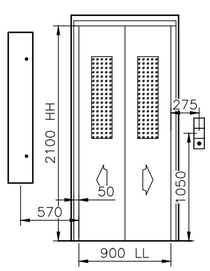

L1_24_7
FOR LANDING CALL
FLOOR 7, Side A
Scale 1:25

FOR REFERENCE ONLY

© KONE Corporation

Version	Date	Description	Designed by	Checked by	Approved by
–	2024-02-21	First issue	Nuttiya Nimitsumawong		

KONE Elevators Co. Ltd.
No.88 Middle GuCheng Road
Phaholyothin
10900
Bangkok

Project name: 7 Floors Khun Keng
Site address:
Drawing title: LAYOUT FOR BUILDER
Equipment number(s): L1_24_7
FL ref. number: T-0007184627
Drg no: T-0007184627-010-B-3-1
Issue: –
Page: 2 (2)

CAMOS R23.1 M006387071 KONE E MonoSpace (23.1)

PROJECT NUMBER : VC2023-024

PROJECT

MACHI RESIDENCES
อาคารพักอาศัยรวม ค.ส.ล 7 ชั้น

OWNER

บริษัท ฤทธิกร ลิฟวิ่ง จำกัด

ARCHITECT :

อัคคะศักร์ จิระอารีย์บุตร ส–สถ.3040
403 ซ.พัฒนาการ 50 พัฒนาการ
กรุงเทพมหานคร 10250

INTERIOR DESIGNER :

–

STRUCTURAL ENGINEER :

นายพงษ์ธวิทย์ คฑาวุธเจริญกุล สย.12291

ELECTRICAL ENGINEER :

นายภาคภูมิ คำพิทูรย์ สพก.5587

MECHANICAL ENGINEER :

SANITARY ENGINEER :

นส.อรวรรณ พลตรี สส.134

DRAWING TITLE

แบบขยายลิฟท์ (4)

DRAWING FOR CONSTRUCTION

DRAW BY :	CHECKER :	REVISION :
Weerayuth L.	Akapatr C.	–

SCALE : 1 : 100
DRAWING NO. A-L04
DATE : 04–12–2024
FILE NAME :
JOB NO.

REVISION	DESCRIPTION


GERNERAL NOTE
DO NOT SCALE DRAWING ALL MEASUREMENT MUST BE CHECKED AT THE SIDE BY THE CONTRACTOR
ALL DESIGN AND DRAWINGS ARE THE PROPERTY OF MARCHTEN CO.,LTD
AND NOT BE USED WITH OUT THEIR WRITTEN PERMISSION

MARCHTEN
ARCHITECTURE / INTERIOR
บริษัท มาร์ชเทน จำกัด
403 ซ.พัฒนาการ 50 สวนหลวง กรุงเทพมหานคร 10250


TECHNICAL SPECIFICATION FOR ELEVATOR	L1_24_7
Equipment Number	L1_24_7
Safety code	EN81-1
KONE product type	PW13/10-19
Rated load	1000 kg
Number of persons	13
Rated speed	1.00 m/s
Acceleration/deceleration rate	0.5 m/s²
Travel	19260 mm
No. of floors/No. of stops	7/7
Car entrances	1
LandingDoor type	Base duty (N2)
Door width	900 mm
Door height	2100 mm
Car type	HMC
Car internal height	2300 mm
Car internal width	1500 mm
Car internal depth	1600 mm
Car area	2.47 m²
Car guide rails	T82/B
Car buffers	E165/72
Car Deco Allowance	0 kg
Counterweight sling	CWF11PWS
Counterweight guide rails	HG65-2.0
Counterweight buffers	E165/72
Drive system	KDL16L
Control system	KCE
Machine	NMX11
Traction sheave diameter	420 mm
Undercut angle	105°
Roping arrangement	2:1
Suspension ropes (no x D)	6xd8
Overspeed governor(Car)	OL35
Overspeed governor rope(Car)	d6
Car mass (K)+Car sling mass (T)	868 kg
Car balancing factor	50%
ELECTRICAL REQUIREMENTS	
Main supply voltage	3x380Vac +10%/-10%
Frequency	50 Hz ± 1Hz
Riser fuses	3x20 A
Riser fuses for separate lighting	1x16 A
Nominal line current (no including lighting)	13.8 A
Max. RMS acceleration line current	18.5 A
Main fuses	3x16 A
Lighting fuses (shaft + car)	10 A + 6 A
Thermal losses in machine room	1.04 kW
Motor output power at nominal load	5.7 kW
Motor RPM at full speed	90.9 rpm
Maximum start/hour	180/ED40%


Important information for builders:
All the items marked with * should be provided by Builder
1. Concrete structural wall for brackets of guide rail landing doors and sill supports.
   If not please contact KONE for confirmation.
2. Ventilation to ensure the temperature is within 5°C – 40°C humidity is 95% in well or machine room.
3. Reaction forces in pit shown on the drawing must be fulfilled. Pit is clean and dry.
4. Extra concrete plinth or cwt safety gear must be provided if there is any space that people can access under the pit.
5. Landing door cutout height should be accounted from the finished floor level. Floor sill is not allowed.
6. Nominal power main supply is TN-S type: l1+l2+l3+n+pe (TN-S).
7. A partition between the moving parts of different lifts if well contains several lifts. This partition shall extend at least from the lowest point of travel of the car the counterweight or the balancing weight to a height of 2.5m above the floor of the lowest landing. The width shall be as to prevent access from one pit to another.
8. Elevator main switch and isolator can't have the function of earth leakage Protection.
9. The illumination intensity must at least be 50 LUX at 1m above the car roof pit floor. The machine room should be provided with permanently installed electric lighting on the basis of at least 200 lux at floor level.
13. The elevator shaft and elevator machine room shall not be arranged close to the bedroom, and other rooms with quiet requirements?
11. Installation and access of any 3rd party electrical equipment must be confirmed with Kone.

L1_24_7 ELECTRICAL SCHEMATIC

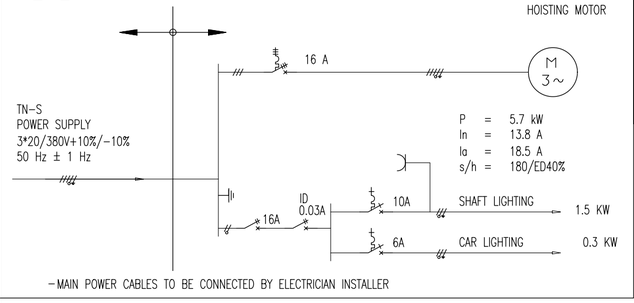

-MAIN POWER CABLES TO BE CONNECTED BY ELECTRICIAN INSTALLER

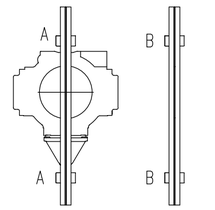

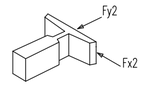

Equipment Number	Fx2 (kN) A		Fx2 (kN) B		Fy2 (kN) A	
	Static	Impact	Static	Impact	Static	Impact
L1_24_7	2.63	3.7	3.97	5.23	2.09	3.3

Guide bracket loads on shaft overhead

The building reaction forces and moments shall be calculated using the Fx, Fy, Fz, Fx2 and Fy2 bracket forces and the lenght of fixing bracket (see drawing I-1). The pull out forces of the fixing elements shall be calculated using the fixing elements distance (see drawing B-1).


Fx effects two car brackets at the same time (per guide)
The direction is opposite to each other.

Fy effects one car bracket (per guide) at the same time. The direction of the force is always positive (force against guide rail nose)

Fx2 effects the two topmost car brackets at the same time. The magnitude of both forces is the same however the directions are opposite to each other. Same applies to Fy2.

On each bracket supporting point affects a vertical force Fz,which is due to building settlement.

COMPONENT NAMES

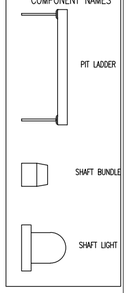

© KONE Corporation

FOR REFERENCE ONLY

Layout approved with/without comments:

– –
–

Date: Signature/stamp:

Version	Date	Description	Designed by	Checked by	Approved by
–	2024-02-21	First issue	Nuttiya Nimitsumarong		

KONE Elevators Co. Ltd.
No.88 Middle GuCheng Road
Phaholyothin
10900
Bangkok

Project name: 7 Floors Khun Keng
Site address:
Drawing title: GENERAL DRAWING
Equipment number(s): L1_24_7
FI. ref. number: T-0007184627
Drg no: T-0007184627-010-G-1
Issue: –
Page: 1 (1)

CAMOS R23.1 M006387071 KONE E MonoSpace (23.1)

PROJECT NUMBER : VC2023-024

PROJECT

MACHI RESIDENCES
อาคารพักอาศัยรวม ค.ส.ล 7 ชั้น

OWNER

บริษัท ฤทธิกร ลิฟวิ่ง จำกัด

ARCHITECT :

อัคคะภัทร์ จิระอารีย์บุตร ส-สถ.3040
403 ซ.พัฒนาการ 50 พัฒนาการ
กรุงเทพมหานคร 10250

INTERIOR DESIGNER :

–

STRUCTURAL ENGINEER :

นายพงษ์ธวิทย์ คทาวุธเจริญกุล สย.12291

ELECTRICAL ENGINEER :

นายภาคภูมิ คำพิทูรย์ สพก.5587

MECHANICAL ENGINEER :

SANITARY ENGINEER :

นส.อรวรรณ พลตรี สส.134

DRAWING TITLE

แบบขยายลิฟท์ (5)

DRAWING FOR CONSTRUCTION


DRAW BY :	CHECKER :	REVISION :
Weerayuth L.	Akapatr C.	–

SCALE : 1 : 100
DRAWING NO. A-L05
DATE : 04-12-2024
FILE NAME :
JOB NO.


REVISION	DESCRIPTION

GERNERAL NOTE
DO NOT SCALE DRAWING ALL MEASUREMENT MUST BE CHECKED AT THE SIDE BY THE CONTRACTOR
ALL DESIGN AND DRAWINGS ARE THE PROPERTY OF MARCHTEN CO.,LTD
AND NOT BE USED WITH OUT THEIR WRITTEN PERMISSION


MARCHTEN
ARCHITECTURE / INTERIOR
บริษัท มาร์ชเทน จำกัด
403 ซ.พัฒนาการ 50 สวนหลวง กรุงเทพมหานคร 10250

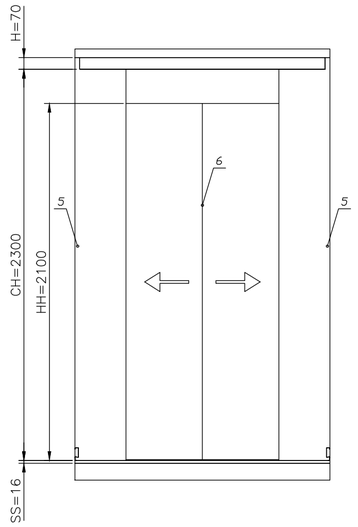


VIEW "A"

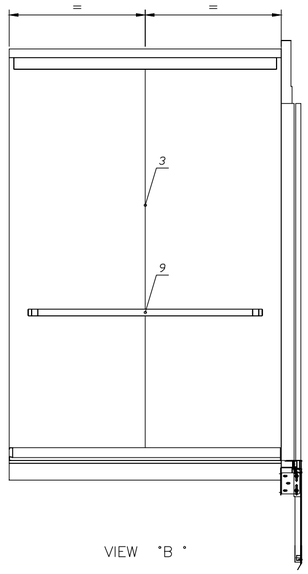


VIEW "B"

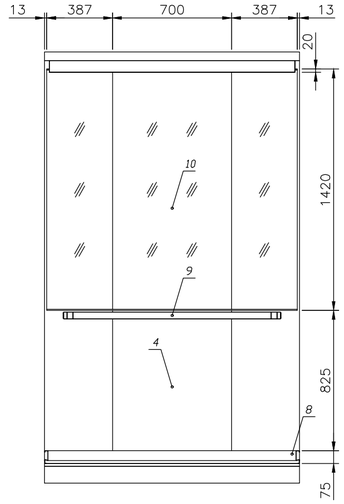


VIEW "C"

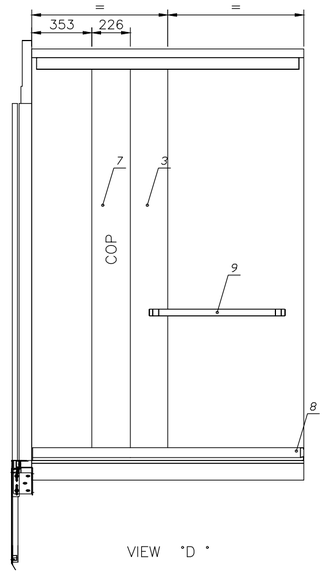

VIEW "D"

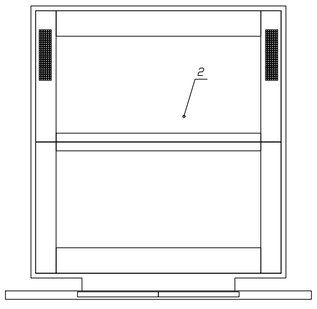

REFLECTED CEILING PLAN

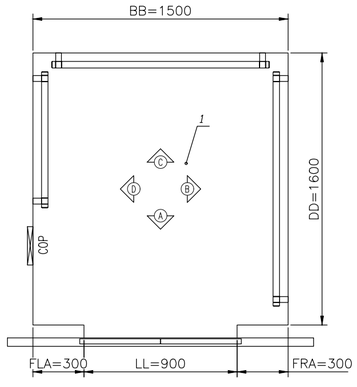

FLOOR PLAN

DESCRIPTION OF ITEMS		
1	FLOOR DECORATION	PVC D25 Rocky gray
2	ROOF	Ceiling CL71 Silver brushed StSt-ST4
3	B SIDE WALL D SIDE WALL	Silver brushed StSt-ST4 Silver brushed StSt-ST4
4	REAR WALL MIDDLE PANEL REAR WALL SIDE PANEL	Silver brushed StSt-ST4 Silver brushed StSt-ST4
5	FRONT WALL	Silver brushed StSt-ST4
6	CAR DOOR	Silver brushed StSt-ST4
7	CAR OPERATING PANEL	ST43
8	SKIRTING	Silver brushed StSt-ST4
9	HANDRAIL	HR61
10	MIRROR	MIRROR

Version	Date	Description	Designed by	Checked by	Approved by
–	2024-02-21	First issue	Nuttiya Nimitsumaneng		

KONE Elevators Co. Ltd.
No.88 Middle GuCheng Road
Phaholyothin
10900
Bangkok

Project name: 7 Floors Khun Keng
Site address:
Drawing title: CAR INTERIOR DRAWING
Equipment number(s): L1_24_7
FL ref. number: T-0007184627
Drg no: T-0007184627-010-M-1-1
Issue: –
Page: 1 (1)

CAMOS R23.1 M006387071 KONE E MonoSpace (23.1)

© KONE Corporation

PROJECT NUMBER : VC2023-024

PROJECT

MACHI RESIDENCES
อาคารพักอาศัยรวม ค.ส.ล 7 ชั้น

OWNER

บริษัท ฤทธิกร ลิฟวิ่ง จำกัด

ARCHITECT :
อัคคะภัทร์ จิระอารีย์บุตร ส-สถ.3040
403 ซ.พัฒนาการ 50 พัฒนาการ
กรุงเทพมหานคร 10250

INTERIOR DESIGNER :
–

STRUCTURAL ENGINEER :
นายพงษ์ธวิทย์ คทาวุธเจริญกุล สย.12291

ELECTRICAL ENGINEER :
นายภาคภูมิ คำพิทูรย์ สพก.5587

MECHANICAL ENGINEER :

SANITARY ENGINEER :
นส.อรวรรณ พลตรี สส.134

DRAWING TITLE

แบบขยายลิฟท์ (6)

DRAWING FOR CONSTRUCTION


DRAW BY :	CHECKER :	REVISION :
Weerayuth L.	Akapatr C.	–

SCALE : 1 : 100
DRAWING NO. A-L06
DATE : 04-12-2024
FILE NAME :
JOB NO.

REVISION	DESCRIPTION

GERNERAL NOTE
DO NOT SCALE DRAWING ALL MEASUREMENT MUST BE CHECKED AT THE SIDE BY THE CONTRACTOR
ALL DESIGN AND DRAWINGS ARE THE PROPERTY OF MARCHTEN CO.,LTD AND NOT BE USED WITH OUT THEIR WRITTEN PERMISSION

MARCHTEN
ARCHITECTURE / INTERIOR
บริษัท มาร์ชเทน จำกัด
403 ซ.พัฒนาการ 50 สวนหลวง กรุงเทพมหานคร 10250

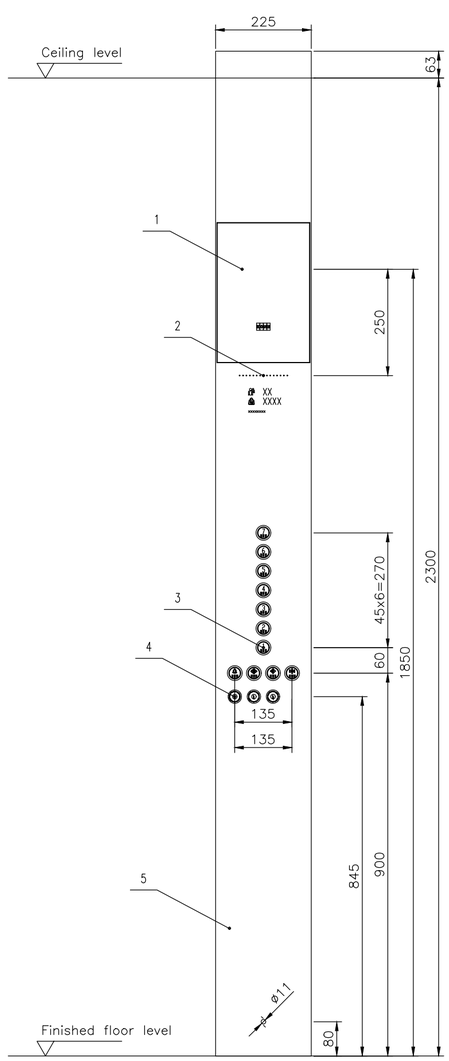

Main COP
Scale 1:6

DESCRIPTION OF ITEMS	
1	Display:
2	Intercom
3	Button: Round surface with Braille
4	Key switch: OCL AF;OCV AF;OSS;
5	Faceplate: ST43

Note: For reference only

Version	Date	Description	Designed by	Checked by	Approved by
–	2024-02-21	First issue	Nuttiya Nimitsumawong		

KONE Elevators Co. Ltd.
No.88 Middle GuCheng Road
Phaholyothin
10900
Bangkok

Project name: 7 Floors Khun Keng
Site address:
Drawing title: SIGNALIZATION DRAWING
Equipment number(s): L1_24_7
FL ref. number: T-0007184627
Drg no.: T-0007184627-010-S-1-1
Issue: –
Page: 1 (1)

CAMOS R23.1 M006387071 KONE E MonoSpace (23.1)

PROJECT NUMBER : VC2023-024

PROJECT

MACHI RESIDENCES
อาคารพักอาศัยรวม ค.ส.ล 7 ชั้น

OWNER

บริษัท ฤทธิกร ลิฟวิ่ง จำกัด

ARCHITECT :

อัคคะภัทร์ จิระอารีย์บุตร ส-สถ.3040
403 ซ.พัฒนาการ 50 พัฒนาการ
กรุงเทพมหานคร 10250

INTERIOR DESIGNER :

–

STRUCTURAL ENGINEER :

นายพงษ์ธวิทย์ คทาวุธเจริญกุล สย.12291

ELECTRICAL ENGINEER :

นายภาคภูมิ คำพิทูรย์ สพก.5587

MECHANICAL ENGINEER :

SANITARY ENGINEER :

นส.อรวรรณ พลตรี สส.134

DRAWING TITLE

แบบขยายลิฟท์ (7)

DRAWING FOR CONSTRUCTION

DRAW BY :	CHECKER :	REVISION :
Weerayuth L.	Akapatr C.	–

SCALE : 1 : 100
DRAWING NO. A-L07
DATE : 04-12-2024
FILE NAME :
JOB NO.

REVISION	DESCRIPTION

GERNERAL NOTE
DO NOT SCALE DRAWING ALL MEASUREMENT MUST BE CHECKED AT THE SIDE BY THE CONTRACTOR

ALL DESIGN AND DRAWINGS ARE THE PROPERTY OF MARCHTEN CO.,LTD AND NOT BE USED WITH OUT THEIR WRITTEN PERMISSION

MARCHTEN
ARCHITECTURE / INTERIOR

บริษัท มาร์ชเทน จำกัด
403 ซ.พัฒนาการ 50 สวนหลวง กรุงเทพมหานคร 10250