แบบระบบไฟฟ้า (ELECTRICAL SYSTEM)

DRAWING LIST

DWG. No.	DRAWING TITLE
EE-01	DRAWING LIST SYMBOLS AND DESCRIPTION
EE-02	Riser Diagram for Electrical System And Firalarm System.
EE-03	Riser Diagram for MATV System.
	Riser Diagram for CCTV System And Computer System.
EE-04	MDB SINGLE LINE DIAGRAM
EE-05	Load schedule ตารางโหลด Consuer Unit ในห้องพัก
EE-06	ผังไฟฟ้าและสวิตช์ชั้น 1
EE-07	ผังไฟฟ้าและสวิตช์ชั้น 2
EE-08	ผังไฟฟ้าและสวิตช์ชั้น 3-5
EE-09	ผังไฟฟ้าและสวิตช์ชั้น 6
EE-10	ผังไฟฟ้าและสวิตช์ชั้น 7
EE-11	ผังปลั๊กไฟชั้น 1
EE-12	ผังปลั๊กไฟชั้น 2
EE-13	ผังปลั๊กไฟชั้น 3-5
EE-14	ผังปลั๊กไฟชั้น 6
EE-15	ผังปลั๊กไฟชั้น 7
EE-16	แปลนแสดงระบบสัญญาณแจ้งเหตุเพลิงไหม้ , กล้องวงจรปิด , Access Point ชั้น 1
EE-17	แปลนแสดงระบบสัญญาณแจ้งเหตุเพลิงไหม้ , กล้องวงจรปิด , Access Point ชั้น 2
EE-18	แปลนแสดงระบบสัญญาณแจ้งเหตุเพลิงไหม้ , กล้องวงจรปิด , Access Point ชั้น 3-5
EE-19	แปลนแสดงระบบสัญญาณแจ้งเหตุเพลิงไหม้ , กล้องวงจรปิด , Access Point ชั้น 6
EE-20	แปลนแสดงระบบสัญญาณแจ้งเหตุเพลิงไหม้ , กล้องวงจรปิด , Access Point ชั้น 7
EE-21	แปลนแสดงระบบล่อฟ้า
EE-22	TYPICAL DETAIL OF LIGHTNING PROTECTION
EE-23	แบบขยายการติดตั้ง 1
EE-24	แบบขยายการติดตั้ง 2

SYMBOLS AND DESCRIPTION

ITEM	DESCRIPTION
	ELECTRICAL SYSTEM
MDB	MAIN DISTRIBUTION BOARD (MDB.) ตู้เมนประจำอาคาร
	LOAD PANEL (LP.) ตู้เมนประจำชั้น
	LOAD CENTER (LCX ตู้เมนประจำห้อง)
	เต้ารับไฟฟ้าคู่มีกราวด์ 16A-250V ตราช้าง
U	เต้ารับไฟฟ้าคู่มีกราวด์ 16A-250V(Universal type) ตราช้าง
WP.	เต้ารับไฟฟ้าคู่มีกราวด์กันน้ำ 16A-250V ตราช้าง
AP	เต้ารับไฟฟ้าคู่มีกราวด์ สำหรับ Access Point ตราช้าง
C	เต้ารับไฟฟ้าคู่มีกราวด์ สำหรับกล้องวงจรปิด ตราช้าง
	เต้ารับไฟฟ้าคู่ ฝังพื้น
	สวิทช์ทางเดียว 10A-250V ตราช้าง
	EMERGENCY LIGHT ไฟฉุกเฉิน พร้อมเต้ารับเดี่ยวมีกราวด์
	EXIT SIGN พร้อมเต้ารับเดี่ยวมีกราวด์
H	เครื่องทำน้ำอุ่น 4,500 VA
K	KEY TAG
	FIRE ALARM SYSTEM
S	SMOKE DETECTOR
H	HEAT DETECTOR
R	RATE OF RISE HEAT DETECTOR
L	Remote Lamp
M	MANUAL PULL STATION
B	ALARM BELL
FCP	FIRE CONTROL PANEL & DISPLAY ALARM
	END RESISTOR 10K-OHM/1W
	ถังดับเพลิงชนิดน้ำยาเคมี (a,b,c) แบบมือถือ
	COMPUTER SYSTEM
DR	แผงกระจายสัญญาณคอมพิวเตอร์ (DATA DISTRIBUTION RACK)
L	COMPUTER OUTLET RJ-45 CAT6
	COMPUTER OUTLET RJ-45 CAT6 ฝังพื้น
	Access Point
	CCTV SYSTEM
CCTV	ชุดระบบกล้องทีวีวงจรปิด (CCTV CONTROLLER)
	กล้องทีวีวงจรปิด ใช้กล้อง IP POE

SYMBOLS AND DESCRIPTION

ITEM	DESCRIPTION
	Luminaire List
DL1	ดวงโคม ดาวน์ไลท์ แบบฝังฝ้าเพดาน LED 9 W
DL2	ดวงโคม ดาวน์ไลท์แบบคู่ แบบฝังฝ้าเพดาน LED 9 W (CENSOR)
	ดวงโคม ดาวน์ไลท์ แบบทรงกระบอก สีดำ LED 14 W
	ดวงโคม ดาวน์ไลท์ แบบฝังฝ้าเพดาน LED 14 W
	ไฟกระบอกติดผนัง 18 W.
	FLUORESENT T8 1x28W
	1x32W LED SQUARE
	LED Wall Washer
TAG LIGHT	TAG LIGHT
LED STL.	LED STRIP LIGHT ซ่อนในรางหลุมฝ้าเพดาน
W1	ไฟแบบมีฝาครอบ ติดผนัง 18 W. บันไดหนีไฟภายนอกอาคาร
MDF	MAIN TELEPHONE DISTRIBUTION FAME
PABX	PRIVATE AUTOMATIC BRANCH EXCHANGE
TCx	TCx
	TELEPHONE OUT LET
	TELEPHONE POPUP OUT LET (ฝังพื้น)
	MATV SYSTEM
	4- WAY SPLITER
	2- WAY SPLITER
	4- WAY TAP OFF
	2- WAY TAP OFF
	TV Outlet
TV-xx	ชุดต่อสายทีวีประจำชั้น
	LIGHTNING PROTECTION SYSTEM
	AIR TERMINAL LIGHTNING PROTECTION
C	BARE COPPER GROUND WIRE
	HEAT METAL WELD TAP JOINT
G	GROUND TEST BOX
	GROUND ROD ø 5/8" x10'
	กล่องต่อสายสำหรับเครื่องปรับอากาศ
	เครื่องปรับอากาศ แบบ Spit type INVERTER

PROJECT NUMBER : VC2023-024

PROJECT

MACHI RESIDENCES

อาคารพักอาศัยรวม ค.ส.ล 7 ชั้น

OWNER

บริษัท ฤทธิกร ลิฟวิ่ง จำกัด

ARCHITECT :

อัคคะภัทร์ จิระอารีย์บุตร ส-สถ.3040

403 ซ.พัฒนาการ 50 พัฒนาการ

กรุงเทพมหานคร 10250

INTERIOR DESIGNER :

-

STRUCTURAL ENGINEER :

นายพงษ์ธวิทย์ คทาวุธเจริญกุล ลย.12291

ELECTRICAL ENGINEER :

นายภาคภูมิ คำพิทูรย์ ลพก.5587

MECHANICAL ENGINEER :

SANITARY ENGINEER :

นส.อรวรรณ พลตรี ลส.134

DRAWING TITLE

DRAWING LIST SYMBOLS AND DESCRIPTION

DRAWING FOR CONSTRUCTION

DRAW BY :	CHECKER :	REVISION :
Weerayuth L.	Akapatr C.	-

SCALE :	DRAWING NO.
1 : 100	EE-01
DATE : 20-10-2024	
FILE NAME :	JOB NO.

REVISION	DESCRIPTION

GERNERAL NOTE

DO NOT SCALE DRAWING ALL MEASUREMENT MUST BE **CHECKED AT THE SIDE BY THE CONTRACTOR**


ALL DESIGN AND DRAWINGS ARE THE PROPERTY OF MARCHTEN CO.,LTD **AND NOT BE USED WITH OUT THEIR WRITTEN PERMISSION**

MARCHTEN


ARCHITECTURE / INTERIOR

บริษัท มาร์ชเทน จำกัด

403 ซ.พัฒนาการ 50 สวนหลวง กรุงเทพมหานคร 10250

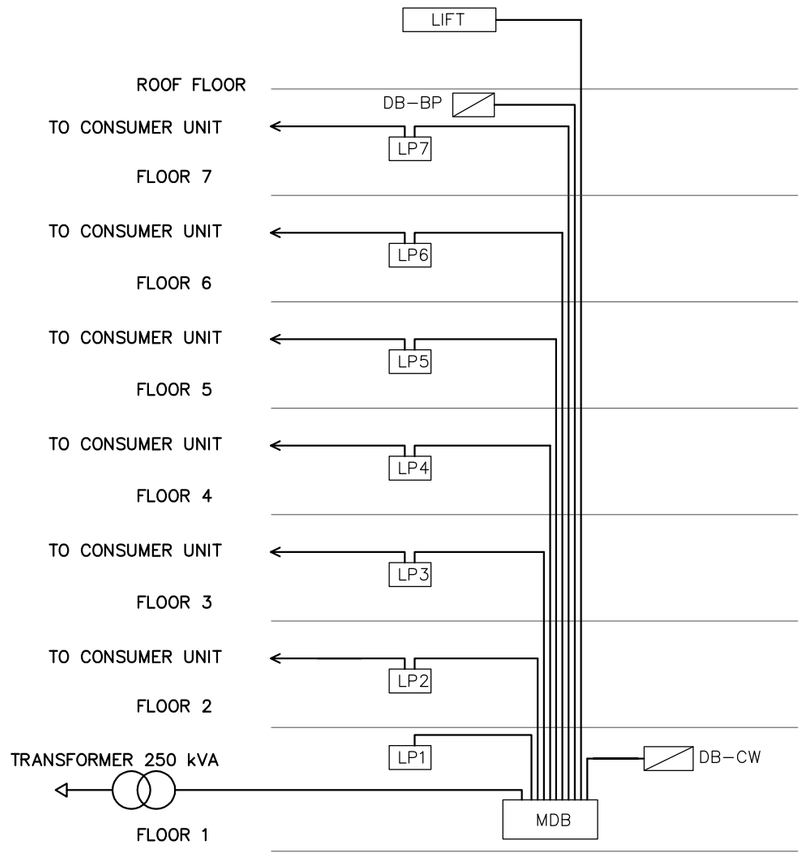

ELECTRICAL RISER DIAGRAM

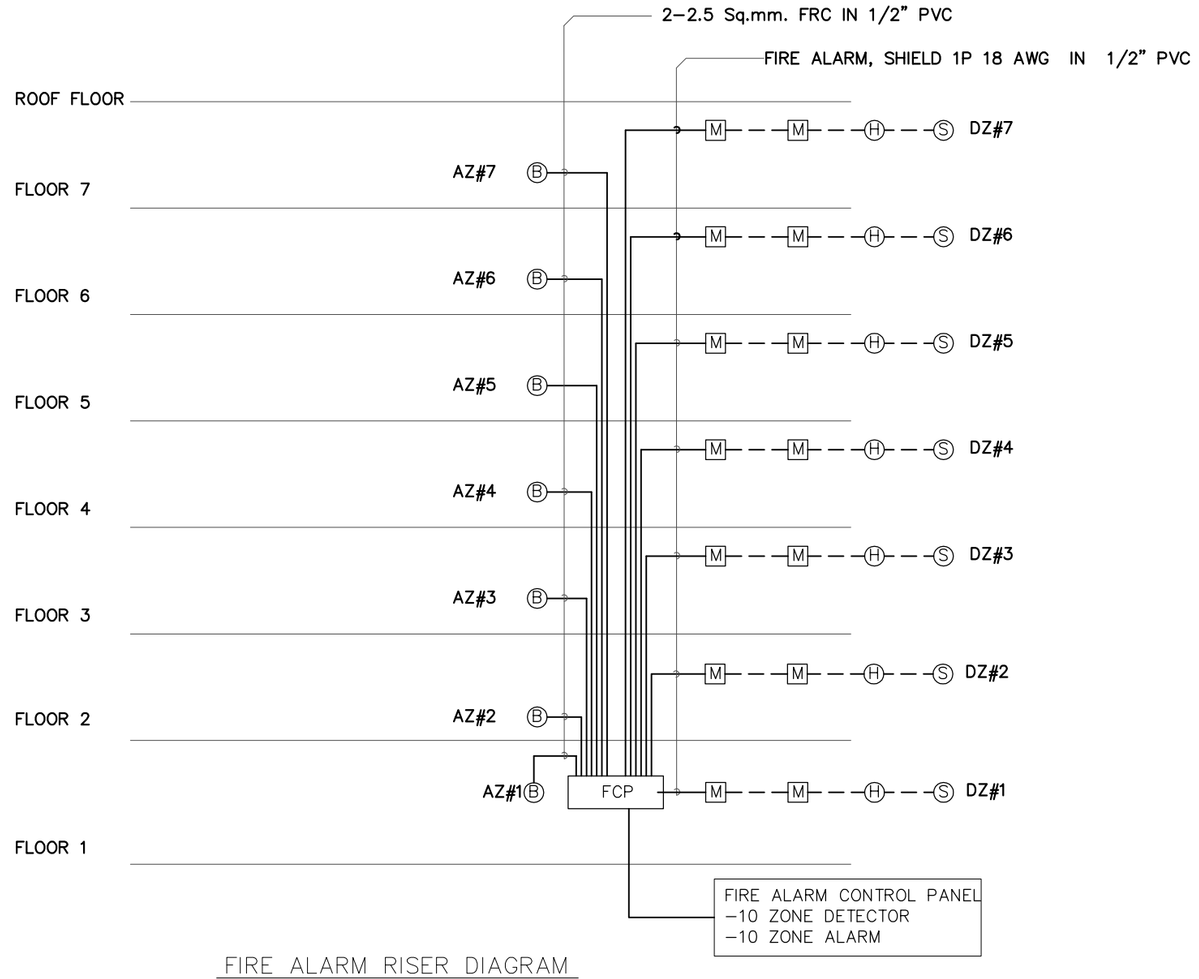

FIRE ALARM RISER DIAGRAM

PROJECT NUMBER : VC2023-024

PROJECT

MACHI RESIDENCES

อาคารพักอาศัยรวม ค.ส.ล 7 ชั้น

OWNER

บริษัท ฤทธิกร ลิฟวิ่ง จำกัด

ARCHITECT :

อัคคะภัทร์ จิระอารียบุตร ส-สถ.3040

403 ซ.พัฒนาการ 50 พัฒนาการ

กรุงเทพมหานคร 10250

INTERIOR DESIGNER :

-

STRUCTURAL ENGINEER :

นายพงษ์ธวิทย์ คทาวุธเจริญกุล ลย.12291

ELECTRICAL ENGINEER :

นายภาคภูมิ คำพิทูรย์ ลฟก.5587

MECHANICAL ENGINEER :

SANITARY ENGINEER :

พล.อ.อรวรรณ พลดรี ลส.134

DRAWING TITLE

Riser Diagram for Electrical System

And Firalarm System.

DRAWING FOR CONSTRUCTION

DRAW BY :	CHECKER :	REVISION :
Weerayuth L.	Akapatr C.	-

SCALE :	DRAWING NO.
1 : 100	EE-02
DATE : 20-10-2024	
FILE NAME :	JOB NO.

REVISION	DESCRIPTION

GERNERAL NOTE

DO NOT SCALE DRAWING ALL MEASUREMENT MUST BE **CHECKED AT THE SIDE BY THE CONTRACTOR**


ALL DESIGN AND DRAWINGS ARE THE PROPERTY OF MARCHTEN CO.,LTD **AND NOT BE USED WITH OUT THEIR WRITTEN PERMISSION**

MARCHTEN


ARCHITECTURE / INTERIOR

บริษัท มาร์ชเทน จำกัด


403 ซ.พัฒนาการ 50 สวนหลวง กรุงเทพมหานคร 10250

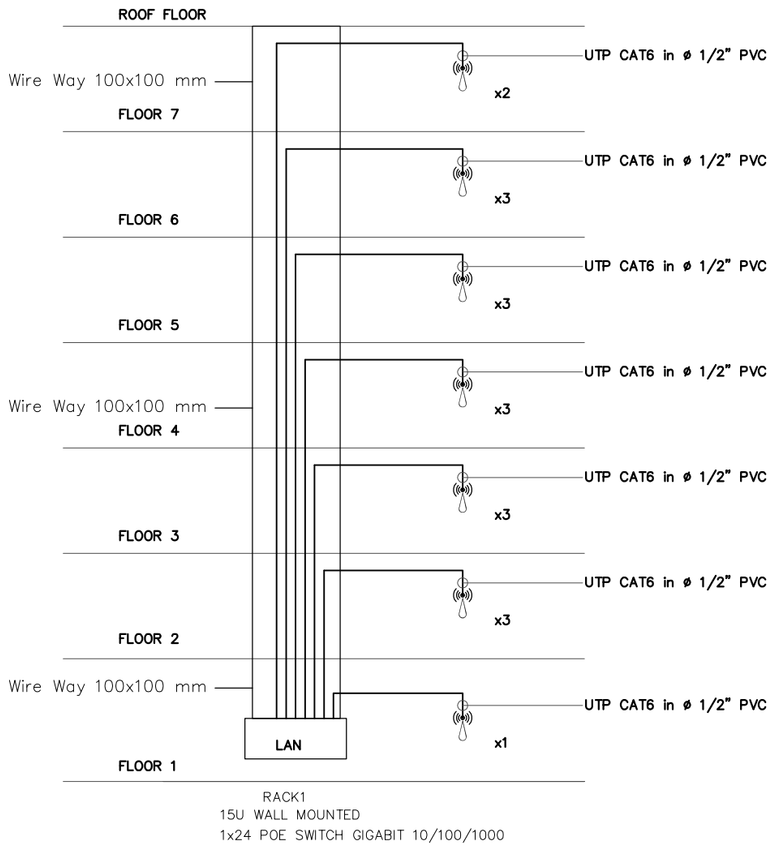

COMPUTER RISER DIAGRAM

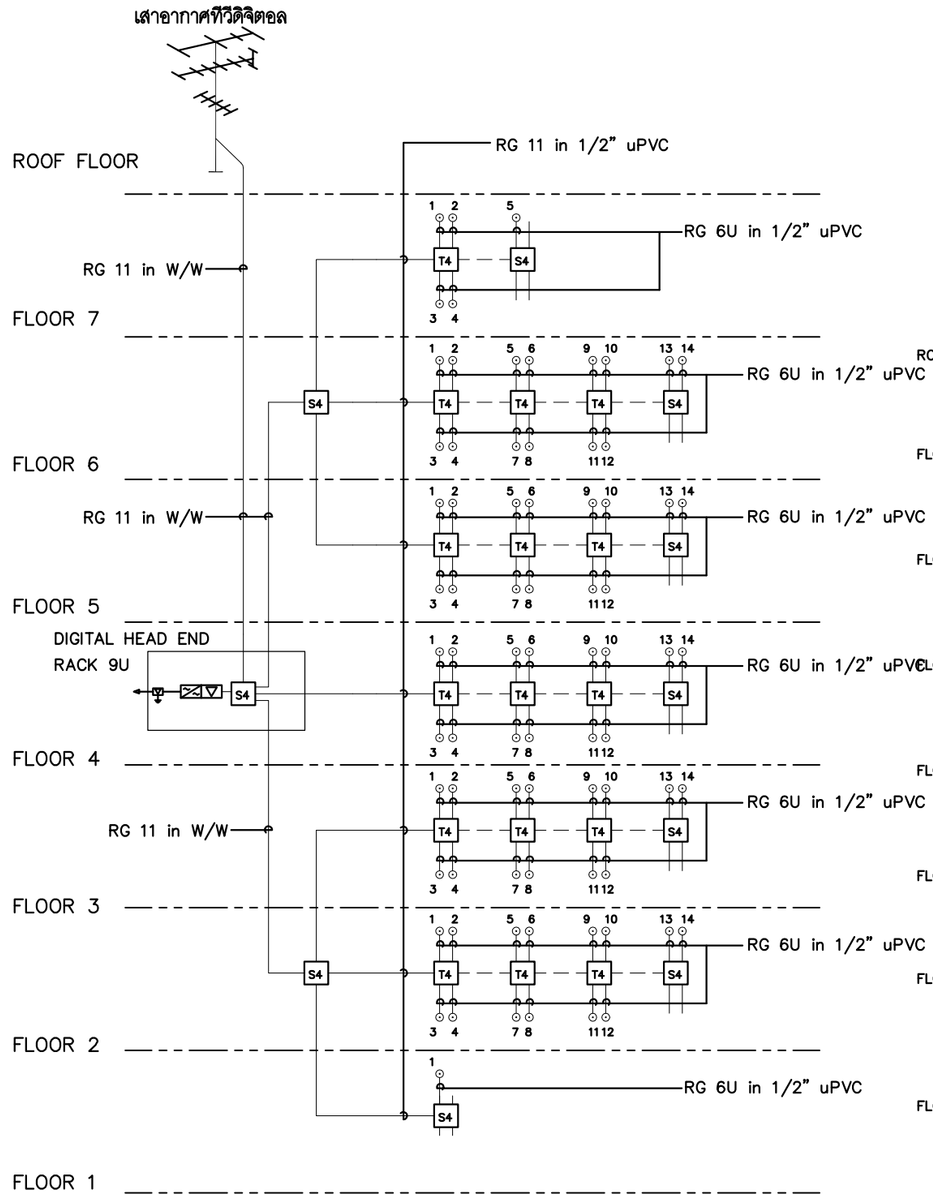

TV RISER DIAGRAM

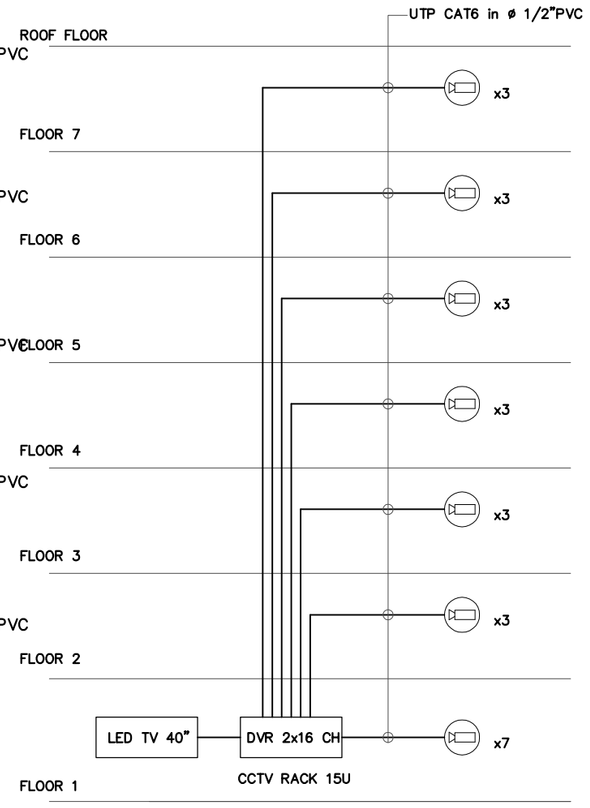

CCTV RISER DIAGRAM

PROJECT NUMBER : VC2023-024

PROJECT

MACHI RESIDENCES

อาคารพักอาศัยรวม ค.ส.ล 7 ชั้น

OWNER

บริษัท ฤทธิกร ลิฟวิ่ง จำกัด

ARCHITECT :

อัคคะภัทร์ จิระอารียบุตร ส-สถ.3040

403 ซ.พัฒนาการ 50 พัฒนาการ

กรุงเทพมหานคร 10250

INTERIOR DESIGNER :

-

STRUCTURAL ENGINEER :

นายพงษ์ธวิทย์ คทาวุธเจริญกุล ลย.12291

ELECTRICAL ENGINEER :

นายภาคภูมิ คำพิทูรย์ ลฟก.5587

MECHANICAL ENGINEER :

SANITARY ENGINEER :

นส.อรวรรณ พลตรี ลว.134

DRAWING TITLE

COMPUTER RISER DIAGRAM

TV RISER DIAGRAM

CCTV RISER DIAGRAM

DRAWING FOR CONSTRUCTION

DRAW BY :	CHECKER :	REVISION :
Weerayuth L.	Akapatr C.	-

SCALE :	DRAWING NO.
1 : 100	EE-03
DATE : 20-10-2024	
FILE NAME :	JOB NO.

REVISION	DESCRIPTION

GERNERAL NOTE

DO NOT SCALE DRAWING ALL MEASUREMENT MUST BE

CHECKED AT THE SIDE BY THE CONTRACTOR

ALL DESIGN AND DRAWINGS ARE THE PROPERTY OF

MARCHTEN CO.,LTD


AND NOT BE USED WITH OUT THEIR WRITTEN PERMISSION

MARCHTEN


ARCHITECTURE / INTERIOR

บริษัท มาร์ชเทน จำกัด


403 ซ.พัฒนาการ 50 สวนหลวง กรุงเทพมหานคร 10250

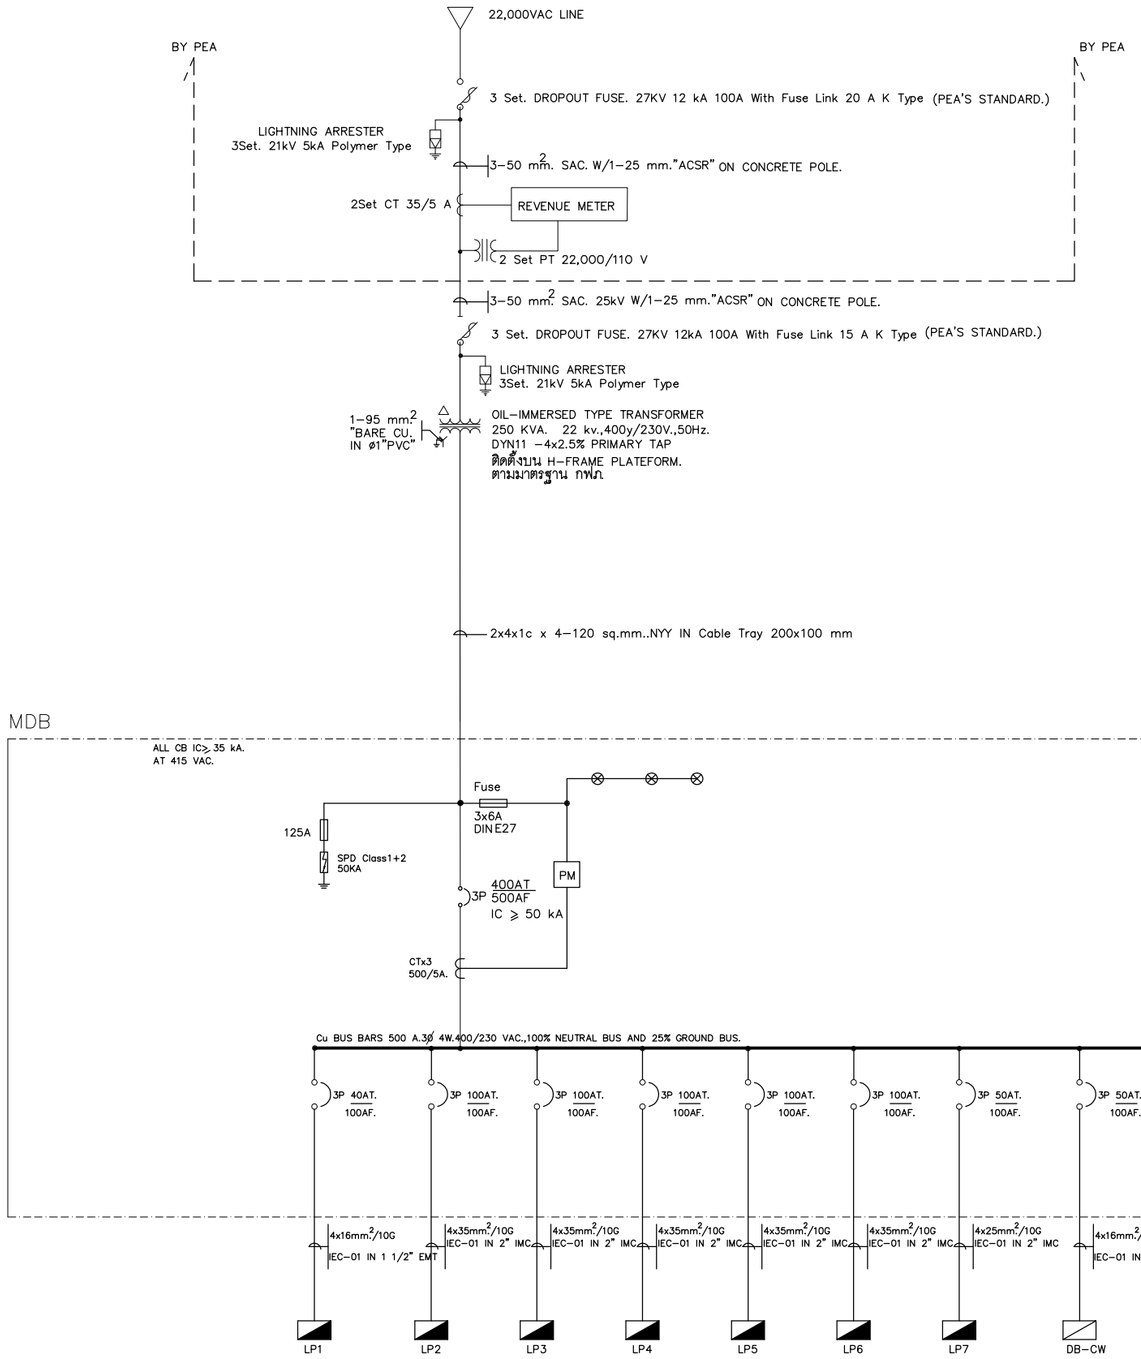

MDB SINGLE LINE DIAGRAM

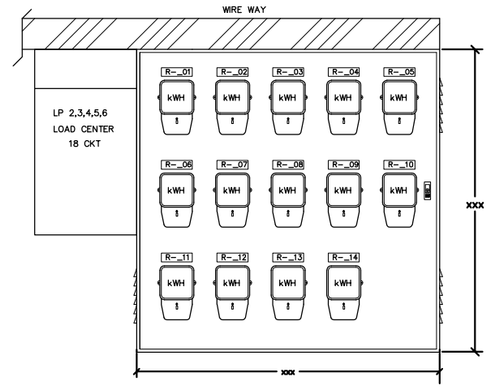

แผงมิเตอร์ไฟฟ้าประจำชั้น 2-6
NOT TO SCALE

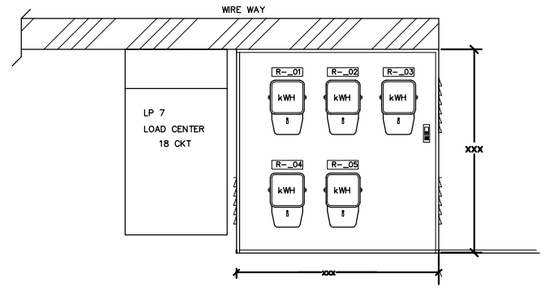

แผงมิเตอร์ไฟฟ้าประจำชั้น 7
NOT TO SCALE

PROJECT NUMBER : VC2023-024

PROJECT

MACHI RESIDENCES

อาคารพักอาศัยรวม ค.ส.ล 7 ชั้น

OWNER

บริษัท ฤทธิกร ลิฟวิ่ง จำกัด

ARCHITECT :

อัคคะภัทร์ จิระอารียบุตร ส-สถ.3040

403 ซ.พัฒนาการ 50 พัฒนาการ

กรุงเทพมหานคร 10250

INTERIOR DESIGNER :

-

STRUCTURAL ENGINEER :

นายพงษ์ธวิทย์ คทาวุธเจริญกุล ลย.12291

ELECTRICAL ENGINEER :

นายภาคภูมิ คำพิทรย์ ลฟก.5587

MECHANICAL ENGINEER :

SANITARY ENGINEER :

นส.อรวรรณ พลตรี ลส.134

DRAWING TITLE

MDB SINGLE LINE DIAGRAM

DRAWING FOR CONSTRUCTION

DRAW BY :	CHECKER :	REVISION :
Weerayuth L.	Akapatr C.	-

SCALE :	DRAWING NO.
1 : 100	EE-04
DATE : 20-10-2024	
FILE NAME :	JOB NO.

REVISION	DESCRIPTION

GERNERAL NOTE

DO NOT SCALE DRAWING ALL MEASUREMENT MUST BE
CHECKED AT THE SIDE BY THE CONTRACTOR
ALL DESIGN AND DRAWINGS ARE THE PROPERTY OF
MARCHTEN CO.,LTD
AND NOT BE USED WITH OUT THEIR WRITTEN PERMISSION

MARCHTEN
ARCHITECTURE / INTERIOR

บริษัท มาร์ชเทน จำกัด
403 ซ.พัฒนาการ 50 สวนหลวง กรุงเทพมหานคร 10250

LP1

Panel No.	LP1			Location	ชั้นที่ 1			
Capacity	18 CCT.			Mounting	SURFACE			
Connected to.	MDB			IC ≥ 10 KA. at 400/230 V.				

CKT. NO.	DESCRIPTION	Connected Load(VA) A	B	C	BRANCH CB POLE	AT	CONDUIT	WIRE SIZE(sq.mm.)	TYPE
1	แสงสว่าง	300			1	16	1/2"PVC	2x2.5.	IEC.01
3	แสงสว่าง		500		1	16	1/2"PVC	2x2.5.	IEC.01
5	สำรอง			1,000	1	16			
7	สำรอง	1,000			1	16			
9	สำรอง		1,000		1	16			
11	สำรอง			1,000	1	16			
13									
15									
17									
2	Emer & Exit	1,000			1	20	1/2"PVC	2x4/2.5"G.	IEC.01
4	เต้ารับไฟฟ้า		1,000		1	20	1/2"PVC	2x4/2.5"G.	IEC.01
6	อุปกรณ์ฮีทกุกเซ็น			500	1	20	1/2"PVC	2x4/2.5"G.	IEC.01
8	POWER FOR F/A	1,000			1	20	1/2"PVC	2x4/2.5"G.	IEC.01
10	POWER FOR LAN 15U		1,000		1	20	1/2"PVC	2x4/2.5"G.	IEC.01
12	POWER FOR LAN 15U			1,000	1	20	1/2"PVC	2x4/2.5"G.	IEC.01
14	สำรอง	1,000			1	16			
16	สำรอง		1,000		1	16			
18	สำรอง			1,000	1	16			
TOTAL CONNECTED LOAD		4,300	4,500	4,000	MAIN CIRCUIT BREAKER			MAIN FEEDER	
TOTAL LOAD		12,800			MCCB 3P 40 AT			4x16/10"G.sq.mm.	
TOTAL DEMAND LOAD		8,960			IC ≥ 25 KA.			IEC-01 1 1/2" EMT	

LP2-LP6

Panel No.	LP2,3,4,5,6			Location	ชั้นที่ 2-6			
Capacity	18 CCT.			Mounting	SURFACE			
Connected to.	MDB			IC ≥ 10 KA. at 400/230 V.				

CKT. NO.	DESCRIPTION	Connected Load(VA) A	B	C	BRANCH CB POLE	AT	CONDUIT	WIRE SIZE(sq.mm.)	TYPE
1	ห้องพัก 1	6,230			1	40	1"PVC	2x10/4"G.	IEC.01
3	ห้องพัก 3		6,230		1	40	1"PVC	2x10/4"G.	IEC.01
5	ห้องพัก 5			6,230	1	40	1"PVC	2x10/4"G.	IEC.01
7	ห้องพัก 7	6,230			1	40	1"PVC	2x10/4"G.	IEC.01
9	ห้องพัก 9		6,230		1	40	1"PVC	2x10/4"G.	IEC.01
11	ห้องพัก 11			6,230	1	40	1"PVC	2x10/4"G.	IEC.01
13	ห้องพัก 13	6,230			1	40	1"PVC	2x10/4"G.	IEC.01
15	แสงสว่าง		500		1	16	1/2"PVC	2x2.5.	IEC.01
17	สำรอง			500	1	16			
2	ห้องพัก 2	6,230			1	40	1"PVC	2x10/4"G.	IEC.01
4	ห้องพัก 4		6,230		1	40	1"PVC	2x10/4"G.	IEC.01
6	ห้องพัก 6			6,230	1	40	1"PVC	2x10/4"G.	IEC.01
8	ห้องพัก 8	6,230			1	40	1"PVC	2x10/4"G.	IEC.01
10	ห้องพัก 10		6,230		1	40	1"PVC	2x10/4"G.	IEC.01
12	ห้องพัก 12			6,230	1	40	1"PVC	2x10/4"G.	IEC.01
14	ห้องพัก 14	6,230			1	40	1"PVC	2x10/4"G.	IEC.01
16	เต้ารับไฟฟ้า		1,000		1	20	1/2"PVC	2x2.5/2.5"G.	IEC.01
18	Emer & Exit			1,000	1	20	1/2"PVC	2x2.5/2.5"G.	IEC.01
TOTAL CONNECTED LOAD		37,380	26,420	26,420	MAIN CIRCUIT BREAKER			MAIN FEEDER	
TOTAL LOAD		90,220			MCCB 3P 100 AT			4x35/10"G.sq.mm.	
TOTAL DEMAND LOAD		63,154			IC ≥ 25 KA.			IEC-01 2" IMC	

LP7

Panel No.	LP7			Location	ชั้นที่ 7			
Capacity	18 CCT.			Mounting	SURFACE			
Connected to.	MDB			IC ≥ 10 KA. at 400/230 V.				

CKT. NO.	DESCRIPTION	Connected Load(VA) A	B	C	BRANCH CB POLE	AT	CONDUIT	WIRE SIZE(sq.mm.)	TYPE
1	ห้องพัก 1	3,130			1	32	3/4"PVC	2x6/4"G.	IEC.01
3	ห้องพัก 3		3,130		1	32	3/4"PVC	2x6/4"G.	IEC.01
5	ห้องพัก 5			3,130	1	32	3/4"PVC	2x6/4"G.	IEC.01
7	แสงสว่าง	500			1	16	1/2"PVC	2x2.5.	IEC.01
9	สำรอง		500		1	16			
11	สำรอง			500	1	16			
13									
15									
17									
2	ห้องพัก 2	3,130			1	32	3/4"PVC	2x6/4"G.	IEC.01
4	ห้องพัก 4		3,130		1	32	3/4"PVC	2x6/4"G.	IEC.01
6	เต้ารับไฟฟ้า			900	1	20	3/4"PVC	2x4.0/2.5"G.	IEC.01
8	Emer & Exit	1,000			1	20	1/2"PVC	2x4.0/2.5"G.	IEC.01
10	สำรอง		1,000		1	20			
12	สำรอง			1,000	1	20			
14									
16									
18									
TOTAL CONNECTED LOAD		7,760	7,760	5,530	MAIN CIRCUIT BREAKER			MAIN FEEDER	
TOTAL LOAD		21,050			MCCB 3P 50 AT			4x25/10"G.sq.mm.	
TOTAL DEMAND LOAD		14,735			IC ≥ 25 KA.			IEC-01 2" IMC	

Panel No.	CUxy			Location	ห้องพัก			
Capacity	4 CCT.			Mounting	SURFACE			
Connected to.				IC ≥ 6 KA. at 230 V.				

CKT. NO.	DESCRIPTION	CONNECTED LOAD IN VA. Phase A or B or C	BRANCH CB POLE	AT	CONDUIT	WIRE SIZE(sq.mm.)	TYPE
1	LIGHTING	150	1	16	1/2" PVC	2 x 2.5	IEC.01
2	RECEPTACLE	1,080	1	20	1/2" PVC	2x4/2.5"G.	IEC.01
3	AIR CONDITION (16,000Btu)	1,500	1	20	1/2" PVC	2x4/2.5"G.	IEC.01
4	WATER HEATER 3,500 W.	3,500	1	32	1/2" PVC	2x4/2.5"G.	IEC.01
	TOTAL CONNECTED LOAD	6,230	MAIN CIRCUIT BREAKER			MAIN FEEDER	
			MCB 2P 32 AT RCCB 32 AT 30mA IC >_ 10 KA.			2x6/4"G. Sq.mm. IEC.01,ø 3/4" PVC	

ตารางโหลดห้องพัก ชั้น 2-6

Panel No.	CUxy			Location	ห้องพัก			
Capacity	4 CCT.			Mounting	SURFACE			
Connected to.				IC ≥ 6 KA. at 230 V.				

CKT. NO.	DESCRIPTION	CONNECTED LOAD IN VA. Phase A or B or C	BRANCH CB POLE	AT	CONDUIT	WIRE SIZE(sq.mm.)	TYPE
1	LIGHTING	50	1	16	1/2" PVC	2 x 2.5	IEC.01
2	RECEPTACLE	1,080	1	20	1/2" PVC	2x4/2.5"G.	IEC.01
3	AIR CONDITION (9,000Btu)	1,000	1	20	1/2" PVC	2x4/2.5"G.	IEC.01
4	สำรอง	1,000	1	16			
	TOTAL CONNECTED LOAD	3,130	MAIN CIRCUIT BREAKER			MAIN FEEDER	
			MCB 2P 32 AT RCCB 32 AT 30mA IC >_ 10 KA.			2x6/4"G. Sq.mm. IEC.01,ø 3/4" PVC	

ตารางโหลดห้องพัก ชั้น 7

PROJECT NUMBER : VC2023-024

PROJECT

MACHI RESIDENCES

อาคารพักอาศัยรวม ค.ส.ล 7 ชั้น

OWNER

บริษัท ฤทธิกร ลิฟวิ่ง จำกัด

ARCHITECT :

อัคคะภัทร์ จิระอารียบุตร ส-สถ.3040

403 ซ.พัฒนาการ 50 พัฒนาการ

กรุงเทพมหานคร 10250

INTERIOR DESIGNER :

-

STRUCTURAL ENGINEER :

นายพงษ์ธวิทย์ คทาวุธเจริญกุล ลย.12291

ELECTRICAL ENGINEER :

นายภาคภูมิ คำพิทูรย์ ลพก.5587

MECHANICAL ENGINEER :

SANITARY ENGINEER :

นส.อรวรรณ พลตรี ลส.134

DRAWING TITLE

Load schedule

ตารางโหลด Consuer Unit ในห้องพัก

DRAWING FOR CONSTRUCTION

DRAW BY :	CHECKER :	REVISION :
Weerayuth L.	Akapatr C.	-

SCALE :	DRAWING NO.
1 : 100	EE-05
DATE : 20-10-2024	
FILE NAME :	JOB NO.

REVISION	DESCRIPTION

GERNERAL NOTE

DO NOT SCALE DRAWING ALL MEASUREMENT MUST BE **CHECKED AT THE SIDE BY THE CONTRACTOR**


ALL DESIGN AND DRAWINGS ARE THE PROPERTY OF MARCHTEN CO.,LTD **AND NOT BE USED WITH OUT THEIR WRITTEN PERMISSION**

MARCHTEN

ARCHITECTURE / INTERIOR

บริษัท มาร์ชเทน จำกัด

403 ซ.พัฒนาการ 50 สวนหลวง กรุงเทพมหานคร 10250

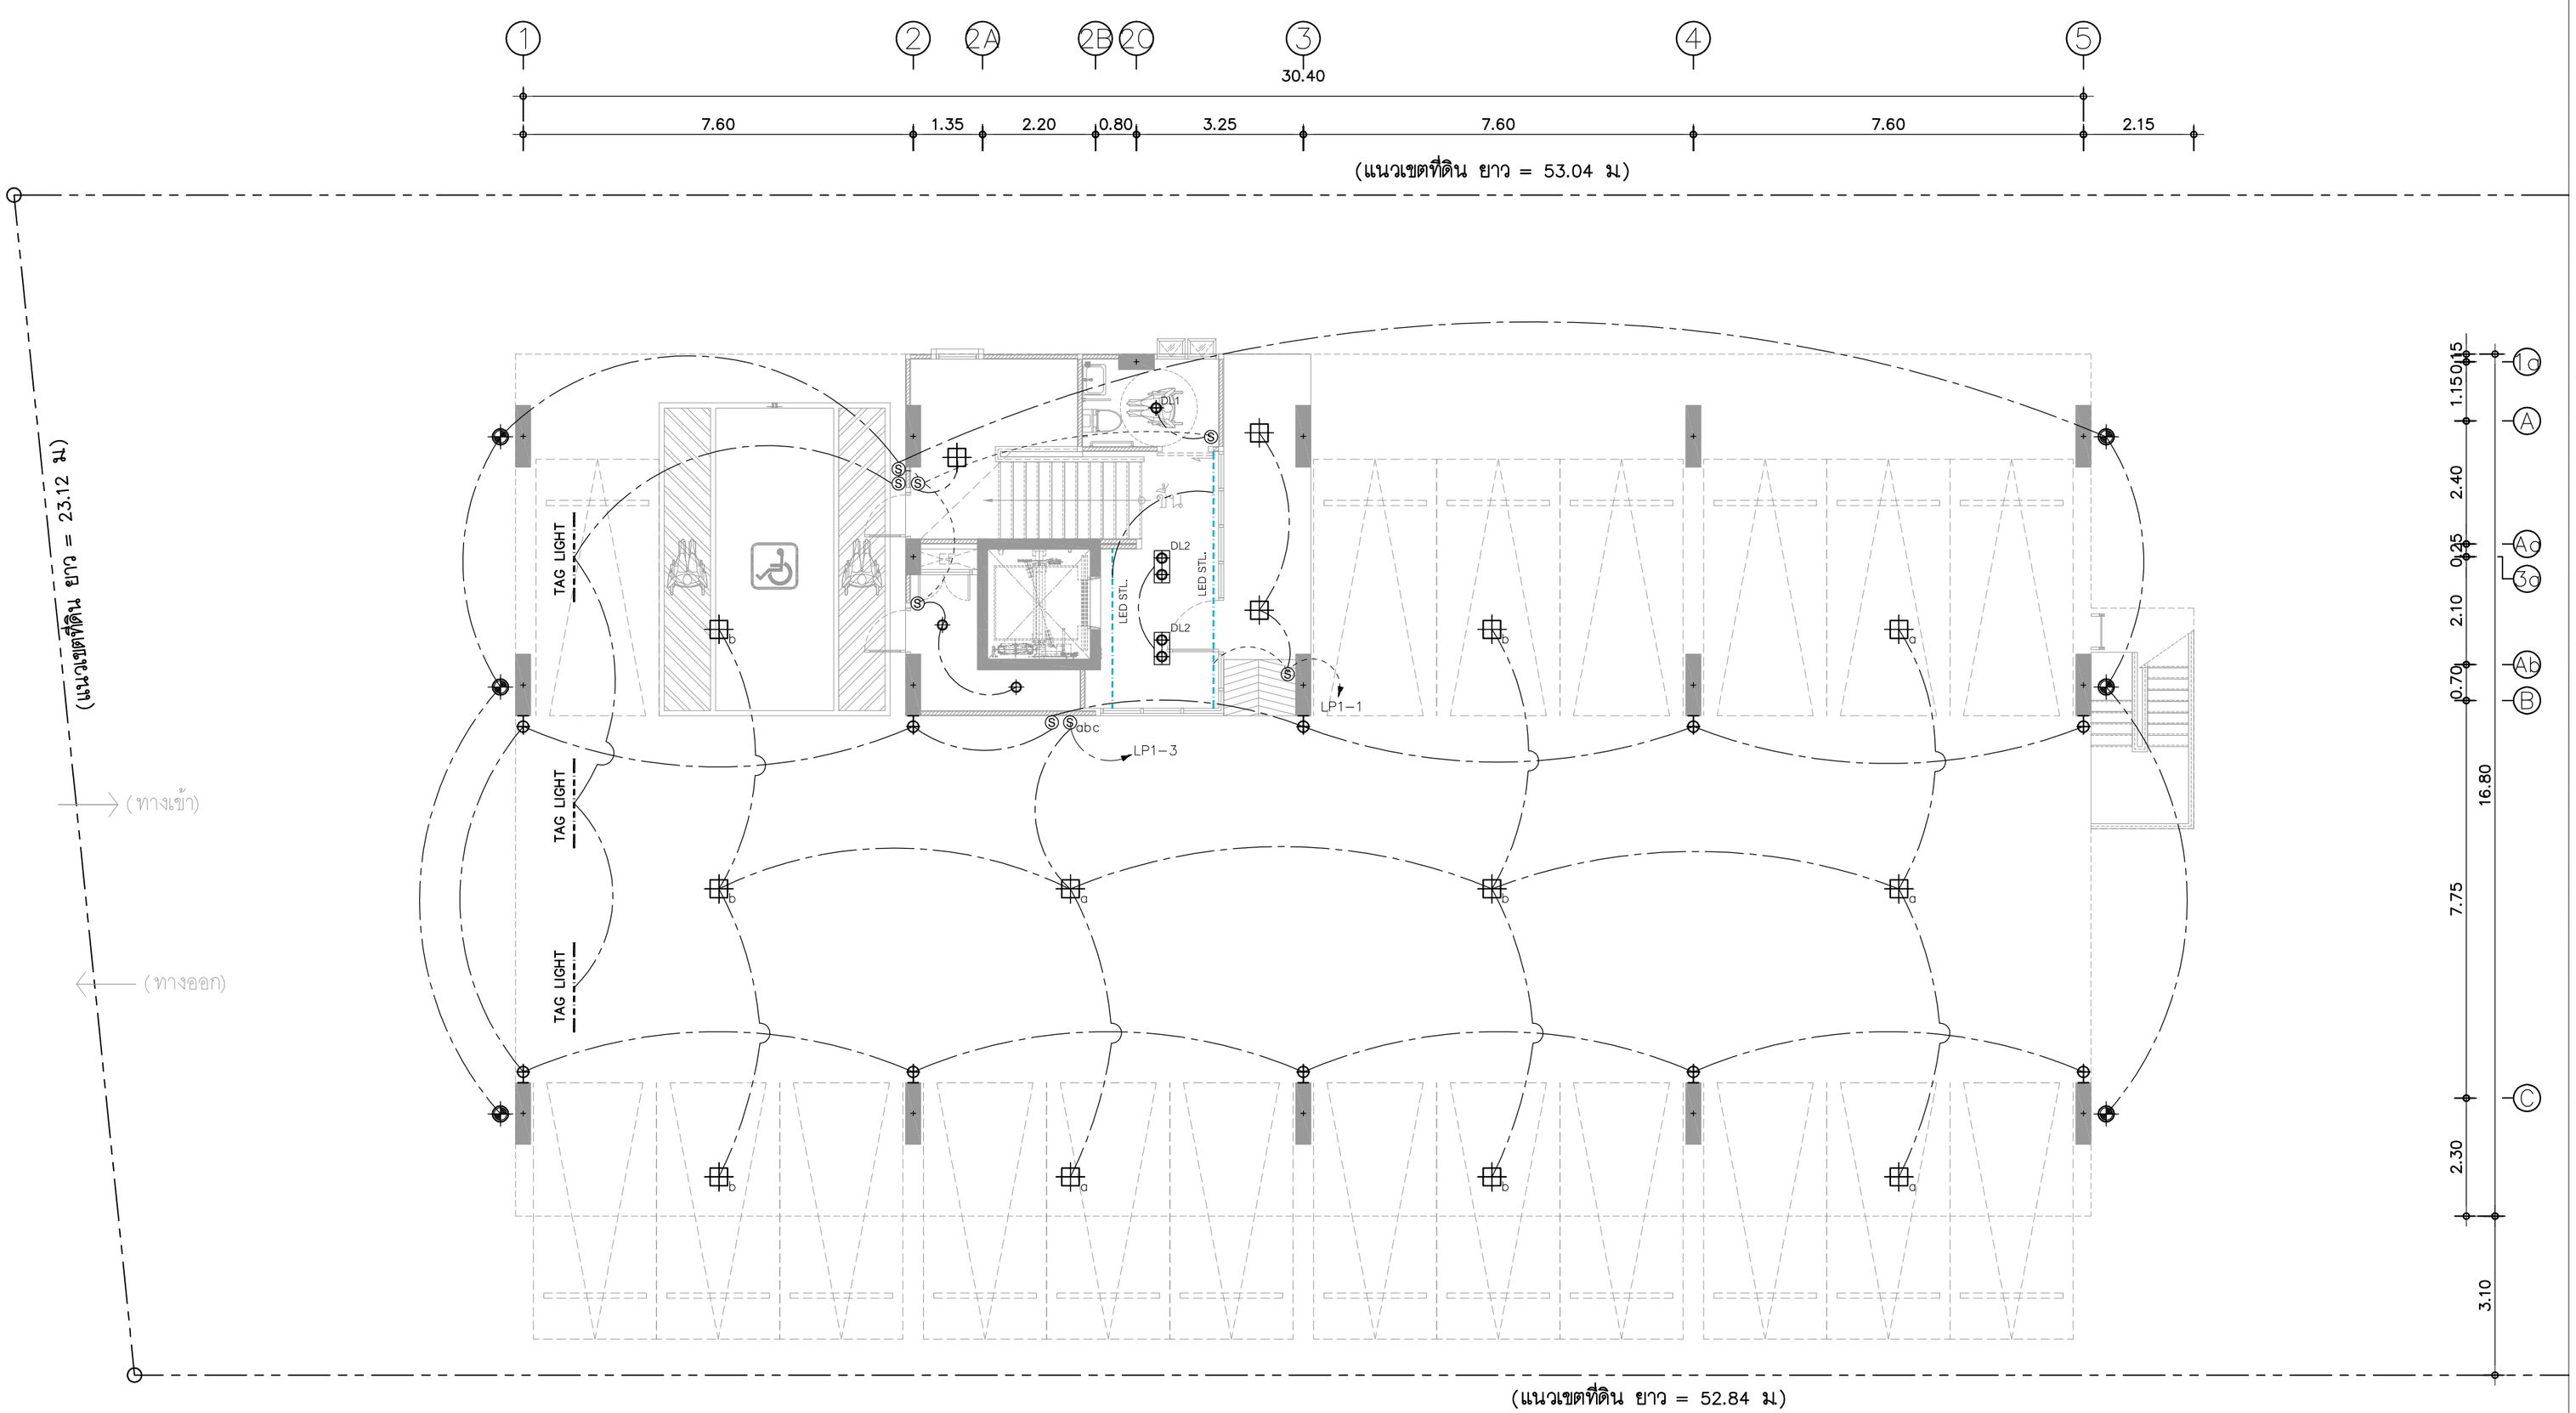

ผังไฟฟ้าและสวิตช์ชั้น 1

SCALE 1:100

PROJECT NUMBER : VC2023-024

PROJECT

MACHI RESIDENCES

อาคารพักอาศัยรวม ค.ส.ล 7 ชั้น

OWNER

บริษัท ฤทธิกร ลิฟวิ่ง จำกัด

ARCHITECT :

อัคคะภัทร์ จิระอารียบุตร ส-สถ.3040

403 ซ.พัฒนาการ 50 พัฒนาการ

กรุงเทพมหานคร 10250

INTERIOR DESIGNER :

-

STRUCTURAL ENGINEER :

นายพงษ์ธวิทย์ คทาวุธเจริญกุล ลย.12291

ELECTRICAL ENGINEER :

นายภาคภูมิ คำพิทูรย์ ลฟก.5587

MECHANICAL ENGINEER :

SANITARY ENGINEER :

นส.อรวรรณ พลตรี ลส.134

DRAWING TITLE

ผังไฟฟ้าและสวิตช์ชั้น 1

DRAWING FOR CONSTRUCTION


DRAW BY :	CHECKER :	REVISION :
Weerayuth L.	Akapatr C.	-

SCALE :	DRAWING NO.
1 : 100	EE-06
DATE : 20-10-2024	
FILE NAME :	JOB NO.

REVISION	DESCRIPTION

GERNERAL NOTE
DO NOT SCALE DRAWING ALL MEASUREMENT MUST BE
CHECKED AT THE SIDE BY THE CONTRACTOR
ALL DESIGN AND DRAWINGS ARE THE PROPERTY OF
MARCHTEN CO.,LTD
AND NOT BE USED WITH OUT THEIR WRITTEN PERMISSION

MARCHTEN
ARCHITECTURE / INTERIOR
บริษัท มาร์ชเทน จำกัด
403 ซ.พัฒนาการ 50 สวนหลวง กรุงเทพมหานคร 10250

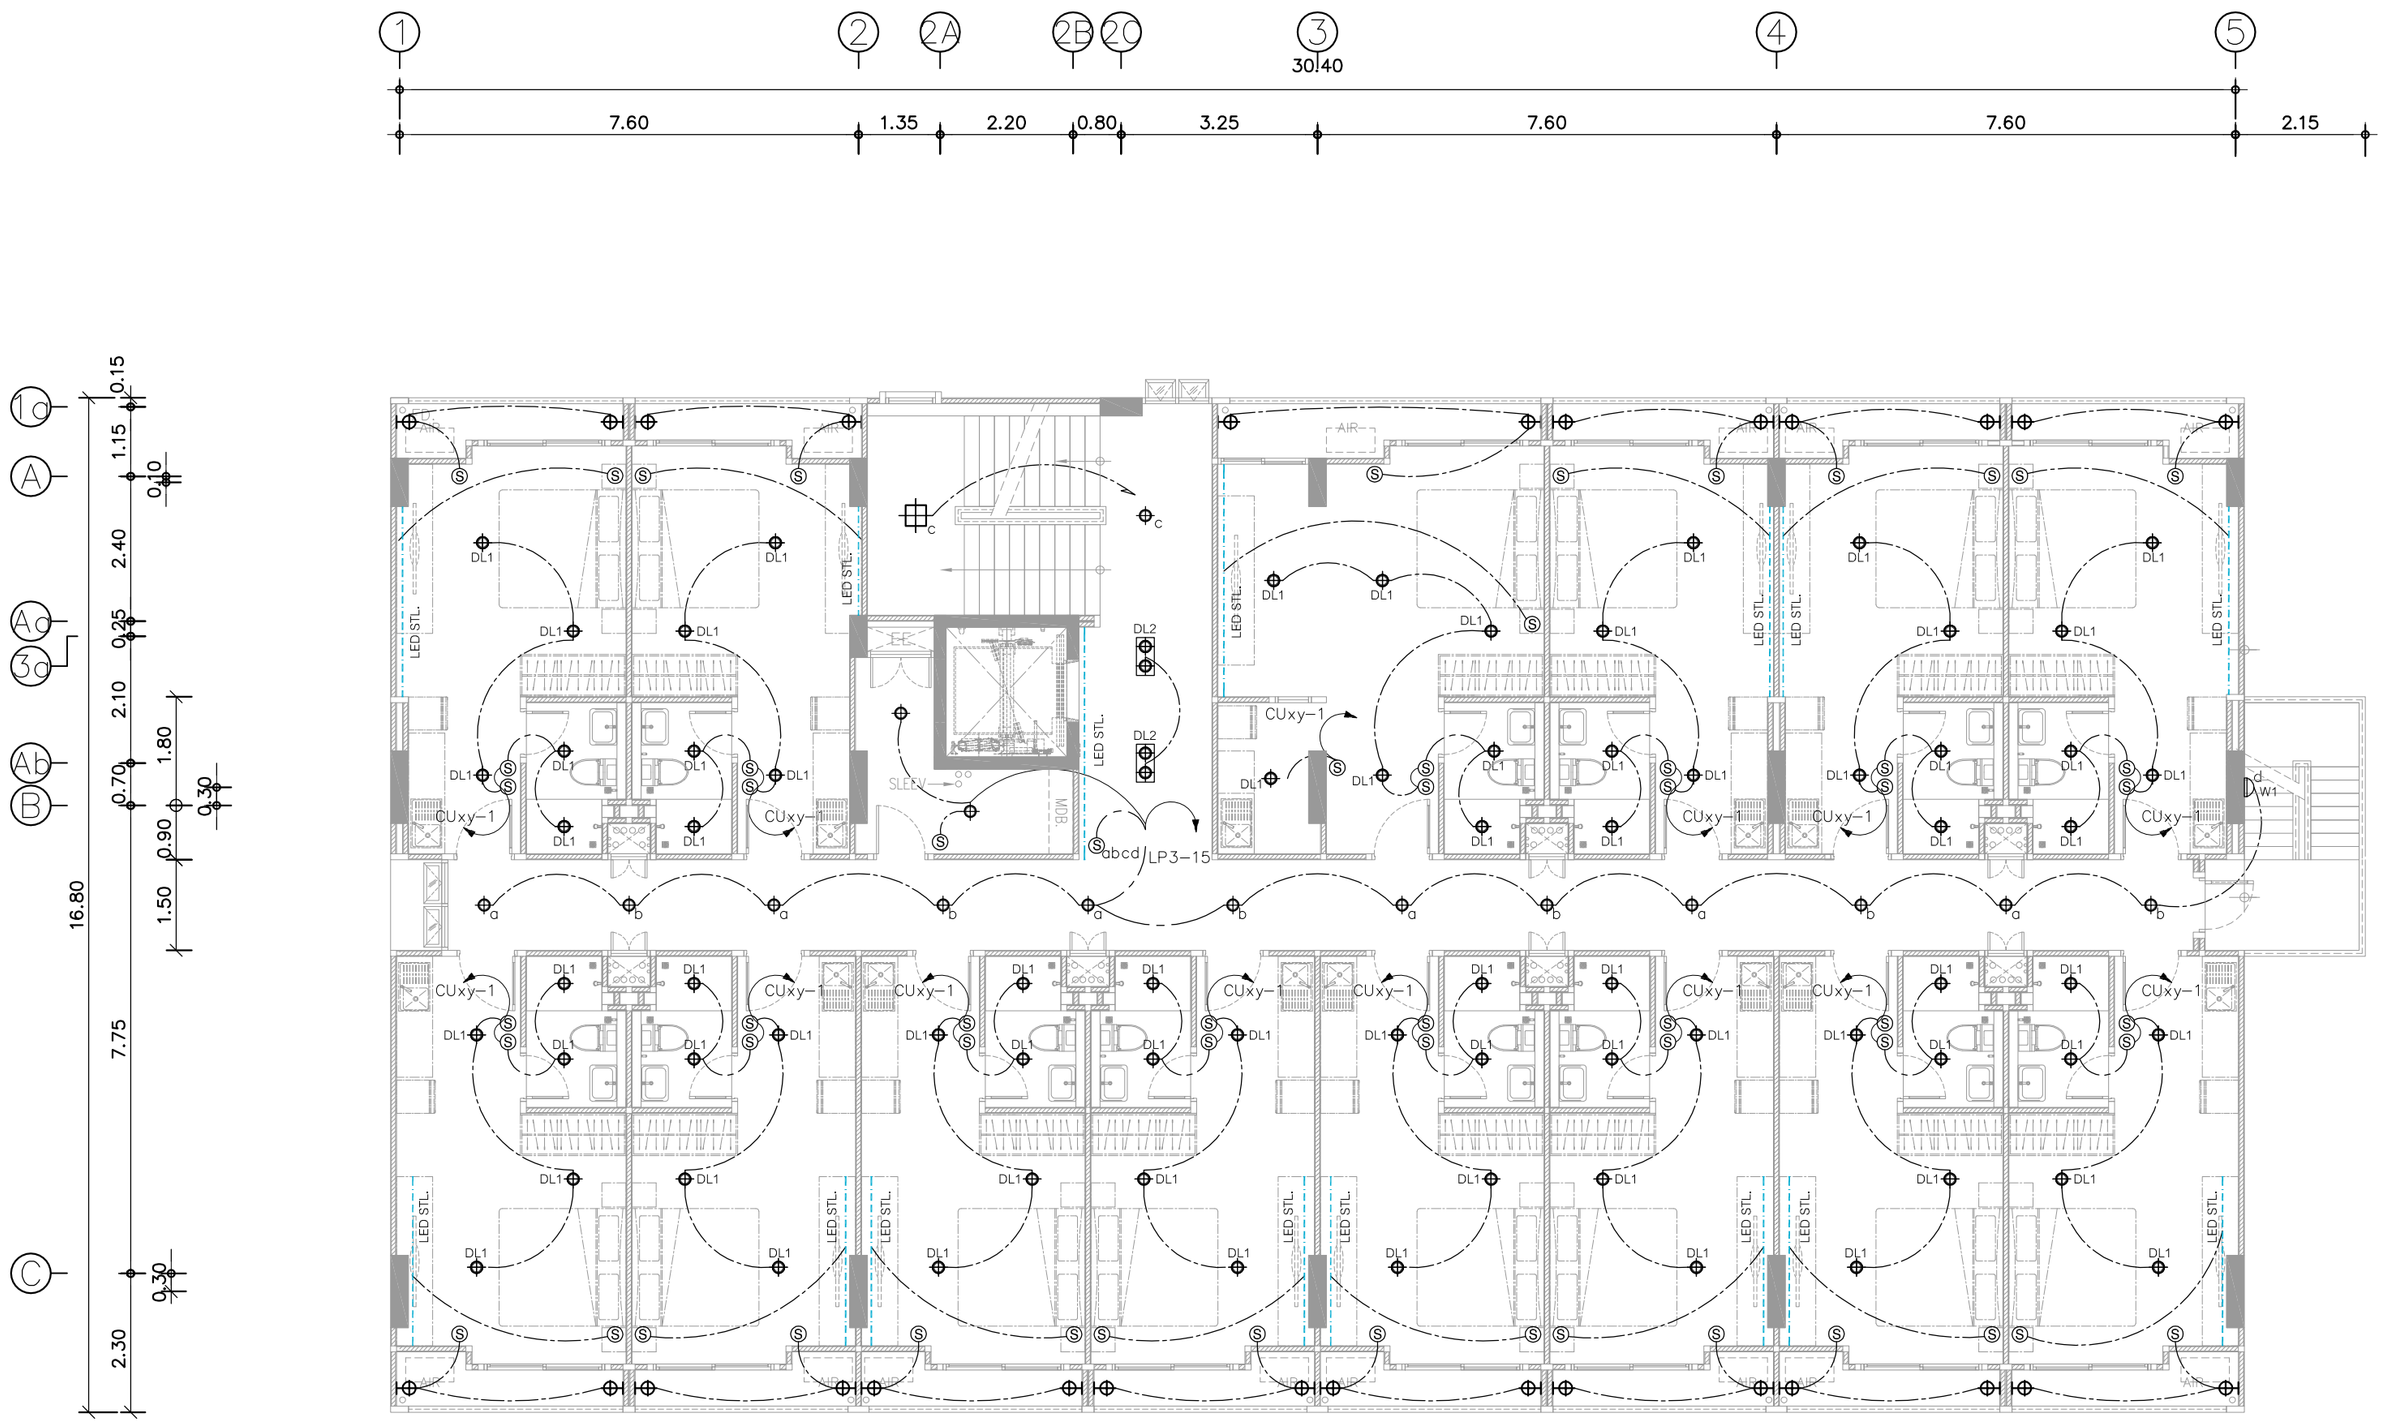

ผังไฟฟ้าและสวิตช์ชั้น 2

SCALE 1:100

PROJECT NUMBER : VC2023-024

PROJECT

MACHI RESIDENCES

อาคารพักอาศัยรวม ค.ส.ล 7 ชั้น

OWNER

บริษัท ฤทธิกร ลิฟวิ่ง จำกัด

ARCHITECT :

อัคคะภัทร์ จิระอารีย์บุตร ส-สถ.3040

403 ซ.พัฒนาการ 50 พัฒนาการ

กรุงเทพมหานคร 10250

INTERIOR DESIGNER :

-

STRUCTURAL ENGINEER :

นายพงษ์ธวิทย์ คทาวุธเจริญกุล ลย.12291

ELECTRICAL ENGINEER :

นายภาคภูมิ คำพิทูรย์ ลฟก.5587

MECHANICAL ENGINEER :

SANITARY ENGINEER :

นส.อรวรรณ พลตรี ลส.134

DRAWING TITLE

ผังไฟฟ้าและสวิตช์ชั้น 2

DRAWING FOR CONSTRUCTION


DRAW BY :	CHECKER :	REVISION :
Weerayuth L.	Akapatr C.	-

SCALE :	DRAWING NO.
1 : 100	EE-07
DATE : 20-10-2024	
FILE NAME :	JOB NO.

REVISION	DESCRIPTION

GERNERAL NOTE
DO NOT SCALE DRAWING ALL MEASUREMENT MUST BE
CHECKED AT THE SIDE BY THE CONTRACTOR
ALL DESIGN AND DRAWINGS ARE THE PROPERTY OF
MARCHTEN CO.,LTD
AND NOT BE USED WITH OUT THEIR WRITTEN PERMISSION

MARCHTEN
ARCHITECTURE / INTERIOR
บริษัท มาร์ชเทน จำกัด
403 ซ.พัฒนาการ 50 สวนหลวง กรุงเทพมหานคร 10250

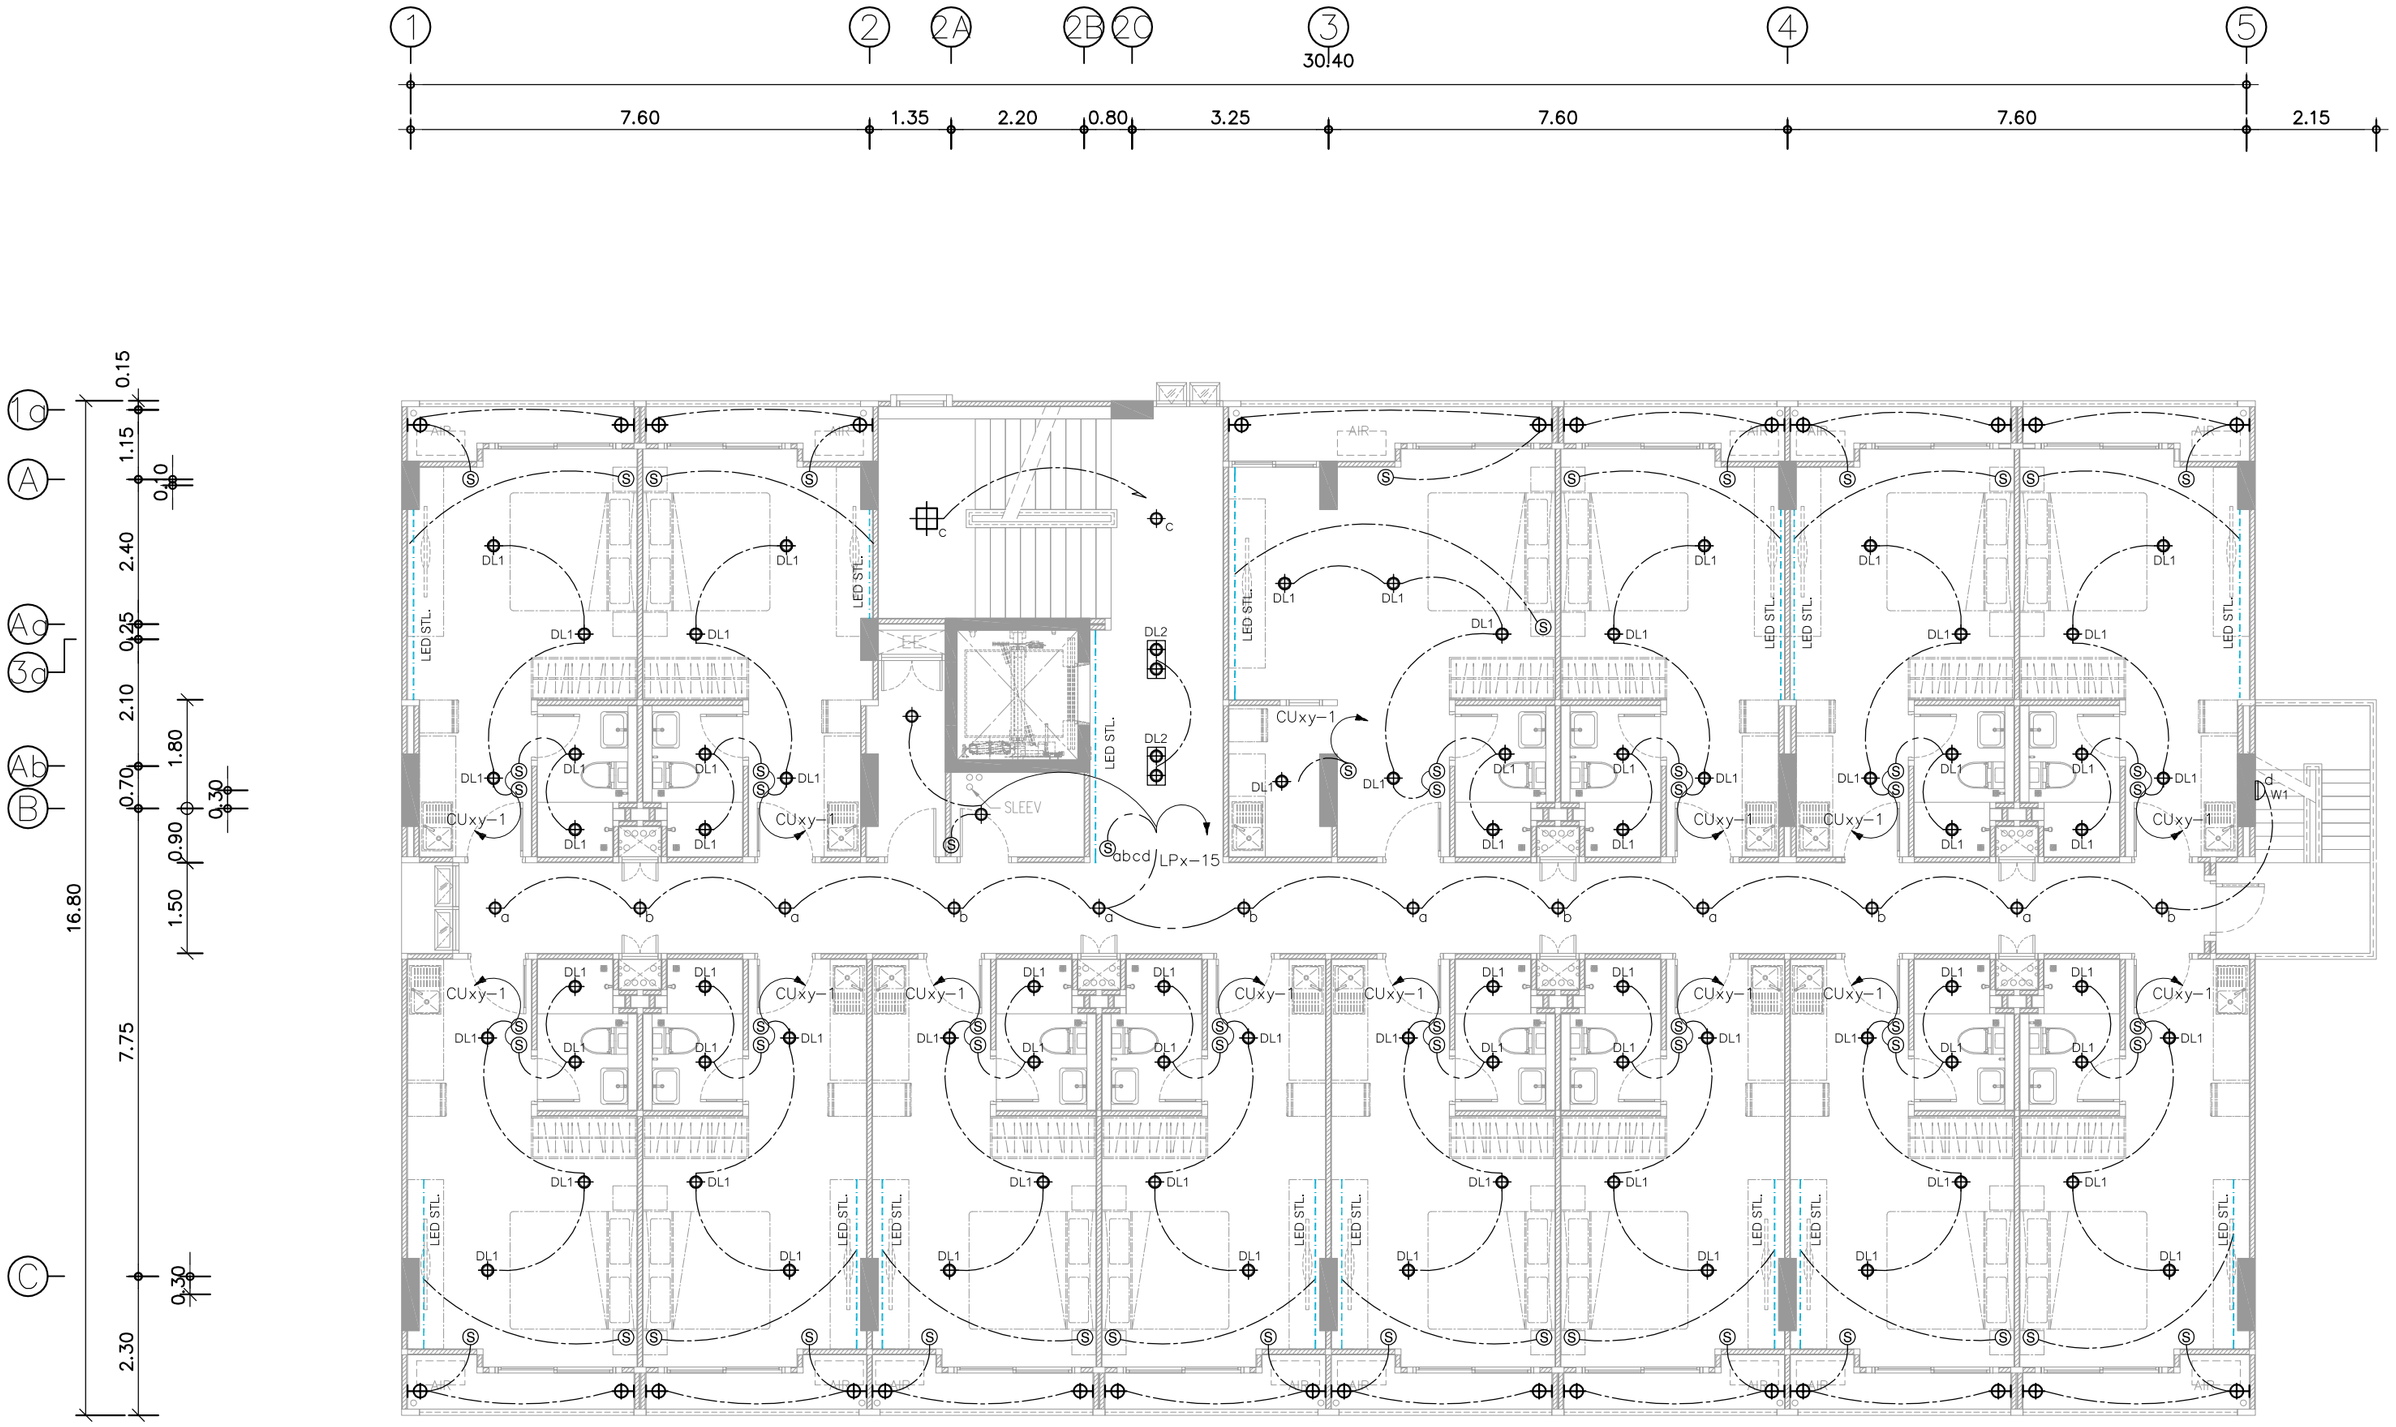

ผังไฟฟ้าและสวิตช์ชั้น 3-5

SCALE 1:100

PROJECT NUMBER : VC2023-024

PROJECT

MACHI RESIDENCES

อาคารพักอาศัยรวม ค.ส.ล 7 ชั้น

OWNER

บริษัท ฤทธิกร ลิฟวิ่ง จำกัด

ARCHITECT :

อัคคะภัทร์ จิระอารียบุตร ส-สถ.3040

403 ซ.พัฒนาการ 50 พัฒนาการ

กรุงเทพมหานคร 10250

INTERIOR DESIGNER :

-

STRUCTURAL ENGINEER :

นายพงษ์ธวิทย์ คทาวุธเจริญกุล ลย.12291

ELECTRICAL ENGINEER :

นายภาคภูมิ คำพิทูรย์ ลฟก.5587

MECHANICAL ENGINEER :

SANITARY ENGINEER :

นส.อรวรรณ พลตรี ลส.134

DRAWING TITLE

ผังไฟฟ้าและสวิตช์ชั้น 3-5

DRAWING FOR CONSTRUCTION

DRAW BY :	CHECKER :	REVISION :
Weerayuth L.	Akapatr C.	-

SCALE :	DRAWING NO.
1 : 100	EE-08
DATE : 20-10-2024	
FILE NAME :	JOB NO.

REVISION	DESCRIPTION

GERNERAL NOTE


DO NOT SCALE DRAWING ALL MEASUREMENT MUST BE **CHECKED AT THE SIDE BY THE CONTRACTOR**

ALL DESIGN AND DRAWINGS ARE THE PROPERTY OF MARCHTEN CO.,LTD **AND NOT BE USED WITH OUT THEIR WRITTEN PERMISSION**

MARCHTEN

ARCHITECTURE / INTERIOR

บริษัท มาร์ชเทน จำกัด
403 ซ.พัฒนาการ 50 สวนหลวง กรุงเทพมหานคร 10250

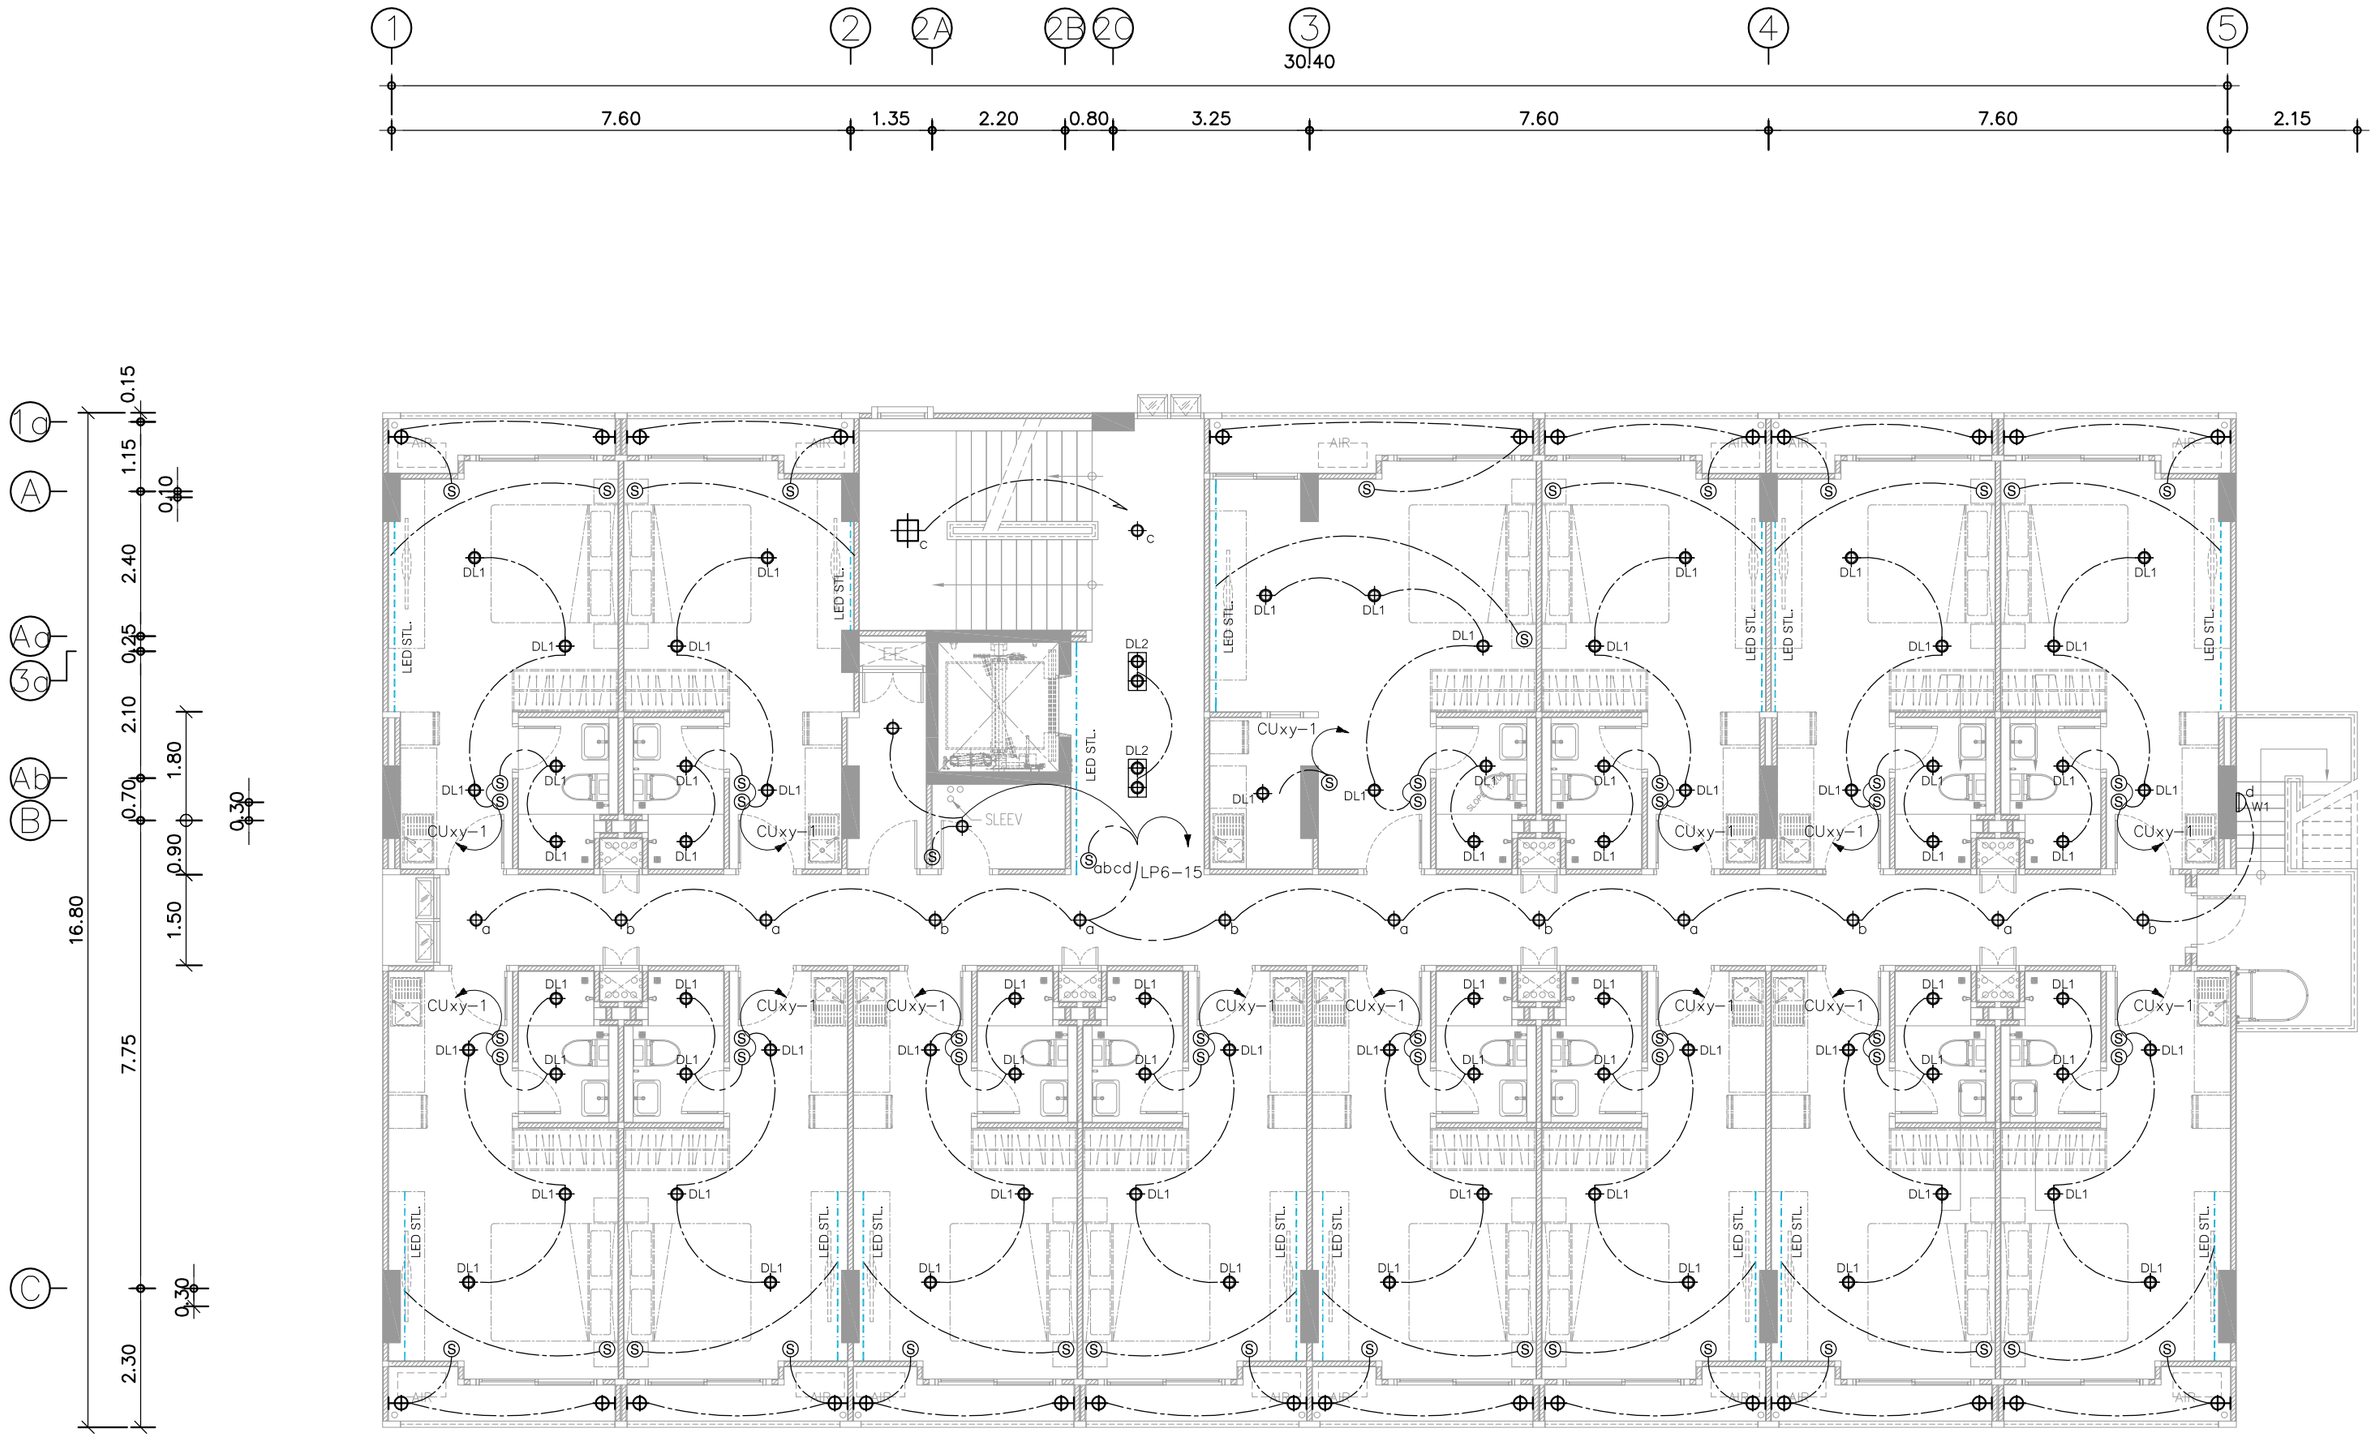

ผังไฟฟ้าและสวิตช์ชั้น 6

SCALE 1:100

PROJECT NUMBER : VC2023-024

PROJECT

MACHI RESIDENCES

อาคารพักอาศัยรวม ค.ส.ล 7 ชั้น

OWNER

บริษัท ฤทธิกร ลิฟวิ่ง จำกัด

ARCHITECT :

อัคคะภัทร์ จิระอารียบุตร ส-สถ.3040

403 ซ.พัฒนาการ 50 พัฒนาการ

กรุงเทพมหานคร 10250

INTERIOR DESIGNER :

-

STRUCTURAL ENGINEER :

นายพงษ์ธวิทย์ คทาวุธเจริญกุล ลย.12291

ELECTRICAL ENGINEER :

นายภาคภูมิ คำพิทูรย์ ลฟก.5587

MECHANICAL ENGINEER :

SANITARY ENGINEER :

นส.อรวรรณ พลตรี ลส.134

DRAWING TITLE

ผังไฟฟ้าและสวิตช์ชั้น 6

DRAWING FOR CONSTRUCTION

DRAW BY :	CHECKER :	REVISION :
Weerayuth L.	Akapatr C.	-

SCALE :	DRAWING NO.
1 : 100	EE-09
DATE : 20-10-2024	
FILE NAME :	JOB NO.

REVISION	DESCRIPTION

GERNERAL NOTE

DO NOT SCALE DRAWING ALL MEASUREMENT MUST BE **CHECKED AT THE SIDE BY THE CONTRACTOR**


ALL DESIGN AND DRAWINGS ARE THE PROPERTY OF MARCHTEN CO.,LTD **AND NOT BE USED WITH OUT THEIR WRITTEN PERMISSION**

MARCHTEN

ARCHITECTURE / INTERIOR

บริษัท มาร์ชเทน จำกัด

403 ซ.พัฒนาการ 50 สวนหลวง กรุงเทพมหานคร 10250

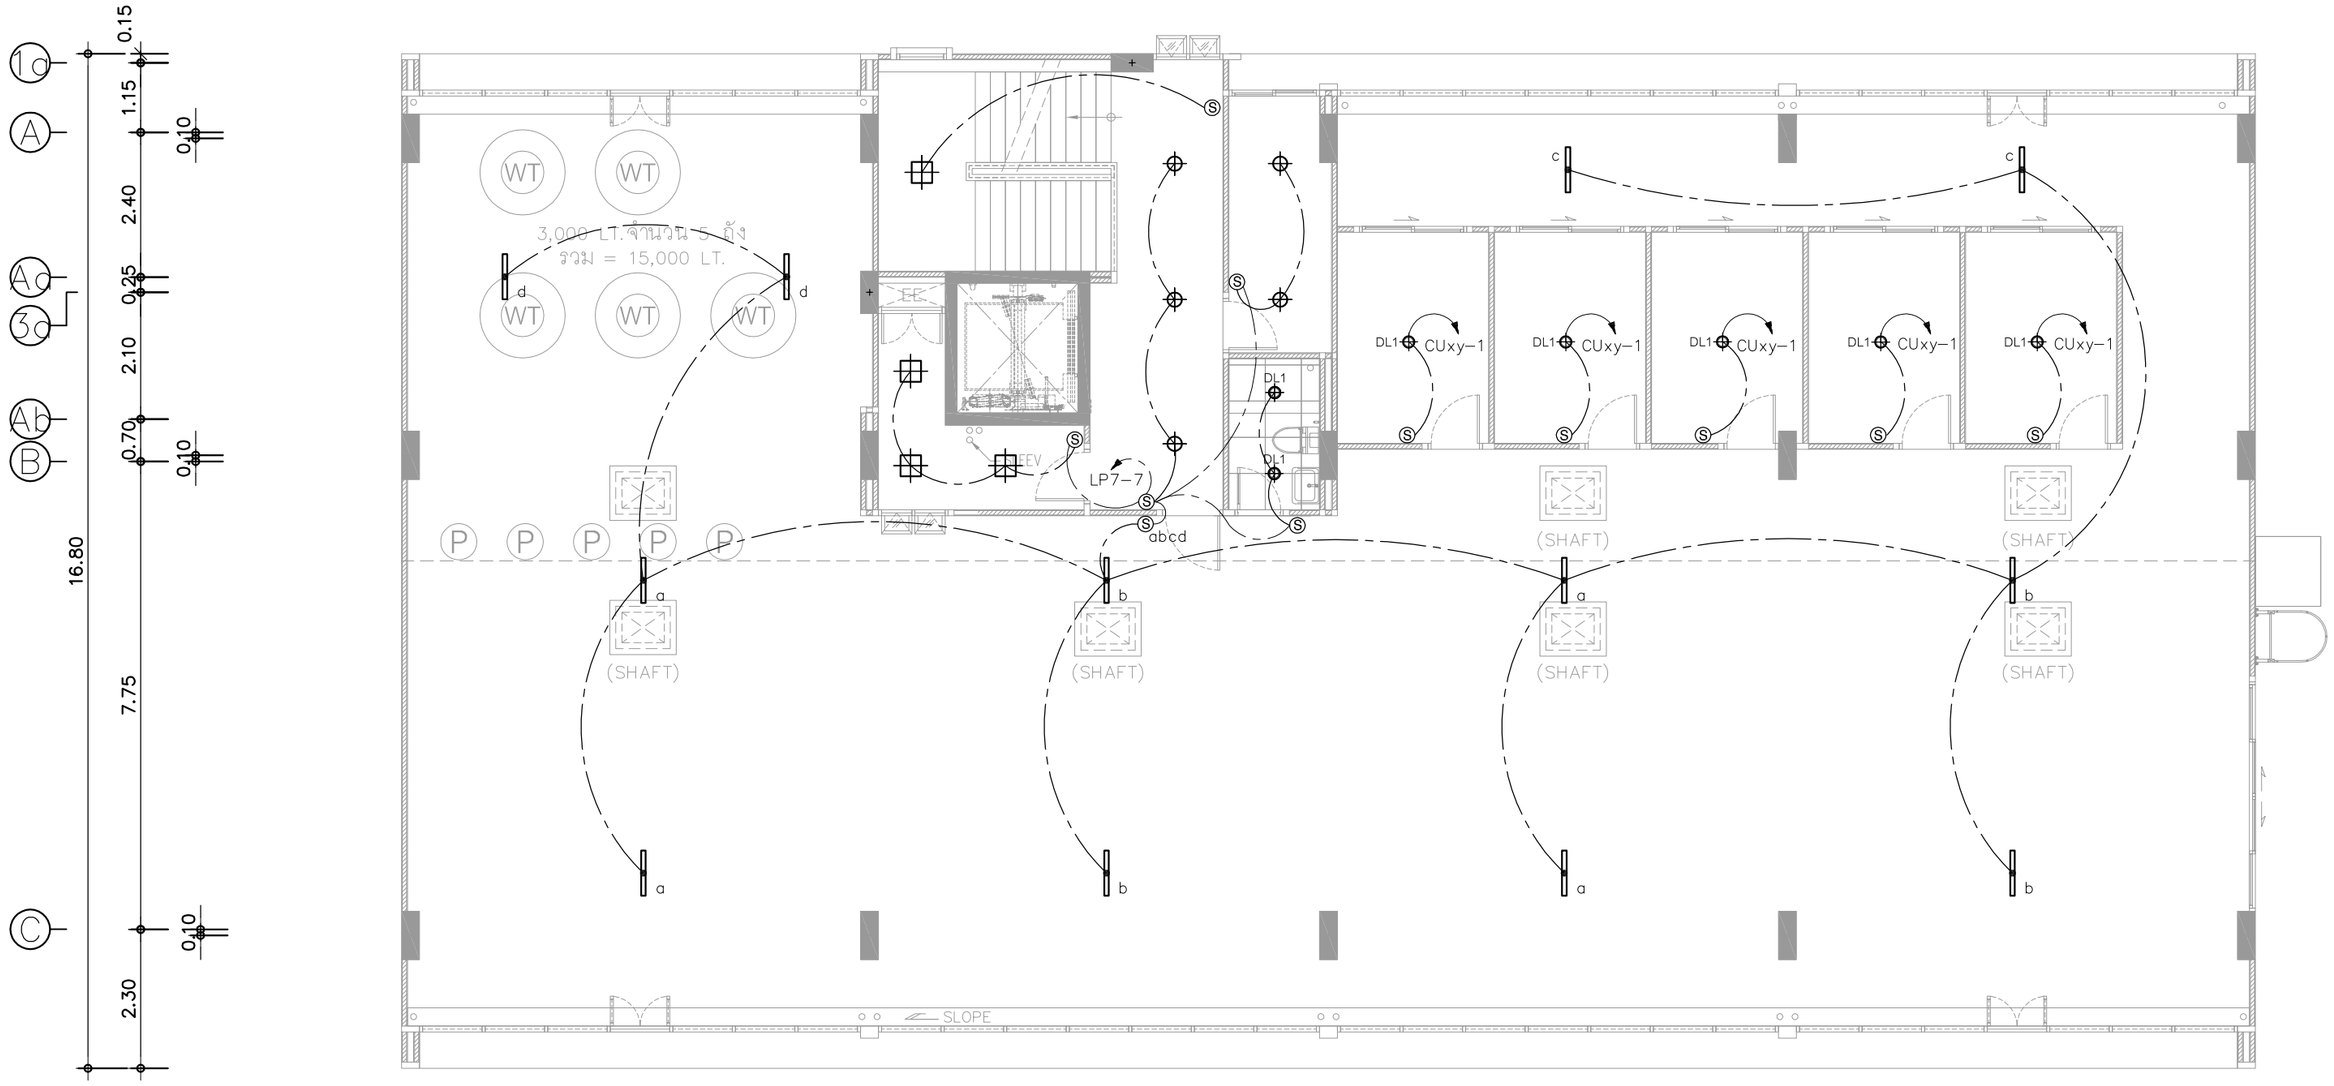

ผังไฟฟ้าและสวิตช์ชั้น 7 ห้องใต้หลังคา

SCALE 1:100

PROJECT NUMBER : VC2023-024

PROJECT

MACHI RESIDENCES

อาคารพักอาศัยรวม ค.ส.ล 7 ชั้น

OWNER

บริษัท ฤทธิกร ลิฟวิ่ง จำกัด

ARCHITECT :

อัคคะภัทร์ จิระอารียบุตร ส-สถ.3040

403 ซ.พัฒนาการ 50 พัฒนาการ

กรุงเทพมหานคร 10250

INTERIOR DESIGNER :

-

STRUCTURAL ENGINEER :

นายพงษ์ธวิทย์ คทาวุธเจริญกุล ลย.12291

ELECTRICAL ENGINEER :

นายภาคภูมิ คำพิทูรย์ ลฟก.5587

MECHANICAL ENGINEER :

SANITARY ENGINEER :

นส.อรวรรณ พลตรี ลส.134

DRAWING TITLE

ผังไฟฟ้าและสวิตช์ชั้น 7 ห้องใต้หลังคา

DRAWING FOR CONSTRUCTION

DRAW BY :	CHECKER :	REVISION :
Weerayuth L.	Akapatr C.	–

SCALE :	DRAWING NO.
1 : 100	EE-10
DATE : 20-10-2024	
FILE NAME :	JOB NO.

REVISION	DESCRIPTION

GERNERAL NOTE


DO NOT SCALE DRAWING ALL MEASUREMENT MUST BE **CHECKED AT THE SIDE BY THE CONTRACTOR**

ALL DESIGN AND DRAWINGS ARE THE PROPERTY OF MARCHTEN CO.,LTD **AND NOT BE USED WITH OUT THEIR WRITTEN PERMISSION**

MARCHTEN

ARCHITECTURE / INTERIOR

บริษัท มาร์ชเทน จำกัด
403 ซ.พัฒนาการ 50 สวนหลวง กรุงเทพมหานคร 10250

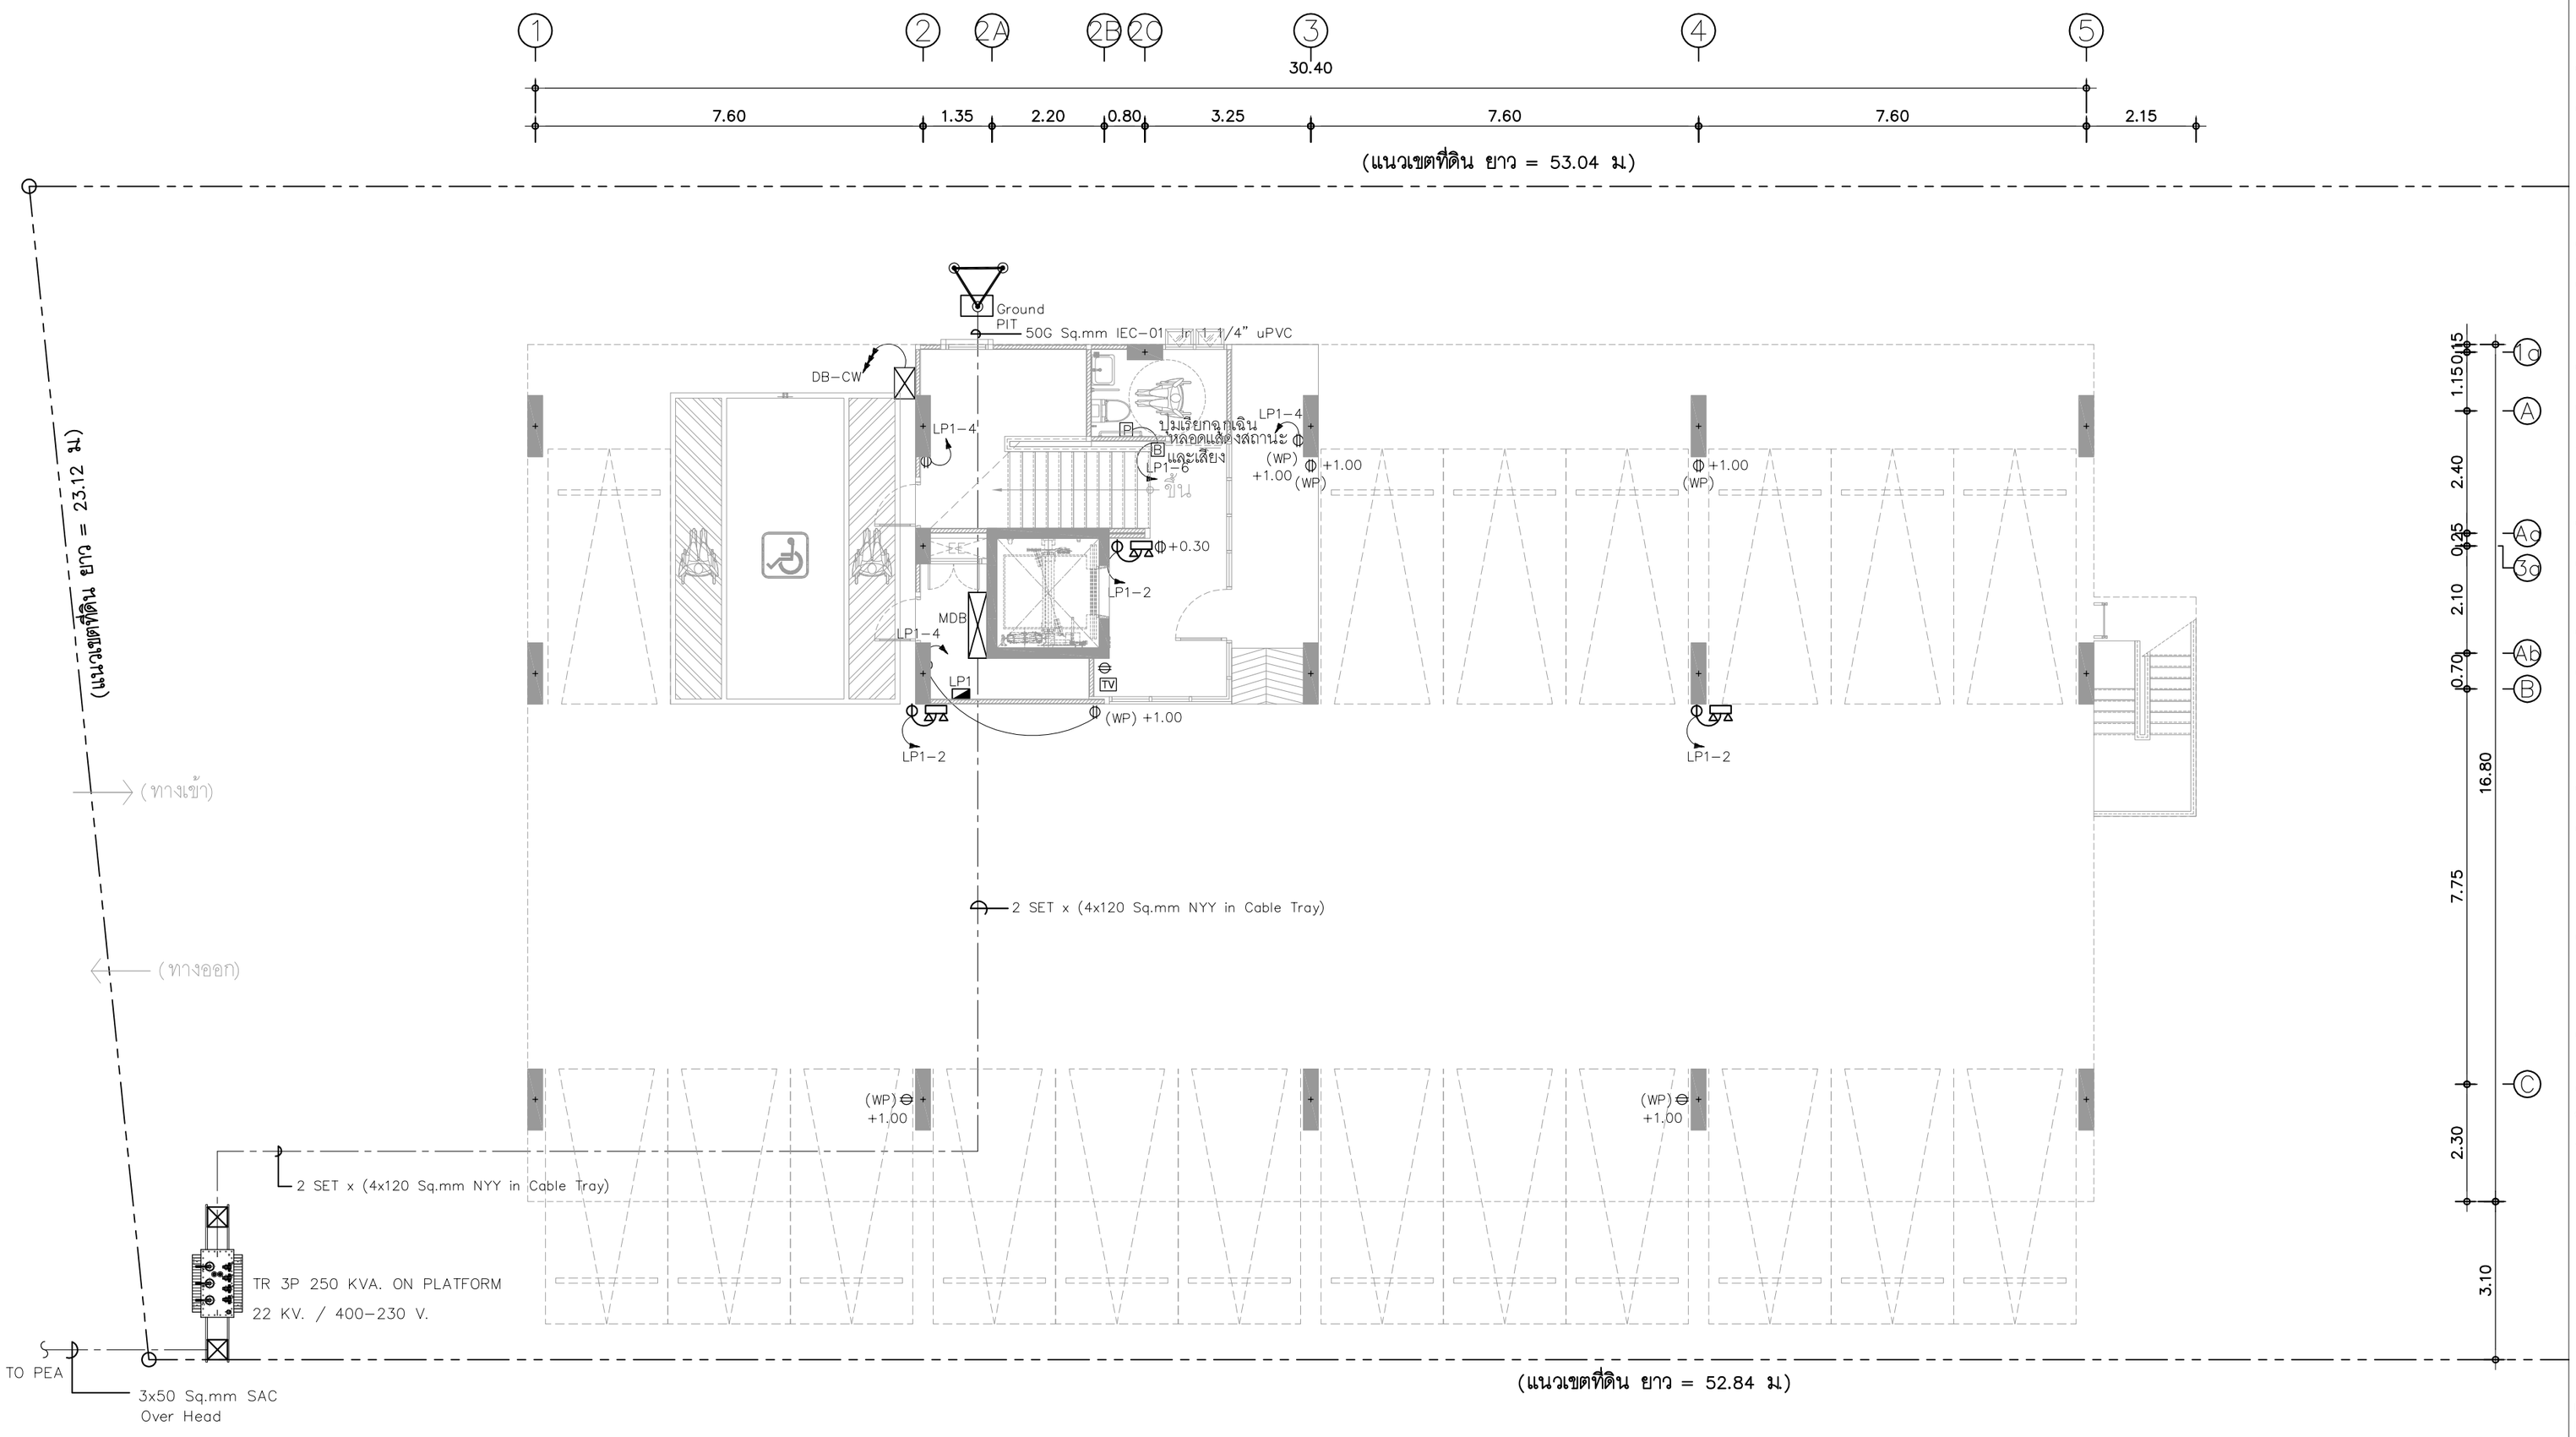

ผังปลั๊กไฟชั้น 1

SCALE 1:100

PROJECT NUMBER : VC2023-024

PROJECT

MACHI RESIDENCES

อาคารพักอาศัยรวม ค.ส.ล 7 ชั้น

OWNER

บริษัท ฤทธิกร ลิฟวิ่ง จำกัด

ARCHITECT :

อัคคะภัทร์ จิระอารียบุตร ส-สถ.3040

403 ซ.พัฒนาการ 50 พัฒนาการ

กรุงเทพมหานคร 10250

INTERIOR DESIGNER :

-

STRUCTURAL ENGINEER :

นายพงษ์ธวิทย์ คทาวุธเจริญกุล ลย.12291

ELECTRICAL ENGINEER :

นายภาคภูมิ คำพิทูรย์ ลพก.5587

MECHANICAL ENGINEER :

SANITARY ENGINEER :

นส.อรวรรณ พลตรี ลส.134

DRAWING TITLE

ผังปลั๊กไฟชั้น 1

DRAWING FOR CONSTRUCTION

DRAW BY :	CHECKER :	REVISION :
Weerayuth L.	Akapatr C.	-

SCALE :	DRAWING NO.
1 : 100	EE-11
DATE : 20-10-2024	
FILE NAME :	JOB NO.

REVISION	DESCRIPTION

GERNERAL NOTE

DO NOT SCALE DRAWING ALL MEASUREMENT MUST BE **CHECKED AT THE SIDE BY THE CONTRACTOR**


ALL DESIGN AND DRAWINGS ARE THE PROPERTY OF MARCHTEN CO.,LTD **AND NOT BE USED WITH OUT THEIR WRITTEN PERMISSION**

MARCHTEN

ARCHITECTURE / INTERIOR

บริษัท มาร์ชเทน จำกัด

403 ซ.พัฒนาการ 50 สวนหลวง กรุงเทพมหานคร 10250

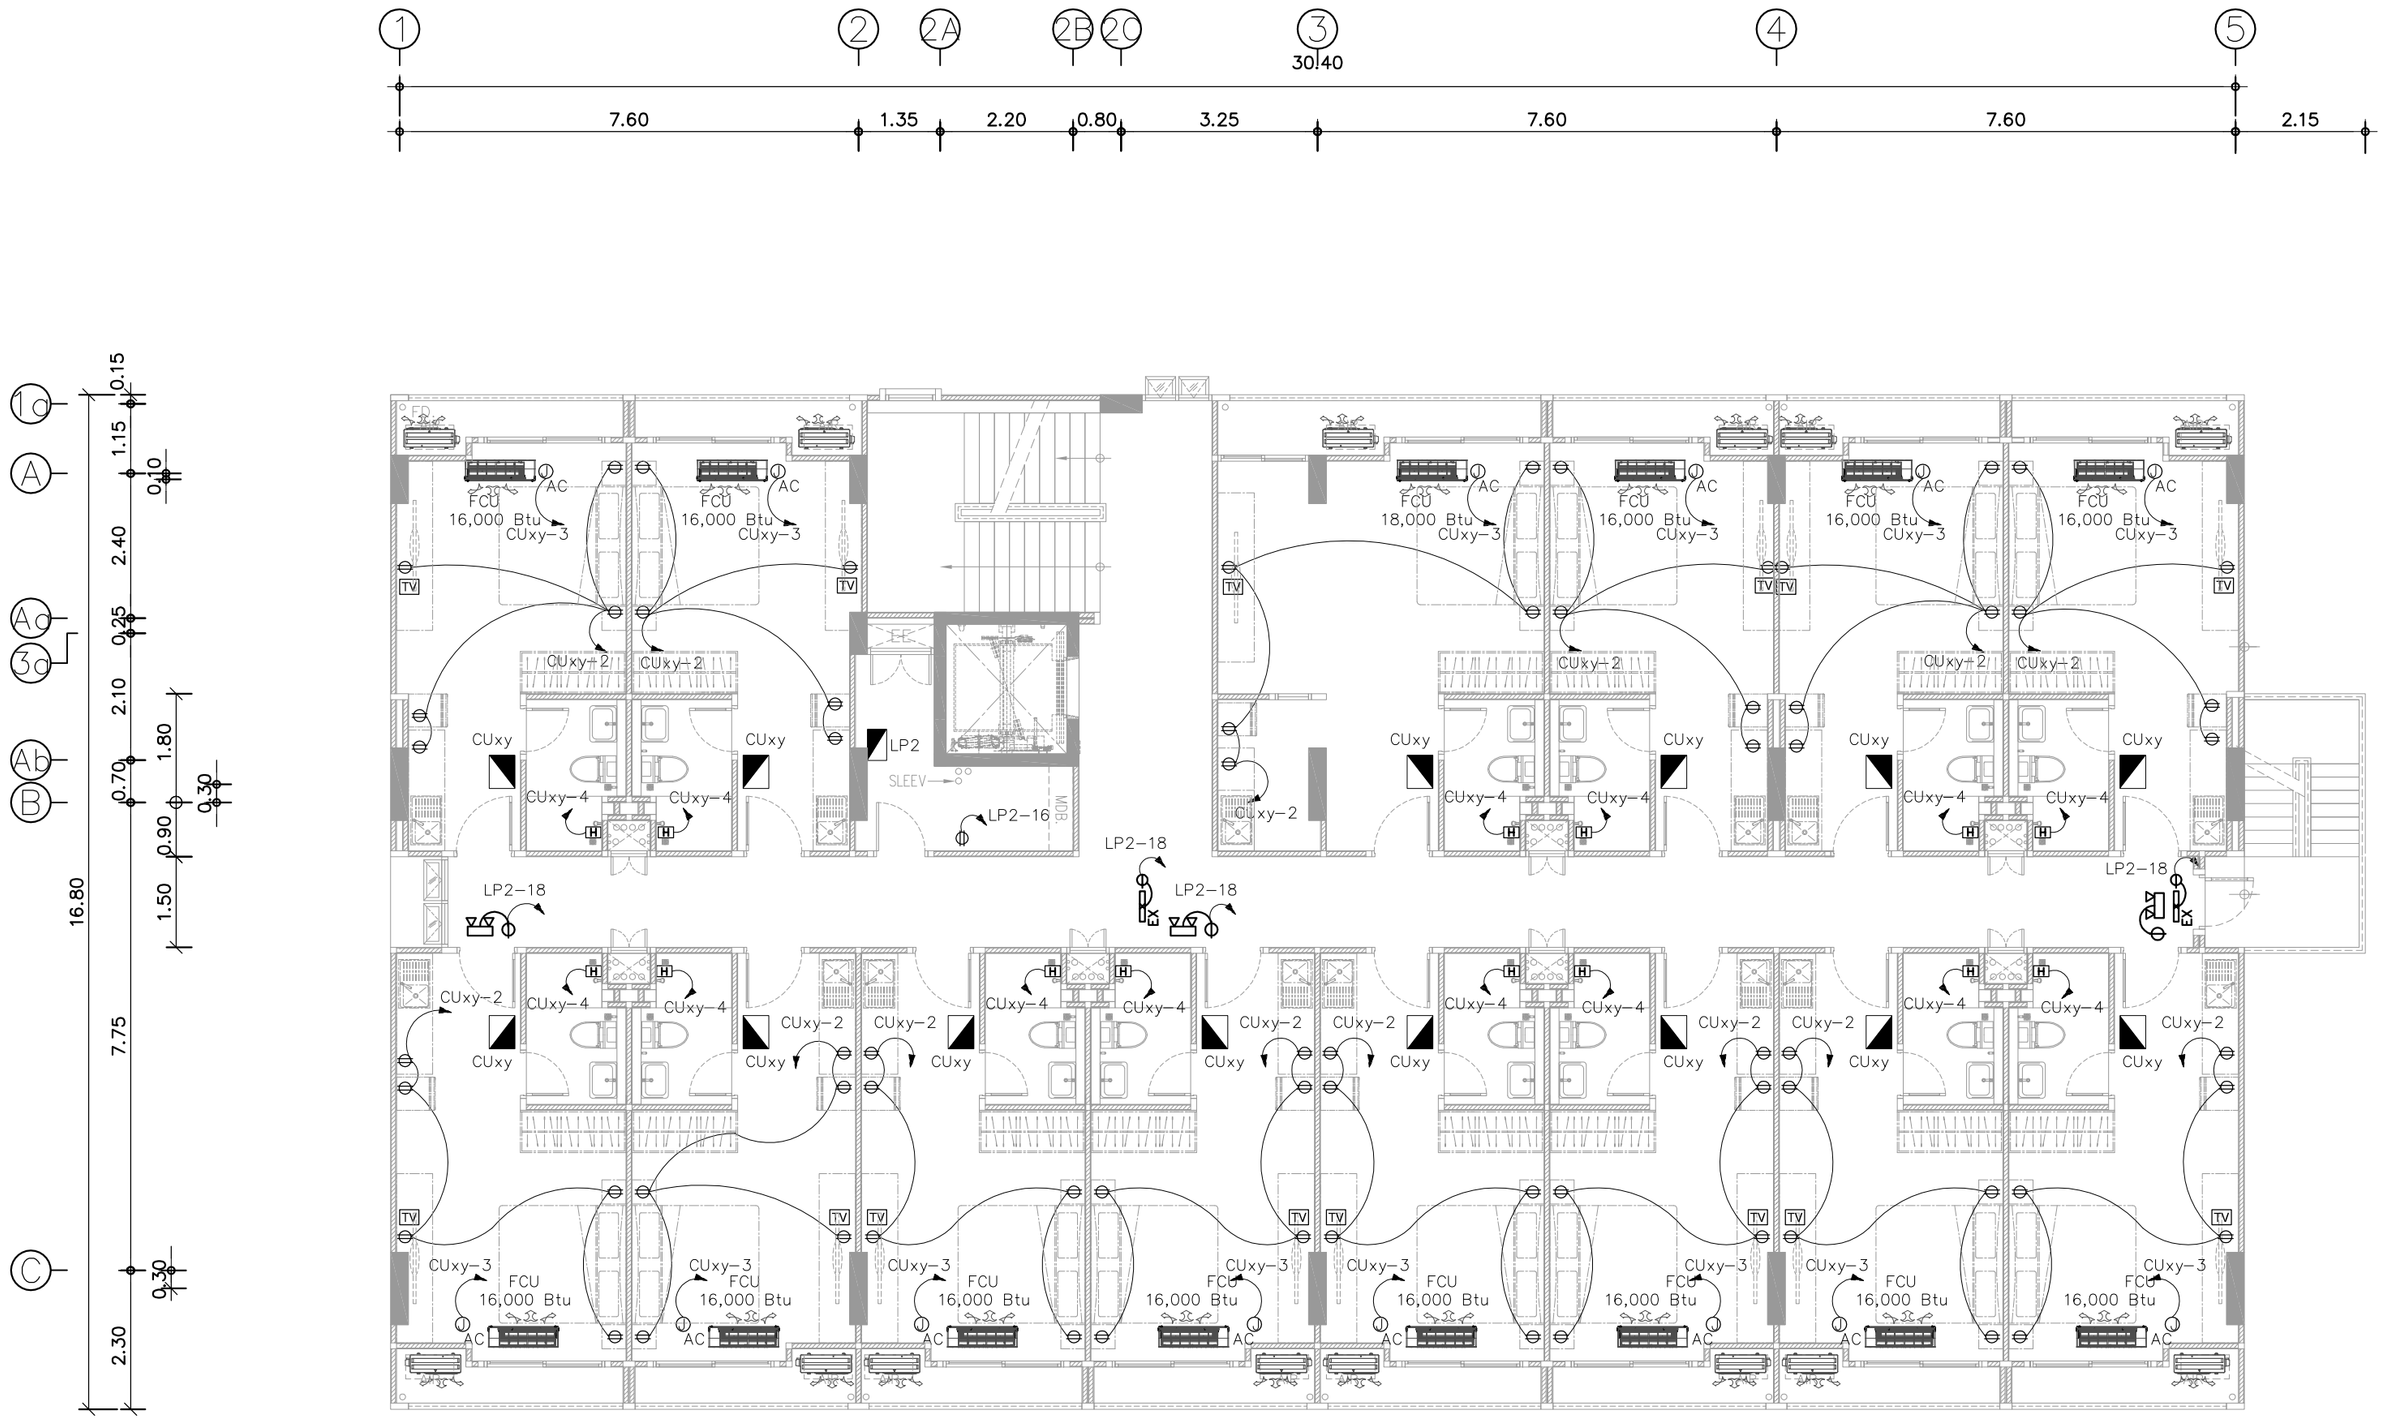

ผังปลั๊กไฟชั้น 2

SCALE 1:100

PROJECT NUMBER : VC2023-024

PROJECT

MACHI RESIDENCES

อาคารพักอาศัยรวม ค.ส.ล 7 ชั้น

OWNER

บริษัท ฤทธิกร ลิฟวิ่ง จำกัด

ARCHITECT :

อัคคะภัทร์ จิระอารีย์บุตร ส-สถ.3040

403 ซ.พัฒนาการ 50 พัฒนาการ

กรุงเทพมหานคร 10250

INTERIOR DESIGNER :

-

STRUCTURAL ENGINEER :

นายพงษ์ธวิทย์ คทาวุธเจริญกุล ลย.12291

ELECTRICAL ENGINEER :

นายภาคภูมิ คำพิทูรย์ ลฟก.5587

MECHANICAL ENGINEER :

SANITARY ENGINEER :

พล.อรวรรณ พลตรี ลส.134

DRAWING TITLE

ผังปลั๊กไฟชั้น 2

DRAWING FOR CONSTRUCTION

DRAW BY :	CHECKER :	REVISION :
Weerayuth L.	Akapatr C.	-

SCALE :	DRAWING NO.
1 : 100	EE-12
DATE : 20-10-2024	
FILE NAME :	JOB NO.

REVISION	DESCRIPTION

GERNERAL NOTE

DO NOT SCALE DRAWING ALL MEASUREMENT MUST BE **CHECKED AT THE SIDE BY THE CONTRACTOR**


ALL DESIGN AND DRAWINGS ARE THE PROPERTY OF MARCHTEN CO.,LTD **AND NOT BE USED WITH OUT THEIR WRITTEN PERMISSION**

MARCHTEN

ARCHITECTURE / INTERIOR

บริษัท มาร์ชเทน จำกัด

403 ซ.พัฒนาการ 50 สวนหลวง กรุงเทพมหานคร 10250

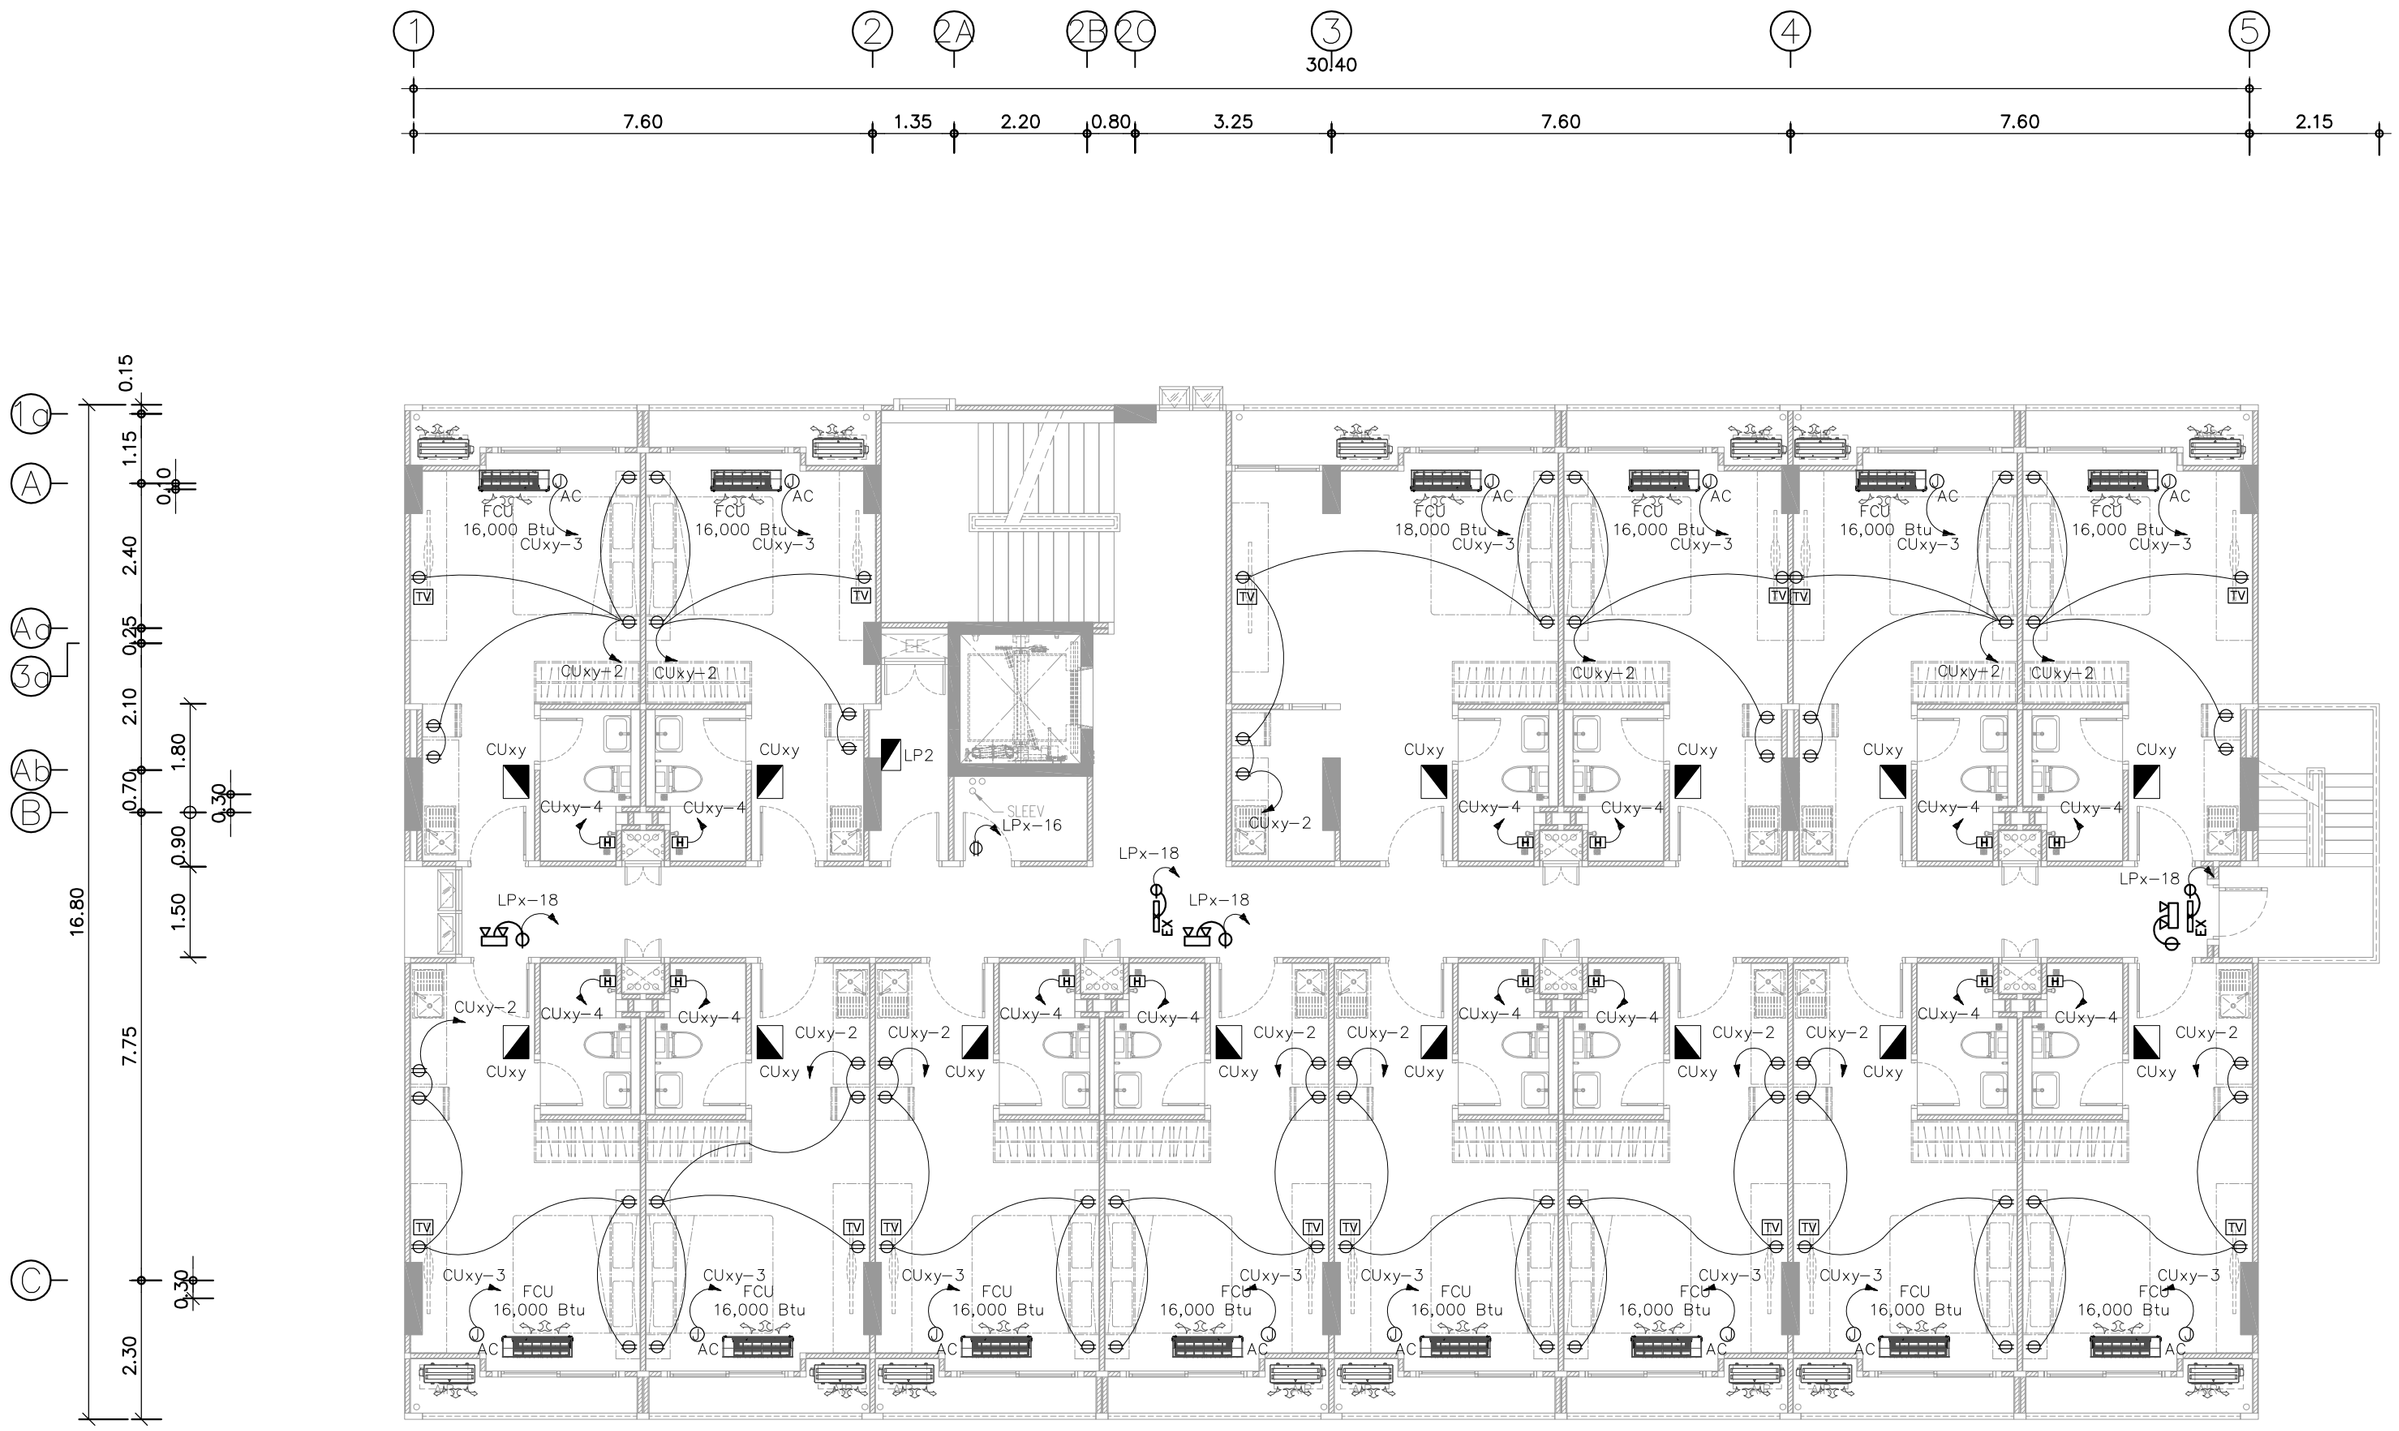

ผังปลั๊กไฟชั้น 3-5

SCALE 1:100

PROJECT NUMBER : VC2023-024

PROJECT

MACHI RESIDENCES

อาคารพักอาศัยรวม ค.ส.ล 7 ชั้น

OWNER

บริษัท ฤทธิกร ลิฟวิ่ง จำกัด

ARCHITECT :

อัคคะภัทร์ จิระอารียบุตร ส-สถ.3040

403 ซ.พัฒนาการ 50 พัฒนาการ

กรุงเทพมหานคร 10250

INTERIOR DESIGNER :

-

STRUCTURAL ENGINEER :

นายพงษ์ธวิทย์ คทาวุธเจริญกุล ลย.12291

ELECTRICAL ENGINEER :

นายภาคภูมิ คำพิทูรย์ ลฟก.5587

MECHANICAL ENGINEER :

SANITARY ENGINEER :

พล.อรวรรณ พลตรี ลส.134

DRAWING TITLE

ผังปลั๊กไฟชั้น 3-5

DRAWING FOR CONSTRUCTION

DRAW BY :	CHECKER :	REVISION :
Weerayuth L.	Akapatr C.	-

SCALE :	DRAWING NO.
1 : 100	EE-13
DATE : 20-10-2024	
FILE NAME :	JOB NO.

REVISION	DESCRIPTION

GERNERAL NOTE

DO NOT SCALE DRAWING ALL MEASUREMENT MUST BE **CHECKED AT THE SIDE BY THE CONTRACTOR**


ALL DESIGN AND DRAWINGS ARE THE PROPERTY OF MARCHTEN CO.,LTD **AND NOT BE USED WITH OUT THEIR WRITTEN PERMISSION**

MARCHTEN

ARCHITECTURE / INTERIOR

บริษัท มาร์ชเทน จำกัด

403 ซ.พัฒนาการ 50 สวนหลวง กรุงเทพมหานคร 10250

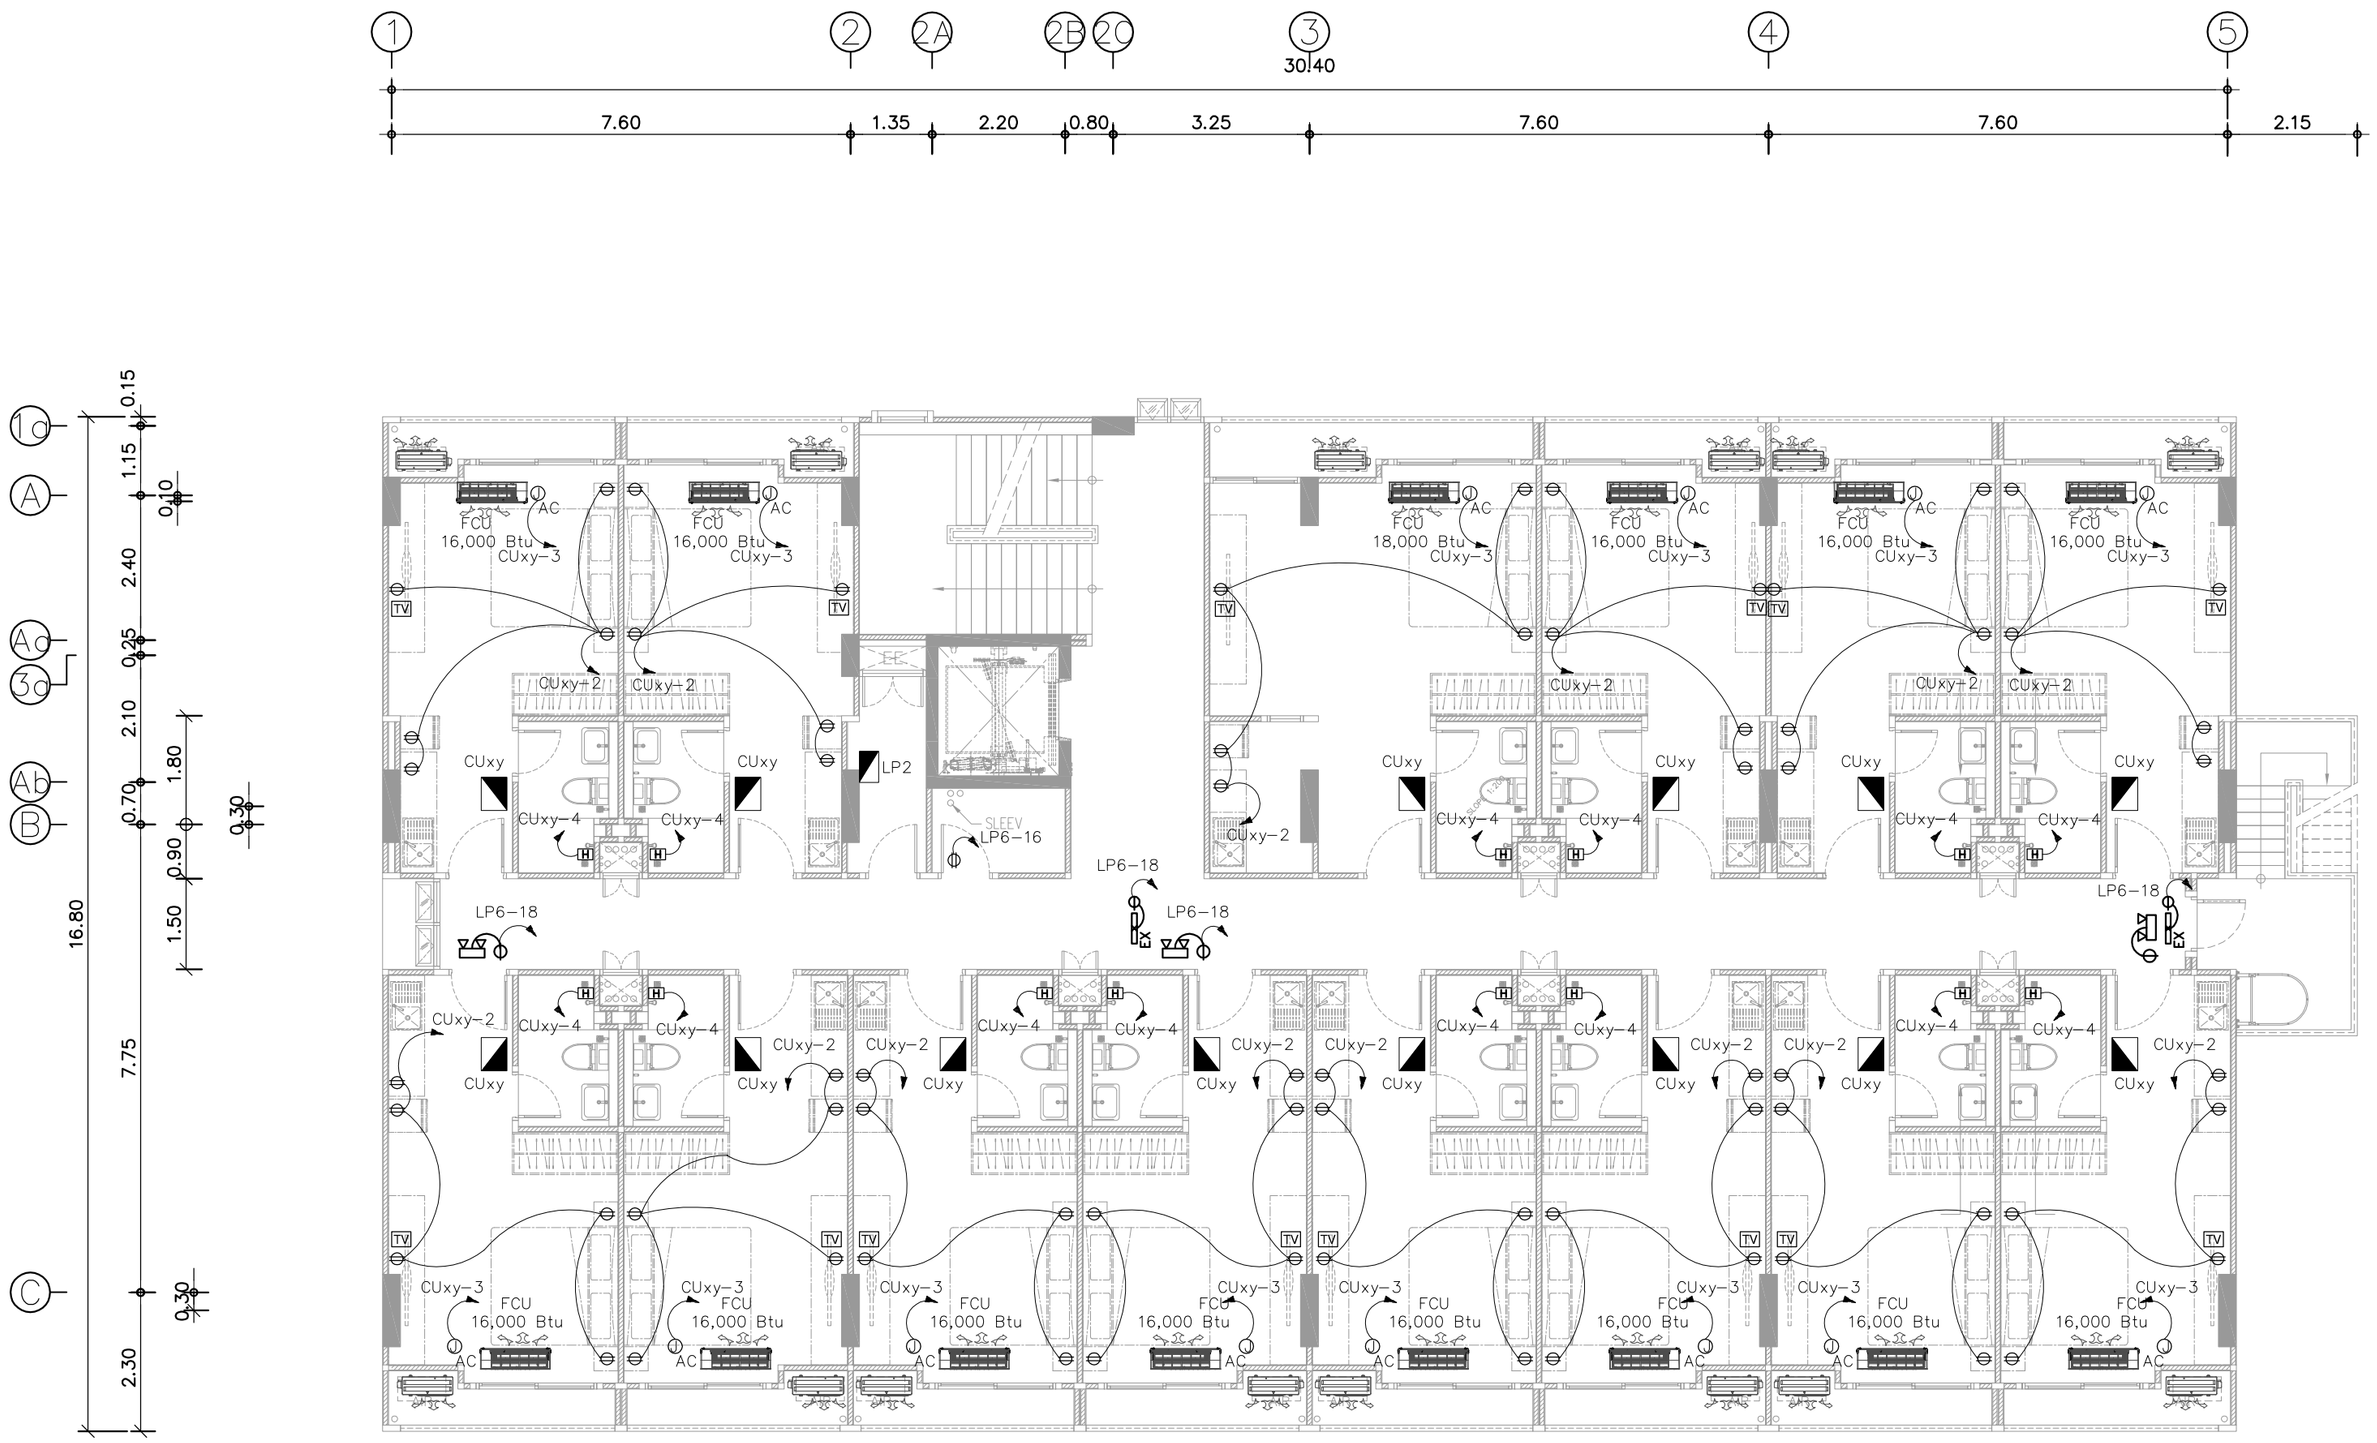

ผังปลั๊กไฟชั้น 6

SCALE 1:100

PROJECT NUMBER : VC2023-024

PROJECT

MACHI RESIDENCES

อาคารพักอาศัยรวม ค.ส.ล 7 ชั้น

OWNER

บริษัท ฤทธิกร ลิฟวิ่ง จำกัด

ARCHITECT :

อัคคะภัทร์ จิระอารียบุตร ส-สถ.3040

403 ซ.พัฒนาการ 50 พัฒนาการ

กรุงเทพมหานคร 10250

INTERIOR DESIGNER :

-

STRUCTURAL ENGINEER :

นายพงษ์ธวิทย์ คทาวุธเจริญกุล ลย.12291

ELECTRICAL ENGINEER :

นายภาคภูมิ คำพิทูรย์ ลฟก.5587

MECHANICAL ENGINEER :

SANITARY ENGINEER :

พล.อรวรรณ พลตรี ลส.134

DRAWING TITLE

ผังปลั๊กไฟชั้น 6

DRAWING FOR CONSTRUCTION


DRAW BY :	CHECKER :	REVISION :
Weerayuth L.	Akapatr C.	-

SCALE :	DRAWING NO.
1 : 100	EE-14
DATE : 20-10-2024	
FILE NAME :	JOB NO.

REVISION	DESCRIPTION

GERNERAL NOTE
DO NOT SCALE DRAWING ALL MEASUREMENT MUST BE
CHECKED AT THE SIDE BY THE CONTRACTOR
ALL DESIGN AND DRAWINGS ARE THE PROPERTY OF
MARCHTEN CO.,LTD
AND NOT BE USED WITH OUT THEIR WRITTEN PERMISSION

MARCHTEN
ARCHITECTURE / INTERIOR
บริษัท มาร์ชเทน จำกัด
403 ซ.พัฒนาการ 50 สวนหลวง กรุงเทพมหานคร 10250

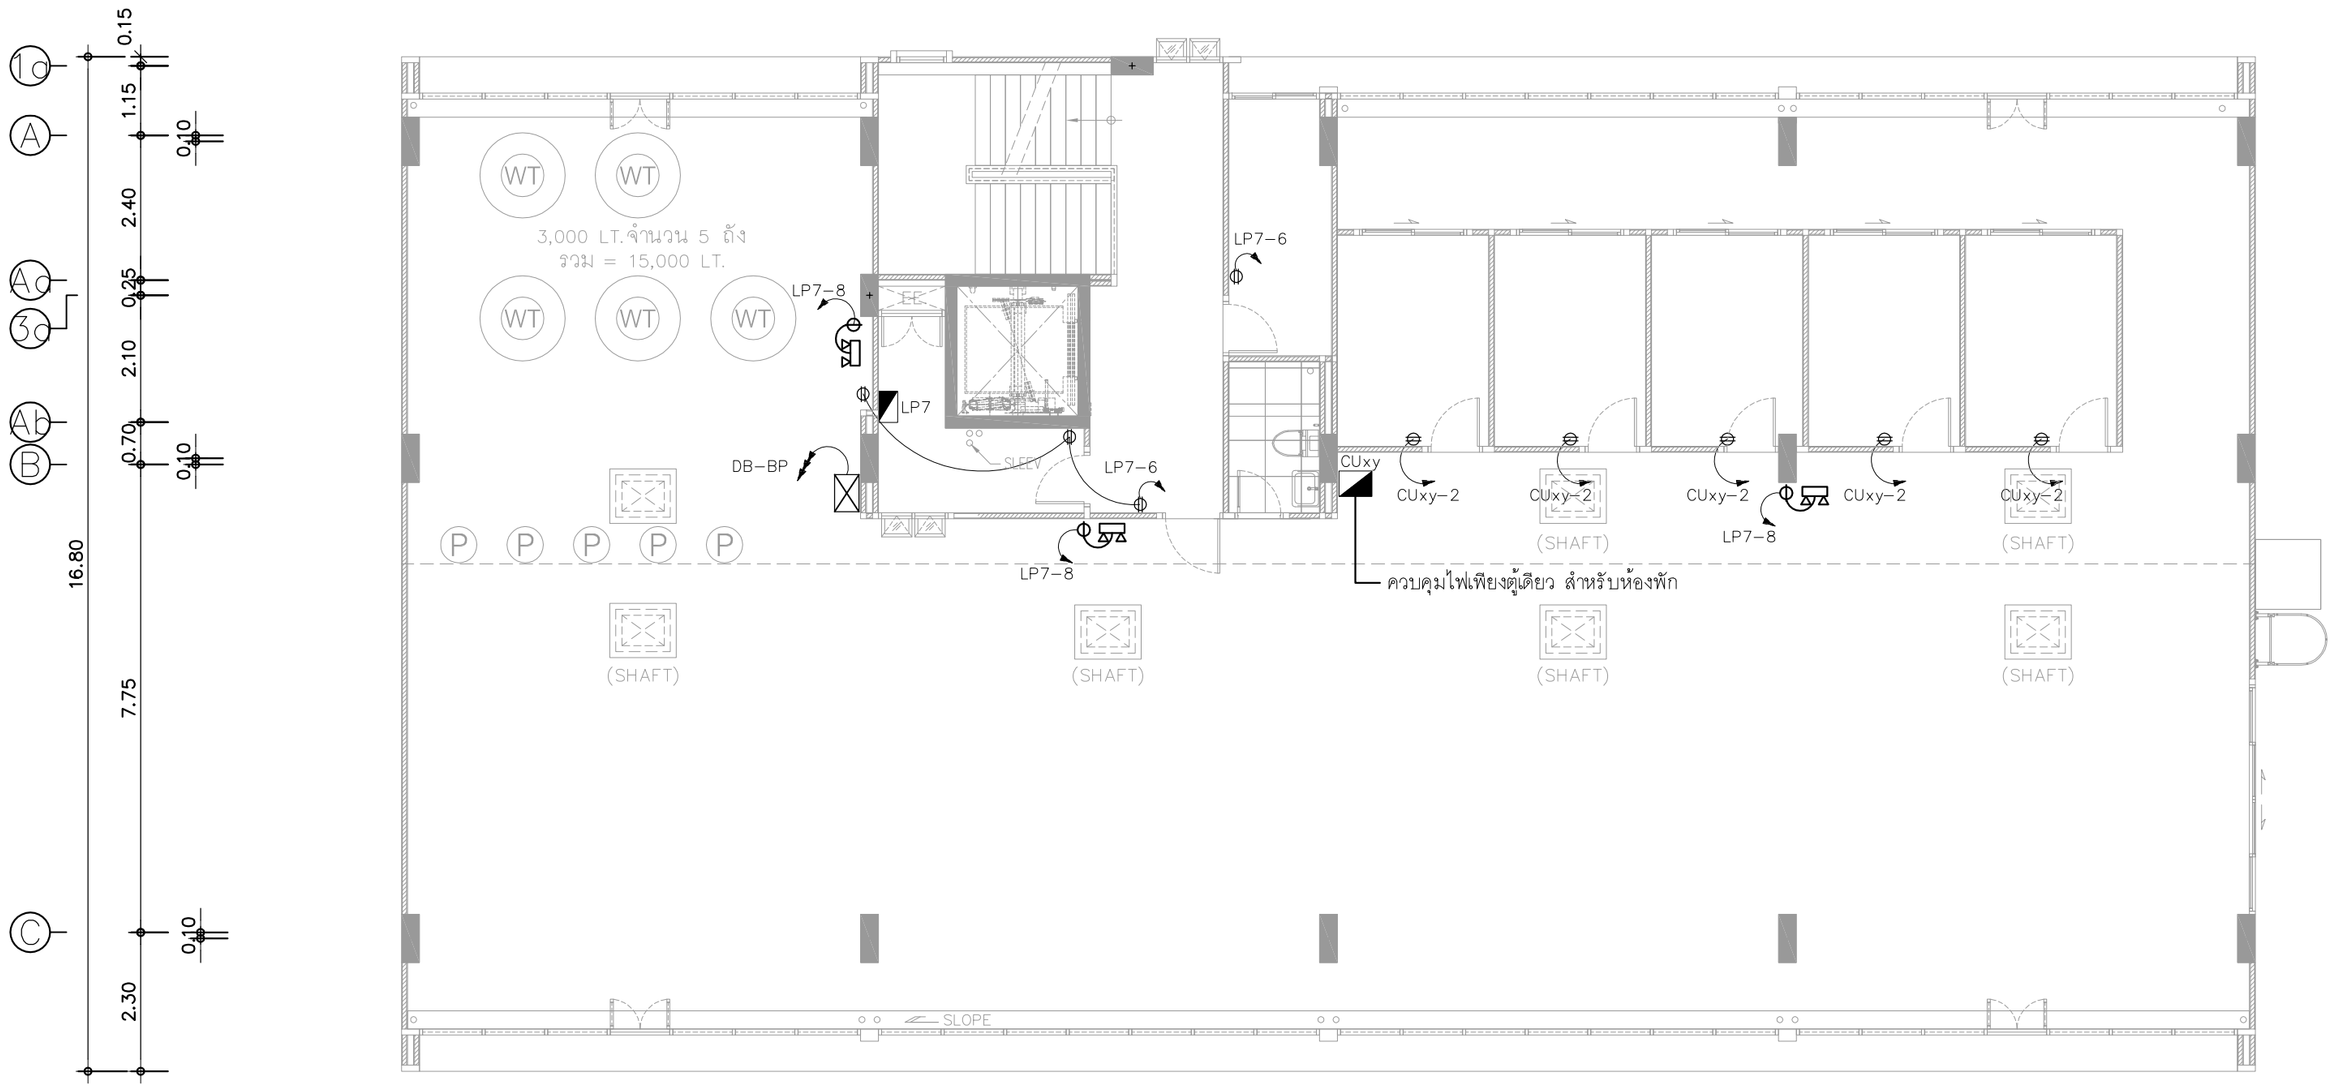

ผังปลั๊กไฟชั้น 7 ห้องใต้หลังคา

SCALE 1:100

PROJECT NUMBER : VC2023-024

PROJECT

MACHI RESIDENCES

อาคารพักอาศัยรวม ค.ส.ล 7 ชั้น

OWNER

บริษัท ฤทธิกร ลิฟวิ่ง จำกัด

ARCHITECT :

อัคคะภัทร์ จิระอารียบุตร ส-สถ.3040

403 ซ.พัฒนาการ 50 พัฒนาการ

กรุงเทพมหานคร 10250

INTERIOR DESIGNER :

-

STRUCTURAL ENGINEER :

นายพงษ์ธวิทย์ คทาวุธเจริญกุล ลย.12291

ELECTRICAL ENGINEER :

นายภาคภูมิ คำพิทูรย์ ลฟก.5587

MECHANICAL ENGINEER :

SANITARY ENGINEER :

นส.อรวรรณ พลศรี ลส.134

DRAWING TITLE

ผังปลั๊กไฟชั้น 7 ห้องใต้หลังคา

DRAWING FOR CONSTRUCTION

DRAW BY :	CHECKER :	REVISION :
Weerayuth L.	Akapatr C.	–

SCALE :	DRAWING NO.
1 : 100	EE-15
DATE : 20-10-2024	
FILE NAME :	JOB NO.

REVISION	DESCRIPTION

GERNERAL NOTE

DO NOT SCALE DRAWING ALL MEASUREMENT MUST BE

CHECKED AT THE SIDE BY THE CONTRACTOR

ALL DESIGN AND DRAWINGS ARE THE PROPERTY OF

MARCHTEN CO.,LTD


AND NOT BE USED WITH OUT THEIR WRITTEN PERMISSION

MARCHTEN

ARCHITECTURE / INTERIOR

บริษัท มาร์ชเทน จำกัด

403 ซ.พัฒนาการ 50 สวนหลวง กรุงเทพมหานคร 10250

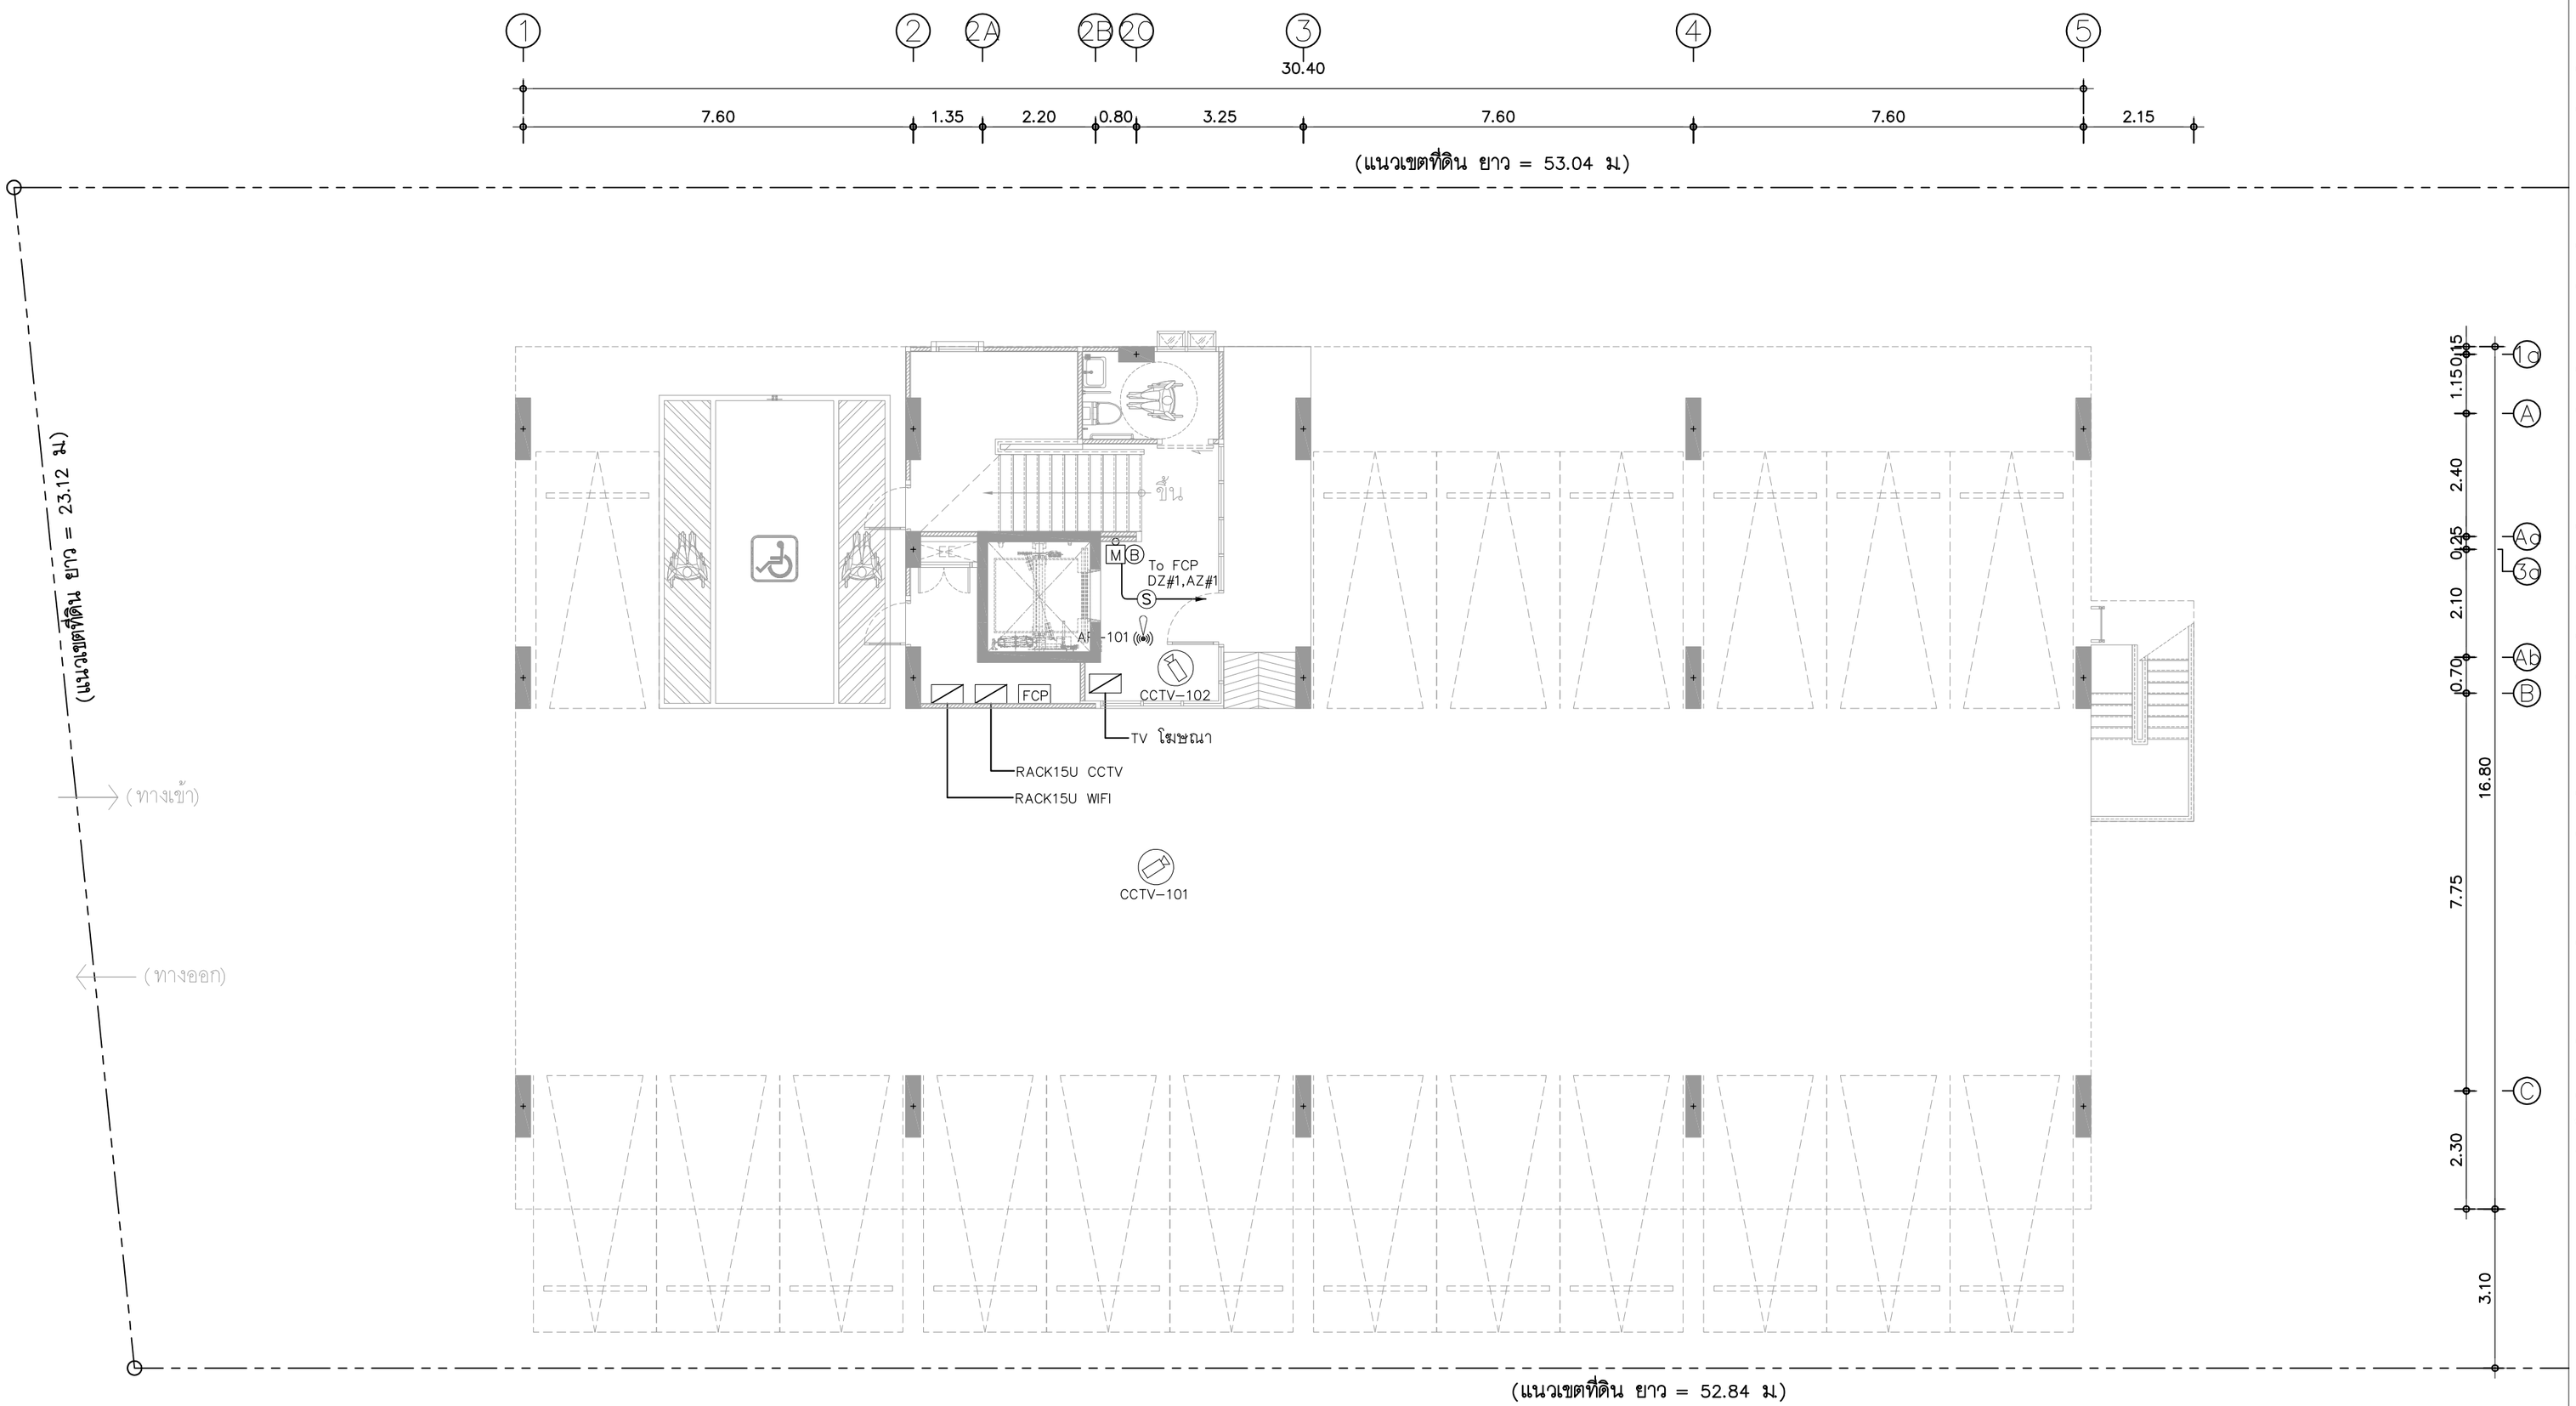

แปลนแสดงระบบสัญญาณแจ้งเหตุเพลิงไหม้ , กล้องวงจรปิด , Access Point ชั้น 1

SCALE 1:100

PROJECT NUMBER : VC2023-024

PROJECT

MACHI RESIDENCES

อาคารพักอาศัยรวม ค.ส.ล 7 ชั้น

OWNER

บริษัท ฤทธิกร ลิฟวิ่ง จำกัด

ARCHITECT :

อัคคะภัทร์ จิระอารีย์บุตร ส-สถ.3040

403 ซ.พัฒนาการ 50 พัฒนาการ

กรุงเทพมหานคร 10250

INTERIOR DESIGNER :

-

STRUCTURAL ENGINEER :

นายพงษ์ธวิทย์ คทาวุธเจริญกุล ลย.12291

ELECTRICAL ENGINEER :

นายภาคภูมิ คำพิทูรย์ ลฟก.5587

MECHANICAL ENGINEER :

SANITARY ENGINEER :

นส.อรวรรณ พลตรี ลส.134

DRAWING TITLE

แปลนแสดงระบบสัญญาณแจ้งเหตุเพลิงไหม้

กล้องวงจรปิด , Access Point ชั้น 1

DRAWING FOR CONSTRUCTION

DRAW BY :	CHECKER :	REVISION :
Weerayuth L.	Akapatr C.	–

SCALE :	DRAWING NO.
1 : 100	EE-16
DATE : 20-10-2024	
FILE NAME :	JOB NO.

REVISION	DESCRIPTION

GERNERAL NOTE

DO NOT SCALE DRAWING ALL MEASUREMENT MUST BE

CHECKED AT THE SIDE BY THE CONTRACTOR

ALL DESIGN AND DRAWINGS ARE THE PROPERTY OF

MARCHTEN CO.,LTD


AND NOT BE USED WITH OUT THEIR WRITTEN PERMISSION

MARCHTEN

ARCHITECTURE / INTERIOR

บริษัท มาร์ชเทน จำกัด

403 ซ.พัฒนาการ 50 สวนหลวง กรุงเทพมหานคร 10250

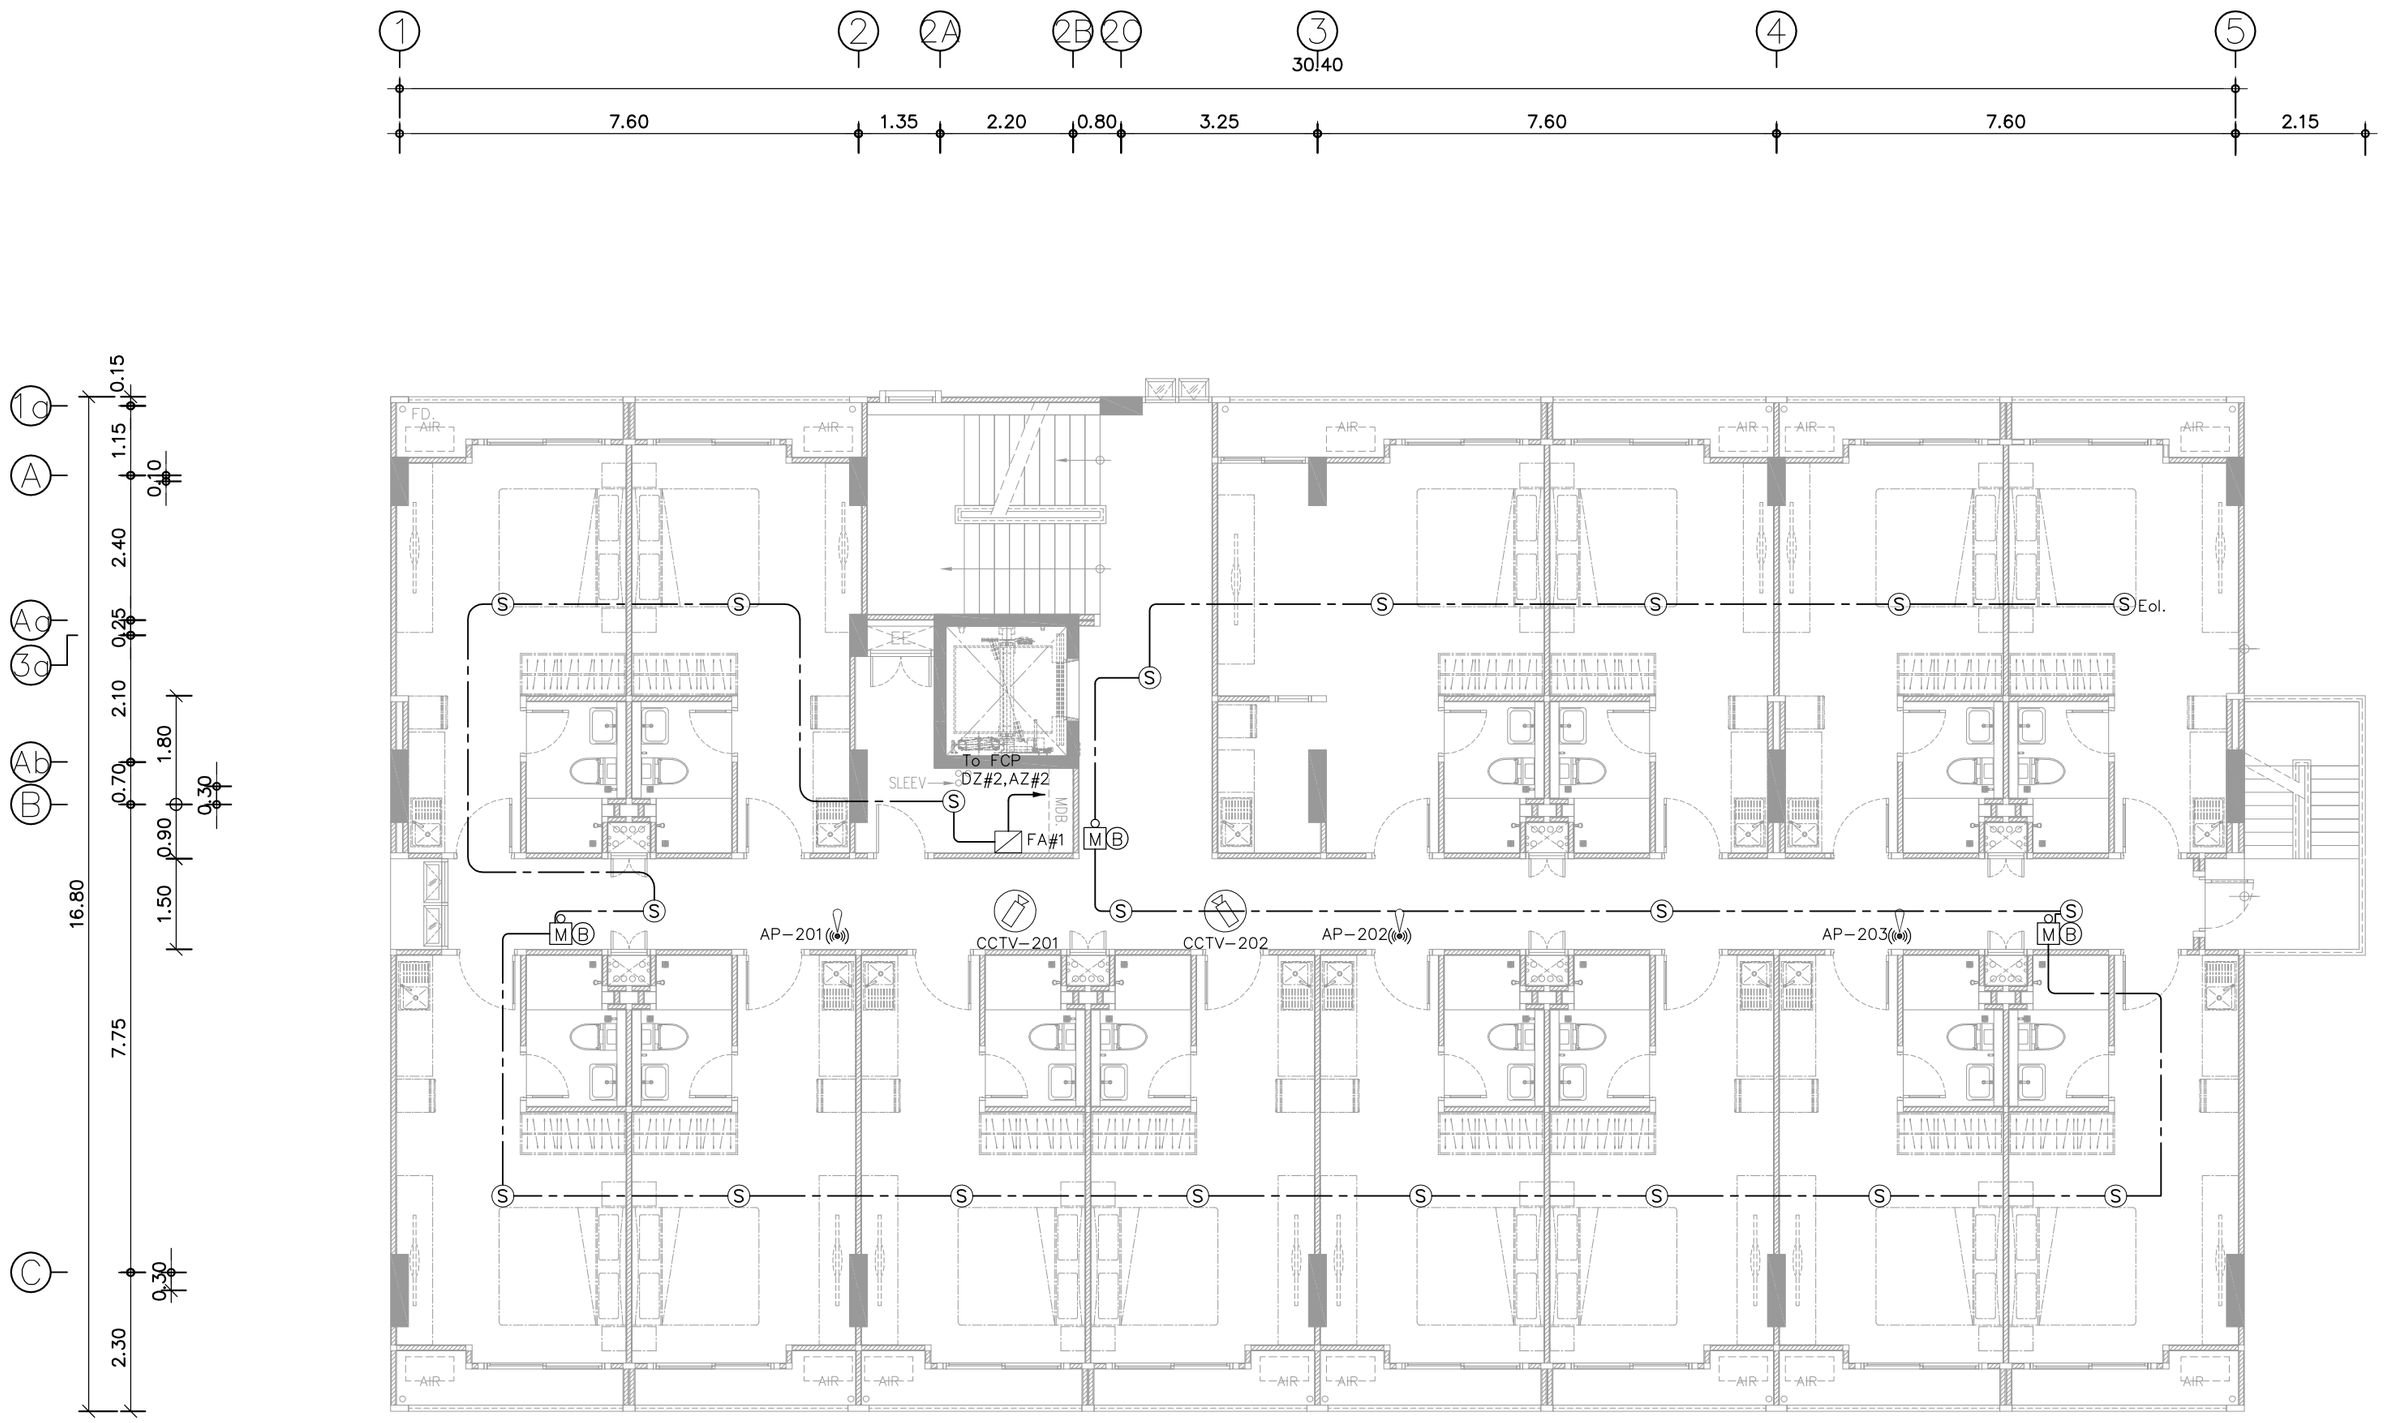

แปลนแสดงระบบสัญญาณแจ้งเหตุเพลิงไหม้ , กล้องวงจรปิด , Access Point ชั้น 2

SCALE 1:100

PROJECT NUMBER : VC2023-024

PROJECT

MACHI RESIDENCES

อาคารพักอาศัยรวม ค.ส.ล 7 ชั้น

OWNER

บริษัท ฤทธิกร ลิฟวิ่ง จำกัด

ARCHITECT :

อัคคะภัทร์ จิระอารีย์บุตร ส-สถ.3040

403 ซ.พัฒนาการ 50 พัฒนาการ

กรุงเทพมหานคร 10250

INTERIOR DESIGNER :

-

STRUCTURAL ENGINEER :

นายพงษ์ธวิทย์ คทาวุธเจริญกุล ลย.12291

ELECTRICAL ENGINEER :

นายภาคภูมิ คำพิทูรย์ ลฟก.5587

MECHANICAL ENGINEER :

SANITARY ENGINEER :

นส.อรวรรณ พลตรี ลส.134

DRAWING TITLE

แปลนแสดงระบบสัญญาณแจ้งเหตุเพลิงไหม้

กล้องวงจรปิด , Access Point ชั้น 2

DRAWING FOR CONSTRUCTION

DRAW BY :	CHECKER :	REVISION :
Weerayuth L.	Akapatr C.	-

SCALE :	DRAWING NO.
1 : 100	EE-17
DATE : 20-10-2024	
FILE NAME :	JOB NO.

REVISION	DESCRIPTION

GERNERAL NOTE

DO NOT SCALE DRAWING ALL MEASUREMENT MUST BE **CHECKED AT THE SIDE BY THE CONTRACTOR**


ALL DESIGN AND DRAWINGS ARE THE PROPERTY OF MARCHTEN CO.,LTD **AND NOT BE USED WITH OUT THEIR WRITTEN PERMISSION**

MARCHTEN

ARCHITECTURE / INTERIOR

บริษัท มาร์ชเทน จำกัด

403 ซ.พัฒนาการ 50 แขวนหลวง กรุงเทพมหานคร 10250

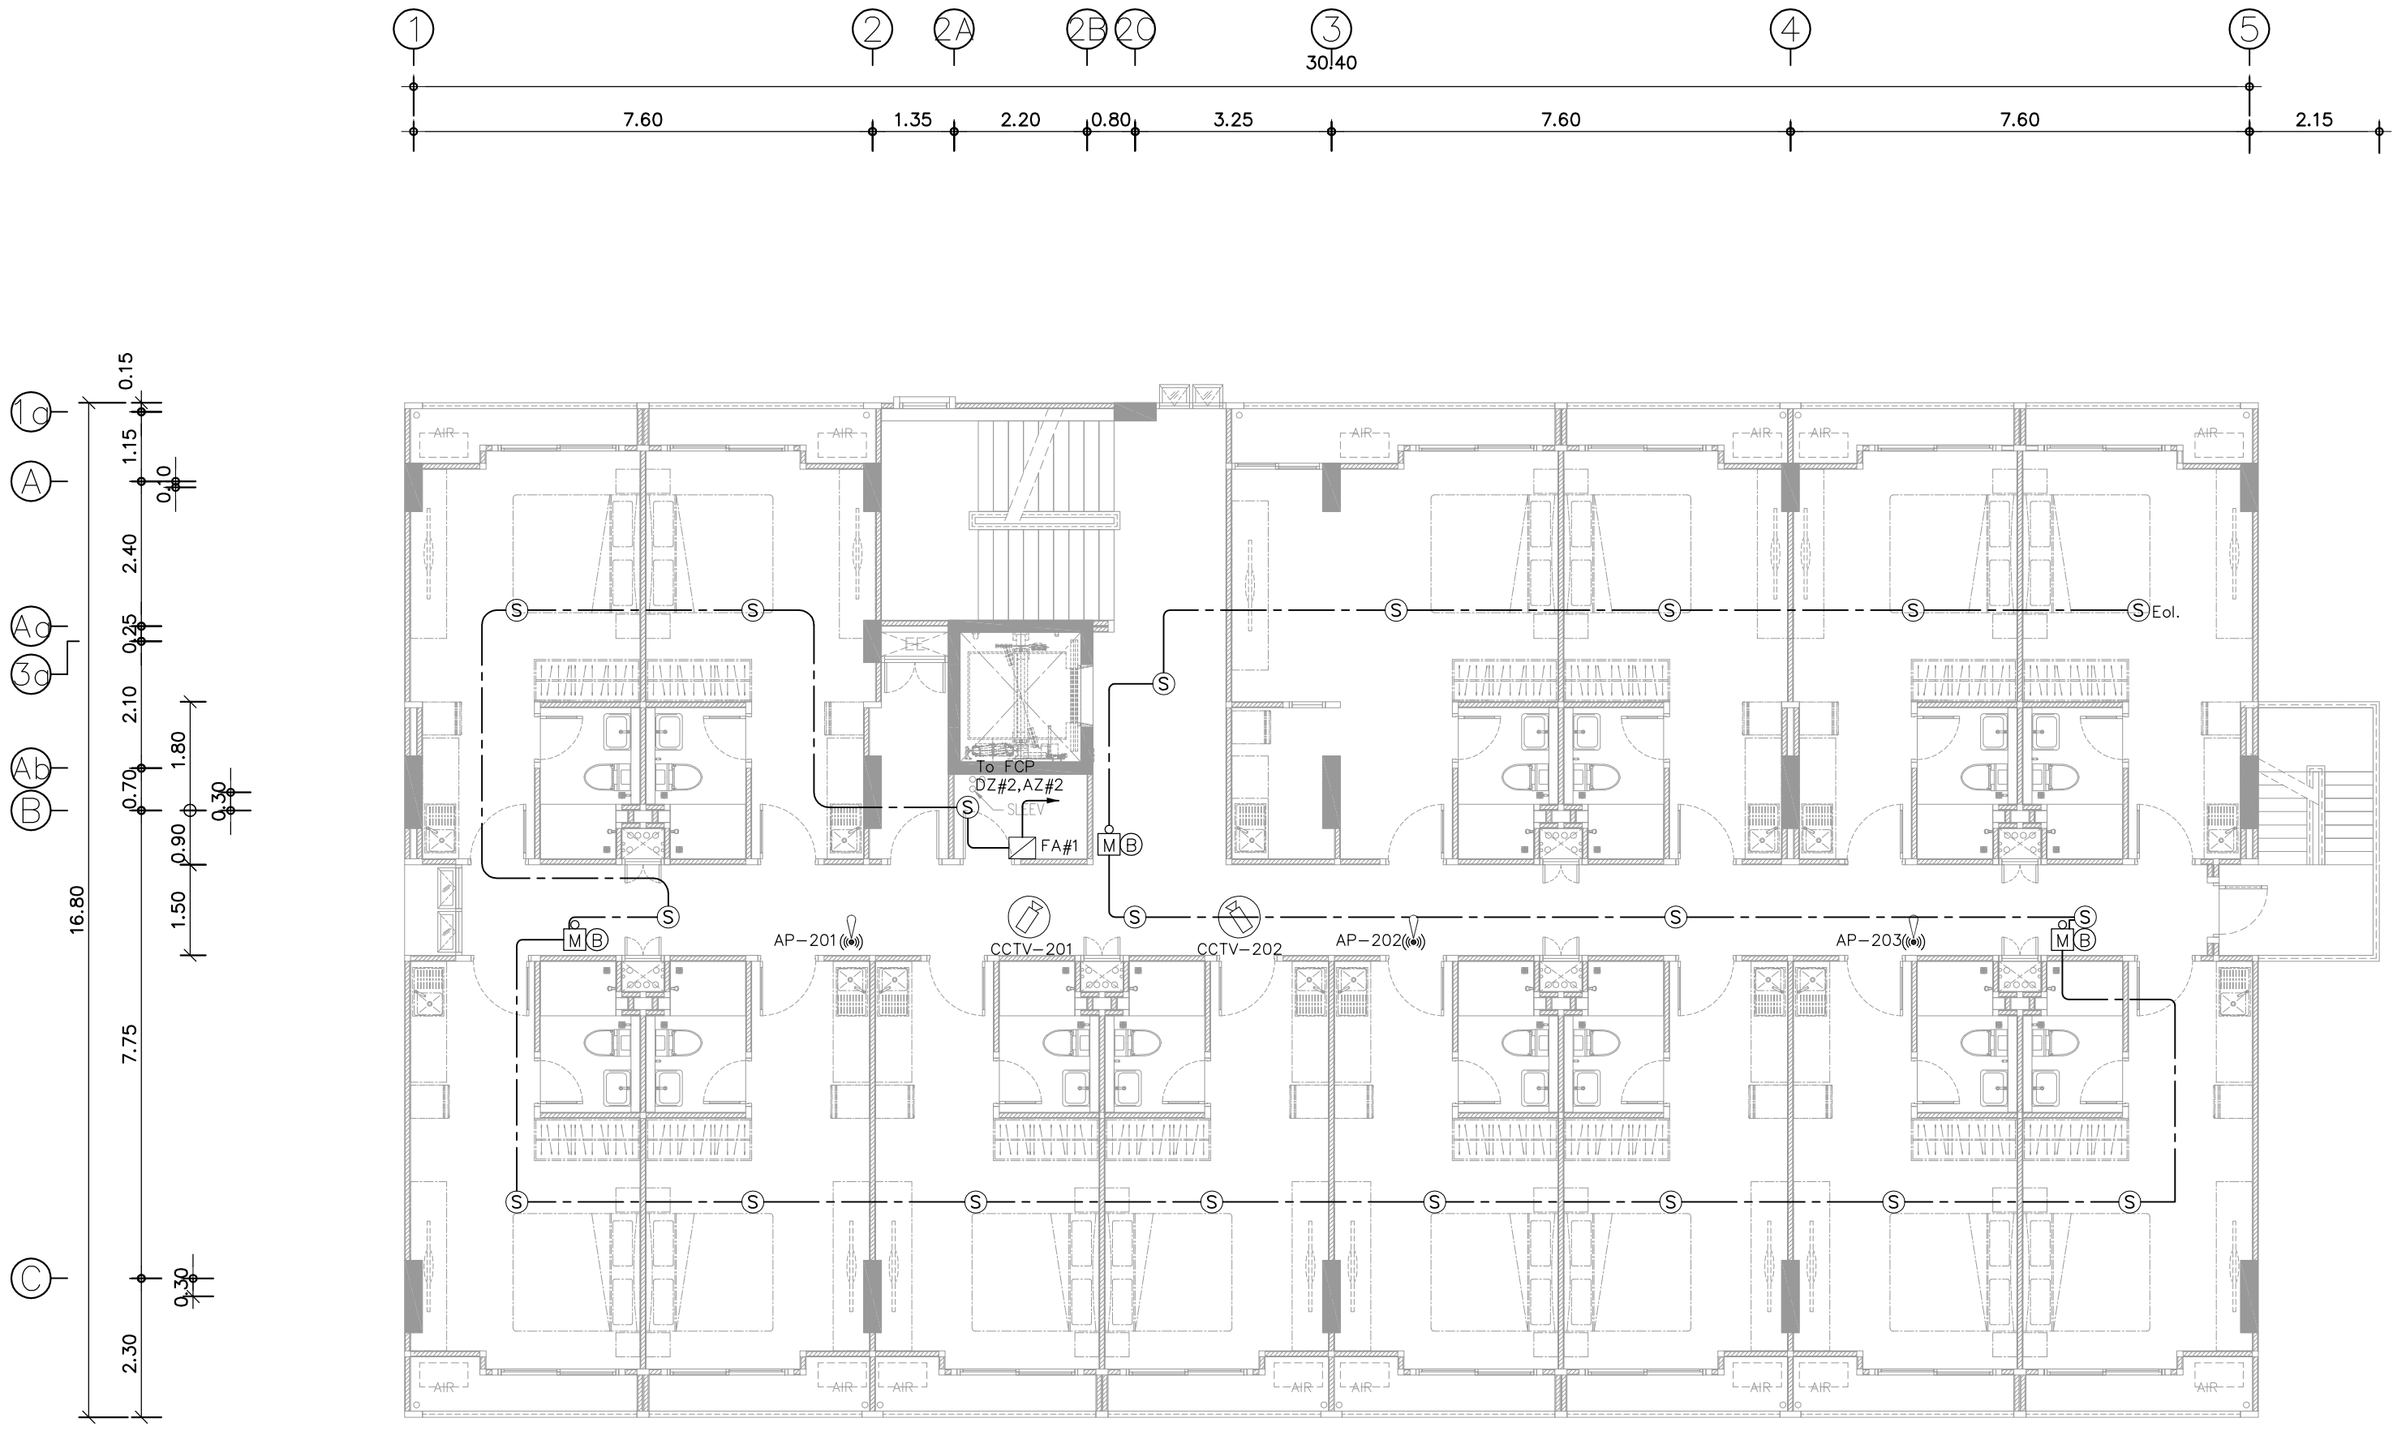

แปลนแสดงระบบสัญญาณแจ้งเหตุเพลิงไหม้ , กล้องวงจรปิด , Access Point ชั้น 3-5

SCALE 1:100

PROJECT NUMBER : VC2023-024

PROJECT

MACHI RESIDENCES

อาคารพักอาศัยรวม ค.ส.ล 7 ชั้น

OWNER

บริษัท ฤทธิกร ลิฟวิ่ง จำกัด

ARCHITECT :

อัคคะภัทร์ จิระอารียบุตร ส-สถ.3040

403 ซ.พัฒนาการ 50 พัฒนาการ

กรุงเทพมหานคร 10250

INTERIOR DESIGNER :

-

STRUCTURAL ENGINEER :

นายพงษ์ธวิทย์ คทาวุธเจริญกุล ลย.12291

ELECTRICAL ENGINEER :

นายภาคภูมิ คำพิทูรย์ ลฟก.5587

MECHANICAL ENGINEER :

SANITARY ENGINEER :

นส.อรวรรณ พลตรี ลส.134

DRAWING TITLE

แปลนแสดงระบบสัญญาณแจ้งเหตุเพลิงไหม้

กล้องวงจรปิด , Access Point ชั้น 3-5

DRAWING FOR CONSTRUCTION

DRAW BY :	CHECKER :	REVISION :
Weerayuth L.	Akapatr C.	-

SCALE :	DRAWING NO.
1 : 100	EE-18
DATE : 20-10-2024	
FILE NAME :	JOB NO.

REVISION	DESCRIPTION

GERNERAL NOTE

DO NOT SCALE DRAWING ALL MEASUREMENT MUST BE **CHECKED AT THE SIDE BY THE CONTRACTOR**


ALL DESIGN AND DRAWINGS ARE THE PROPERTY OF MARCHTEN CO.,LTD **AND NOT BE USED WITH OUT THEIR WRITTEN PERMISSION**

MARCHTEN

ARCHITECTURE / INTERIOR

บริษัท มาร์ชเทน จำกัด

403 ซ.พัฒนาการ 50 สวนหลวง กรุงเทพมหานคร 10250

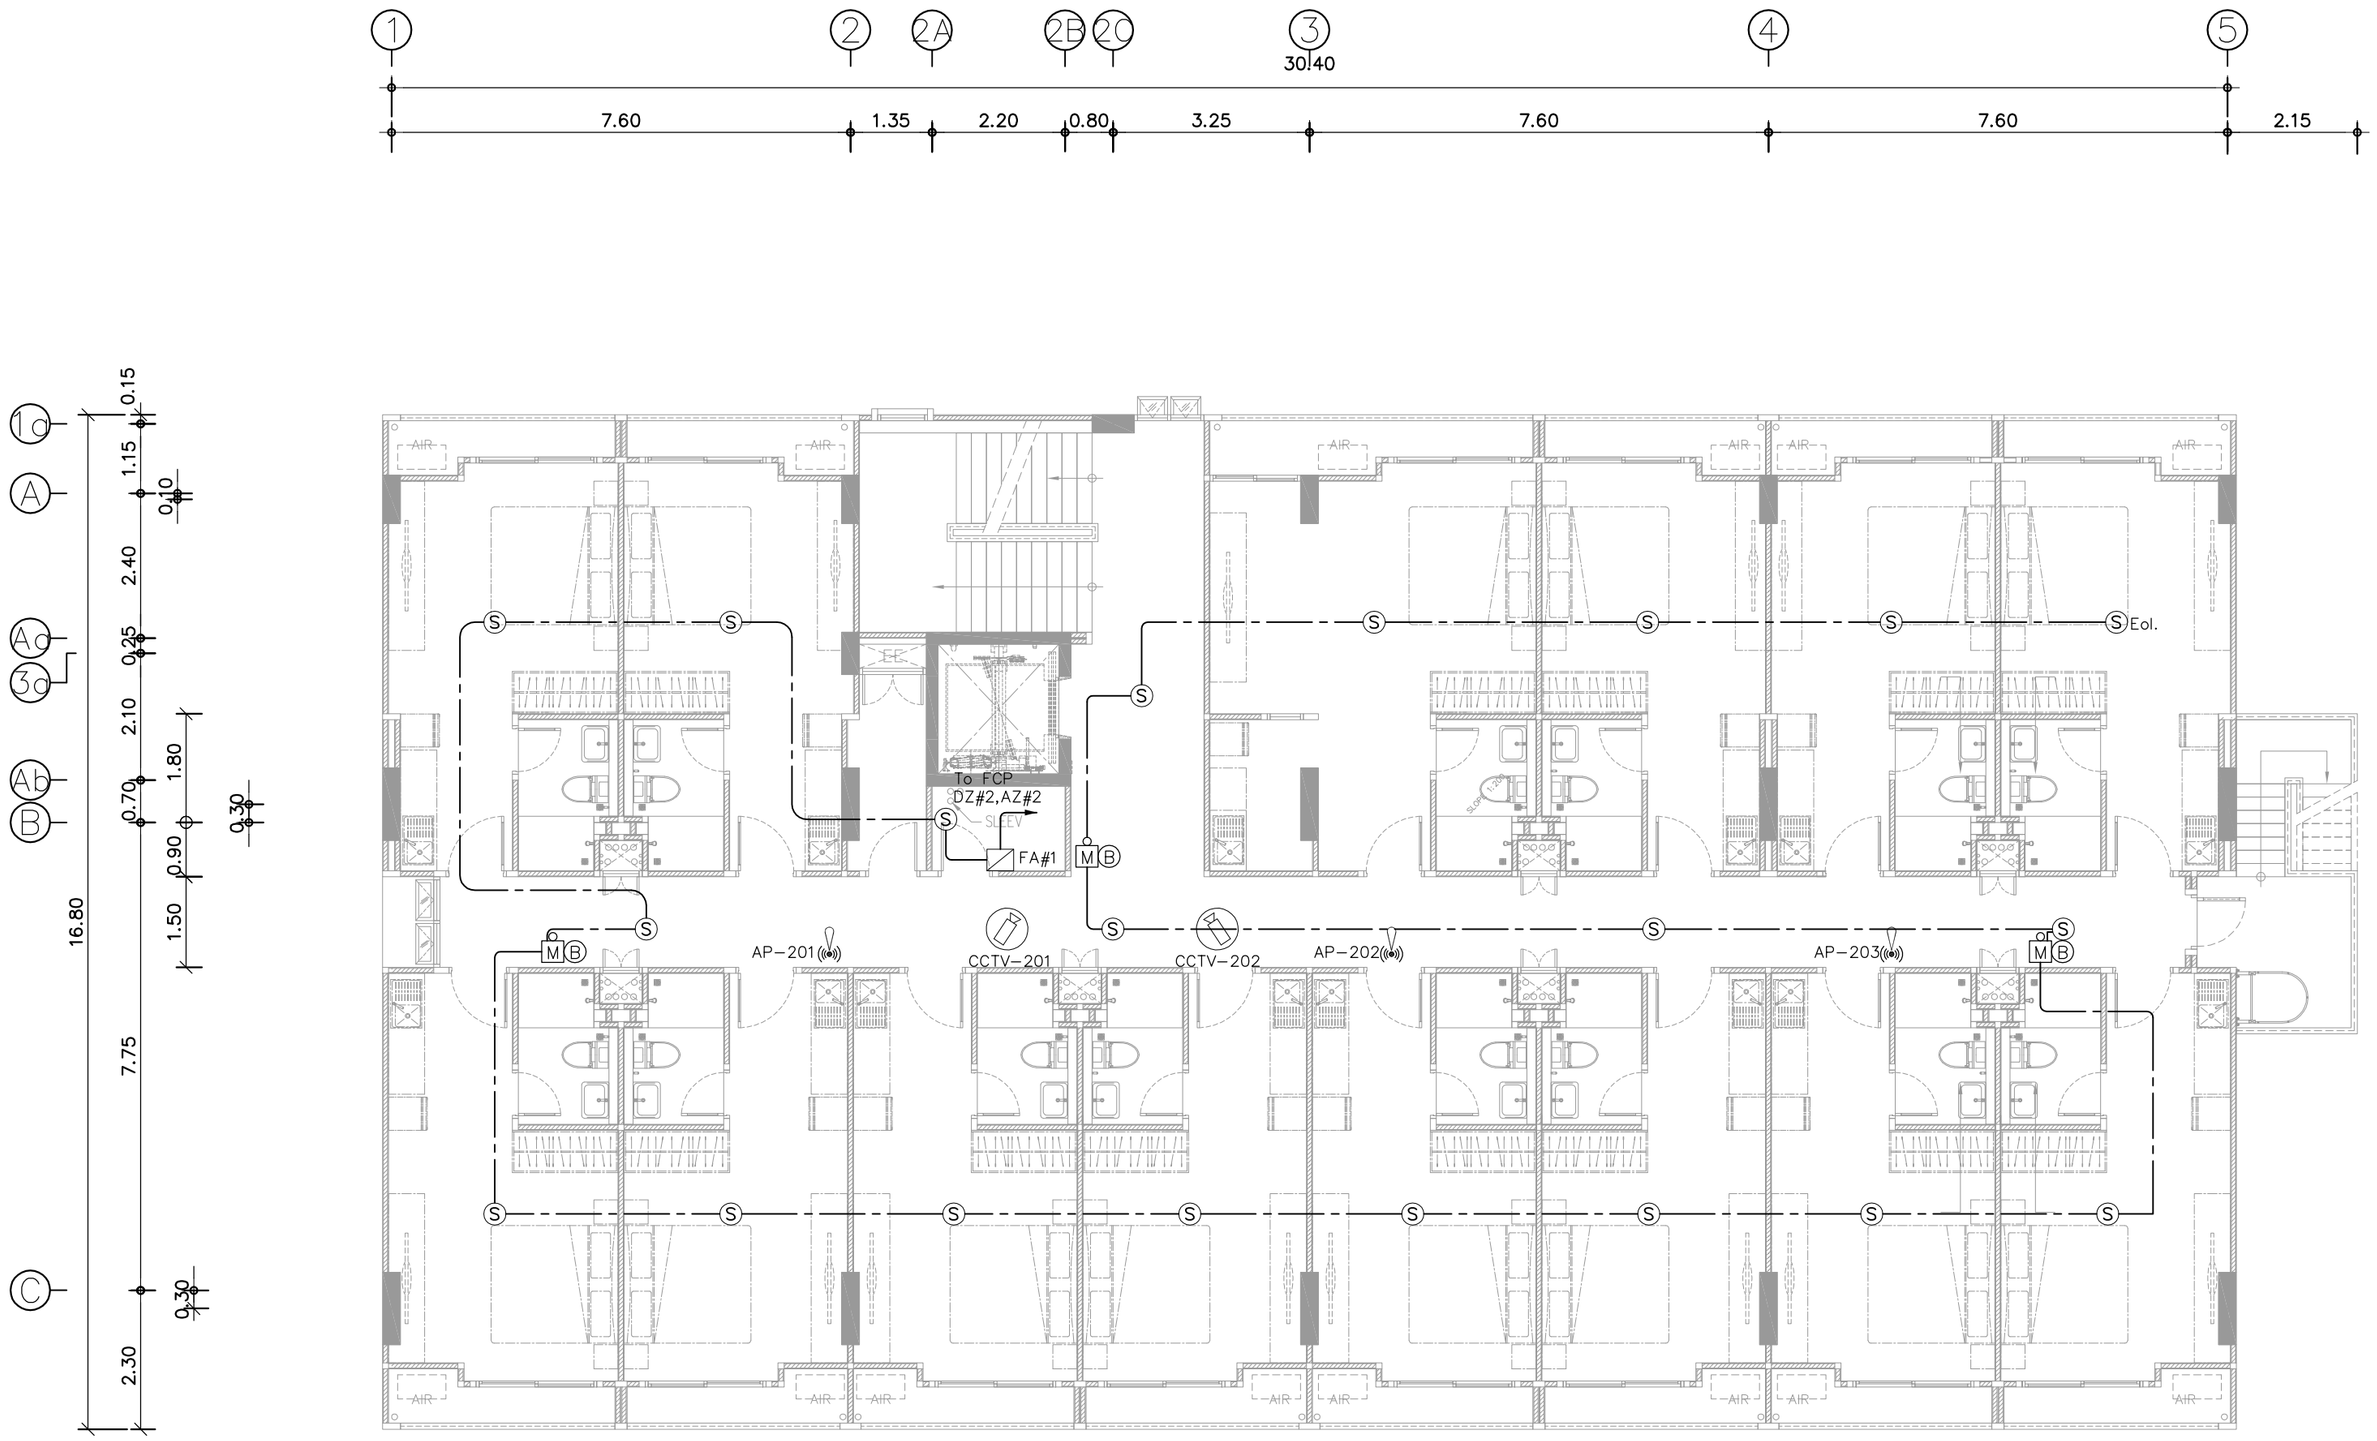

แปลนแสดงระบบสัญญาณแจ้งเหตุเพลิงไหม้ , กล้องวงจรปิด , Access Point ชั้น 6

SCALE 1:100

PROJECT NUMBER : VC2023-024

PROJECT

MACHI RESIDENCES

อาคารพักอาศัยรวม ค.ส.ล 7 ชั้น

OWNER

บริษัท ฤทธิกร ลิฟวิ่ง จำกัด

ARCHITECT :

อัคคะภัทร์ จิระอารียบุตร ส-สถ.3040

403 ซ.พัฒนาการ 50 พัฒนาการ

กรุงเทพมหานคร 10250

INTERIOR DESIGNER :

-

STRUCTURAL ENGINEER :

นายพงษ์ธวิทย์ คทาวุธเจริญกุล ลย.12291

ELECTRICAL ENGINEER :

นายภาคภูมิ คำพิทูรย์ ลฟก.5587

MECHANICAL ENGINEER :

SANITARY ENGINEER :

นส.อรวรรณ พลตรี ลส.134

DRAWING TITLE

แปลนแสดงระบบสัญญาณแจ้งเหตุเพลิงไหม้

กล้องวงจรปิด , Access Point ชั้น 6

DRAWING FOR CONSTRUCTION

DRAW BY :	CHECKER :	REVISION :
Weerayuth L.	Akapatr C.	-

SCALE :	DRAWING NO.
1 : 100	EE-19
DATE : 20-10-2024	
FILE NAME :	JOB NO.

REVISION	DESCRIPTION

GERNERAL NOTE

DO NOT SCALE DRAWING ALL MEASUREMENT MUST BE **CHECKED AT THE SIDE BY THE CONTRACTOR**


ALL DESIGN AND DRAWINGS ARE THE PROPERTY OF MARCHTEN CO.,LTD **AND NOT BE USED WITH OUT THEIR WRITTEN PERMISSION**

MARCHTEN

ARCHITECTURE / INTERIOR

บริษัท มาร์ชเทน จำกัด

403 ซ.พัฒนาการ 50 แขวนหลวง กรุงเทพมหานคร 10250

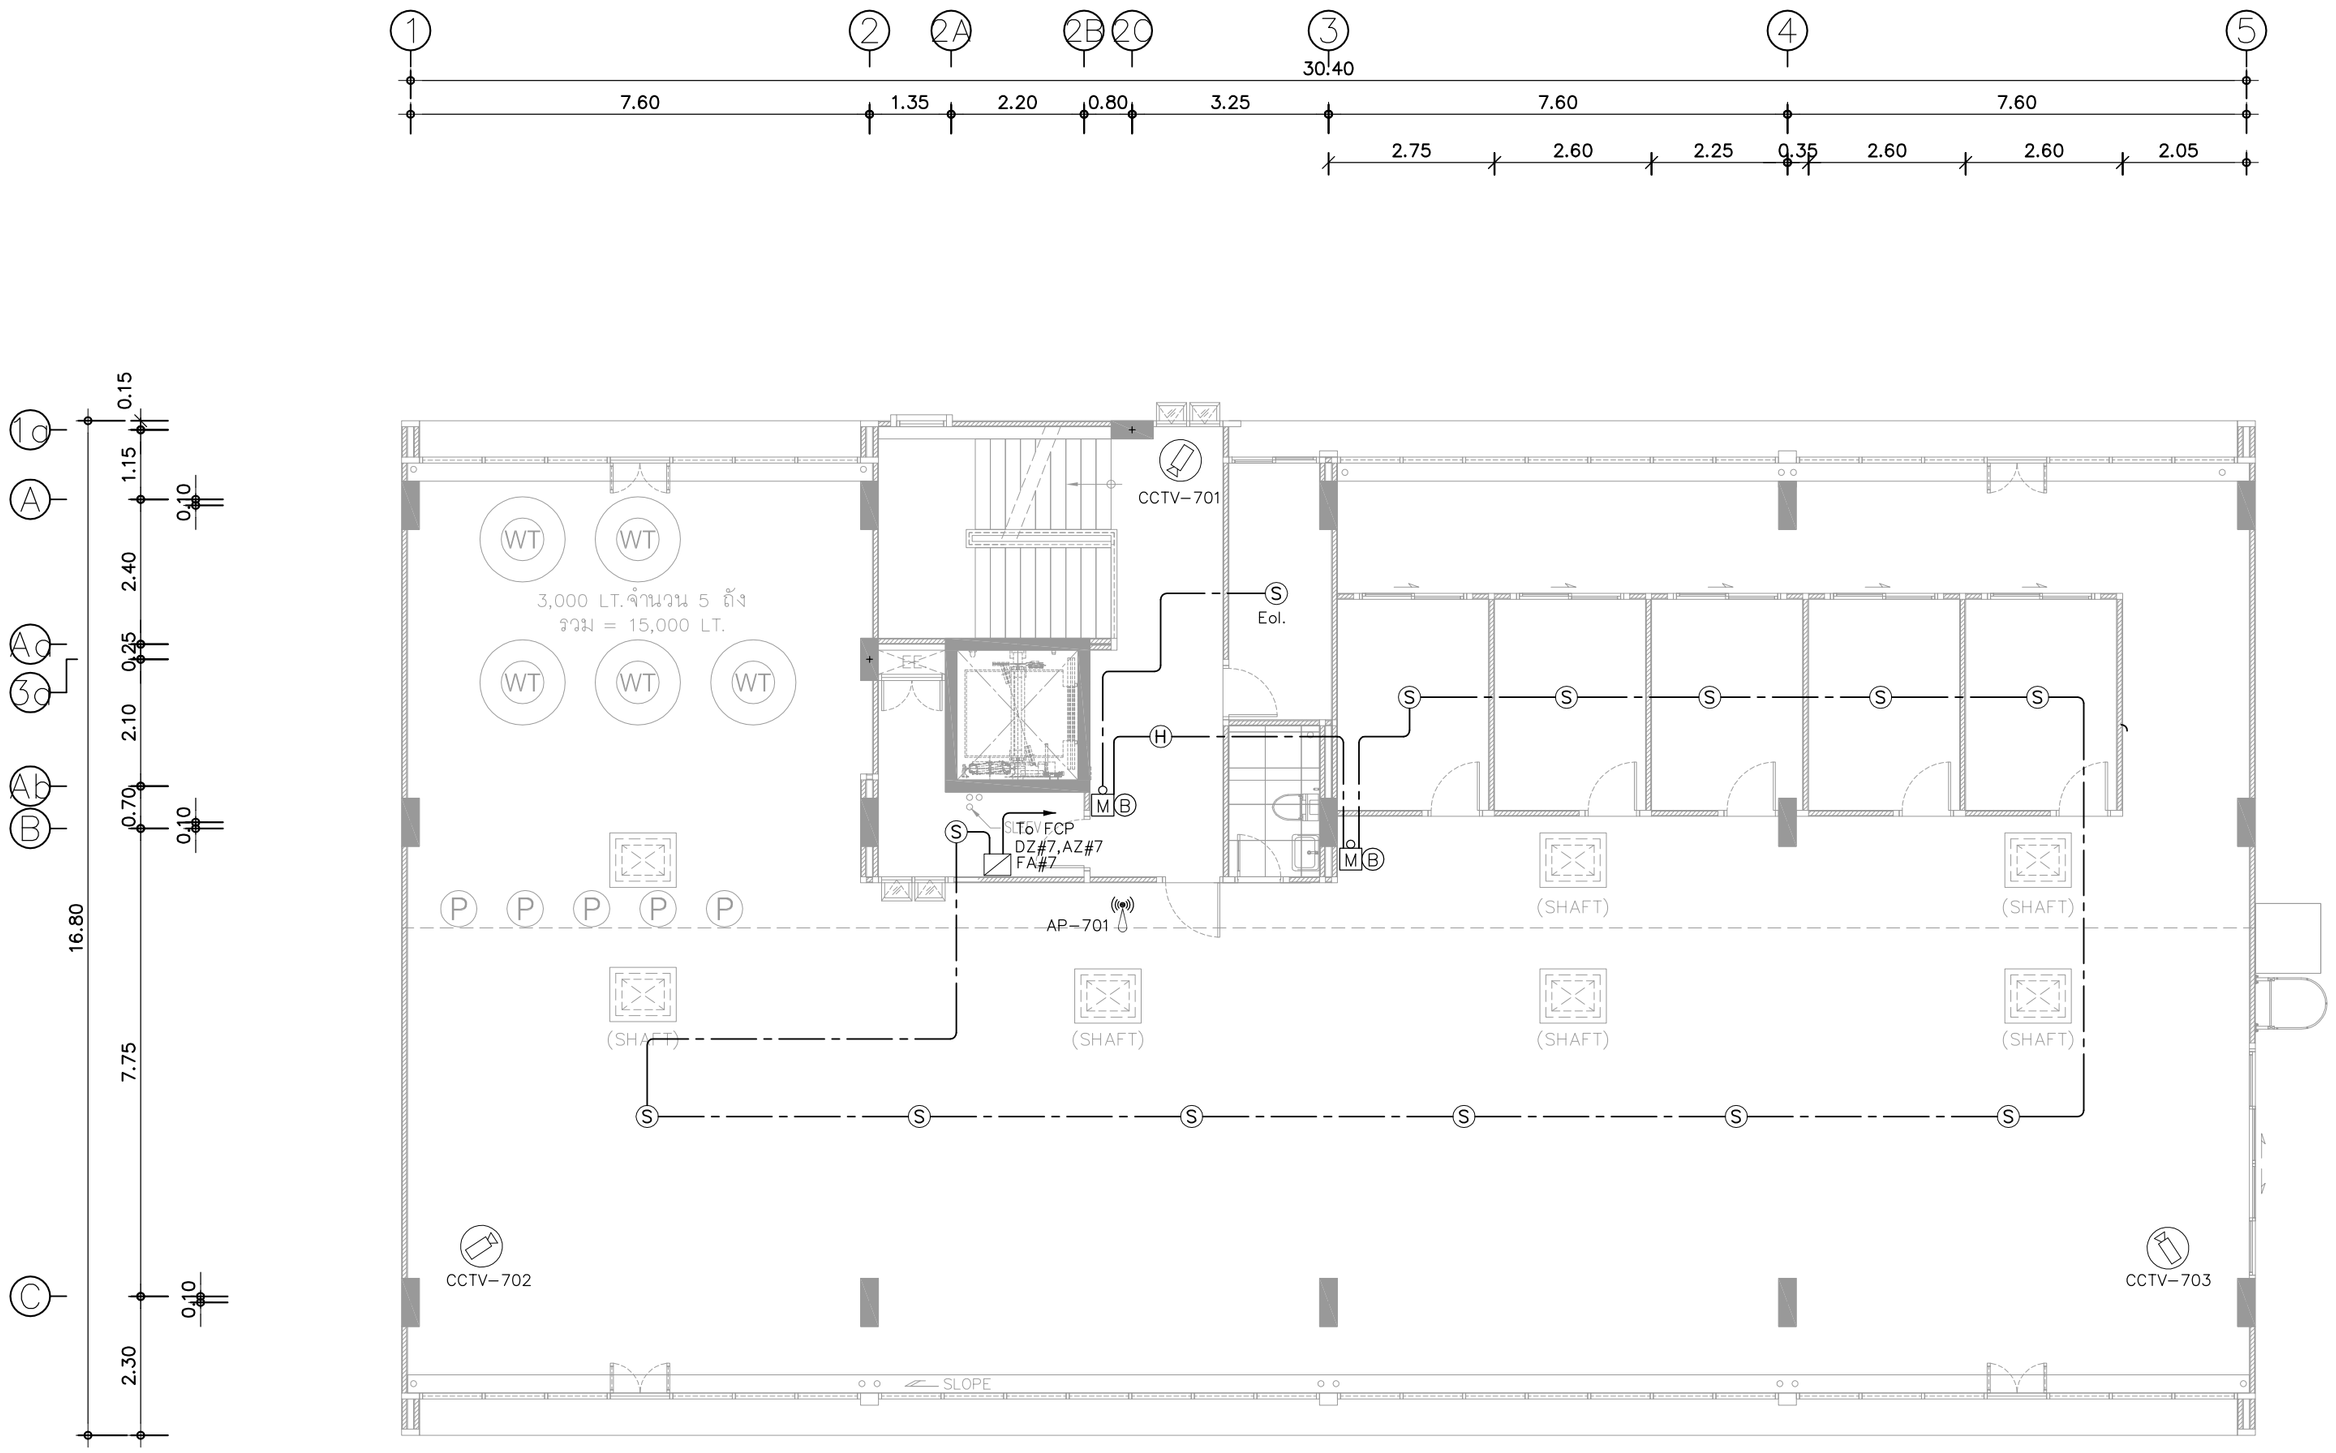

แปลนแสดงระบบสัญญาณแจ้งเหตุเพลิงไหม้ , กล้องวงจรปิด , Access Point ชั้น 7 ห้องใต้หลังคา

SCALE 1:100

PROJECT NUMBER : VC2023-024

PROJECT

MACHI RESIDENCES

อาคารพักอาศัยรวม ค.ส.ล 7 ชั้น

OWNER

บริษัท ฤทธิกร ลิฟวิ่ง จำกัด

ARCHITECT :

อัคคะภัทร์ จิระอารียบุตร ส-สถ.3040

403 ซ.พัฒนาการ 50 พัฒนาการ

กรุงเทพมหานคร 10250

INTERIOR DESIGNER :

-

STRUCTURAL ENGINEER :

นายพงษ์ธวิทย์ คทาวุธเจริญกุล ลย.12291

ELECTRICAL ENGINEER :

นายภาคภูมิ คำพิทูรย์ ลฟก.5587

MECHANICAL ENGINEER :

SANITARY ENGINEER :

นส.อรวรรณ พลตรี ลส.134

DRAWING TITLE

แปลนแสดงระบบสัญญาณแจ้งเหตุเพลิงไหม้

กล้องวงจรปิด , Access Point ชั้น 7 ห้องใต้หลังคา

DRAWING FOR CONSTRUCTION


DRAW BY :	CHECKER :	REVISION :
Weerayuth L.	Akapatr C.	-

SCALE :	DRAWING NO.
1 : 100	EE-20
DATE : 20-10-2024	
FILE NAME :	JOB NO.

REVISION	DESCRIPTION

GERNERAL NOTE
DO NOT SCALE DRAWING ALL MEASUREMENT MUST BE
CHECKED AT THE SIDE BY THE CONTRACTOR
ALL DESIGN AND DRAWINGS ARE THE PROPERTY OF
MARCHTEN CO.,LTD
AND NOT BE USED WITH OUT THEIR WRITTEN PERMISSION

MARCHTEN
ARCHITECTURE / INTERIOR
บริษัท มาร์ชเทน จำกัด
403 ซ.พัฒนาการ 50 สวนหลวง กรุงเทพมหานคร 10250

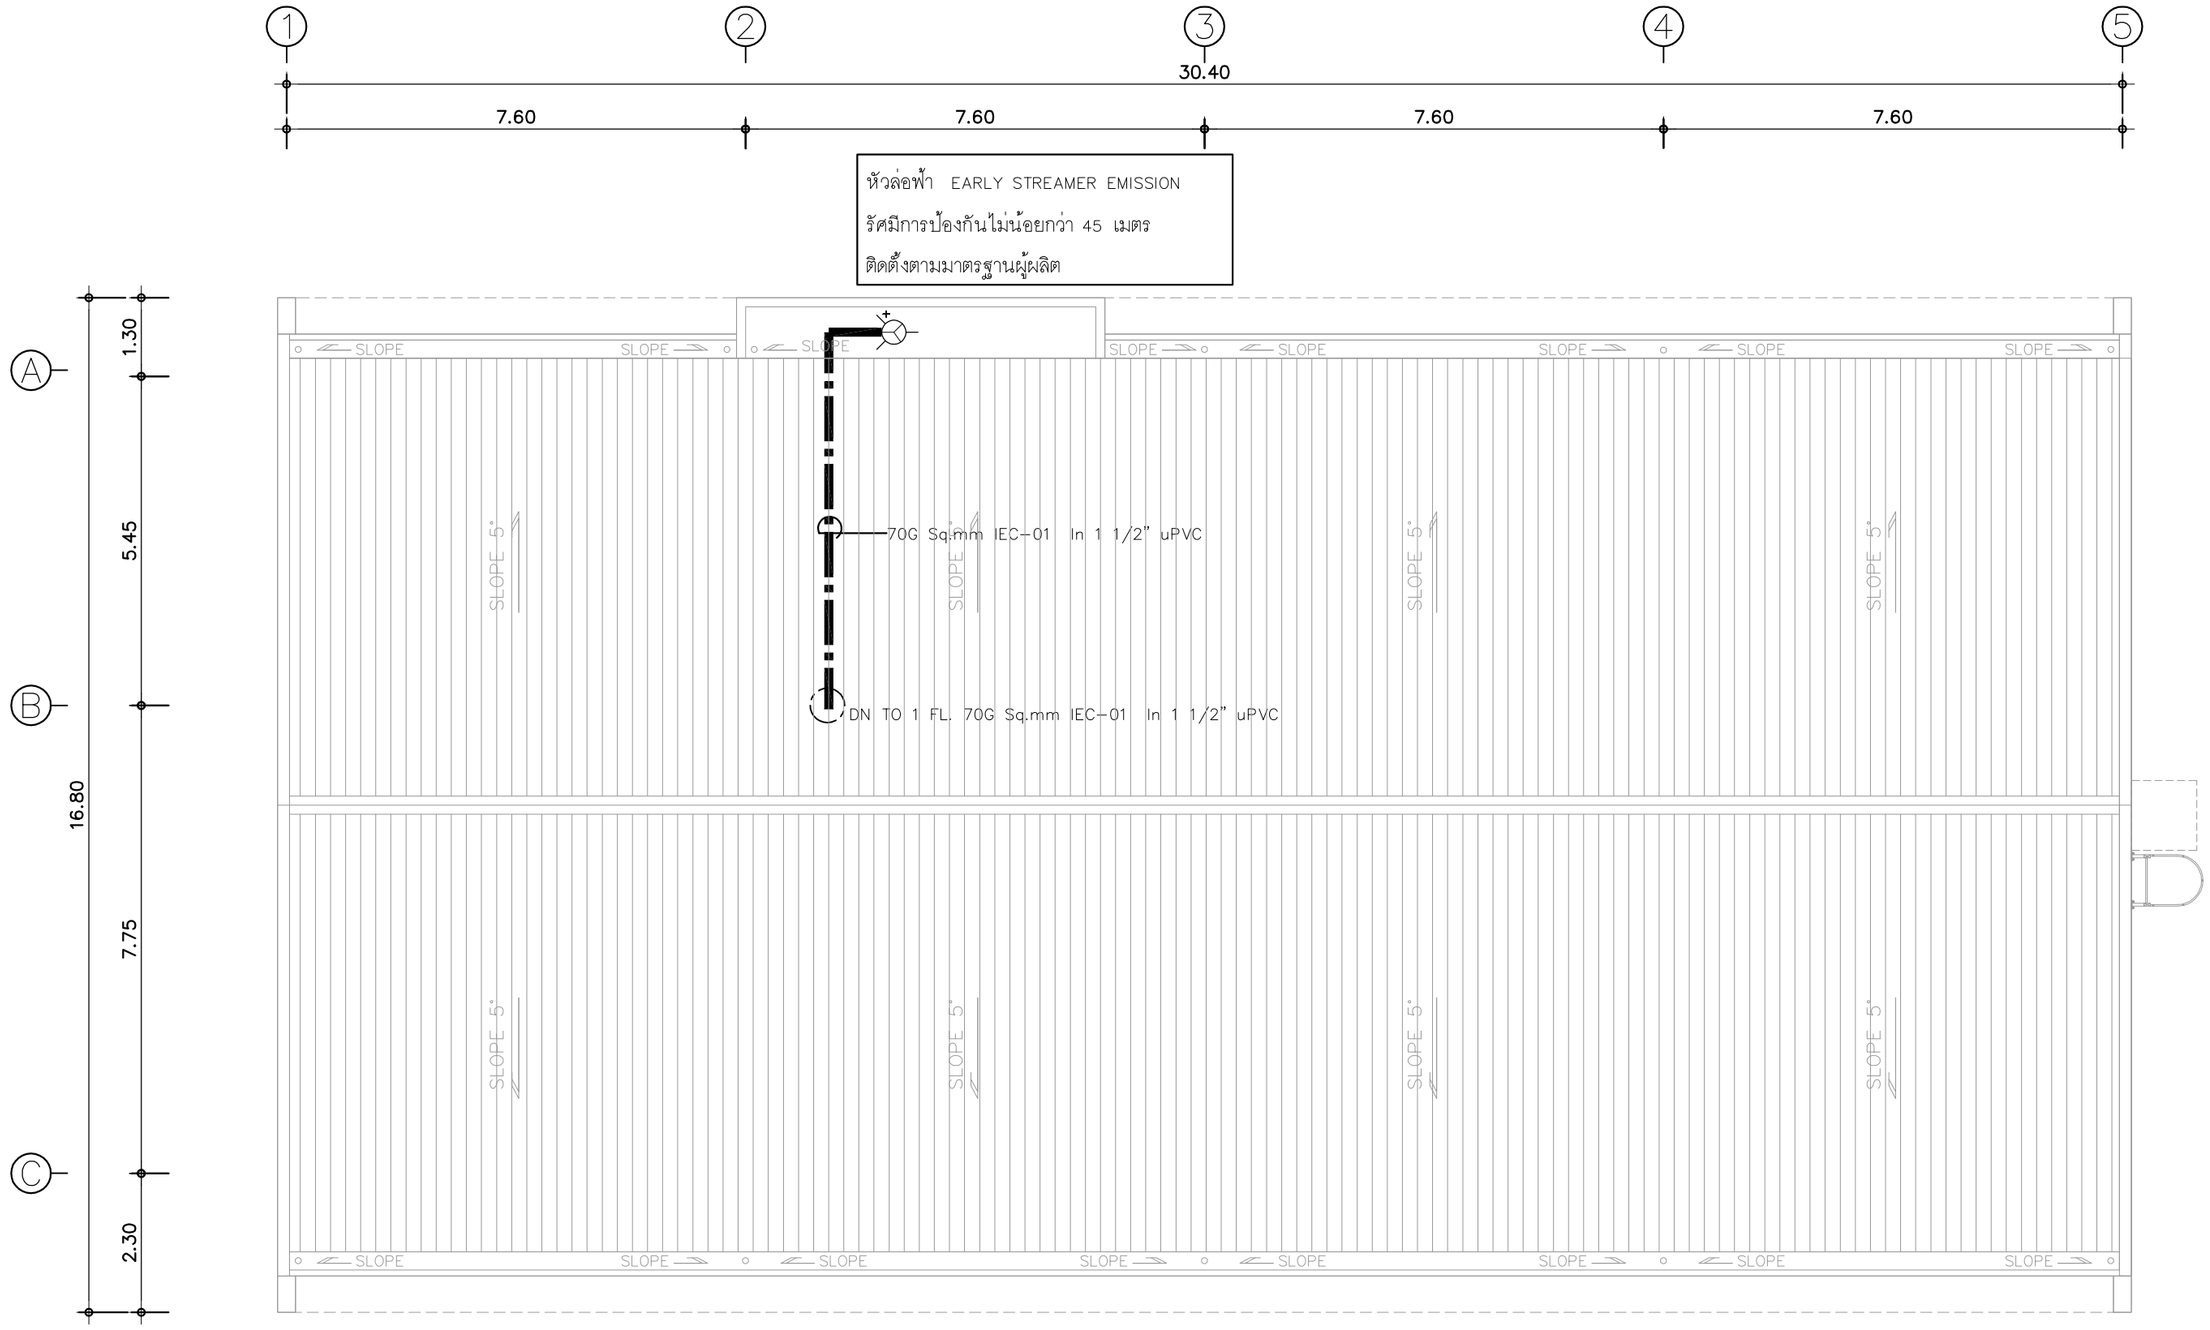

แปลนแสดงระบบล่อฟ้า

SCALE 1:100

PROJECT NUMBER : VC2023-024

PROJECT

MACHI RESIDENCES

อาคารพักอาศัยรวม ค.ส.ล 7 ชั้น

OWNER

บริษัท ฤทธิกร ลิฟวิ่ง จำกัด

ARCHITECT :

อัคคะภัทร์ จิระอารียบุตร ส-สถ.3040

403 ซ.พัฒนาการ 50 พัฒนาการ

กรุงเทพมหานคร 10250

INTERIOR DESIGNER :

-

STRUCTURAL ENGINEER :

นายพงษ์ธวิทย์ คทาวุธเจริญกุล ลย.12291

ELECTRICAL ENGINEER :

นายภาคภูมิ คำพิทูรย์ ลฟก.5587

MECHANICAL ENGINEER :

SANITARY ENGINEER :

นส.อรวรรณ พลตรี ลส.134

DRAWING TITLE

แปลนแสดงระบบล่อฟ้า

DRAWING FOR CONSTRUCTION

DRAW BY :	CHECKER :	REVISION :
Weerayuth L.	Akapatr C.	-

SCALE :	DRAWING NO.
1 : 100	EE-21
DATE : 20-10-2024	
FILE NAME :	JOB NO.


REVISION	DESCRIPTION

GERNERAL NOTE
DO NOT SCALE DRAWING ALL MEASUREMENT MUST BE
CHECKED AT THE SIDE BY THE CONTRACTOR
ALL DESIGN AND DRAWINGS ARE THE PROPERTY OF
MARCHTEN CO.,LTD
AND NOT BE USED WITH OUT THEIR WRITTEN PERMISSION

MARCHTEN

ARCHITECTURE / INTERIOR

บริษัท มาร์ชเทน จำกัด
403 ซ.พัฒนาการ 50 สวนหลวง กรุงเทพมหานคร 10250

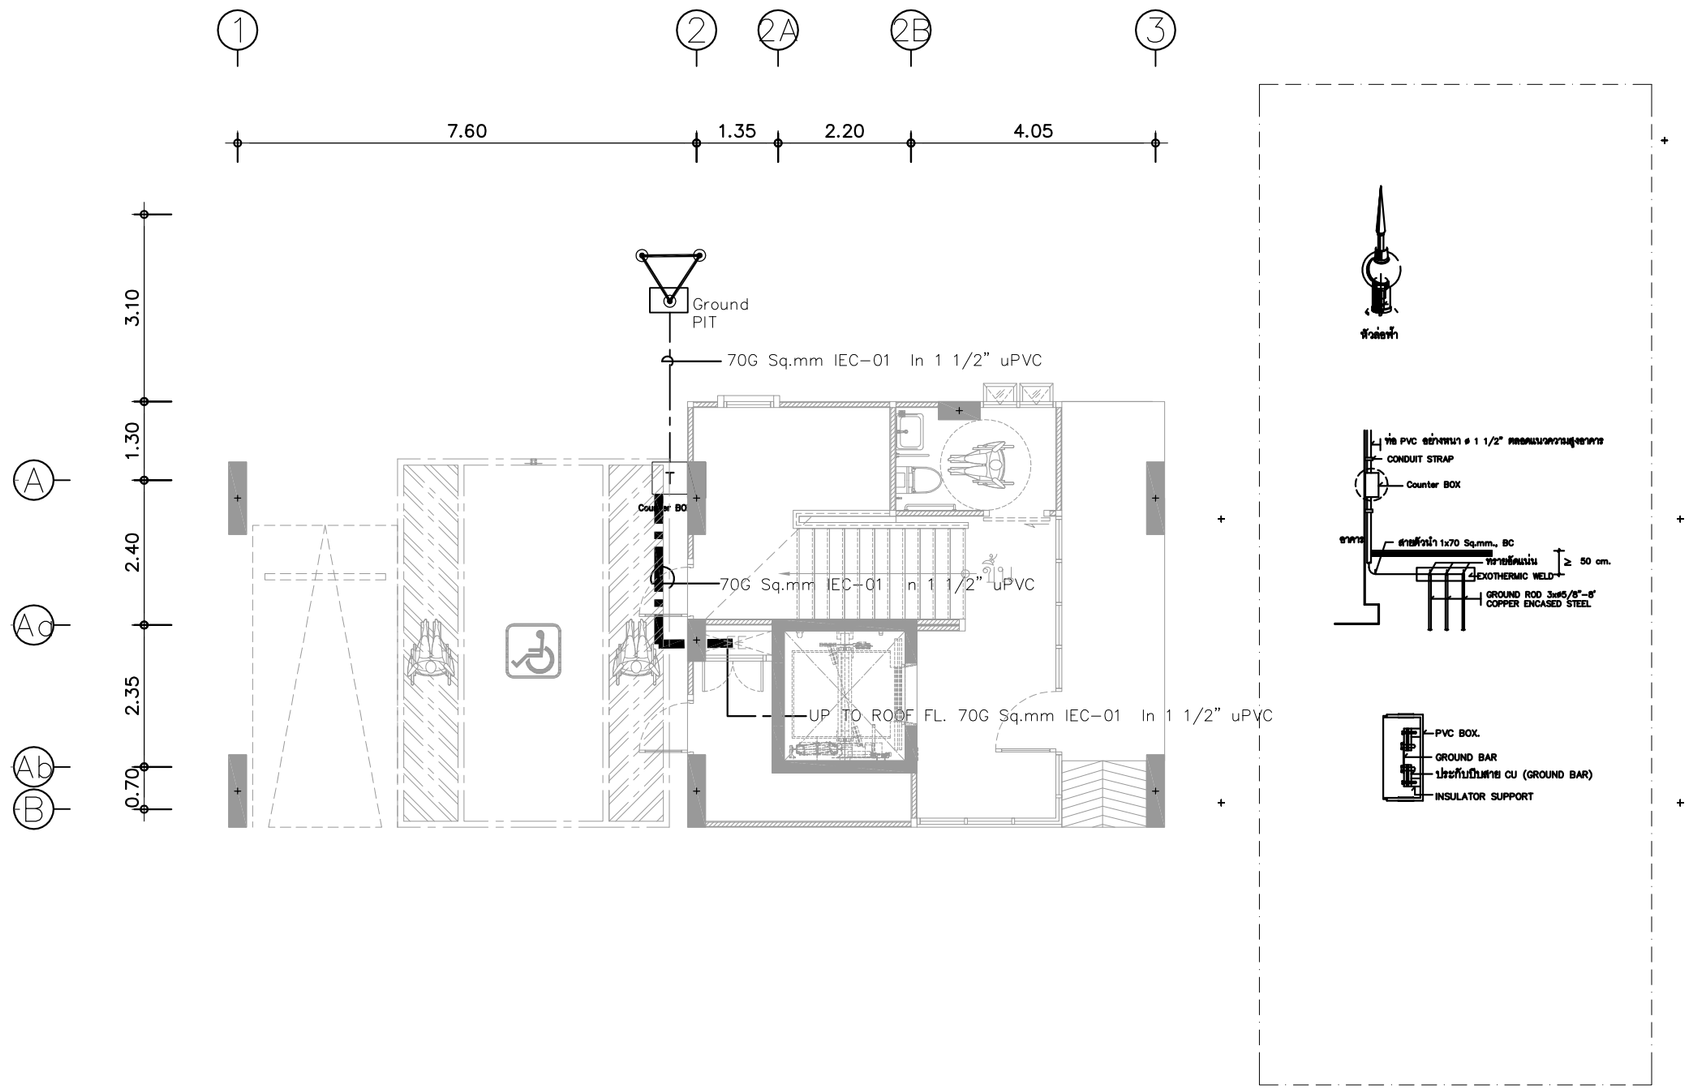

TYPICAL DETAIL OF LIGHTNING PROTECTION

PROJECT NUMBER : VC2023-024

PROJECT

MACHI RESIDENCES

อาคารพักอาศัยรวม ค.ส.ล 7 ชั้น

OWNER

บริษัท ฤทธิกร ลิฟวิ่ง จำกัด

ARCHITECT :

อัคคะภัทร์ จิระอารียบุตร ส-สถ.3040

403 ซ.พัฒนาการ 50 พัฒนาการ

กรุงเทพมหานคร 10250

INTERIOR DESIGNER :

-

STRUCTURAL ENGINEER :

นายพงษ์ธวิทย์ คทาวุธเจริญกุล ลย.12291

ELECTRICAL ENGINEER :

นายภาคภูมิ คำพิทูรย์ ลฟก.5587

MECHANICAL ENGINEER :

SANITARY ENGINEER :

นส.อรวรรณ พลตรี ลส.134

DRAWING TITLE

TYPICAL DETAIL OF

LIGHTNING PROTECTION

DRAWING FOR CONSTRUCTION

DRAW BY :	CHECKER :	REVISION :
Weerayuth L.	Akapatr C.	–

SCALE :	DRAWING NO.
1 : 100	EE-22
DATE : 20-10-2024	
FILE NAME :	JOB NO.


REVISION	DESCRIPTION

GERNERAL NOTE
DO NOT SCALE DRAWING ALL MEASUREMENT MUST BE
CHECKED AT THE SIDE BY THE CONTRACTOR
ALL DESIGN AND DRAWINGS ARE THE PROPERTY OF
MARCHTEN CO.,LTD
AND NOT BE USED WITH OUT THEIR WRITTEN PERMISSION


MARCHTEN

ARCHITECTURE / INTERIOR


บริษัท มาร์ชเทน จำกัด
403 ซ.พัฒนาการ 50 สวนหลวง กรุงเทพมหานคร 10250

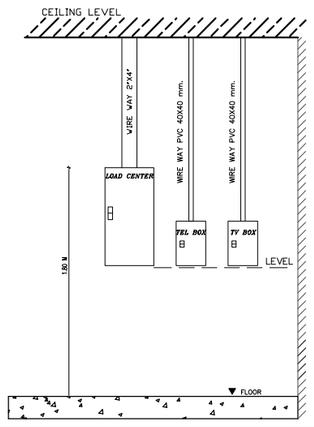


DETAIL LOAD CENTER,TV.TEL BOX
STORE ROOM

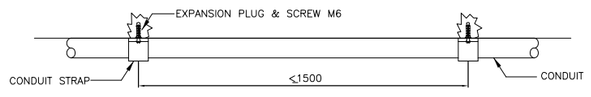


CONDUIT INSTALLATION ON CONCRETE SURFACE

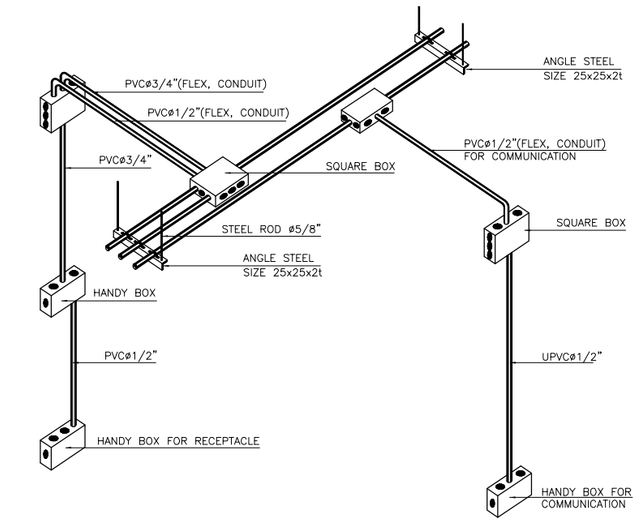


DETAIL OF BRANCH CONDUIT INSTALLATION

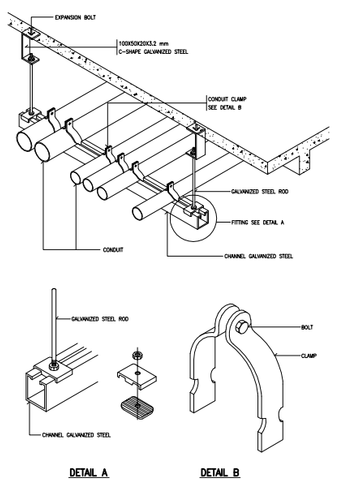

MULTIPLES CONDUIT SUPPORT

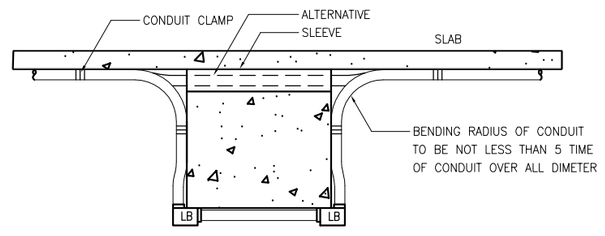

CONDUIT THROUGH BEAM INSTALLATION

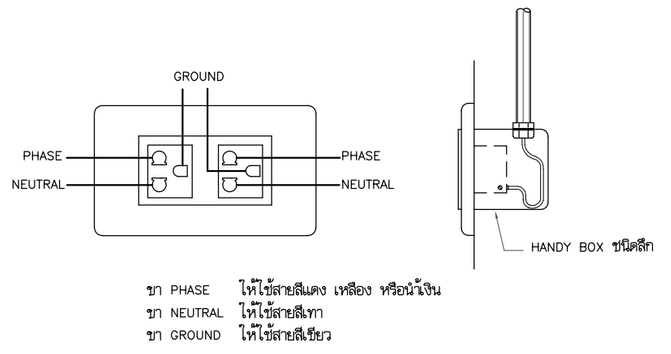

ขา PHASE ให้ใช้สายสีแดง เหลือง หรือน้ำเงิน
ขา NEUTRAL ให้ใช้สายสีเทา
ขา GROUND ให้ใช้สายสีเขียว

DETAIL POWER SOCKET INSTALLATION

INSTALLATION 1
SCALE NTS

PROJECT NUMBER : VC2023-024

PROJECT

MACHI RESIDENCES
อาคารพักอาศัยรวม ค.ส.ล 7 ชั้น

OWNER

บริษัท ฤทธิกร ลิฟวิ่ง จำกัด

ARCHITECT :

อัคคะภัทร์ จิระอารียบุตร ส-สถ.3040
403 ซ.พัฒนาการ 50 พัฒนาการ
กรุงเทพมหานคร 10250

INTERIOR DESIGNER :

-

STRUCTURAL ENGINEER :

นายพงษ์ธวิทย์ คทาวุธเจริญกุล ลย.12291

ELECTRICAL ENGINEER :

นายภาคภูมิ คำพิทรย์ ลฟก.5587

MECHANICAL ENGINEER :

SANITARY ENGINEER :

พล.อรวรรณ พลตรี ลส.134

DRAWING TITLE

INSTALLATION 1

DRAWING FOR CONSTRUCTION

DRAW BY :	CHECKER :	REVISION :
Weerayuth L.	Akapatr C.	-


SCALE :	DRAWING NO.
1 : 100	EE-23
DATE : 20-10-2024	
FILE NAME :	JOB NO.

REVISION	DESCRIPTION


GERNERAL NOTE
DO NOT SCALE DRAWING ALL MEASUREMENT MUST BE
CHECKED AT THE SIDE BY THE CONTRACTOR
ALL DESIGN AND DRAWINGS ARE THE PROPERTY OF
MARCHTEN CO.,LTD
AND NOT BE USED WITH OUT THEIR WRITTEN PERMISSION

MARCHTEN
ARCHITECTURE / INTERIOR


บริษัท มาร์ชเทน จำกัด
403 ซ.พัฒนาการ 50 สวนหลวง กรุงเทพมหานคร 10250

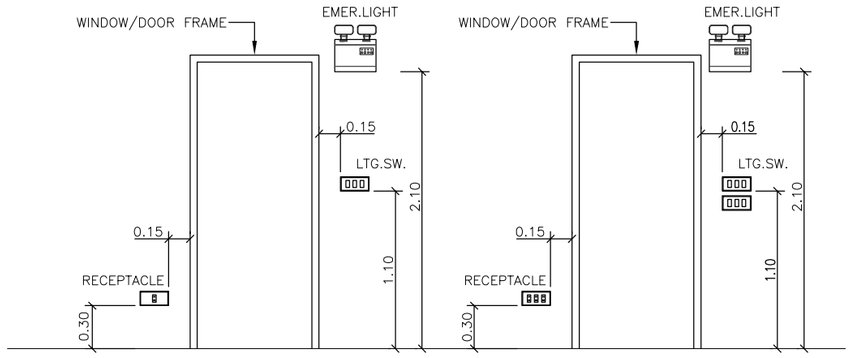


SWITCH, RECEPTACLE TELEPHONE AND TV OUTLET INSTALLATION

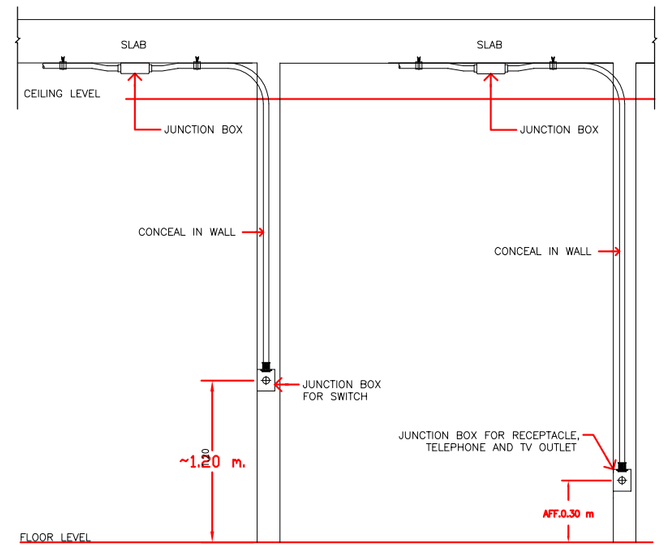


SWITCH, RECEPTACLE INSTALLATION

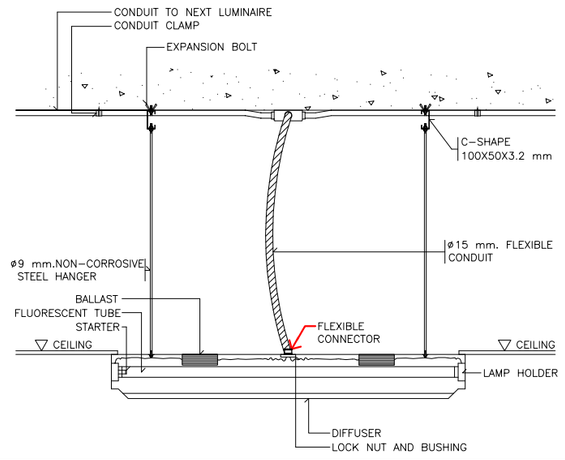

LIGHTING FIXTURE INSTALLATION (SURFACED TYPE)

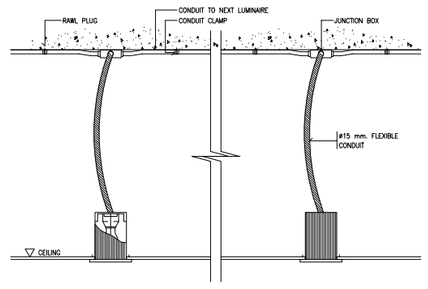

RECESSED DOWNLIGHT LUMINAIRE INSTALLATION DETAIL

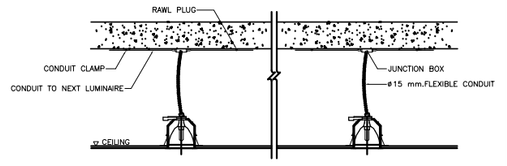

DETAIL FLEX. CONDUIT WITH LIGHTING FIXTURE

INSTALLATION 2

SCALE NTS

PROJECT NUMBER : VC2023-024

PROJECT

MACHI RESIDENCES

อาคารพักอาศัยรวม ค.ส.ล 7 ชั้น

OWNER

บริษัท ฤทธิกร ลิฟวิ่ง จำกัด

ARCHITECT :

อัคคะภัทร์ จิระอารียบุตร ส-สถ.3040

403 ซ.พัฒนาการ 50 พัฒนาการ

กรุงเทพมหานคร 10250

INTERIOR DESIGNER :

-

STRUCTURAL ENGINEER :

นายพงษ์ธวิทย์ คทาวุธเจริญกุล ลย.12291

ELECTRICAL ENGINEER :

นายภาคภูมิ คำพิทรย์ ลฟก.5587

MECHANICAL ENGINEER :

SANITARY ENGINEER :

พล.อรวรรณ พลตรี ลส.134

DRAWING TITLE

INSTALLATION 2

DRAWING FOR CONSTRUCTION

DRAW BY :	CHECKER :	REVISION :
Weerayuth L.	Akapatr C.	-

SCALE :	DRAWING NO.
1 : 100	EE-24
DATE : 20-10-2024	
FILE NAME :	JOB NO.

REVISION	DESCRIPTION

GERNERAL NOTE
DO NOT SCALE DRAWING ALL MEASUREMENT MUST BE
CHECKED AT THE SIDE BY THE CONTRACTOR
ALL DESIGN AND DRAWINGS ARE THE PROPERTY OF
MARCHTEN CO.,LTD
AND NOT BE USED WITH OUT THEIR WRITTEN PERMISSION

MARCHTEN

ARCHITECTURE / INTERIOR

บริษัท มาร์ชเทน จำกัด
403 ซ.พัฒนาการ 50 สวนหลวง กรุงเทพมหานคร 10250