สารบัญแบบระบบสุขาภิบาล

หมายเลขแบบ	รายละเอียด
SN – 01	สารบัญแบบและสัญลักษณ์
	รายการประกอบแบบวิศวกรรมสุขาภิบาล
SN – 02	ไดอะแกรมระบบจ่ายน้ำประปา
SN – 03	ไดอะแกรมระบบดับเพลิง (ระบบท่อแห้ง)
SN – 04	ไดอะแกรมระบบรวบรวมน้ำเสีย
SN – 05	ไดอะแกรมระบบระบายน้ำฝน
SN – 06	ผังระบบสุขาภิบาล (น้ำดี) ชั้น 1
SN – 07	ผังระบบสุขาภิบาล (น้ำดี) ชั้น 2
SN – 08	ผังระบบสุขาภิบาล (น้ำดี) ชั้น 3
SN – 09	ผังระบบสุขาภิบาล (น้ำดี) ชั้น 4 – 5
SN – 10	ผังระบบสุขาภิบาล (น้ำดี) ชั้น 6
SN – 11	ผังระบบสุขาภิบาล (น้ำดี) ชั้นใต้หลังคา
SN – 12	ผังระบบสุขาภิบาล (น้ำทิ้ง) ชั้น 1
SN – 13	ผังระบบสุขาภิบาล (น้ำทิ้ง) ชั้น 2
SN – 14	ผังระบบสุขาภิบาล (น้ำทิ้ง) ชั้น 3 – 5
SN – 15	ผังระบบสุขาภิบาล (น้ำทิ้ง) ชั้น 6
SN – 16	ผังระบบสุขาภิบาล (น้ำทิ้ง) ชั้นใต้หลังคา
SN – 17	ผังระบบสุขาภิบาล (น้ำทิ้ง) ชั้นหลังคา
SN – 18	แบบขยายถังสำรองน้ำประปา ขนาด 5 ลูกบาศก์เมตร
	แบบขยายถังสำรองน้ำประปา ขนาด 3 ลูกบาศก์เมตร
SN – 19	แบบขยายถังบำบัดน้ำเสียสำเร็จรูป
	ขนาด 25 ลูกบาศก์เมตรต่อวัน
SN – 20	แบบขยายห้องน้ำ
SN – 21	แบบขยายห้องน้ำ
SN – 22	แบบมาตรฐานงานวิศวกรรมสุขาภิบาล 1
SN – 23	แบบมาตรฐานงานวิศวกรรมสุขาภิบาล 2
SN – 24	แบบมาตรฐานงานวิศวกรรมสุขาภิบาล 3
SN – 25	แบบมาตรฐานงานวิศวกรรมสุขาภิบาล 4

เครื่องหมายระบบสุขาภิบาล

เครื่องหมาย	รายละเอียด
S OR W	SOIL OR WASTE PIPE LINE
V	VENT PIPE LINE
CW	COLD WATER PIPE LINE
HW	HOT WATER PIPE LINE
	DRAIN PIPE LINE
RW	RAINWATER DRAIN LINE
	FLOW – IN DIRECTION OF ARROW
	PITCH DOWN IN DIRECTION OF ARROW
	ELBOW 90°
	ELBOW TURN UP
	ELBOW TURN DOWN
	TEE
	TEE TURN UP
	TEE TURN DOWN
	CONNECTION BOTTOM
	CONNECTION TOP
	LATERAL
	ELBOW 45°
	UNION
FD. OR SD.	FLOOR DRAIN OR SHOWER DRAIN
FCO.	FLOOR CLEANOUT
	CLEANOUT OR PLUG
FCO.	FLOOR CLEANOUT
FD. OR SD.	FLOOR DRIAN OR SHOWER DRAIN
HB.	HOSE BIBB
	AIR CHAMBER
LAV. OR UR.	LAVATORY OR URINAL
	CAP ON END OF PIPE
WC.	WATER CLOSET
	VENT THRU ROOF
	GATE VALVE
	GLOBE VALVE
	BUTTERFLY VALVE
	CHECK VALVE
	FLOAT VALVE
	FOOT VALVE W/STRAINER
PRV.	PRESSURE REGULATING VALVE
M	WATER METER
	FLEXIBLE CONNECTOR
PG.	PRESSURE GAUGE
	STRAINER BLOW OFF
A	DRAINAGE MANHOLE INDICATED TYPE A
ILPCM	INLET LEVEL OF PIPE CONNECTED TO MANHOLE
U 0.30	U–GUTTER 0.30 M. WIDE
ø 0.30 RCP	REINFORCED CONCRETE PIPE ø 0.30 M.
	PUMP
	SIAMESE CONNECTION W/CHECK VALVE
FHC.	FIRE HOSE CABINET , FHC.
BP.	BOOSTER PUMP
FS.	FLOW SWITCH
	WATER PUMP
	WATER CLOSET , FLUSH VALVE
	WATER CLOSET , FLUSH TANK

อักษรย่อ (ABBREVIATION)

เครื่องหมาย	รายละเอียด
S	SOIL PIPE
W	WASTE PIPE
V	VENT PIPE
CW	COLD WATER PIPE
SP	SOFT PIPE
FD	FLOOR DRAIN
FCO	FLOOR CLEANOUT
CO	CLEANOUT
WC	WATER CLOSET
LAV	LAVATORY
BD	BIDET
SH	SHOWER
SS	SERVICE SINK
KS	KITCHEN SINK
UR	URINAL
RL	ROOF LEADER
RW	RAINWATER DRAIN
P	PUMP
HB	HOSE BIBB
MIN	MINIMUM
MAX	MAXIMUM
VTR	VENT THRU ROOF
LEV	LEVEL
FLR	FLOOR
MWWA	METROPOLITAN WATER WORKS AUTHORITY
CIP	CAST IRON PIPE
GSP	GALVANIZED STEEL PIPE
PVC	POLYVINYL CHLORIDE PIPE
ACP	ASBESTOS CEMENT PIPE
GRP	GLASSFIBER REINFORCEMENT PIPE
MH	MANHOLE
W/	WITH
FC	FAUCET
BT	BATHTUB
HW	HOT WATER PIPE
SD	SHOWER DRAIN
RD	ROOF DRIAN
SP	SEWAGE PUMP
NTS	NOT TO SCALE
A/C	ABOVE CEILING
B/F	BELOW FLOOR
UR.	URINAL
LAV.	LAVATORY
	DRY CHEMICAL FIRE EXTINGUISHER, 6A:10BC
	4.5 kg AND LEAST UL RATING 6A:10BC
	CO2 FIRE EXTINGUISHER,
	4.5 kg AND LEAST UL RATING 10 B:C
FHC	FIRE HOSE CABINET
	FIRE DEPARTMENT CONNECTOR

PLUMBING FIXTURE PIPING SCHEDULE

FIXTURE	CW PIPE ø INCH	HW PIPE ø INCH	S PIPE ø INCH	W PIPE ø INCH	V PIPE ø INCH
HOSE BIBB	3/4	–	–	–	–
LAVATORY	1/2	–	–	2	1½
KITCHEN SINK	1/2	–	–	2	1½
SHOWER	1/2	–	–	–	1½
URINAL FLUSH VALVE	3/4	–	2	–	1½
WATER CLOSET FLUSH VALVE	1	–	4	–	2
WATER CLOSET FLUSH TANKS TYPE "A" (WESTERN TYPE)	1/2	–	4	–	2
WATER CLOSET TYPE "B" (EASTERN TYPE)	1/2	–	4	–	2
FLEXIBLE HOSE FOR CLOSET	1/2	–	–	–	–
HOSE BIBB	1/2	–	–	–	–

หมายเหตุทั่วไป (GENERAL NOTES)

1. ท่อน้ำโลหะและท่อระบายน้ำทิ้ง ภายในและภายนอกอาคาร ใช้ PVC CLASS 8.5 ตามมาตรฐานอุตสาหกรรม มอก. 17–2523
2. ท่อระบายอากาศ ใช้ PVC CLASS 8.5 ตามมาตรฐานอุตสาหกรรม มอก. 17–2532
3. ท่อประปา ภายในและภายนอกอาคาร ใช้ PVC CLASS 13.5 ตามมาตรฐานอุตสาหกรรม มอก. 17–2532
4. ท่อประปาที่จำเป็นต้องมีการหักงอในแนวดิ่ง จะต้องเพิ่มจำนวน AIR VALVE ในจุดที่สูงที่สุดของท่อบริเวณนั้นด้วย
5. ในทุกข้อต่อ ข้องอ ของการวางท่อประปา และท่อระบายน้ำเสีย จะต้องมีสมอดอนกรีตรับท่อเสมอ
6. ท่อระบายน้ำฝนภายนอกอาคารใช้ท่อคอนกรีตเสริมเหล็ก
7. ชุดมาตรวัดน้ำพร้อมประตูน้ำให้ใช้ตามมาตรฐานของการประปาภูมิภาค
8. ท่อระบายน้ำที่ต่อออกจากอ่างล้างมือ และท่อระบายน้ำพื้น จะต้องติดที่ดักกลิ่น
9. ปลายท่อระบายก๊าซ (ท่อ VENT) จะต้องยกให้สูงกว่าระดับหลังคาสูงสุดอย่างน้อย 15 ซม. และติดตะแกรงกันแมลงที่ปลายท่อ
10. ท่อระบายน้ำจะต้องมีความลาดเอียงอย่างน้อย เท่า100 จากจุดขัดขวางที่ใกล้ท่อดิ่ง
11. การตัดท่อ ต้องตัดให้ได้ระยะพอดีในการบรรจบท่อ ปลายท่อที่ตัดต้องทำการคว้านขุดเศษวัสดุที่ติดค้างออกให้หมด และปลายท่อที่จะทำการบรรจบ จะต้องละอาดเรียบลื่นเสมอ
12. การเดินท่อต้องเดินให้ประณีต เรียบร้อยเป็นระเบียบมีแนวลำเลยไม่เลี้ยวคดไปมา และควรจะเดินในช่องท่อ เหนือฝ้าหรือในผนัง
13. ปลายท่อที่เดินค้างไว้ เมื่องานไม่เสร็จ จะต้องใช้ปลั๊กอุดไว้
14. อุปกรณ์ และอุปกรณ์ประกอบจะต้องมีการหุ้มหรือคลุม เพื่อป้องกันไม่ให้ชำรุด หรือบุบสลายขณะที่งานยังไม่เสร็จสิ้น
15. ให้ติดตั้งสายชำระเป็นอุปกรณ์ประกอบโถสุขภัณฑ์ทุกตัว
16. ท่อที่จะต้องเจาะผ่านผนัง พื้นหรือคาน จะต้องมีปลอกร้อยท่อ (PIPE SLEEVE)ทำด้วยท่อเหล็กอาบสังกะสีขนาดตามระเบียบข้อกำหนดเฉพาะงาน ฝังอยู่ในส่วนของอาคารพอดีตรงที่จะต้องเจาะผ่าน หากพื้นนั้นมีการเปียกน้ำอยู่เสมอ เช่นเป็นพื้นห้องน้ำ หรือแผ่นพื้นหลังคา ปลอกร้อยท่อต้องเป็นชนิดกันซึมผ่าน ทั้งสีวด้านนอกและด้านในของปลอกร้อยท่อ และหากบริเวณปลอกร้อยท่อเป็นองค์อาคารด้วย จะต้องทำการสังเขปทำการเทคอนกรีตหล่อองค์อาคารส่วนนั้น
17. การยึดแขวนท่อ จะต้องมีเหล็กรัดท่อที่ผลิตขึ้นสำหรับใช้รัดท่อโดยเฉพาะตามขนาดท่อรัดไว้ สำหรับการแขวนท่อที่วิ่งแนวราบ ต้องมีเหล็กเส้นยึดไว้กับองค์อาคาร การยึดแขวนท่อจะทำไม่ได้โดยมีการประสานงานเตรียมการให้พร้อมไปกับการหล่อคอนกรีตองค์อาคาร ระยะห่างระหว่างจุดยึดแขวนท่อเป็นไปดังต่อไปนี้

17.1 ท่อแนวดิ่ง สำหรับท่อ PVC. จะต้องมีที่ยึด, รองรับหรือแขวนทุกๆ ระยะไม่เกิน 150 ซม. และทุกๆ รอยต่อ และทุกครึ่งหนึ่งของท่อแต่ละท่อน สำหรับท่อ PB ทุกๆ ระยะไม่เกิน 100 ซม.

17.2 ท่อแนวราบ สำหรับท่อ PVC. จะต้องมีที่ยึด, รองรับหรือแขวนทุกๆ ระยะไม่เกิน 100 ซม. และทุกๆ รอยต่อ และทุกๆ 40 ซม. สำหรับท่อ PB ขนาดของเหล็กเส้นที่ใช้แขวนท่อแนวราบ เป็นดังต่อไปนี้

ขนาดของท่อ	ขนาดของเหล็กเส้น
ø 1/2" – 1 1/4"	ø 9 มม.
ø 2" – 3"	ø 12 มม.
ø 4" – 5"	ø 15 มม.

18. เหล็กรัดท่อสำหรับยึดแขวนท่อ และเหล็กแขวนท่อจะต้องขัดสนิมออกให้หมดและทาสี RUST OLIUM หรือเทียบเท่าอย่างน้อย 2 ชั้น
19. การติดตั้งอุปกรณ์ประกอบระบบท่อ เช่น ประตูน้ำ, มาตร, เกจ์วัดแรงดัน, ยูเนี่ยนฯลฯ ต้องอยู่ในตำแหน่งที่เหมาะสมกับการใช้งาน และสะดวกที่จะถอดซ่อมบำรุงรักษาหรือเปลี่ยนใหม่
20. การทำความสะอาดระบบ ก่อนการส่งมอบงาน สุขภัณฑ์และอุปกรณ์ต่างๆ จะต้องได้รับการทำความสะอาด ระบบจ่ายน้ำจะต้องได้รับการทำความสะอาด ฆ่าเชื้อโรคตามวิธีที่ระบุในมาตรฐานท่อในอาคารของวิศวกรรมสถานแห่งประเทศไทย
21. ผู้รับเจ้างานจะต้องทดลองท่อตามข้อกำหนดในรายการประกอบแบบ และต้องล้างท่อตามข้อกำหนดก่อนการส่งจ่ายน้ำจริง

PROJECT NUMBER : VC2023–024

PROJECT

MACHI RESIDENCES

อาคารพักอาศัยรวม ค.ส.ล 7 ชั้น

OWNER

บริษัท ฤทธิกร ลิฟวิ่ง จำกัด

ARCHITECT :

อัคคะภัทร์ จิระอารีย์บุตร ส–สถ.3040

403 ซ.พัฒนาการ 50 พัฒนาการ

กรุงเทพมหานคร 10250

INTERIOR DESIGNER :

-

STRUCTURAL ENGINEER :

นายพงษ์ธวิทย์ คทาวุธเจริญกุล ลย.12291

ELECTRICAL ENGINEER :

นายภาคภูมิ คำพิทูรย์ ลพก.5587

MECHANICAL ENGINEER :

SANITARY ENGINEER :

น.ส.อรวรรณ พลตรี ลส.134

DRAWING TITLE

สารบัญแบบและสัญลักษณ์

รายการประกอบแบบวิศวกรรมสุขาภิบาล

DRAWING FOR CONSTRUCTION

DRAW BY :	CHECKER :	REVISION :
Weerayuth L.	Akapatr C.	–


SCALE :	DRAWING NO.
1 : 100	SN–01
DATE : 20–10–2024	
FILE NAME :	JOB NO.

REVISION	DESCRIPTION

GERNERAL NOTE
DO NOT SCALE DRAWING ALL MEASUREMENT MUST BE
CHECKED AT THE SIDE BY THE CONTRACTOR
ALL DESIGN AND DRAWINGS ARE THE PROPERTY OF
MARCHTEN CO.,LTD
AND NOT BE USED WITH OUT THEIR WRITTEN PERMISSION

ARCHITECTURE / INTERIOR

บริษัท มาร์ชเทน จำกัด
403 ซ.พัฒนาการ 50 สวนหลวง กรุงเทพมหานคร 10250

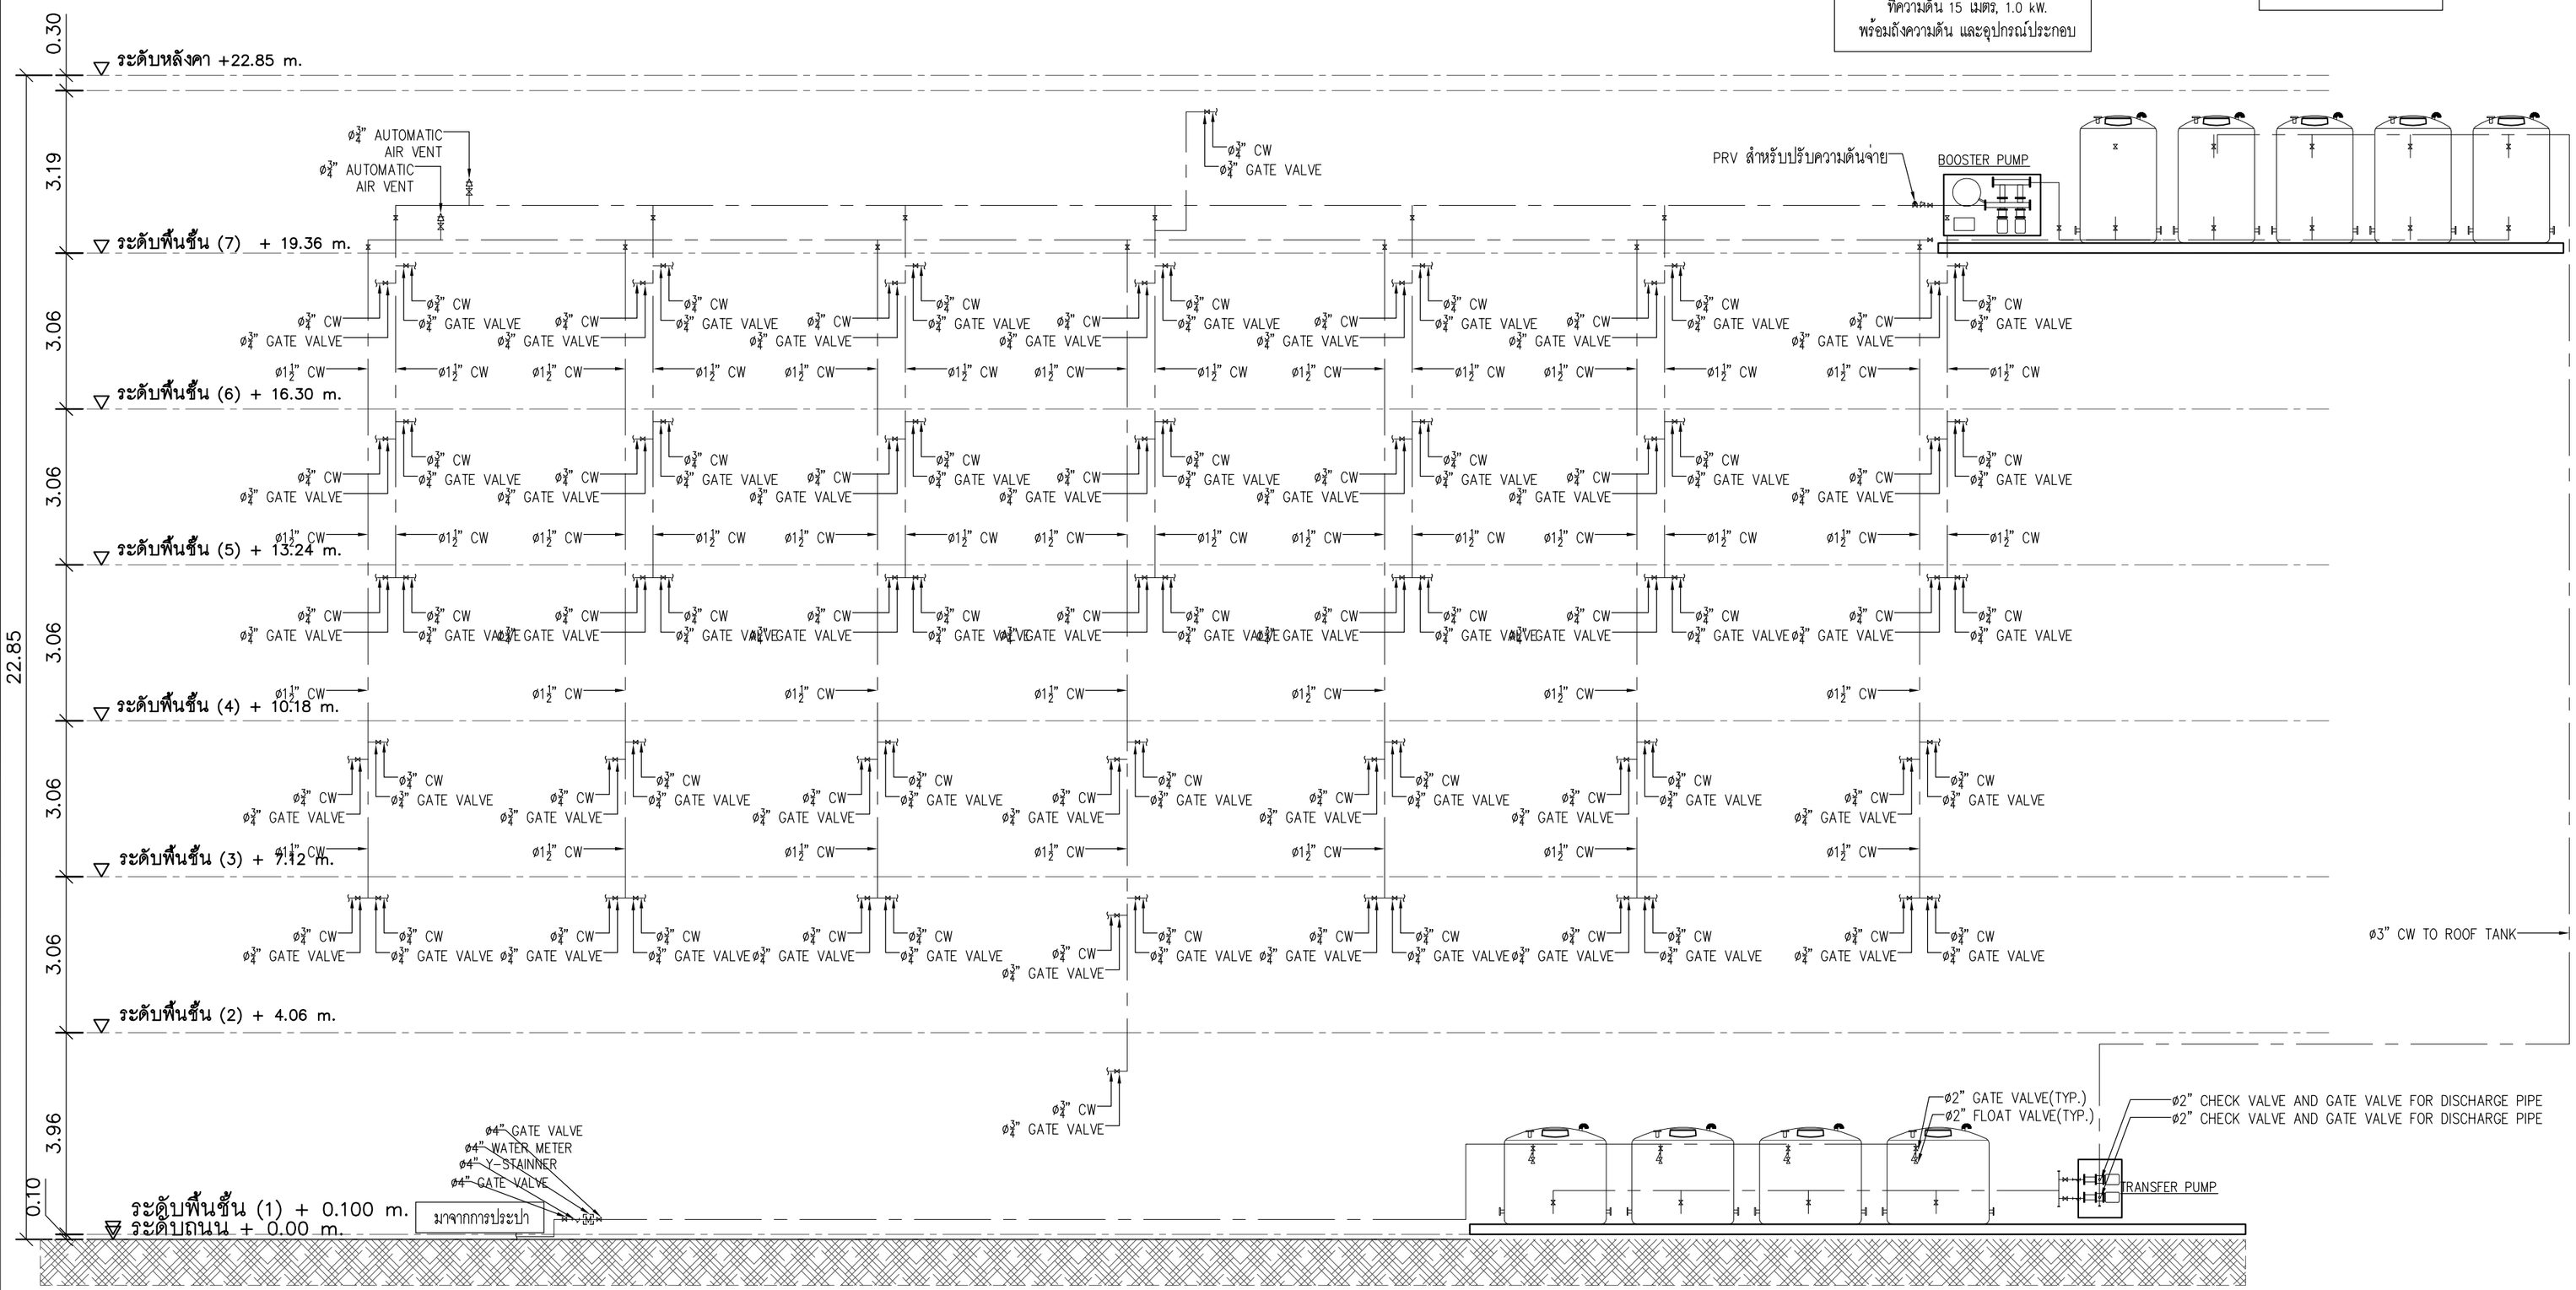

ไดอะแกรมระบบจ่ายน้ำประปา

SCALE NTS.

PROJECT NUMBER : VC2023–024

PROJECT

MACHI RESIDENCES

อาคารพักอาศัยรวม ค.ส.ล 7 ชั้น

OWNER

บริษัท ฤทธิกร ลิฟวิ่ง จำกัด

ARCHITECT :

อัคคะภัทร์ จิระอารีย์บุตร ส–สถ.3040

403 ซ.พัฒนาการ 50 พัฒนาการ

กรุงเทพมหานคร 10250

INTERIOR DESIGNER :

-

STRUCTURAL ENGINEER :

นายพงษ์ธวิทย์ คทาวุธเจริญกุล ลย.12291

ELECTRICAL ENGINEER :

นายภาคภูมิ คำพิทูรย์ ลฟก.5587

MECHANICAL ENGINEER :

SANITARY ENGINEER :

พล.อรวรรณ พลตรี ลส.134

DRAWING TITLE

ไดอะแกรมระบบจ่ายน้ำประปา

DRAWING FOR CONSTRUCTION

DRAW BY :	CHECKER :	REVISION :
Weerayuth L.	Akapatr C.	–

SCALE :	DRAWING NO.
1 : 100	SN–02
DATE : 20–10–2024	
FILE NAME :	JOB NO.

REVISION	DESCRIPTION

GERNERAL NOTE


DO NOT SCALE DRAWING ALL MEASUREMENT MUST BE **CHECKED AT THE SIDE BY THE CONTRACTOR**

ALL DESIGN AND DRAWINGS ARE THE PROPERTY OF MARCHTEN CO.,LTD **AND NOT BE USED WITH OUT THEIR WRITTEN PERMISSION**

ARCHITECTURE / INTERIOR


บริษัท มาร์ชเทน จำกัด

403 ซ.พัฒนาการ 50 สวนหลวง กรุงเทพมหานคร 10250

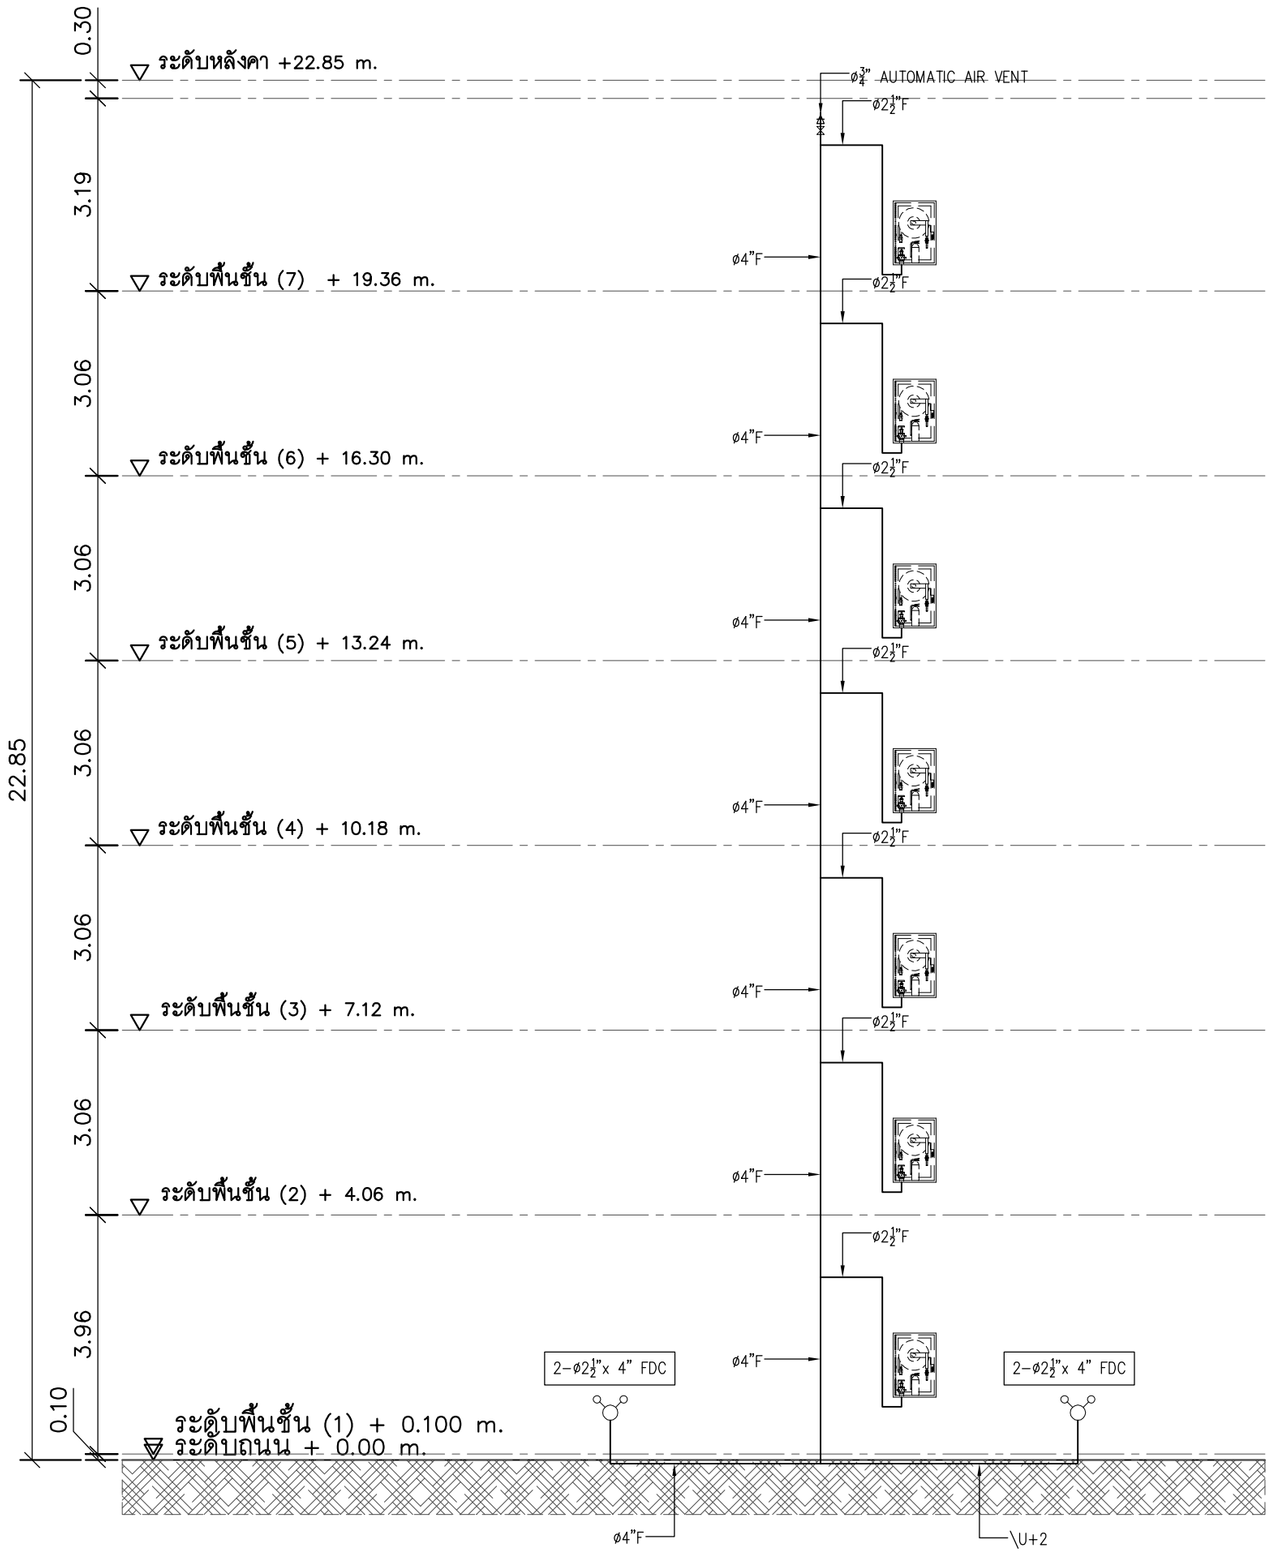

ไดอะแกรมระบบดับเพลิง (ระบบท่อแห้ง)

SCALE NTS.

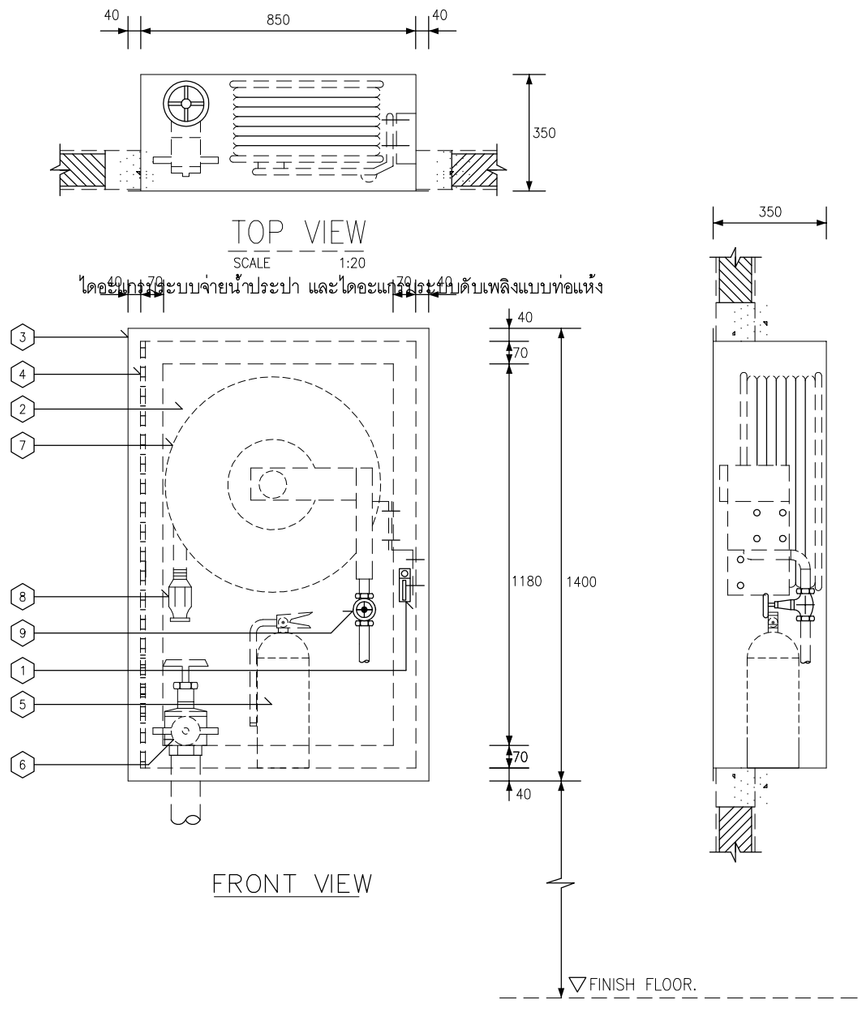

1. PUSH TO OPEN LOCKABLE DEVICE , KEYED ALIKE , FINISHED CHROMED.
2. SAFETY GLASS 5 mm. THICK. DOOR PANEL.
3. RECESSED TYPE CABINET MADE OF 1.6 mm. (16 GAUGE) STEEL WITH STEEL TRIM & DOORFRAME , DOOR TO BE FURNISHED WITH CONTINUOUS STEEL HINGE (BRASS PIN) WITH PUSH TO OPEN LOCKABLE DEVICE , KEYED ALIKE , CABINET SHALL BE CLEANED & COATED WITH PHOSPHATE SOLUTION PRIOR TO BEING FINISHED WITH BAKED ON RED PAINTING (OSHA RED)
4. CONTINUOUS STEEL HINGE WITH BRASS PIN.
5. ABC DRY CHEMICAL (AMMONIUM PHOSPHATE BASE) FIRE EXTINGUISHER , 4.5 kg.(10 LB), UL/FM LISTED , OR AS APPROVED TO TIS 332-2531
6. 65mm.ø (2 1/2"ø CAST BRASS UL/FM. 21 kg./cm. (300 LB) ANGLE HOSE VALVE WITH 65mm. ø (2 1/2"ø) CAST BRASS INSTANTANEOUS COUPLING ADAPTOR WITH CAP & CHAIN.
7. AUTOMATIC RECESSED HOSEREEL COMPLETE SET TO BS 5274 – 1985 WITH 25mm.ø X 30m. (1"ø X 100') RED RUBBER HOSE , THERMOPLASTIC POLYMER COVERED , TO BS 3169 – 1986 CLASS B TYPE 1. AUTOMATIC VALVE MECHANISM SHALL BE NON CORRODED METAL(STAINLESS STEEL)
8. PLASTIC NOZZLE 25mm. ø (1"ø) INLET WITH 10 mm. ORIFICE OR AS APPROVED.
9. 25mm. ø (1"ø) BRASS GATE VALVE OR BALL VALVE AS APPROVED.

แบบขยายตู้ดับเพลิง

SCALE NTS.

PROJECT NUMBER : VC2023-024

PROJECT

MACHI RESIDENCES

อาคารพักอาศัยรวม ค.ส.ล 7 ชั้น

OWNER

บริษัท ฤทธิกร ลิฟวิ่ง จำกัด

ARCHITECT :

อัคคะภัทร์ จิระอารียบุตร ส-สถ.3040

403 ซ.พัฒนาการ 50 พัฒนาการ

กรุงเทพมหานคร 10250

INTERIOR DESIGNER :

-

STRUCTURAL ENGINEER :

นายพงษ์ธวิทย์ คทาวุธเจริญกุล ลย.12291

ELECTRICAL ENGINEER :

นายภาคภูมิ คำพิทูรย์ ลฟก.5587

MECHANICAL ENGINEER :

SANITARY ENGINEER :

พล.อรวรรณ พลตรี ลส.134

DRAWING TITLE

ไดอะแกรมระบบดับเพลิง (ระบบท่อแห้ง)
แบบขยายตู้ดับเพลิง

DRAWING FOR CONSTRUCTION

DRAW BY :	CHECKER :	REVISION :
Weerayuth L.	Akapatr C.	–

SCALE :	DRAWING NO.
1 : 100	SN-03
DATE : 20-10-2024	
FILE NAME :	JOB NO.

REVISION	DESCRIPTION


GERNERAL NOTE

DO NOT SCALE DRAWING ALL MEASUREMENT MUST BE **CHECKED AT THE SIDE BY THE CONTRACTOR**

ALL DESIGN AND DRAWINGS ARE THE PROPERTY OF MARCHTEN CO.,LTD **AND NOT BE USED WITH OUT THEIR WRITTEN PERMISSION**

ARCHITECTURE / INTERIOR

บริษัท มาร์ชเทน จำกัด
403 ซ.พัฒนาการ 50 สวนหลวง กรุงเทพมหานคร 10250

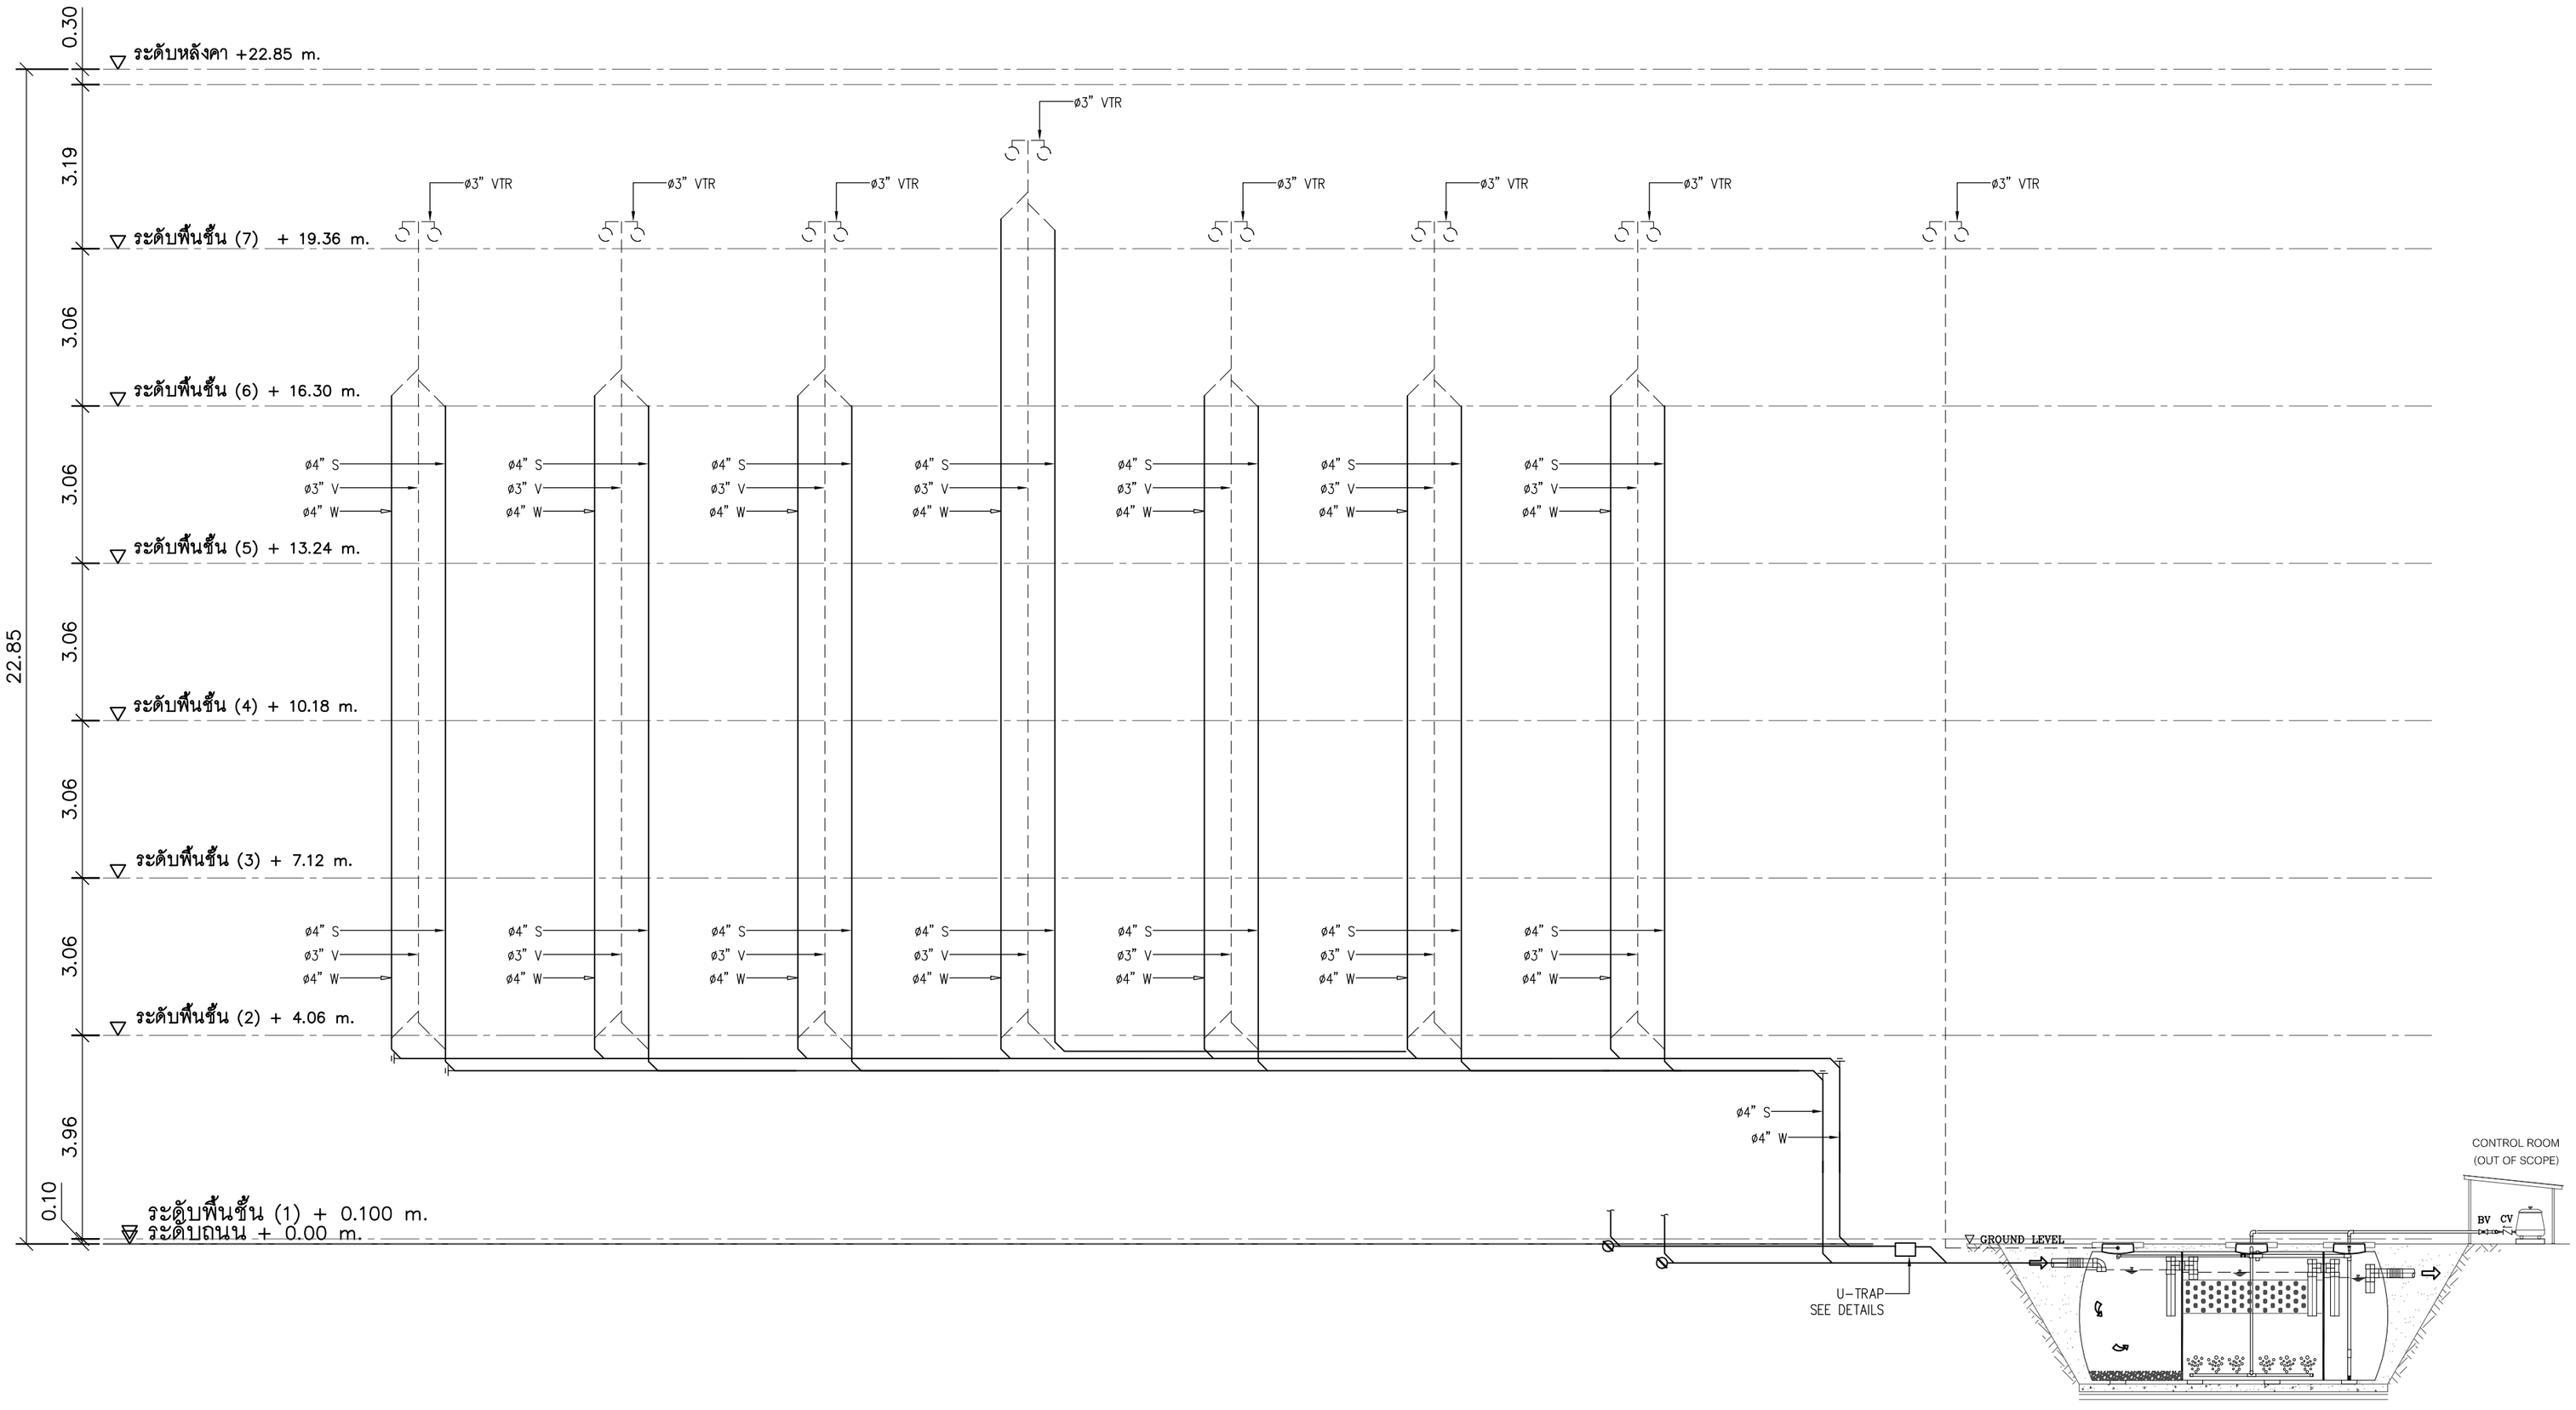

WWTP-01
ถังบำบัดน้ำเสียสำเร็จรูป ขนาด 25 ลบ.ม ต่อวัน

ไดอะแกรมระบบรวบรวมน้ำเสีย

SCALE NTS.

PROJECT NUMBER : VC2023-024

PROJECT

MACHI RESIDENCES

อาคารพักอาศัยรวม ค.ส.ล 7 ชั้น

OWNER

บริษัท ฤทธิกร ลิฟวิ่ง จำกัด

ARCHITECT :

อัคคะภัทร์ จิระอารีย์บุตร ส-สถ.3040

403 ซ.พัฒนาการ 50 พัฒนาการ

กรุงเทพมหานคร 10250

INTERIOR DESIGNER :

-

STRUCTURAL ENGINEER :

นายพงษ์ธวิทย์ คทาวุธเจริญกุล ลย.12291

ELECTRICAL ENGINEER :

นายภาคภูมิ คำพิทูรย์ ลฟก.5587

MECHANICAL ENGINEER :

SANITARY ENGINEER :

พล.อ.รวรรณ พลตรี ลส.134

DRAWING TITLE

ไดอะแกรมระบบรวบรวมน้ำเสีย

DRAWING FOR CONSTRUCTION

DRAW BY :	CHECKER :	REVISION :
Weerayuth L.	Akapatr C.	–

SCALE :	DRAWING NO.
1 : 100	SN-04
DATE : 20-10-2024	
FILE NAME :	JOB NO.

REVISION	DESCRIPTION

GERNERAL NOTE


DO NOT SCALE DRAWING ALL MEASUREMENT MUST BE **CHECKED AT THE SIDE BY THE CONTRACTOR**

ALL DESIGN AND DRAWINGS ARE THE PROPERTY OF MARCHTEN CO.,LTD **AND NOT BE USED WITH OUT THEIR WRITTEN PERMISSION**

ARCHITECTURE / INTERIOR

บริษัท มาร์ชเทน จำกัด

403 ซ.พัฒนาการ 50 สวนหลวง กรุงเทพมหานคร 10250

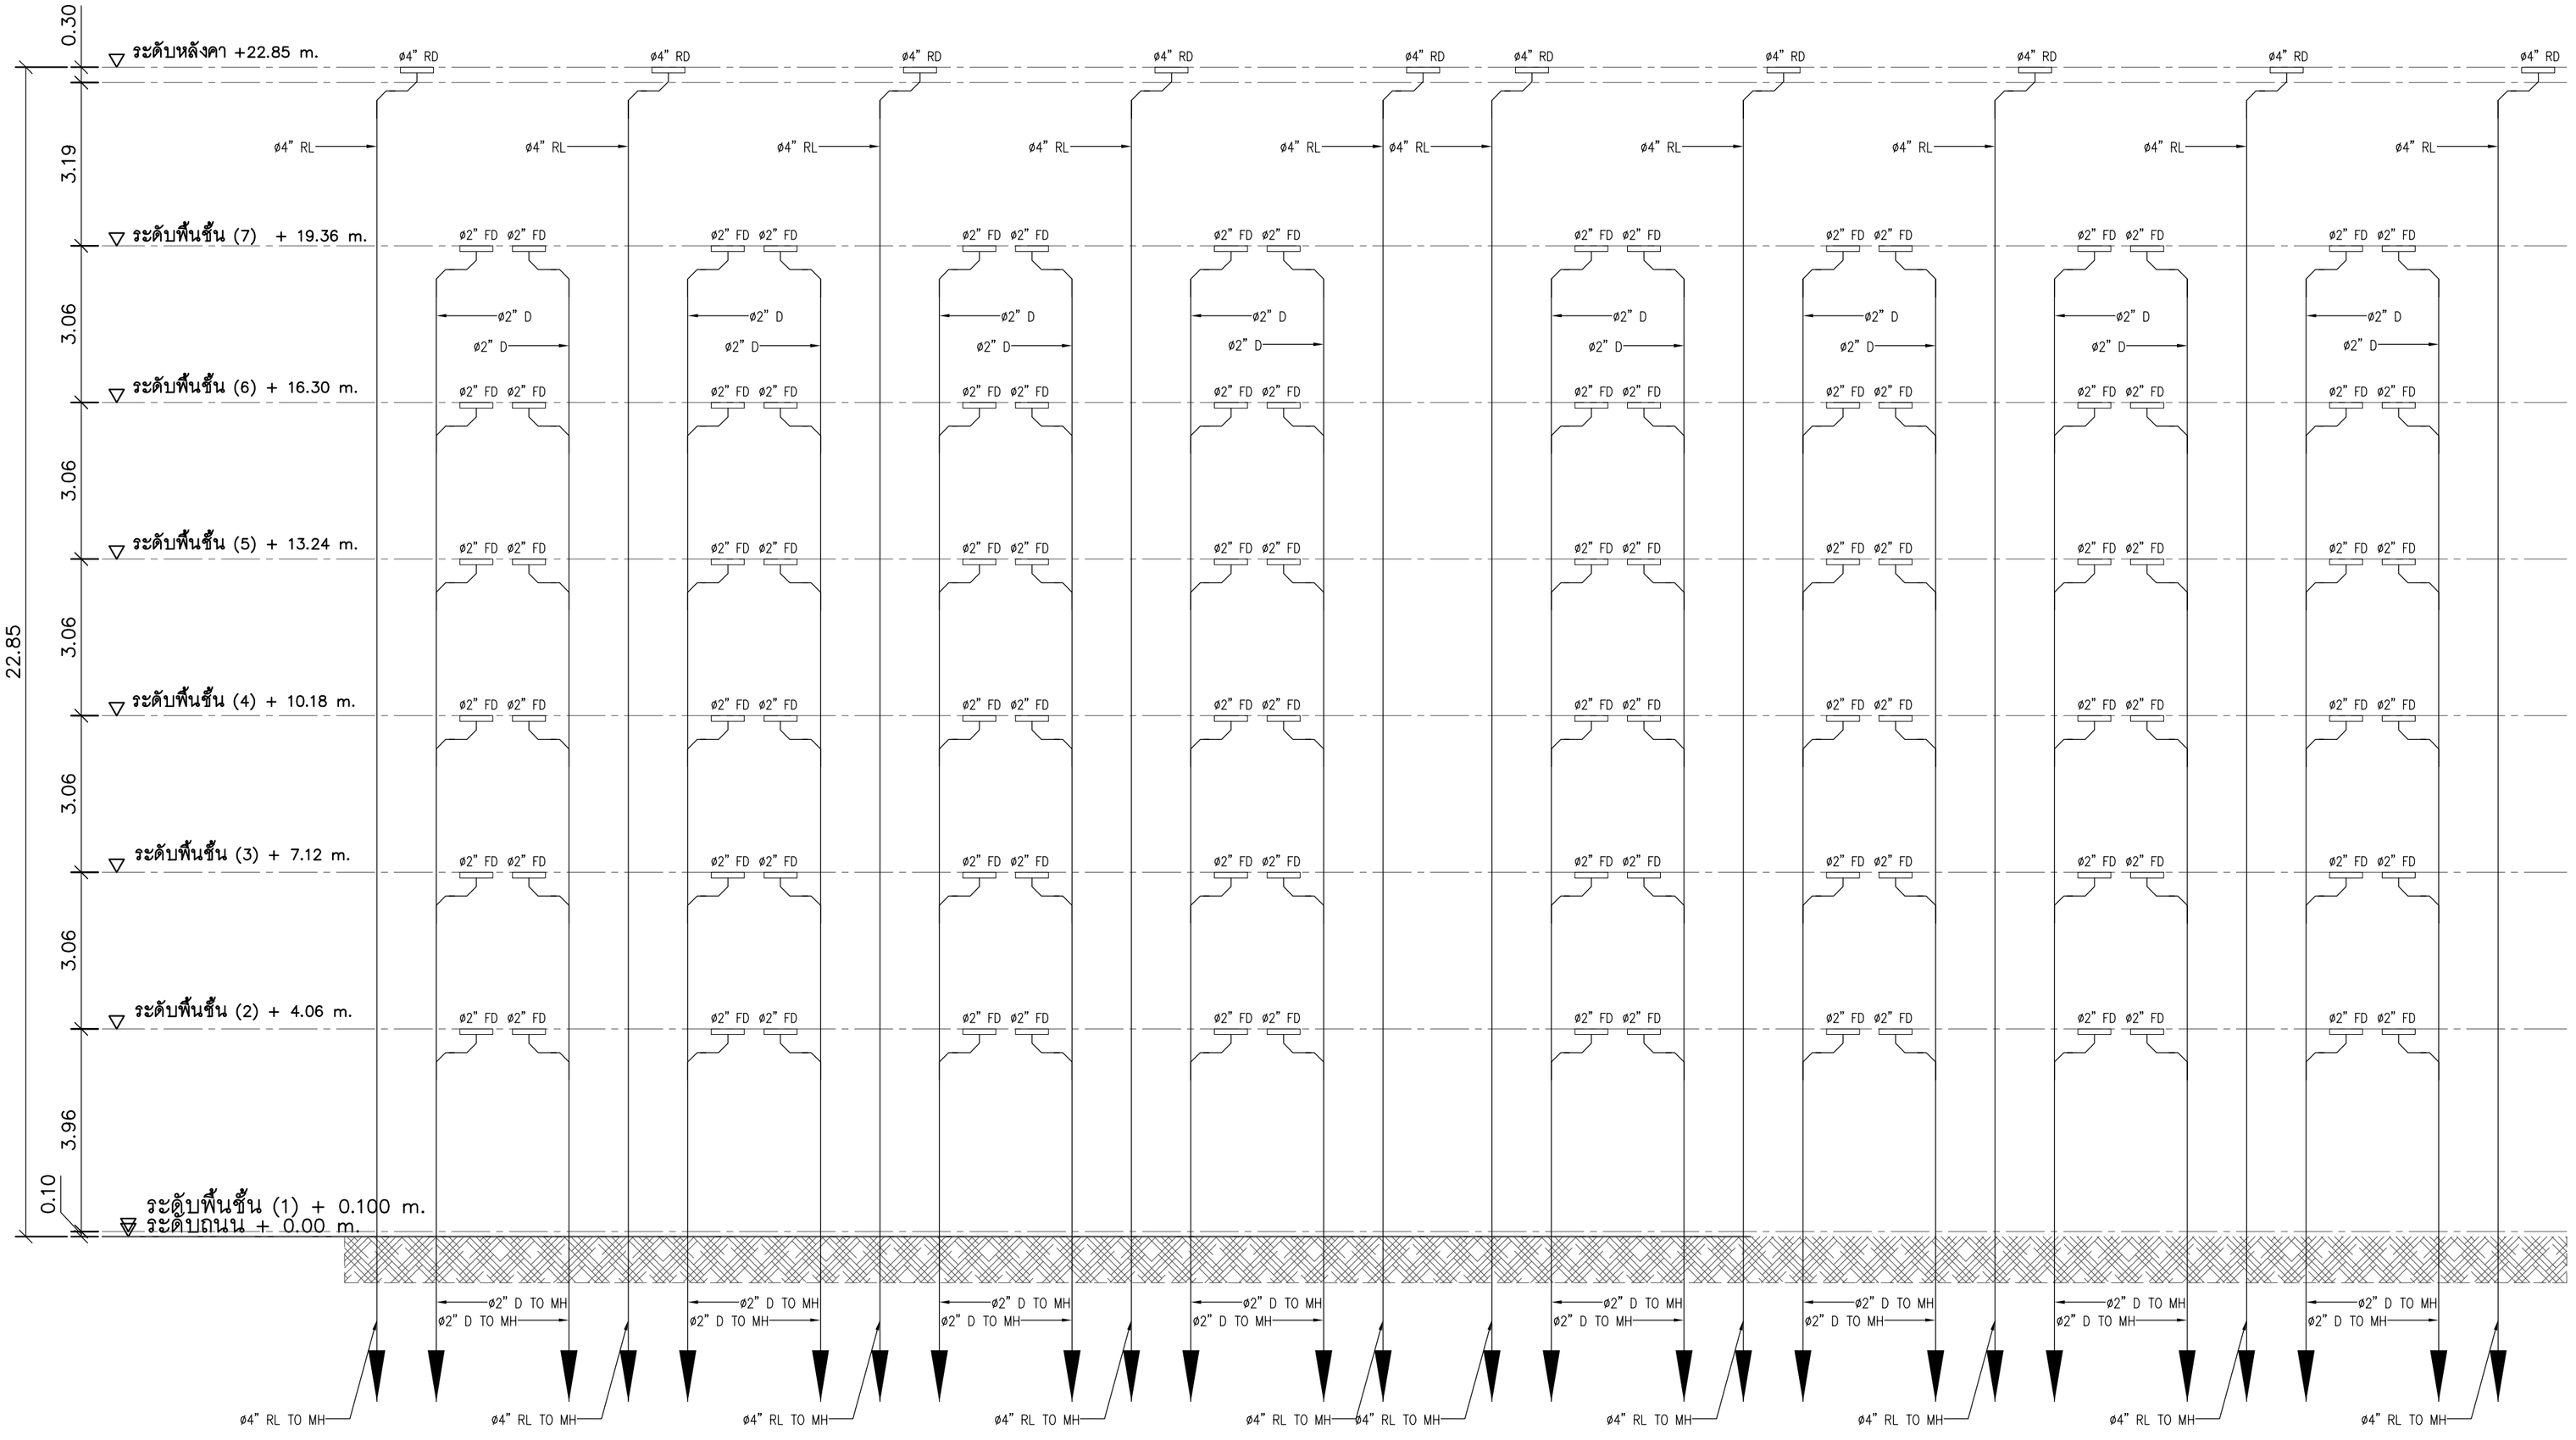

ไดอะแกรมระบบระบายน้ำฝน

SCALE NTS.

PROJECT NUMBER : VC2023-024

PROJECT

MACHI RESIDENCES

อาคารพักอาศัยรวม ค.ส.ล 7 ชั้น

OWNER

บริษัท ฤทธิกร ลิฟวิ่ง จำกัด

ARCHITECT :

อัคคะภัทร์ จิระอารียบุตร ส-สถ.3040

403 ซ.พัฒนาการ 50 พัฒนาการ

กรุงเทพมหานคร 10250

INTERIOR DESIGNER :

-

STRUCTURAL ENGINEER :

นายพงษ์ธวิทย์ คทาวุธเจริญกุล ลย.12291

ELECTRICAL ENGINEER :

นายภาคภูมิ คำพิทูรย์ ลฟก.5587

MECHANICAL ENGINEER :

SANITARY ENGINEER :

น.ส.อรวรรณ พลตรี ลส.134

DRAWING TITLE

ไดอะแกรมระบบระบายน้ำฝน

DRAWING FOR CONSTRUCTION


DRAW BY :	CHECKER :	REVISION :
Weerayuth L.	Akapatr C.	–

SCALE :	DRAWING NO.
1 : 100	SN-05
DATE : 20-10-2024	
FILE NAME :	JOB NO.

REVISION	DESCRIPTION

GERNERAL NOTE
DO NOT SCALE DRAWING ALL MEASUREMENT MUST BE
CHECKED AT THE SIDE BY THE CONTRACTOR
ALL DESIGN AND DRAWINGS ARE THE PROPERTY OF
MARCHTEN CO.,LTD
AND NOT BE USED WITH OUT THEIR WRITTEN PERMISSION

ARCHITECTURE / INTERIOR
บริษัท มาร์ชเทน จำกัด
403 ซ.พัฒนาการ 50 สวนหลวง กรุงเทพมหานคร 10250

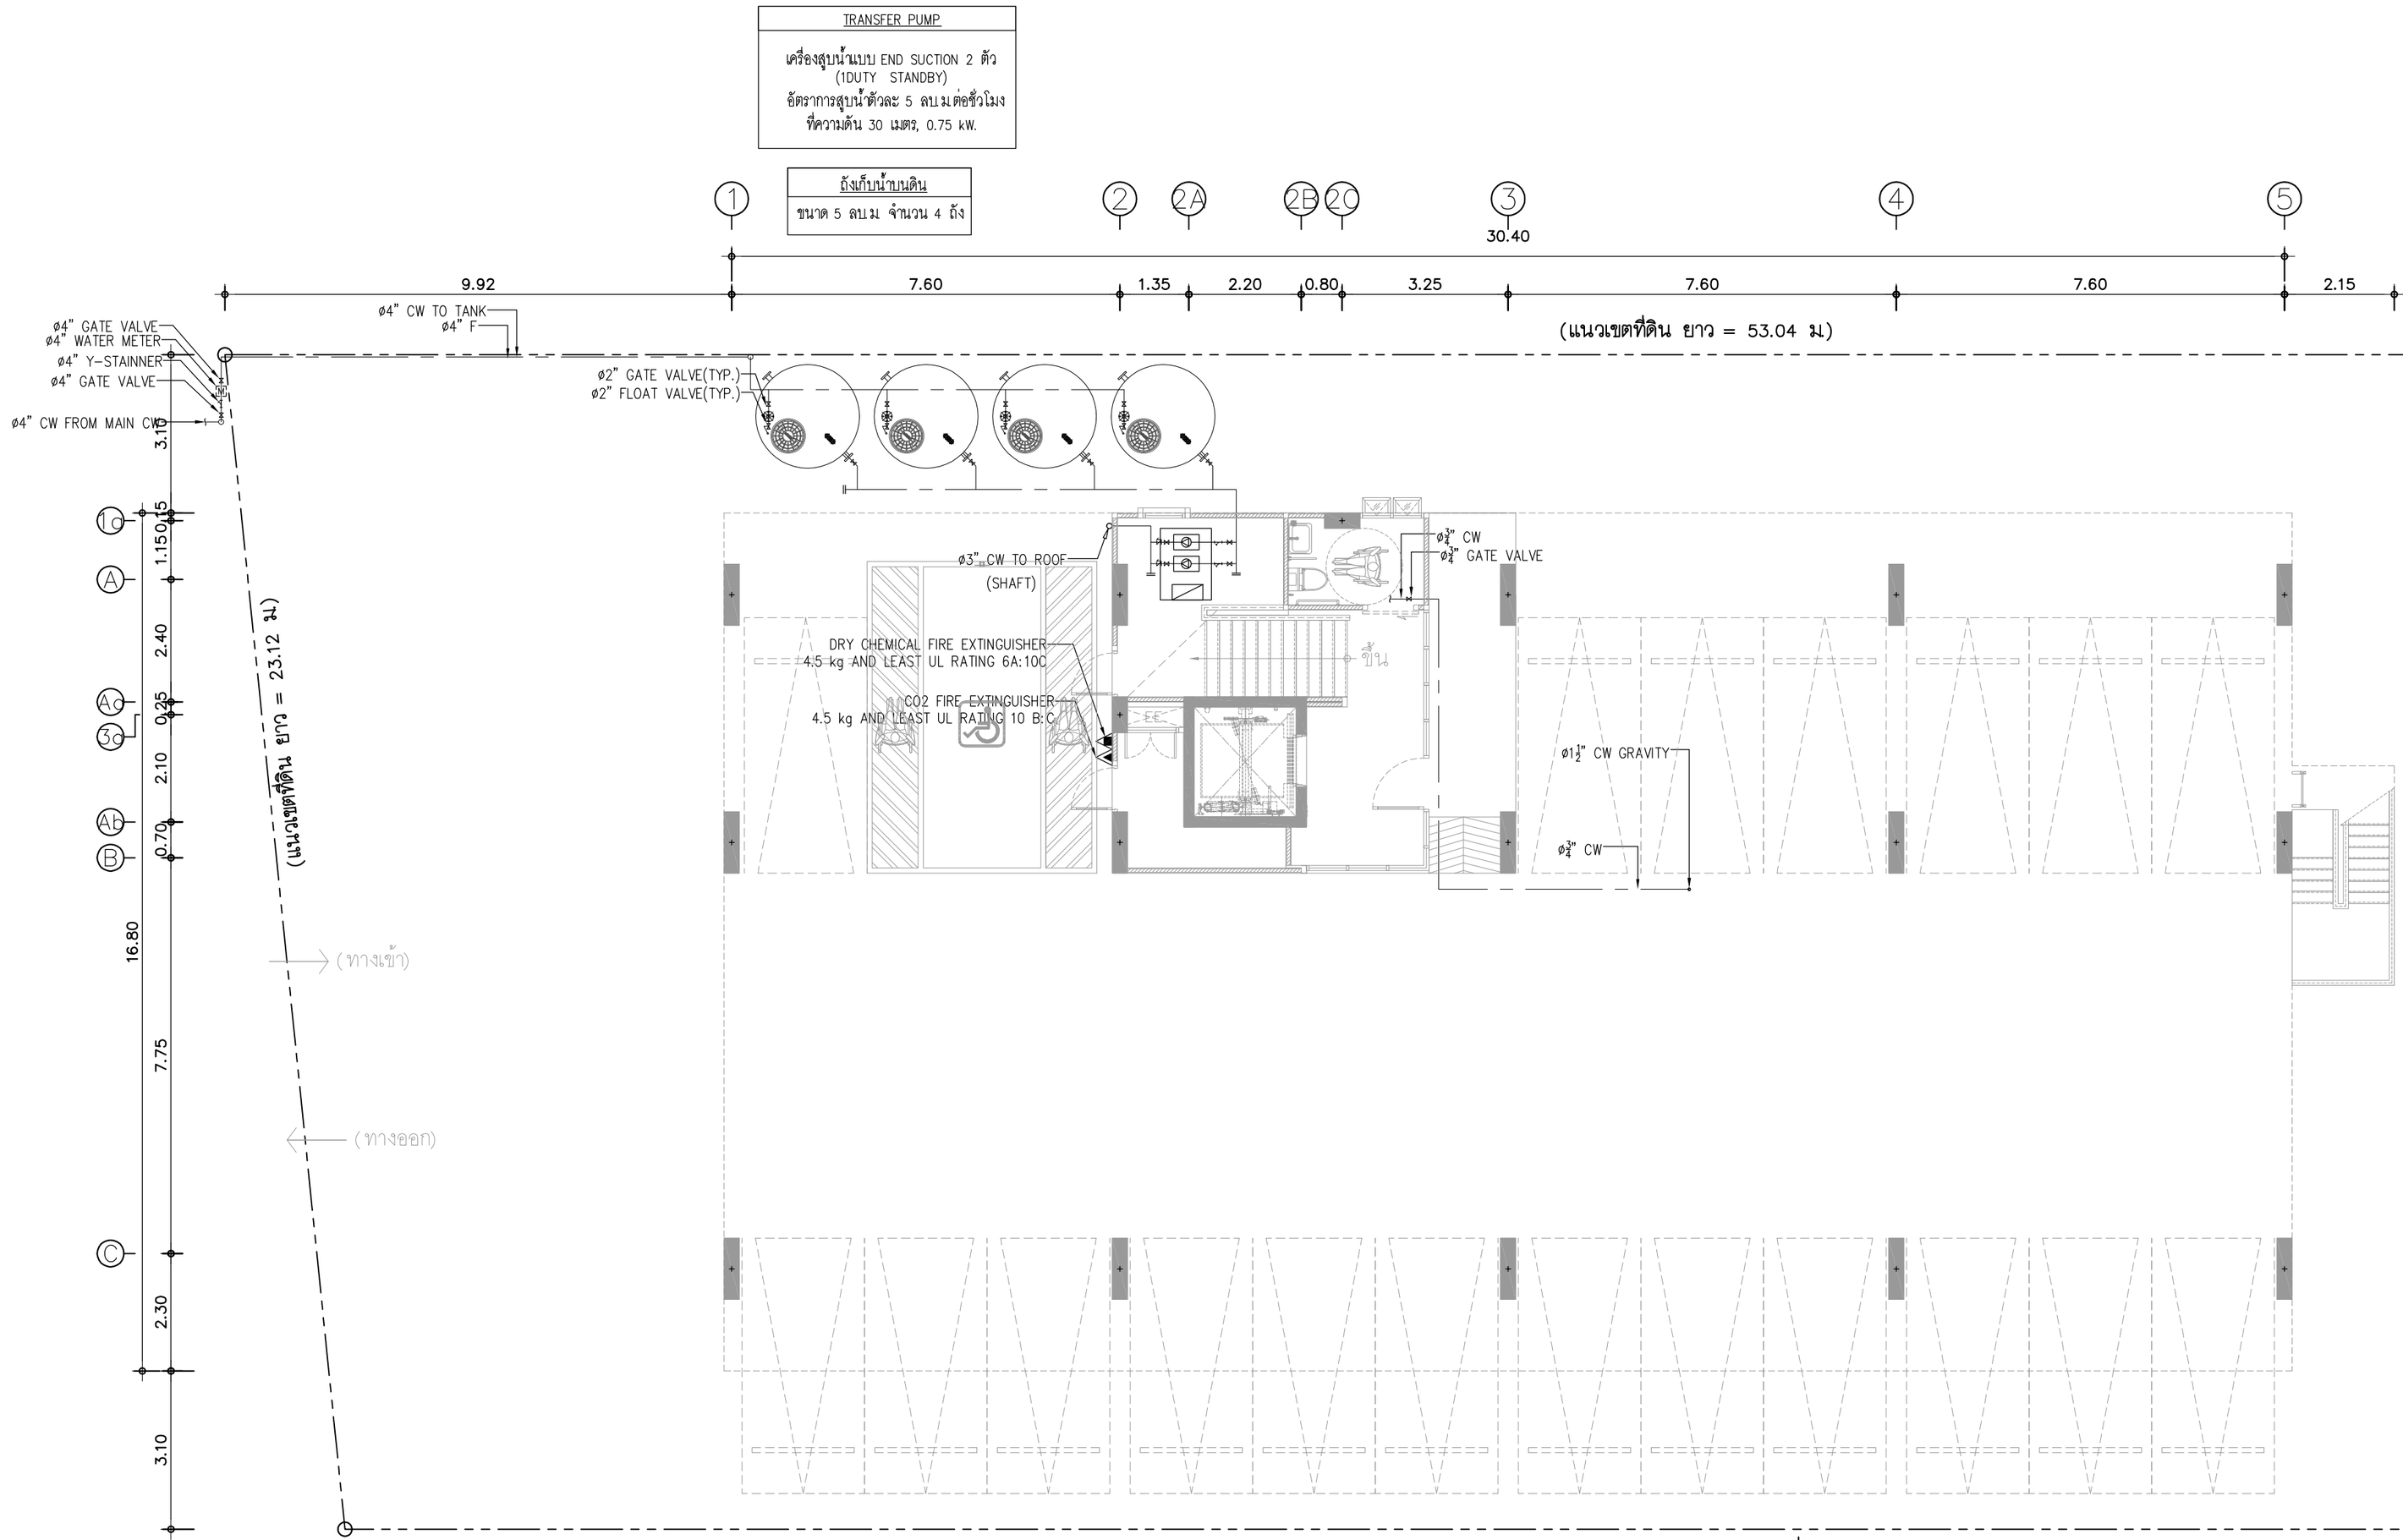

ผังระบบสุขาภิบาล (น้ำดี) ชั้น 1

SCALE 1:100

PROJECT NUMBER : VC2023-024

PROJECT

MACHI RESIDENCES

อาคารพักอาศัยรวม ค.ส.ล 7 ชั้น

OWNER

บริษัท ฤทธิกร ลิฟวิ่ง จำกัด

ARCHITECT :

อัคคะภัทร์ จิระอารีย์บุตร ส-สถ.3040

403 ซ.พัฒนาการ 50 พัฒนาการ

กรุงเทพมหานคร 10250

INTERIOR DESIGNER :

-

STRUCTURAL ENGINEER :

นายพงษ์ธวิทย์ คทาวุธเจริญกุล ลย.12291

ELECTRICAL ENGINEER :

นายภาคภูมิ คำพิทูรย์ ลฟก.5587

MECHANICAL ENGINEER :

SANITARY ENGINEER :

นส.อรวรรณ พลตรี ลส.134

DRAWING TITLE

ผังระบบสุขาภิบาล (น้ำดี) ชั้น 1

DRAWING FOR CONSTRUCTION

DRAW BY :	CHECKER :	REVISION :
Weerayuth L.	Akapatr C.	–

SCALE :	DRAWING NO.
1 : 100	SN-06
DATE : 20-10-2024	
FILE NAME :	JOB NO.

REVISION	DESCRIPTION

GERNERAL NOTE


DO NOT SCALE DRAWING ALL MEASUREMENT MUST BE **CHECKED AT THE SIDE BY THE CONTRACTOR**

ALL DESIGN AND DRAWINGS ARE THE PROPERTY OF MARCHTEN CO.,LTD **AND NOT BE USED WITH OUT THEIR WRITTEN PERMISSION**

ARCHITECTURE / INTERIOR

บริษัท มาร์ชเทน จำกัด

403 ซ.พัฒนาการ 50 สวนหลวง กรุงเทพมหานคร 10250

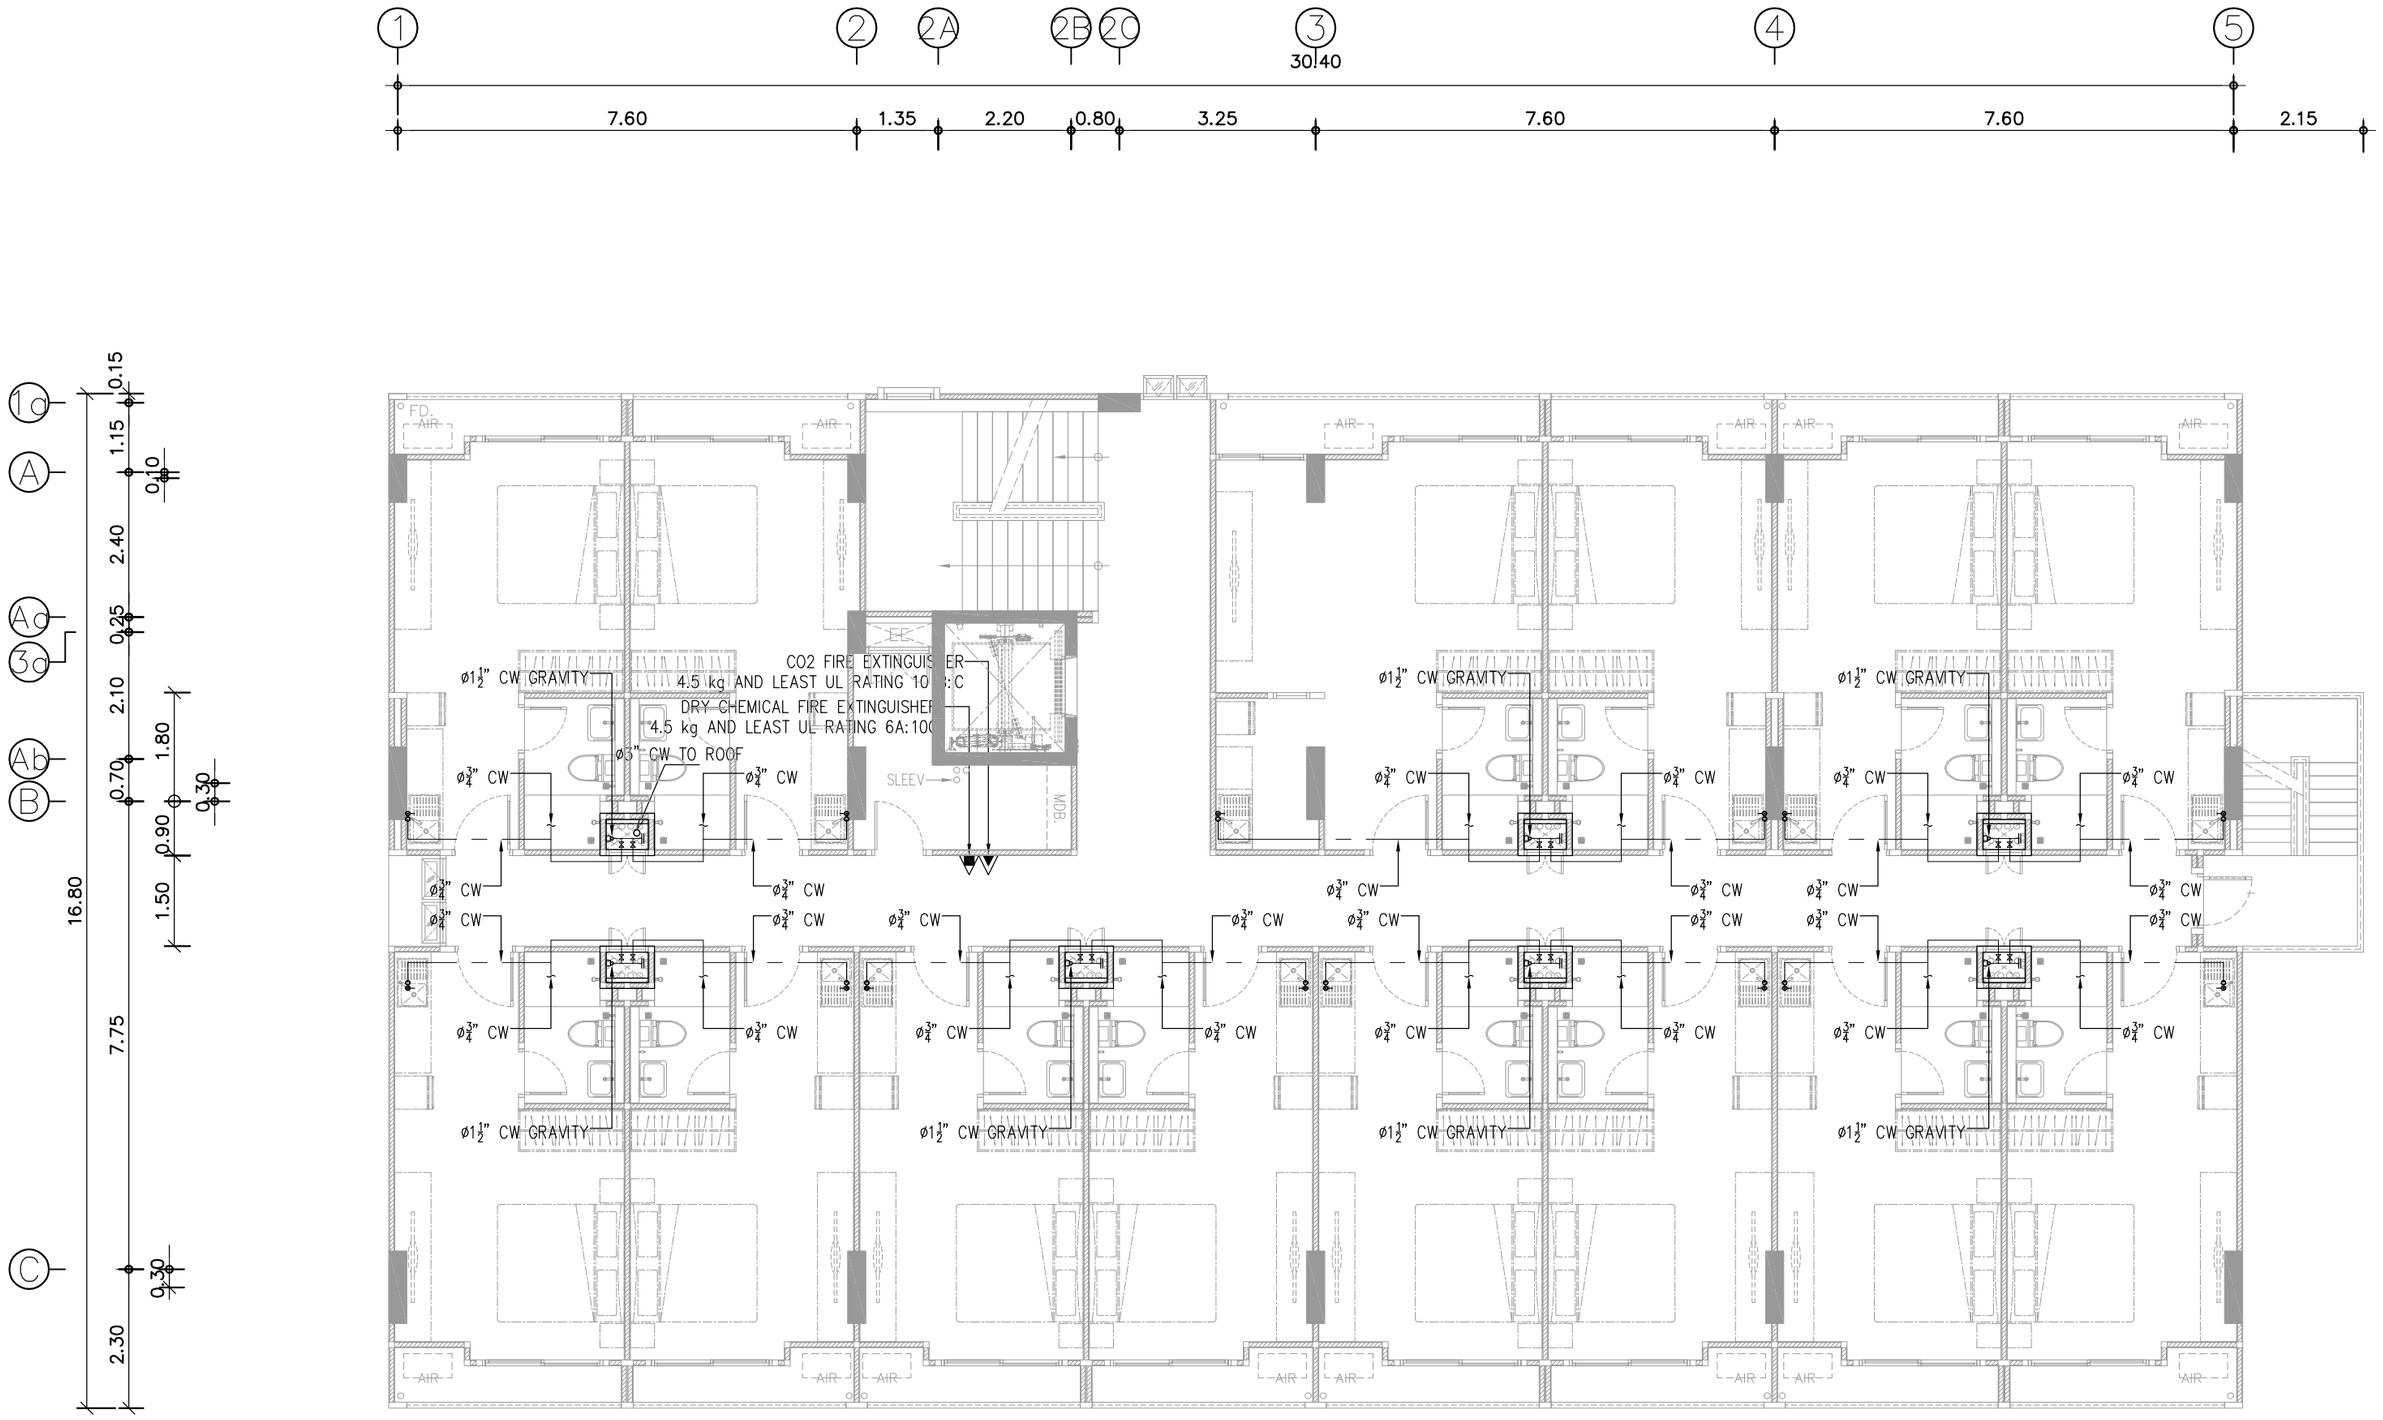

ผังระบบสุขาภิบาล (น้ำดี) ชั้น 2

SCALE 1:100

PROJECT NUMBER : VC2023-024

PROJECT

MACHI RESIDENCES

อาคารพักอาศัยรวม ค.ส.ล 7 ชั้น

OWNER

บริษัท ฤทธิกร ลิฟวิ่ง จำกัด

ARCHITECT :

อัคคะภัทร์ จิระอารียบุตร ส-สถ.3040

403 ซ.พัฒนาการ 50 พัฒนาการ

กรุงเทพมหานคร 10250

INTERIOR DESIGNER :

-

STRUCTURAL ENGINEER :

นายพงษ์ธวิทย์ คทาวุธเจริญกุล ลย.12291

ELECTRICAL ENGINEER :

นายภาคภูมิ คำพิทูรย์ ลฟก.5587

MECHANICAL ENGINEER :

SANITARY ENGINEER :

นส.อรวรรณ พลตรี ลส.134

DRAWING TITLE

ผังระบบสุขาภิบาล (น้ำดี) ชั้น 2

DRAWING FOR CONSTRUCTION

DRAW BY :	CHECKER :	REVISION :
Weerayuth L.	Akapatr C.	–


SCALE :	DRAWING NO.
1 : 100	SN-07
DATE : 20-10-2024	
FILE NAME :	JOB NO.


REVISION	DESCRIPTION


GERNERAL NOTE
DO NOT SCALE DRAWING ALL MEASUREMENT MUST BE
CHECKED AT THE SIDE BY THE CONTRACTOR
ALL DESIGN AND DRAWINGS ARE THE PROPERTY OF
MARCHTEN CO.,LTD
AND NOT BE USED WITH OUT THEIR WRITTEN PERMISSION

ARCHITECTURE / INTERIOR

บริษัท มาร์ชเทน จำกัด
403 ซ.พัฒนาการ 50 สวนหลวง กรุงเทพมหานคร 10250

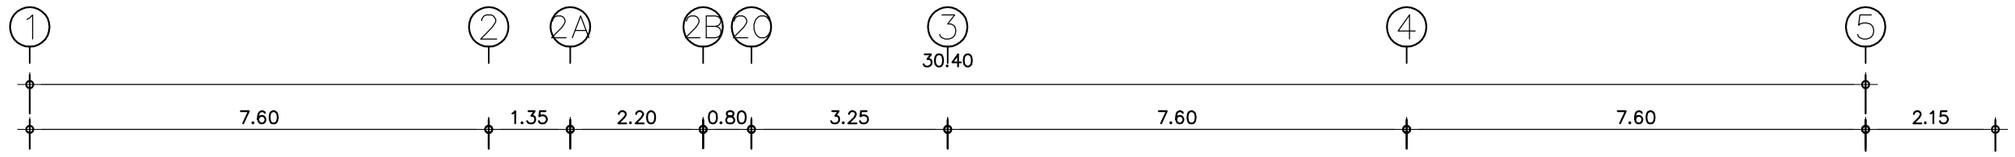

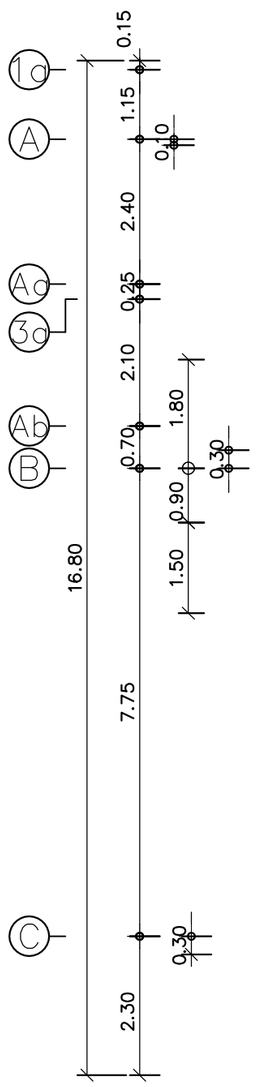

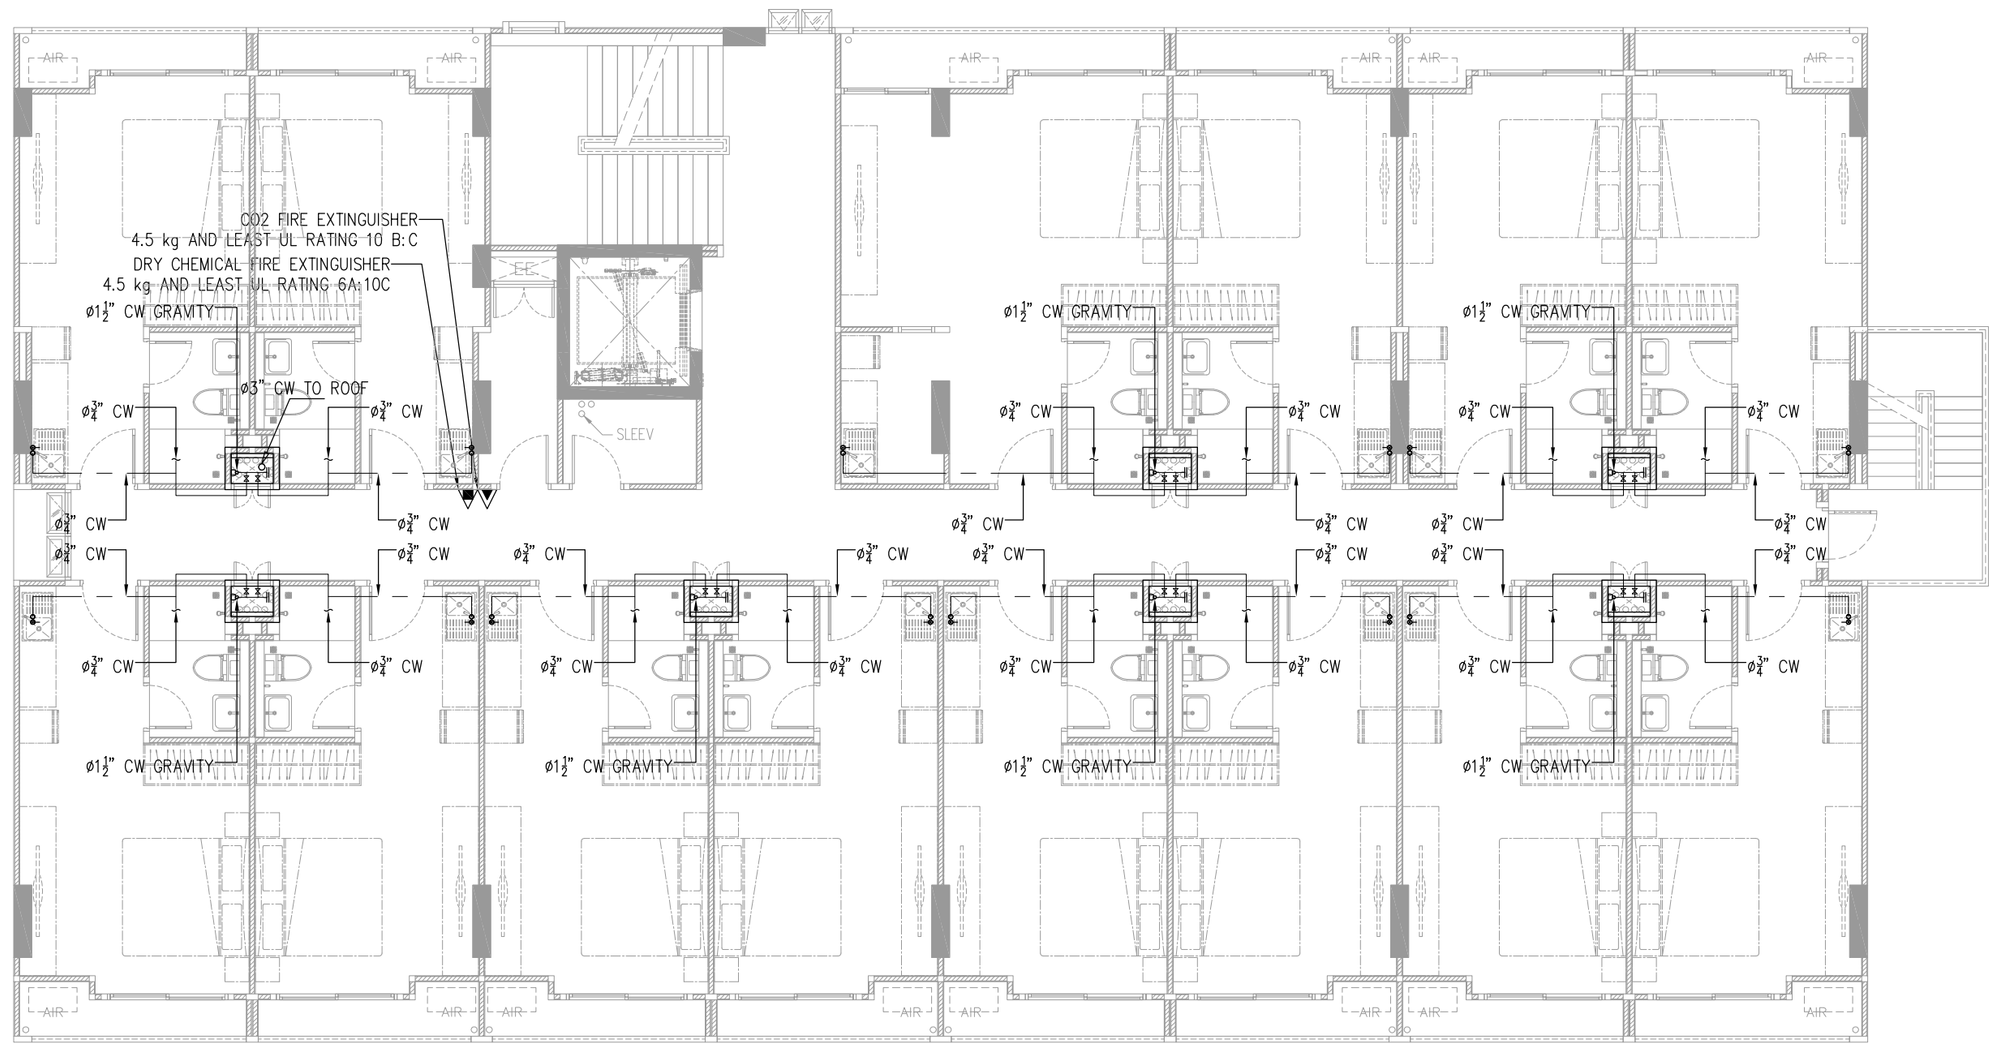

ผังระบบสุขาภิบาล (น้ำดี) ชั้น 3

SCALE 1:100

PROJECT NUMBER : VC2023-024

PROJECT

MACHI RESIDENCES

อาคารพักอาศัยรวม ค.ส.ล 7 ชั้น

OWNER

บริษัท ฤทธิกร ลิฟวิ่ง จำกัด

ARCHITECT :

อัคคะภัทร์ จิระอารีย์บุตร ส-สถ.3040

403 ซ.พัฒนาการ 50 พัฒนาการ

กรุงเทพมหานคร 10250

INTERIOR DESIGNER :

-

STRUCTURAL ENGINEER :

นายพงษ์ธวิทย์ คทาวุธเจริญกุล ลย.12291

ELECTRICAL ENGINEER :

นายภาคภูมิ คำพิทูรย์ ลฟก.5587

MECHANICAL ENGINEER :

SANITARY ENGINEER :

นส.อรวรรณ พลตรี ลส.134

DRAWING TITLE

ผังระบบสุขาภิบาล (น้ำดี) ชั้น 3

DRAWING FOR CONSTRUCTION

DRAW BY :	CHECKER :	REVISION :
Weerayuth L.	Akapatr C.	-


SCALE :	DRAWING NO.
1 : 100	SN-08
DATE : 20-10-2024	
FILE NAME :	JOB NO.


REVISION	DESCRIPTION


GERNERAL NOTE
DO NOT SCALE DRAWING ALL MEASUREMENT MUST BE
CHECKED AT THE SIDE BY THE CONTRACTOR
ALL DESIGN AND DRAWINGS ARE THE PROPERTY OF
MARCHTEN CO.,LTD
AND NOT BE USED WITH OUT THEIR WRITTEN PERMISSION

ARCHITECTURE / INTERIOR

บริษัท มาร์ชเทน จำกัด
403 ซ.พัฒนาการ 50 สวนหลวง กรุงเทพมหานคร 10250

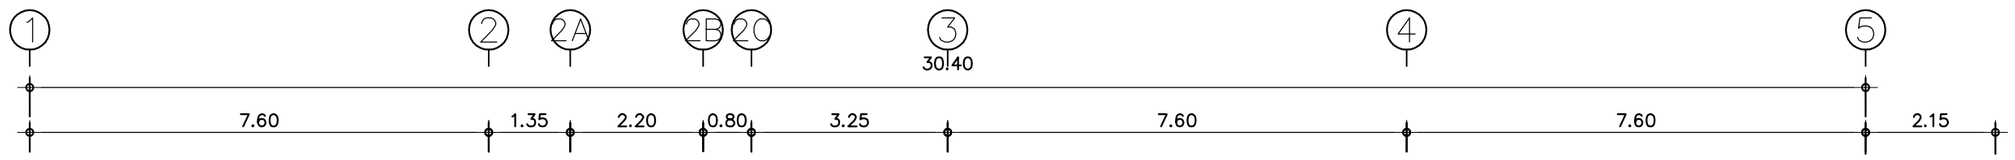

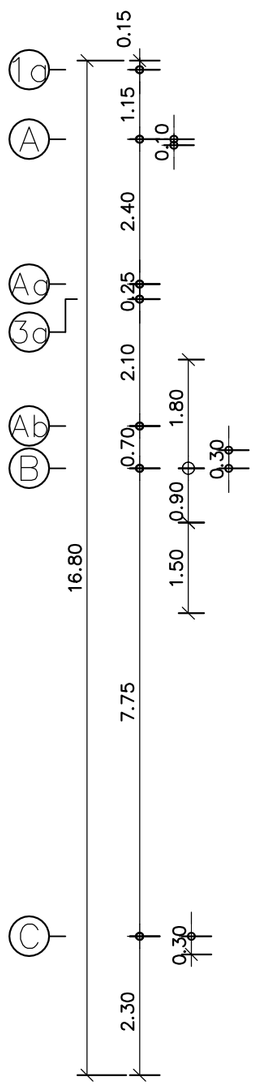

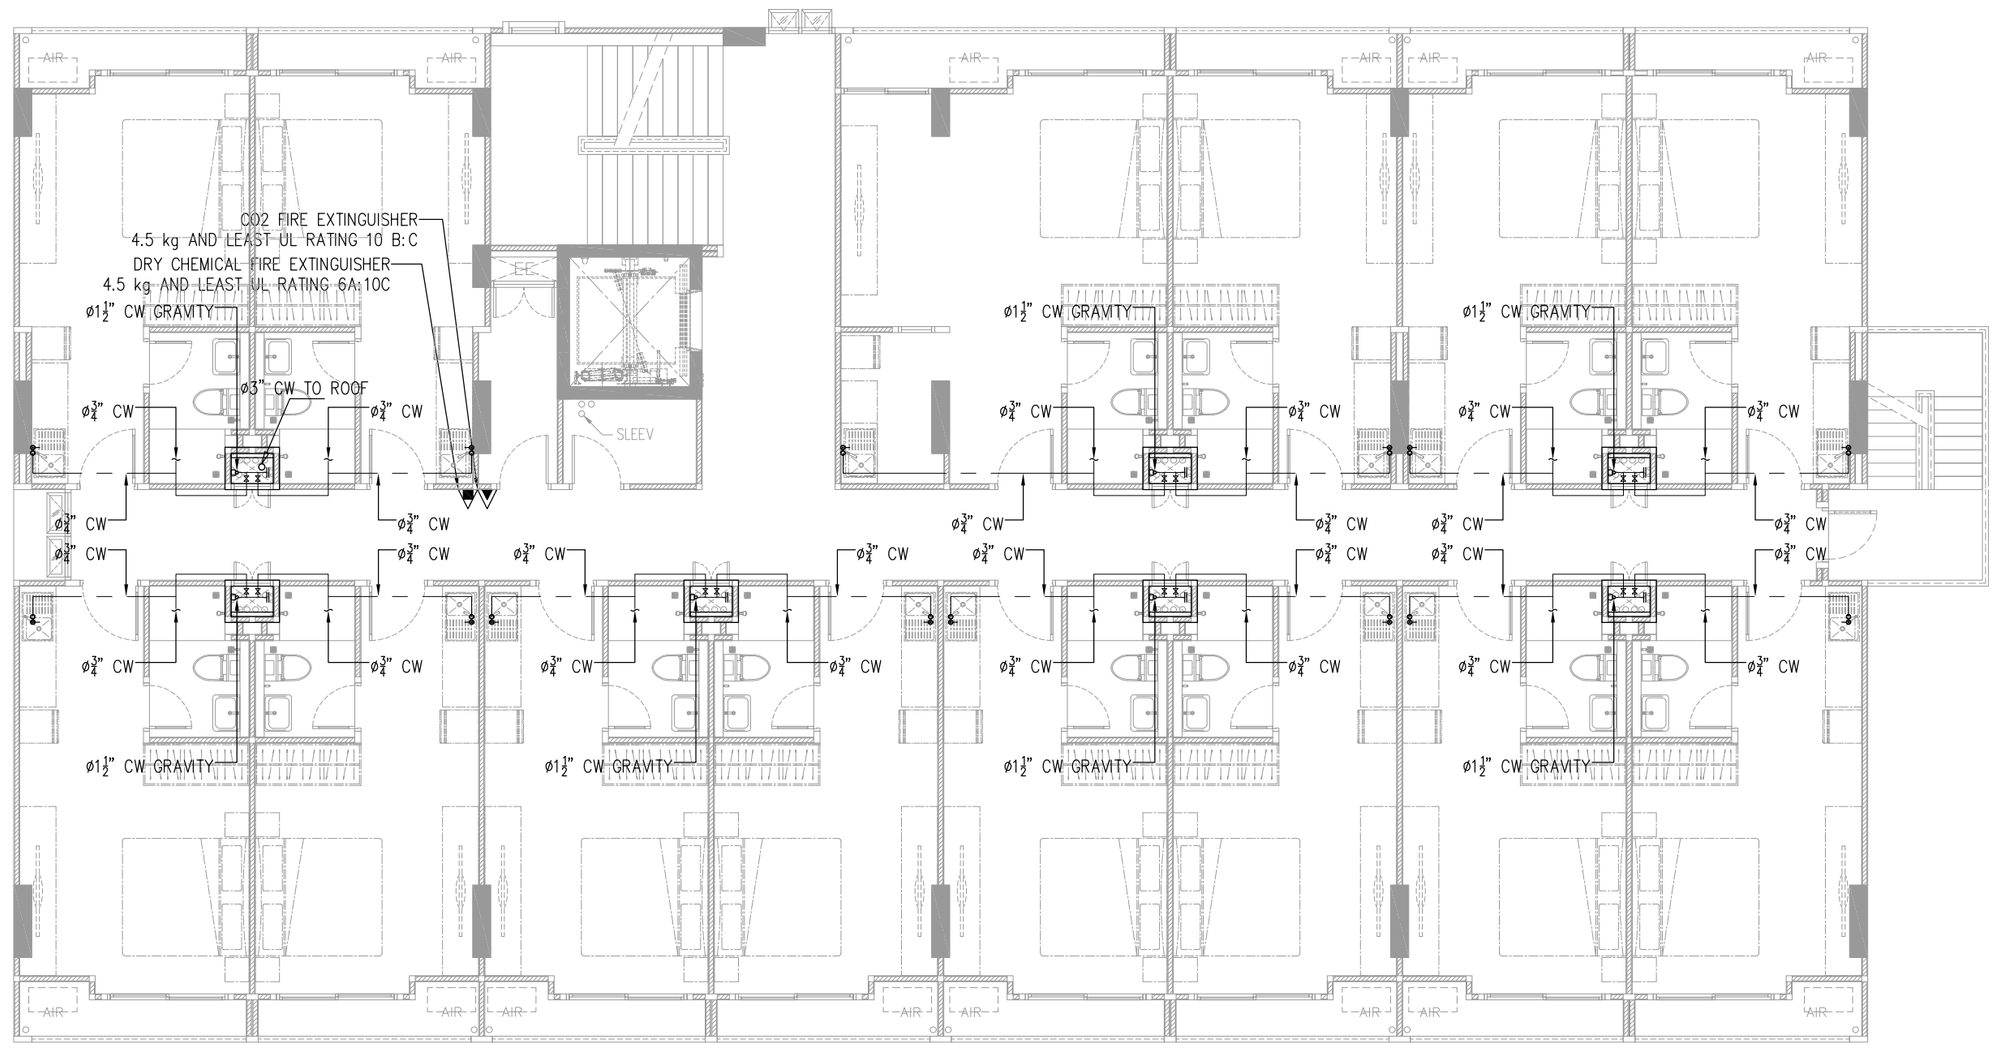

ผังระบบสุขาภิบาล (น้ำดี) ชั้น 4-5

SCALE 1:100

PROJECT NUMBER : VC2023-024

PROJECT

MACHI RESIDENCES

อาคารพักอาศัยรวม ค.ส.ล 7 ชั้น

OWNER

บริษัท ฤทธิกร ลิฟวิ่ง จำกัด

ARCHITECT :

อัคคะภัทร์ จิระอารีย์บุตร ส-สถ.3040

403 ซ.พัฒนาการ 50 พัฒนาการ

กรุงเทพมหานคร 10250

INTERIOR DESIGNER :

-

STRUCTURAL ENGINEER :

นายพงษ์ธวิทย์ คทาวุธเจริญกุล ลย.12291

ELECTRICAL ENGINEER :

นายภาคภูมิ คำพิทูรย์ ลฟก.5587

MECHANICAL ENGINEER :

SANITARY ENGINEER :

นส.อรวรรณ พลตรี ลส.134

DRAWING TITLE

ผังระบบสุขาภิบาล (น้ำดี) ชั้น 4-5

DRAWING FOR CONSTRUCTION

DRAW BY :	CHECKER :	REVISION :
Weerayuth L.	Akapatr C.	-

SCALE :	DRAWING NO.
1 : 100	SN-09
DATE : 20-10-2024	
FILE NAME :	JOB NO.

REVISION	DESCRIPTION

GERNERAL NOTE


DO NOT SCALE DRAWING ALL MEASUREMENT MUST BE **CHECKED AT THE SIDE BY THE CONTRACTOR**


ALL DESIGN AND DRAWINGS ARE THE PROPERTY OF MARCHTEN CO.,LTD **AND NOT BE USED WITH OUT THEIR WRITTEN PERMISSION**

ARCHITECTURE / INTERIOR

บริษัท มาร์ชเทน จำกัด

403 ซ.พัฒนาการ 50 สวนหลวง กรุงเทพมหานคร 10250

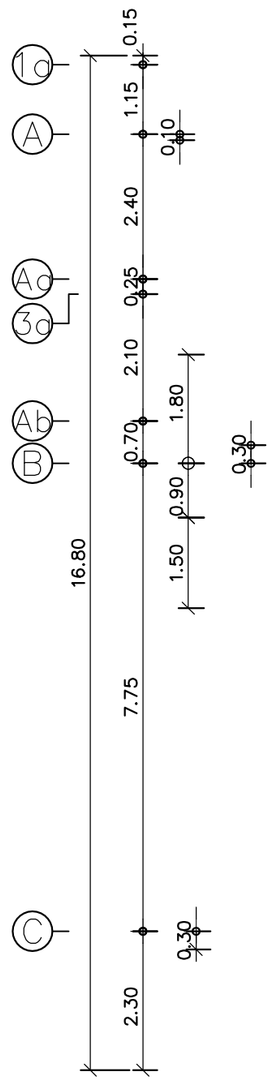

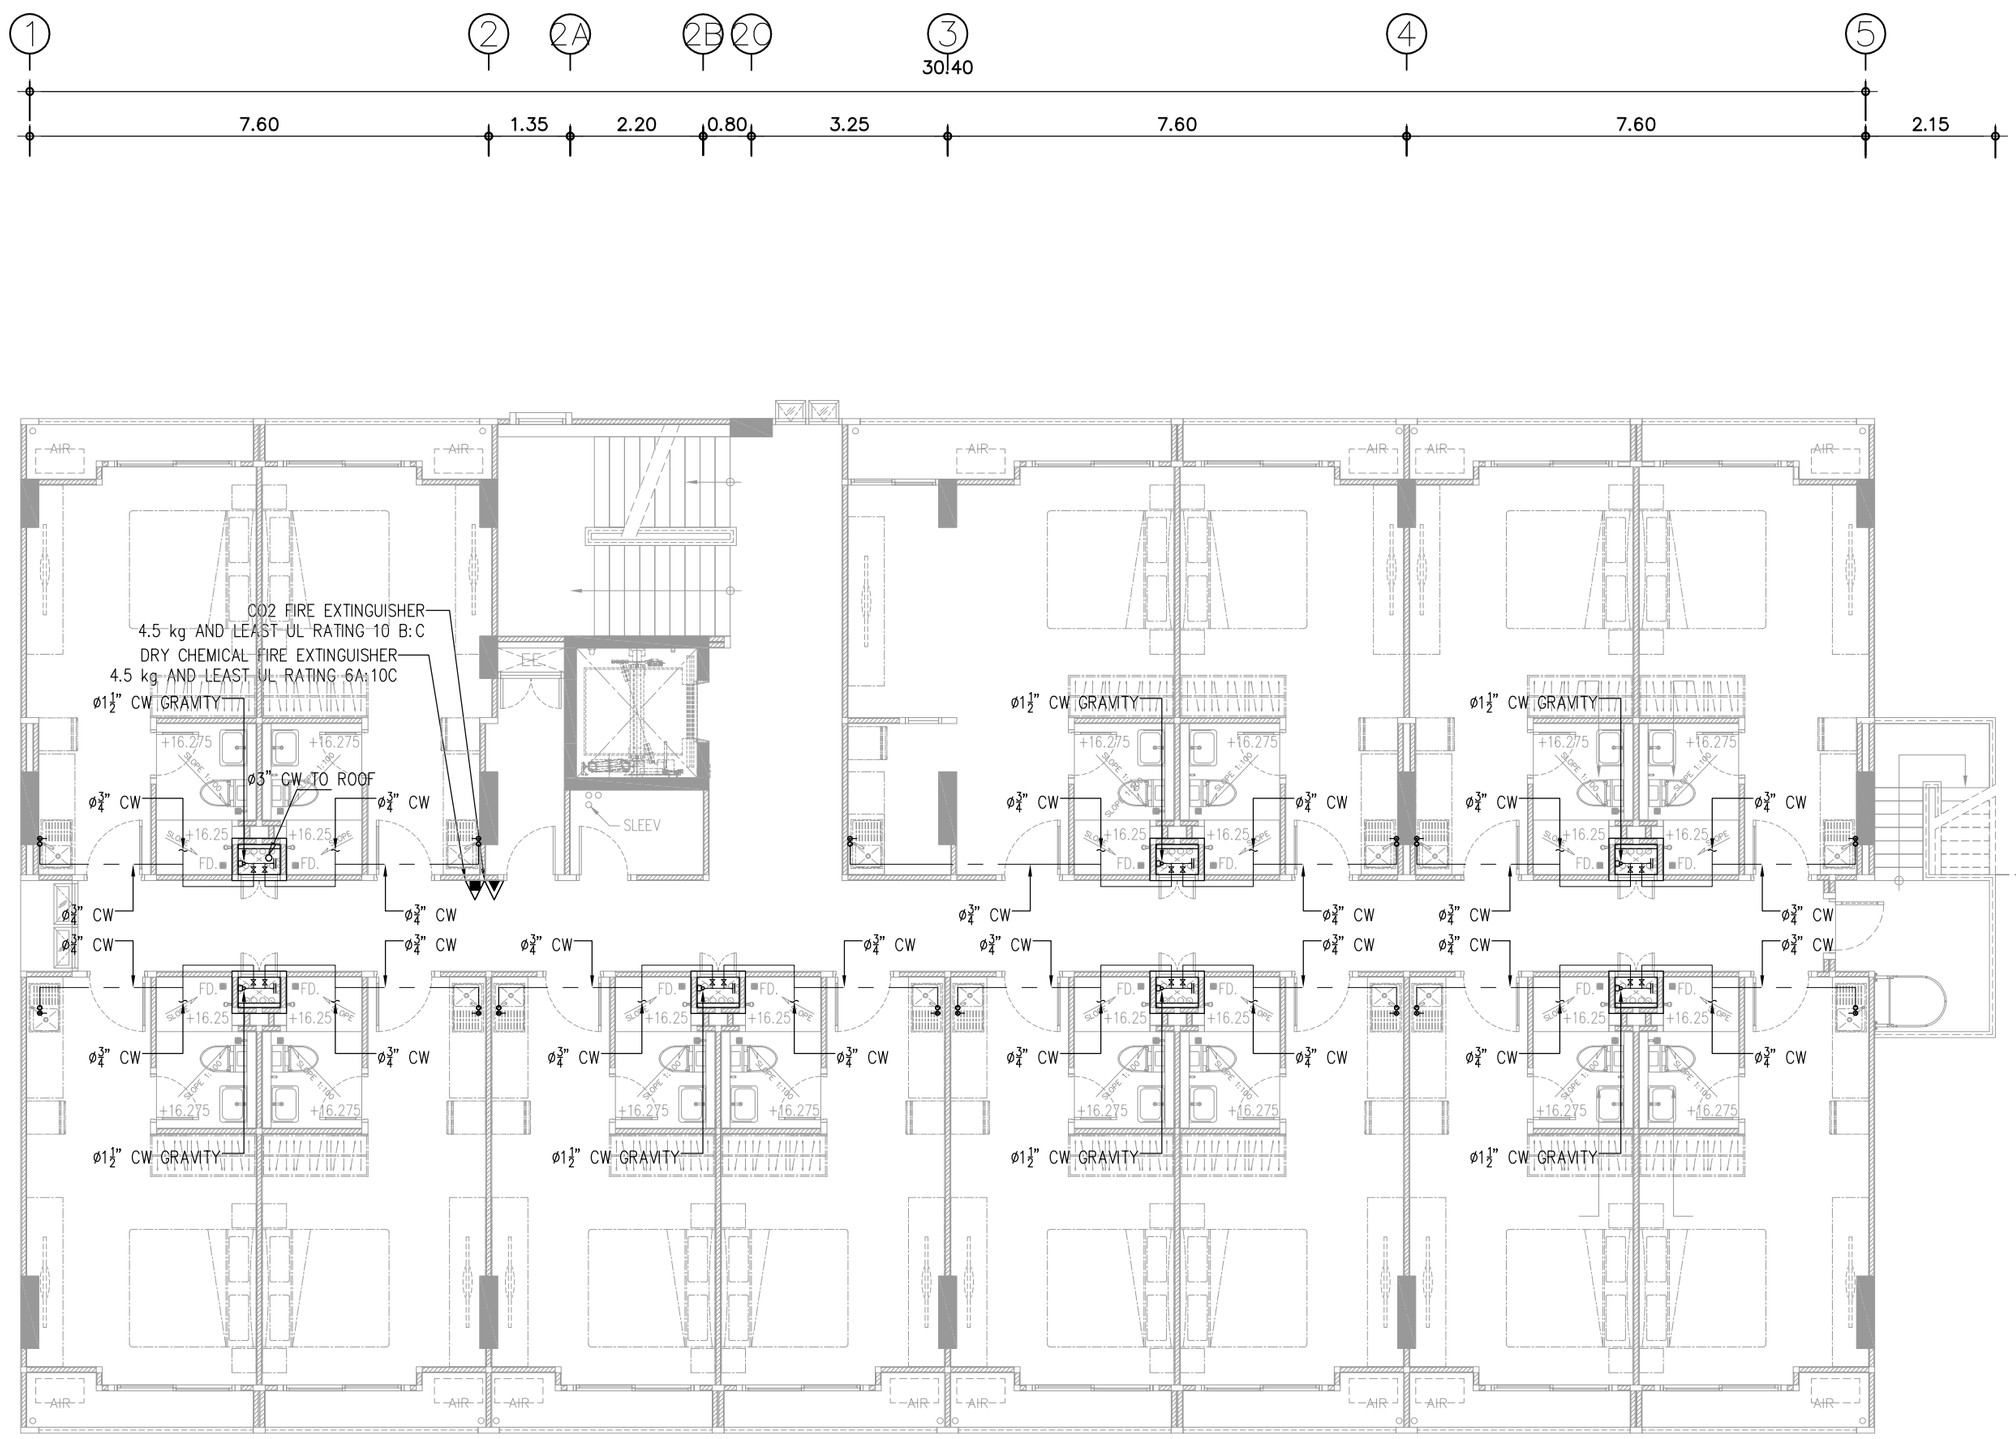

ผังระบบสุขาภิบาล (น้ำดี) ชั้น 6

SCALE 1:100

PROJECT NUMBER : VC2023-024

PROJECT

MACHI RESIDENCES

อาคารพักอาศัยรวม ค.ส.ล 7 ชั้น

OWNER

บริษัท ฤทธิกร ลิฟวิ่ง จำกัด

ARCHITECT :

อัคคะภัทร์ จิระอารีย์บุตร ส-สถ.3040

403 ซ.พัฒนาการ 50 พัฒนาการ

กรุงเทพมหานคร 10250

INTERIOR DESIGNER :

-

STRUCTURAL ENGINEER :

นายพงษ์ธวิทย์ คทาวุธเจริญกุล ลย.12291

ELECTRICAL ENGINEER :

นายภาคภูมิ คำพิทูรย์ ลฟก.5587

MECHANICAL ENGINEER :

SANITARY ENGINEER :

นส.อรวรรณ พลตรี ลส.134

DRAWING TITLE

ผังระบบสุขาภิบาล (น้ำดี) ชั้น 6

DRAWING FOR CONSTRUCTION

DRAW BY :	CHECKER :	REVISION :
Weerayuth L.	Akapatr C.	–

SCALE :	DRAWING NO.
1 : 100	SN-10
DATE : 20-10-2024	
FILE NAME :	JOB NO.

REVISION	DESCRIPTION


GERNERAL NOTE

DO NOT SCALE DRAWING ALL MEASUREMENT MUST BE **CHECKED AT THE SIDE BY THE CONTRACTOR**

ALL DESIGN AND DRAWINGS ARE THE PROPERTY OF MARCHTEN CO.,LTD **AND NOT BE USED WITH OUT THEIR WRITTEN PERMISSION**

ARCHITECTURE / INTERIOR

บริษัท มาร์ชเทน จำกัด
403 ซ.พัฒนาการ 50 สวนหลวง กรุงเทพมหานคร 10250

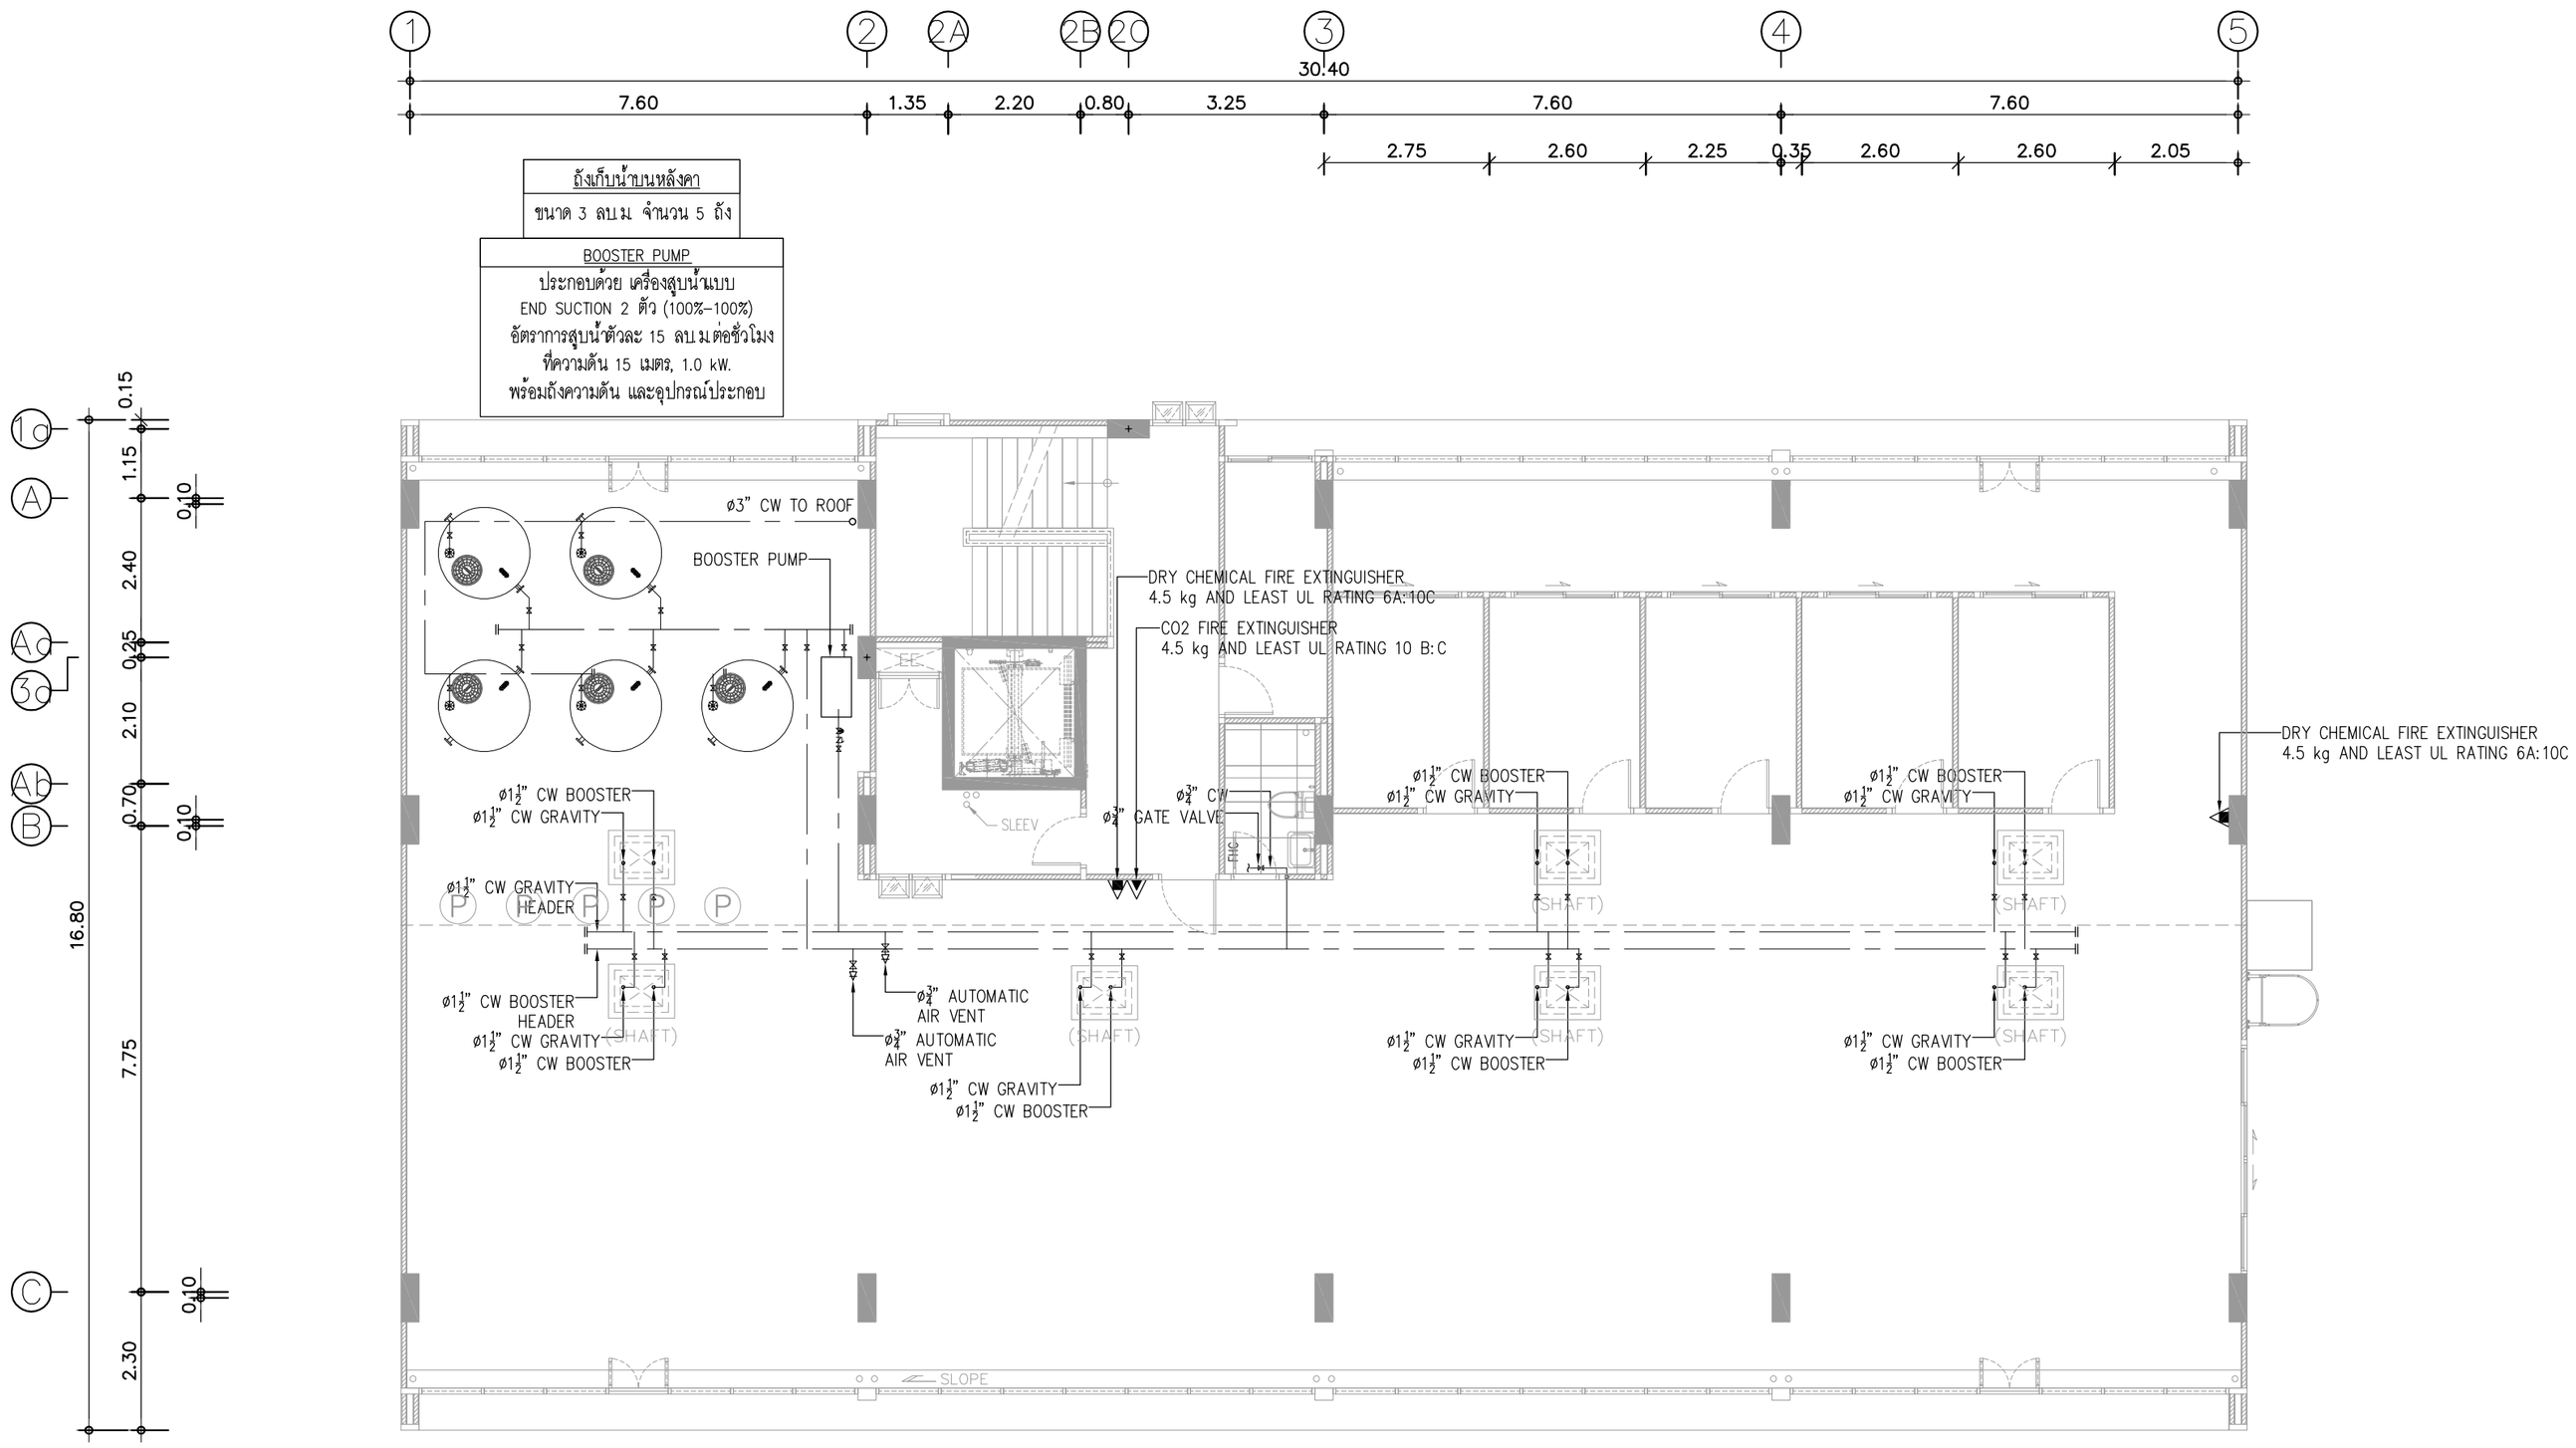

ผังระบบสุขาภิบาล (น้ำดี) ชั้นใต้หลังคา

SCALE 1:100

PROJECT NUMBER : VC2023-024

PROJECT

MACHI RESIDENCES

อาคารพักอาศัยรวม ค.ส.ล 7 ชั้น

OWNER

บริษัท ฤทธิกร ลิฟวิ่ง จำกัด

ARCHITECT :

อัคคะภัทร์ จิระอารียบุตร ส-สถ.3040

403 ซ.พัฒนาการ 50 พัฒนาการ

กรุงเทพมหานคร 10250

INTERIOR DESIGNER :

-

STRUCTURAL ENGINEER :

นายพงษ์ธวิทย์ คทาวุธเจริญกุล ลย.12291

ELECTRICAL ENGINEER :

นายภาคภูมิ คำพิทูรย์ ลฟก.5587

MECHANICAL ENGINEER :

SANITARY ENGINEER :

นส.อรวรรณ พลตรี ลส.134

DRAWING TITLE

ผังระบบสุขาภิบาล (น้ำดี) ชั้นใต้หลังคา

DRAWING FOR CONSTRUCTION


DRAW BY :	CHECKER :	REVISION :
Weerayuth L.	Akapatr C.	-

SCALE :	DRAWING NO.
1 : 100	SN-11
DATE : 20-10-2024	
FILE NAME :	JOB NO.

REVISION	DESCRIPTION

GERNERAL NOTE
DO NOT SCALE DRAWING ALL MEASUREMENT MUST BE
CHECKED AT THE SIDE BY THE CONTRACTOR
ALL DESIGN AND DRAWINGS ARE THE PROPERTY OF
MARCHTEN CO.,LTD
AND NOT BE USED WITH OUT THEIR WRITTEN PERMISSION

ARCHITECTURE / INTERIOR
บริษัท มาร์ชเทน จำกัด
403 ซ.พัฒนาการ 50 สวนหลวง กรุงเทพมหานคร 10250

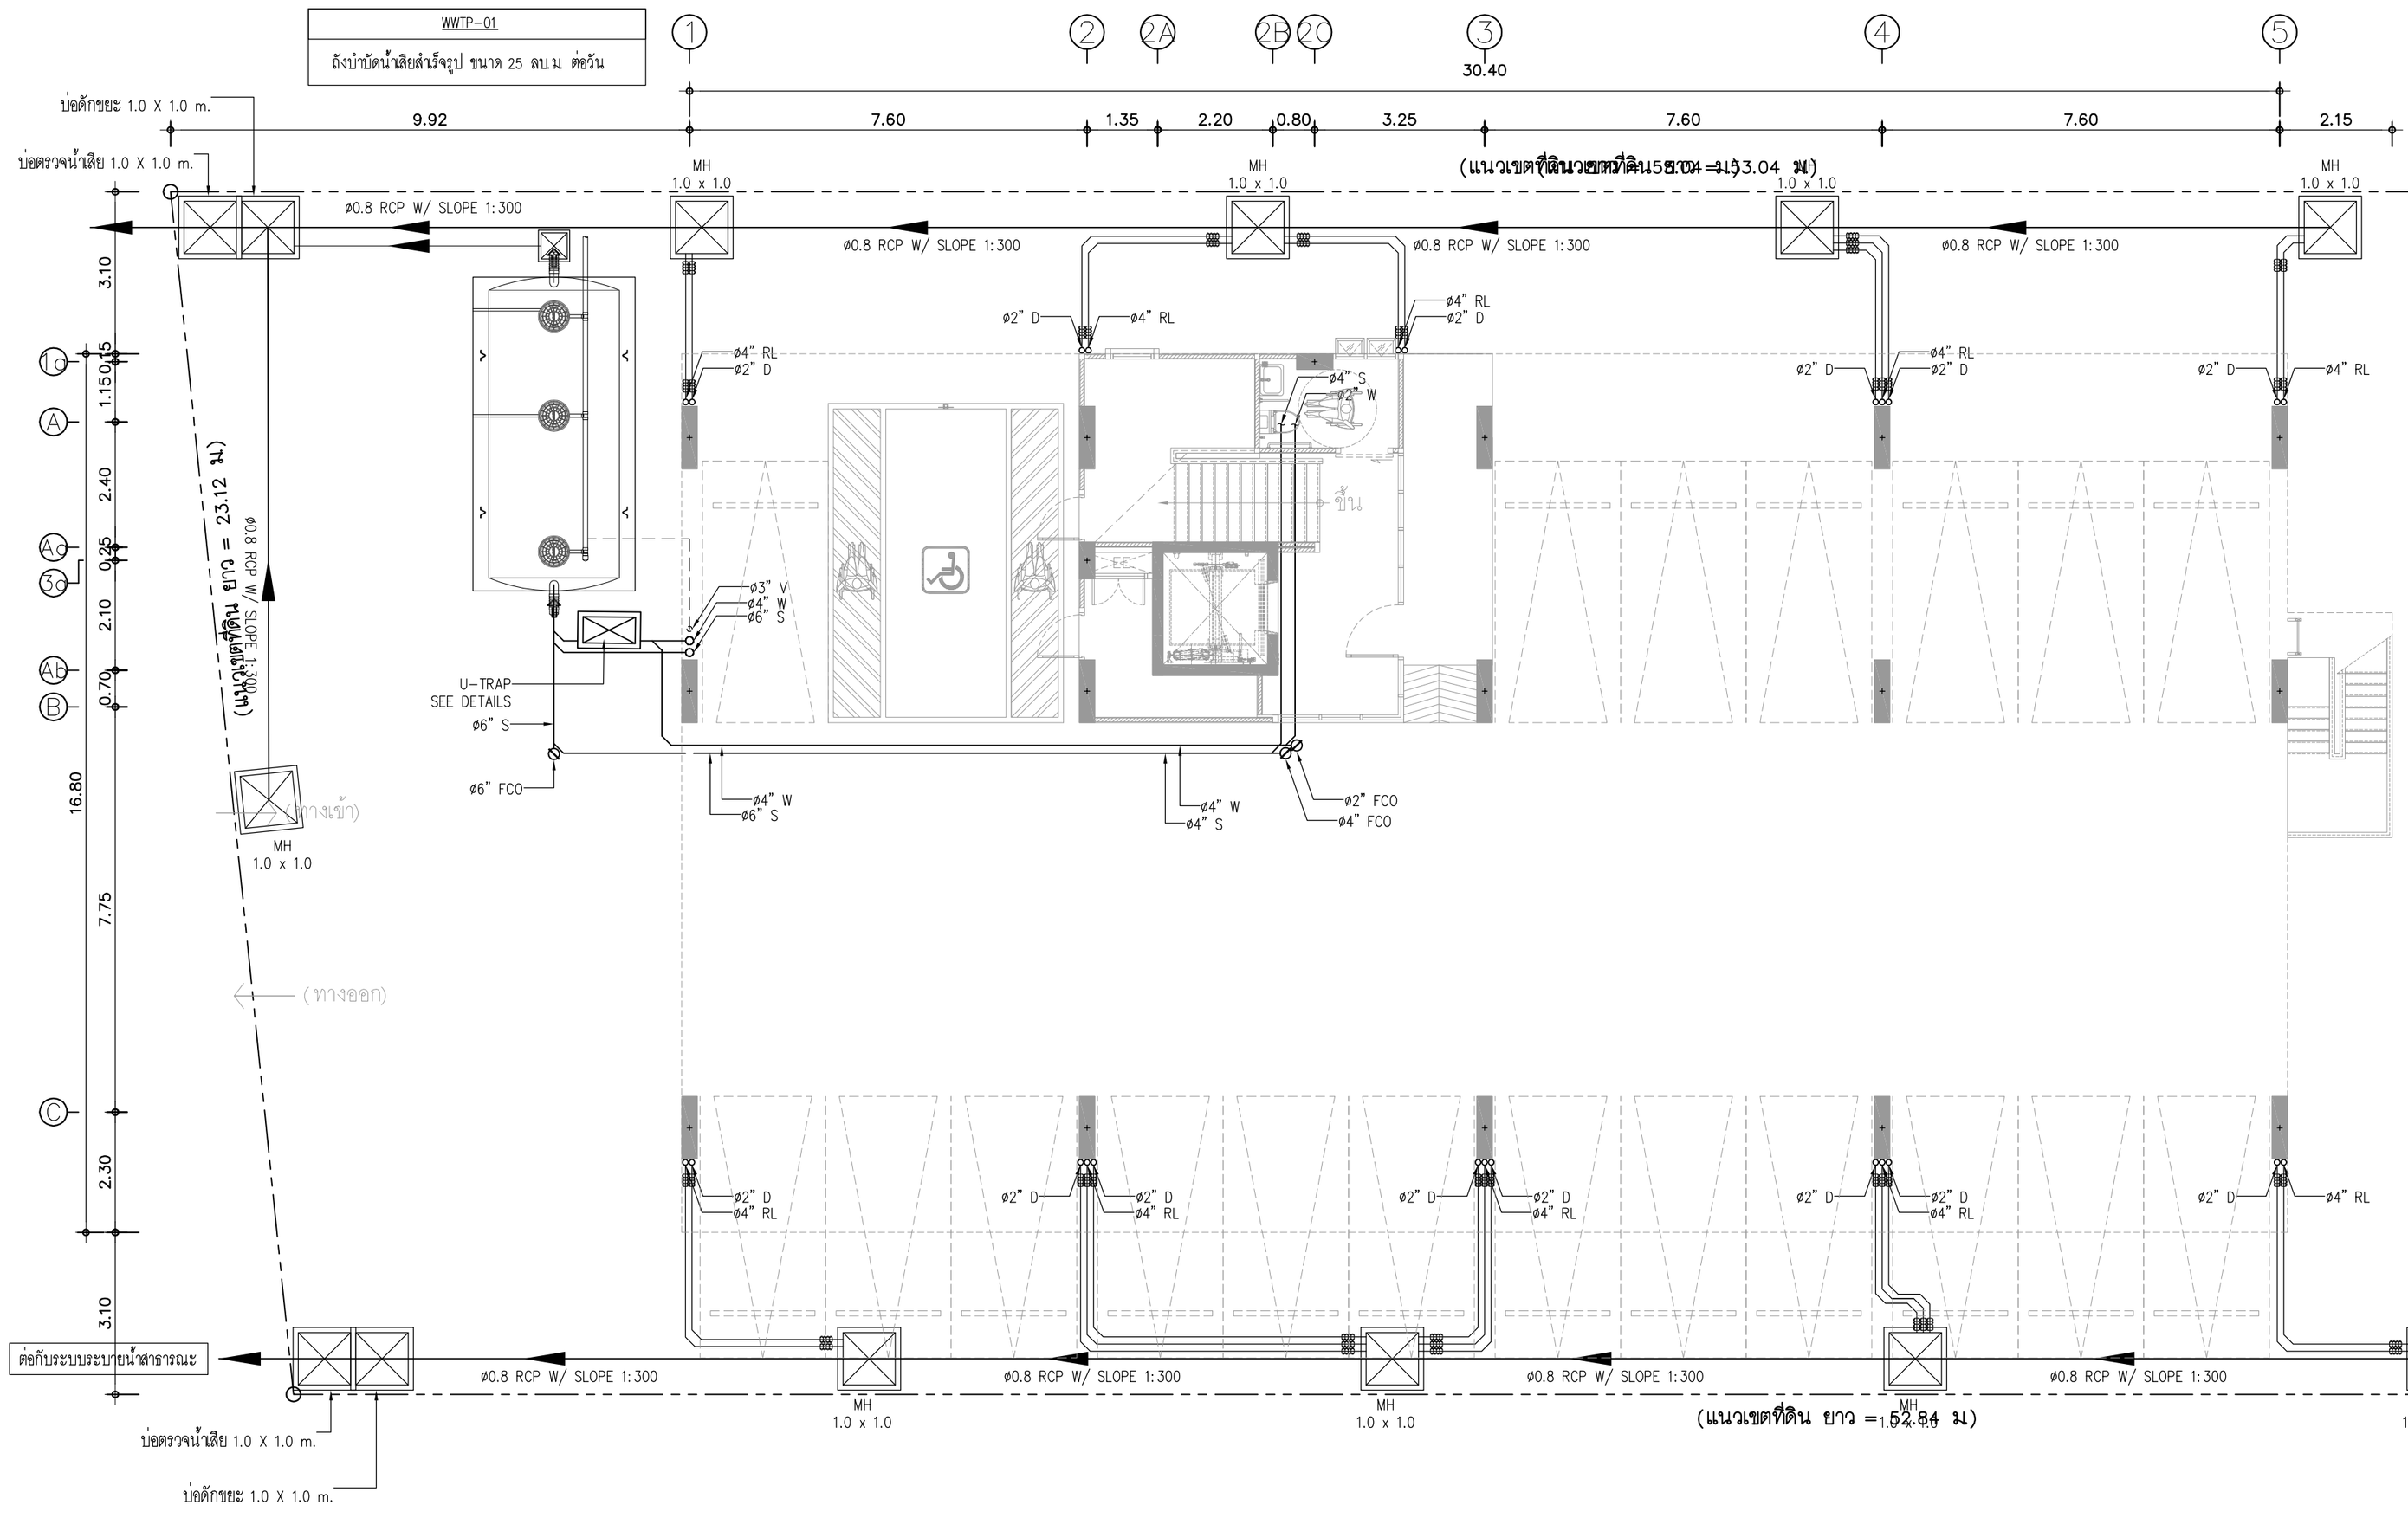

ผังระบบสุขาภิบาล (น้ำทิ้ง) ชั้น 1

SCALE 1:100

PROJECT NUMBER : VC2023-024

PROJECT

MACHI RESIDENCES

อาคารพักอาศัยรวม ค.ส.ล 7 ชั้น

OWNER

บริษัท ฤทธิกร ลิฟวิ่ง จำกัด

ARCHITECT :

อัคคะภัทร์ จิระอารียบุตร ส-สถ.3040

403 ซ.พัฒนาการ 50 พัฒนาการ

กรุงเทพมหานคร 10250

INTERIOR DESIGNER :

-

STRUCTURAL ENGINEER :

นายพงษ์ธวิทย์ คทาวุธเจริญกุล ลย.12291

ELECTRICAL ENGINEER :

นายภาคภูมิ คำพิทูรย์ ลฟก.5587

MECHANICAL ENGINEER :

SANITARY ENGINEER :

นส.อรวรรณ พลตรี ลส.134

DRAWING TITLE

ผังระบบสุขาภิบาล (น้ำทิ้ง) ชั้น 1

DRAWING FOR CONSTRUCTION

DRAW BY :	CHECKER :	REVISION :
Weerayuth L.	Akapatr C.	–

SCALE :	DRAWING NO.
1 : 100	SN-12
DATE : 20-10-2024	
FILE NAME :	JOB NO.

REVISION	DESCRIPTION

GERNERAL NOTE


DO NOT SCALE DRAWING ALL MEASUREMENT MUST BE **CHECKED AT THE SIDE BY THE CONTRACTOR**

ALL DESIGN AND DRAWINGS ARE THE PROPERTY OF MARCHTEN CO.,LTD **AND NOT BE USED WITH OUT THEIR WRITTEN PERMISSION**

ARCHITECTURE / INTERIOR

บริษัท มาร์ชเทน จำกัด

403 ซ.พัฒนาการ 50 สวนหลวง กรุงเทพมหานคร 10250

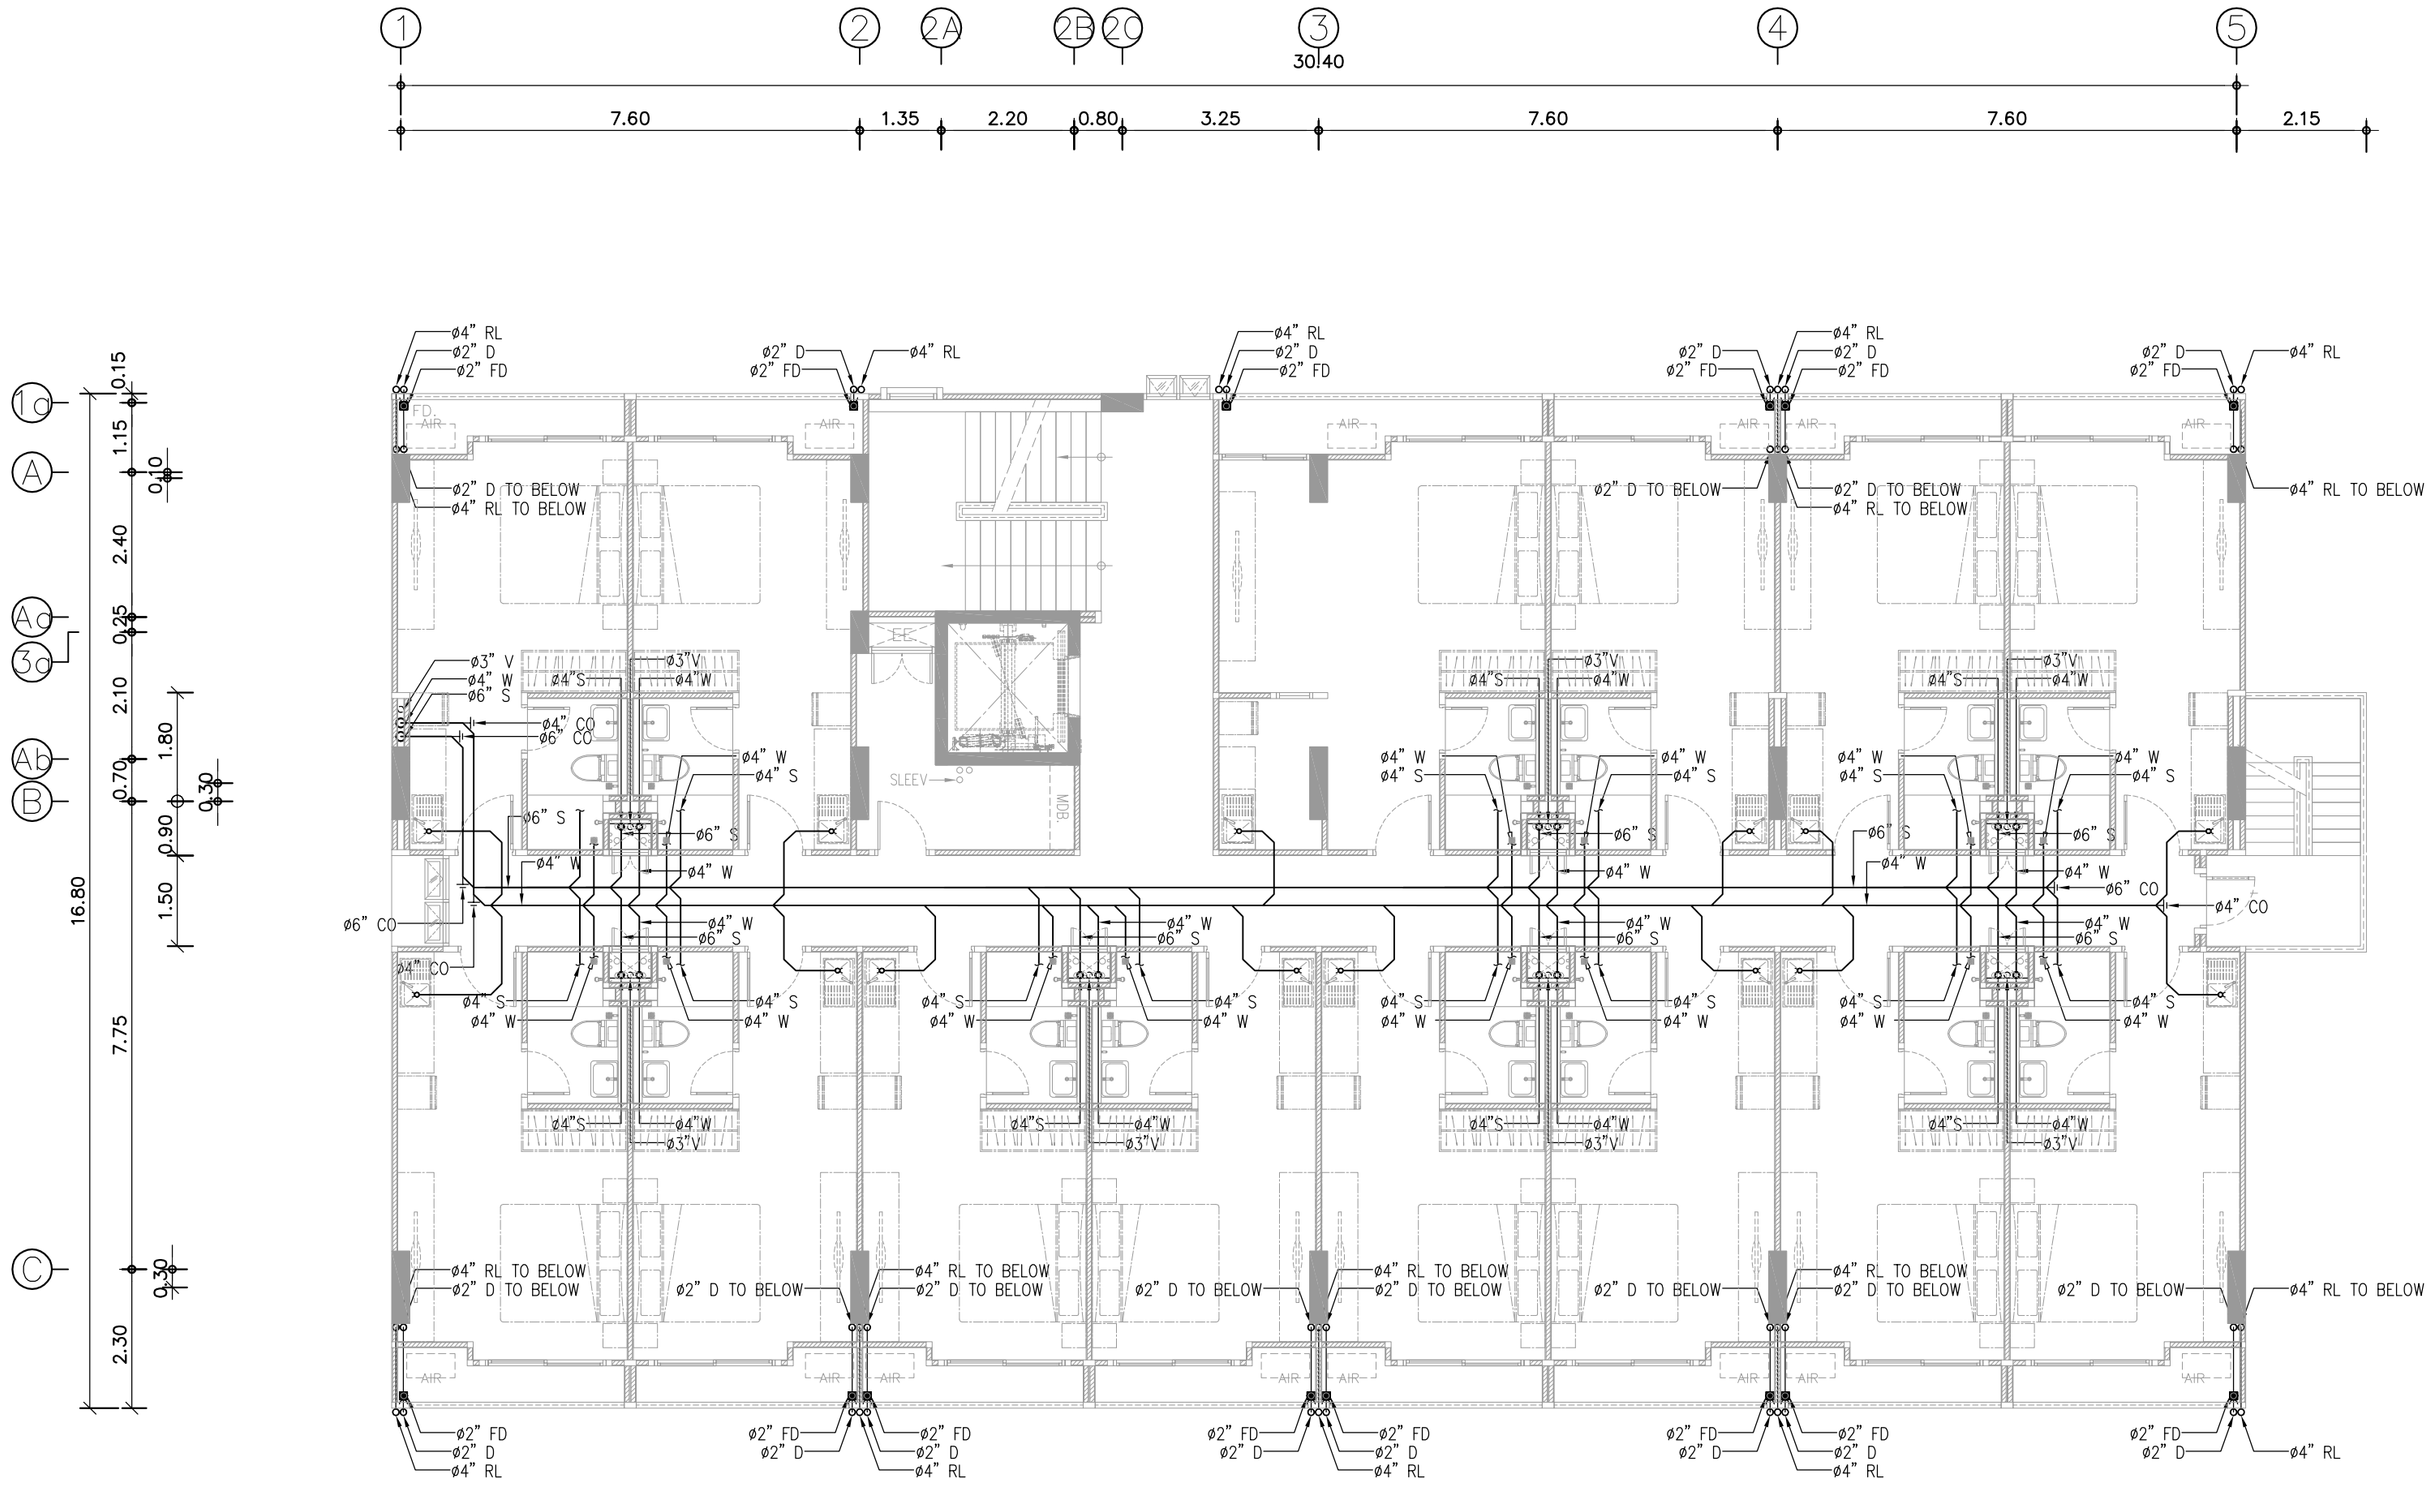

ผังระบบสุขาภิบาล (น้ำทิ้ง) ชั้น 2

SCALE 1:100

PROJECT NUMBER : VC2023-024

PROJECT

MACHI RESIDENCES

อาคารพักอาศัยรวม ค.ส.ล 7 ชั้น

OWNER

บริษัท ฤทธิกร ลิฟวิ่ง จำกัด

ARCHITECT :

อัคคะภัทร์ จิระอารียบุตร ส-สถ.3040

403 ซ.พัฒนาการ 50 พัฒนาการ

กรุงเทพมหานคร 10250

INTERIOR DESIGNER :

-

STRUCTURAL ENGINEER :

นายพงษ์ธวิทย์ คทาวุธเจริญกุล ลย.12291

ELECTRICAL ENGINEER :

นายภาคภูมิ คำพิทูรย์ ลฟก.5587

MECHANICAL ENGINEER :

SANITARY ENGINEER :

พล.อรวรรณ พลตรี ลส.134

DRAWING TITLE

ผังระบบสุขาภิบาล (น้ำทิ้ง) ชั้น 2

DRAWING FOR CONSTRUCTION

DRAW BY :	CHECKER :	REVISION :
Weerayuth L.	Akapatr C.	-

SCALE :	DRAWING NO.
1 : 100	SN-13
DATE : 20-10-2024	
FILE NAME :	JOB NO.

REVISION	DESCRIPTION


GERNERAL NOTE

DO NOT SCALE DRAWING ALL MEASUREMENT MUST BE **CHECKED AT THE SIDE BY THE CONTRACTOR**

ALL DESIGN AND DRAWINGS ARE THE PROPERTY OF MARCHTEN CO.,LTD **AND NOT BE USED WITH OUT THEIR WRITTEN PERMISSION**

ARCHITECTURE / INTERIOR

บริษัท มาร์ชเทน จำกัด
403 ซ.พัฒนาการ 50 สวนหลวง กรุงเทพมหานคร 10250

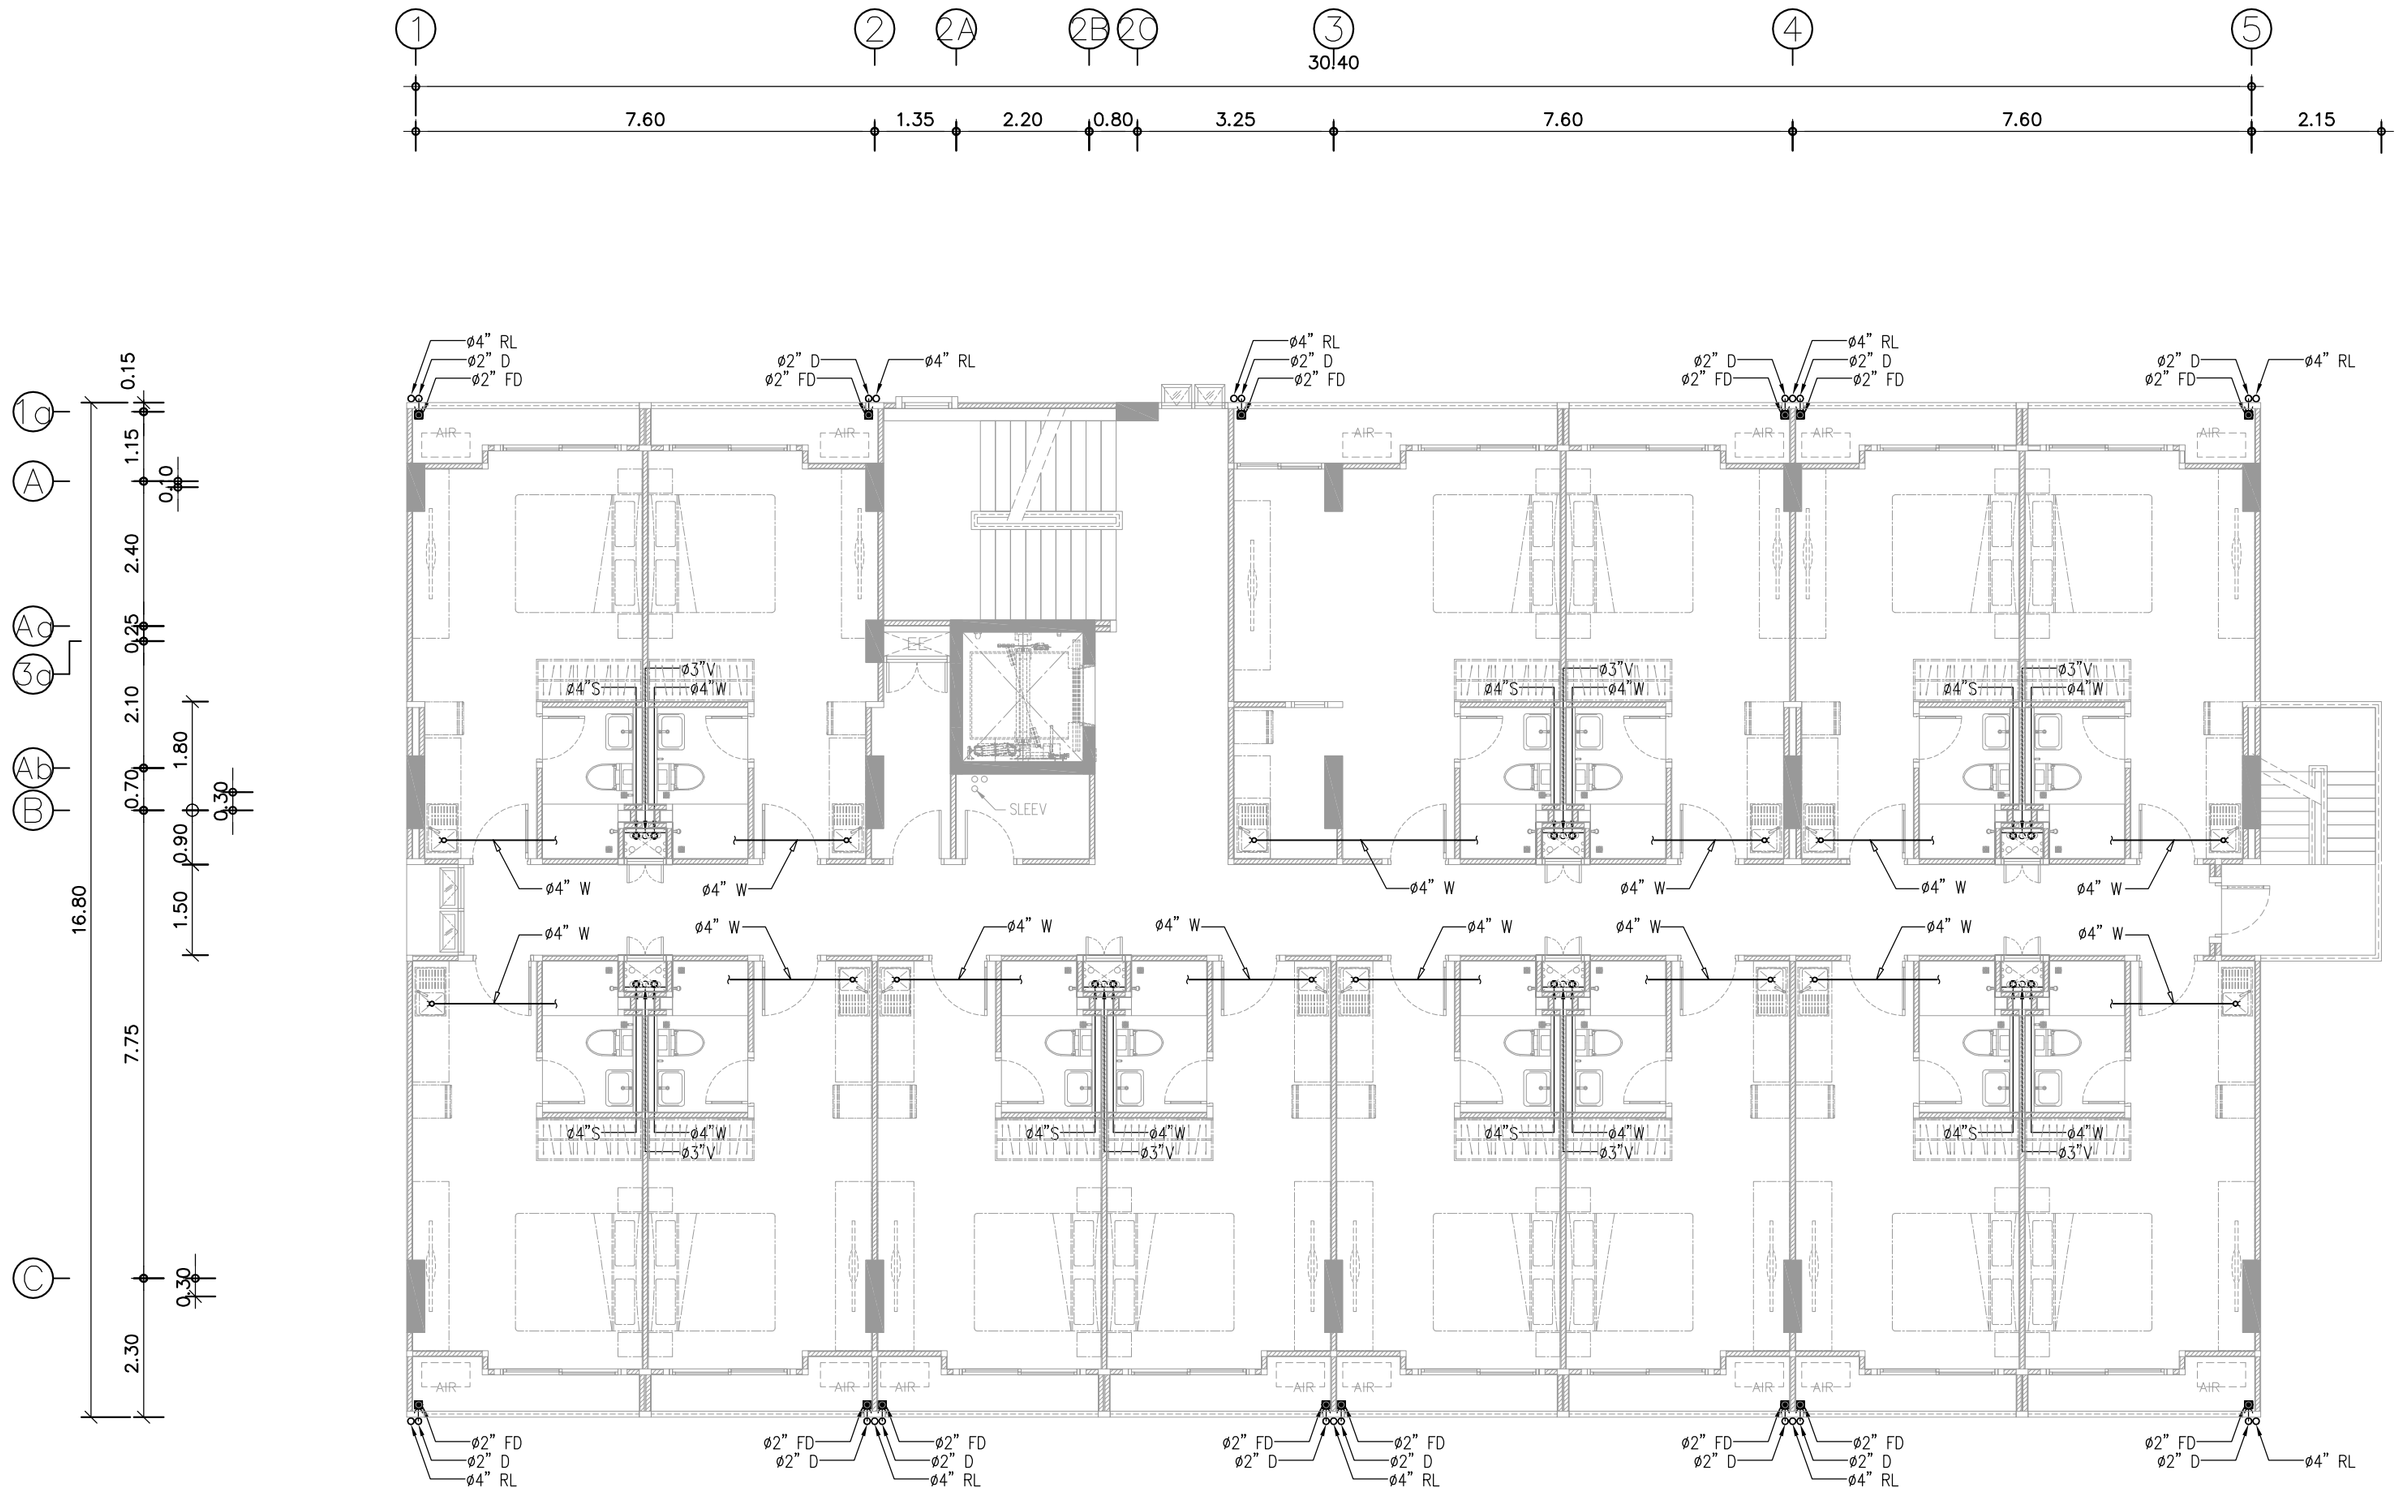

ผังระบบสุขาภิบาล (น้ำทิ้ง) ชั้น 3 – 5

SCALE 1:100

PROJECT NUMBER : VC2023–024

PROJECT

MACHI RESIDENCES

อาคารพักอาศัยรวม ค.ส.ล 7 ชั้น

OWNER

บริษัท ฤทธิกร ลิฟวิ่ง จำกัด

ARCHITECT :

อัคคะภัทร์ จิระอารีย์บุตร ส–สถ.3040

403 ซ.พัฒนาการ 50 พัฒนาการ

กรุงเทพมหานคร 10250

INTERIOR DESIGNER :

-

STRUCTURAL ENGINEER :

นายพงษ์ธวิทย์ คทาวุธเจริญกุล ลย.12291

ELECTRICAL ENGINEER :

นายภาคภูมิ คำพิทูรย์ ลฟก.5587

MECHANICAL ENGINEER :

SANITARY ENGINEER :

นส.อรวรรณ พลตรี ลส.134

DRAWING TITLE

ผังระบบสุขาภิบาล (น้ำทิ้ง) ชั้น 3 – 5

DRAWING FOR CONSTRUCTION

DRAW BY :	CHECKER :	REVISION :
Weerayuth L.	Akapatr C.	–

SCALE : 1 : 100

DRAWING NO. SN–14

DATE : 20–10–2024

FILE NAME :

JOB NO.

REVISION	DESCRIPTION

GERNERAL NOTE


DO NOT SCALE DRAWING ALL MEASUREMENT MUST BE **CHECKED AT THE SIDE BY THE CONTRACTOR**

ALL DESIGN AND DRAWINGS ARE THE PROPERTY OF MARCHTEN CO.,LTD **AND NOT BE USED WITH OUT THEIR WRITTEN PERMISSION**

ARCHITECTURE / INTERIOR

บริษัท มาร์ชเทน จำกัด

403 ซ.พัฒนาการ 50 สวนหลวง กรุงเทพมหานคร 10250

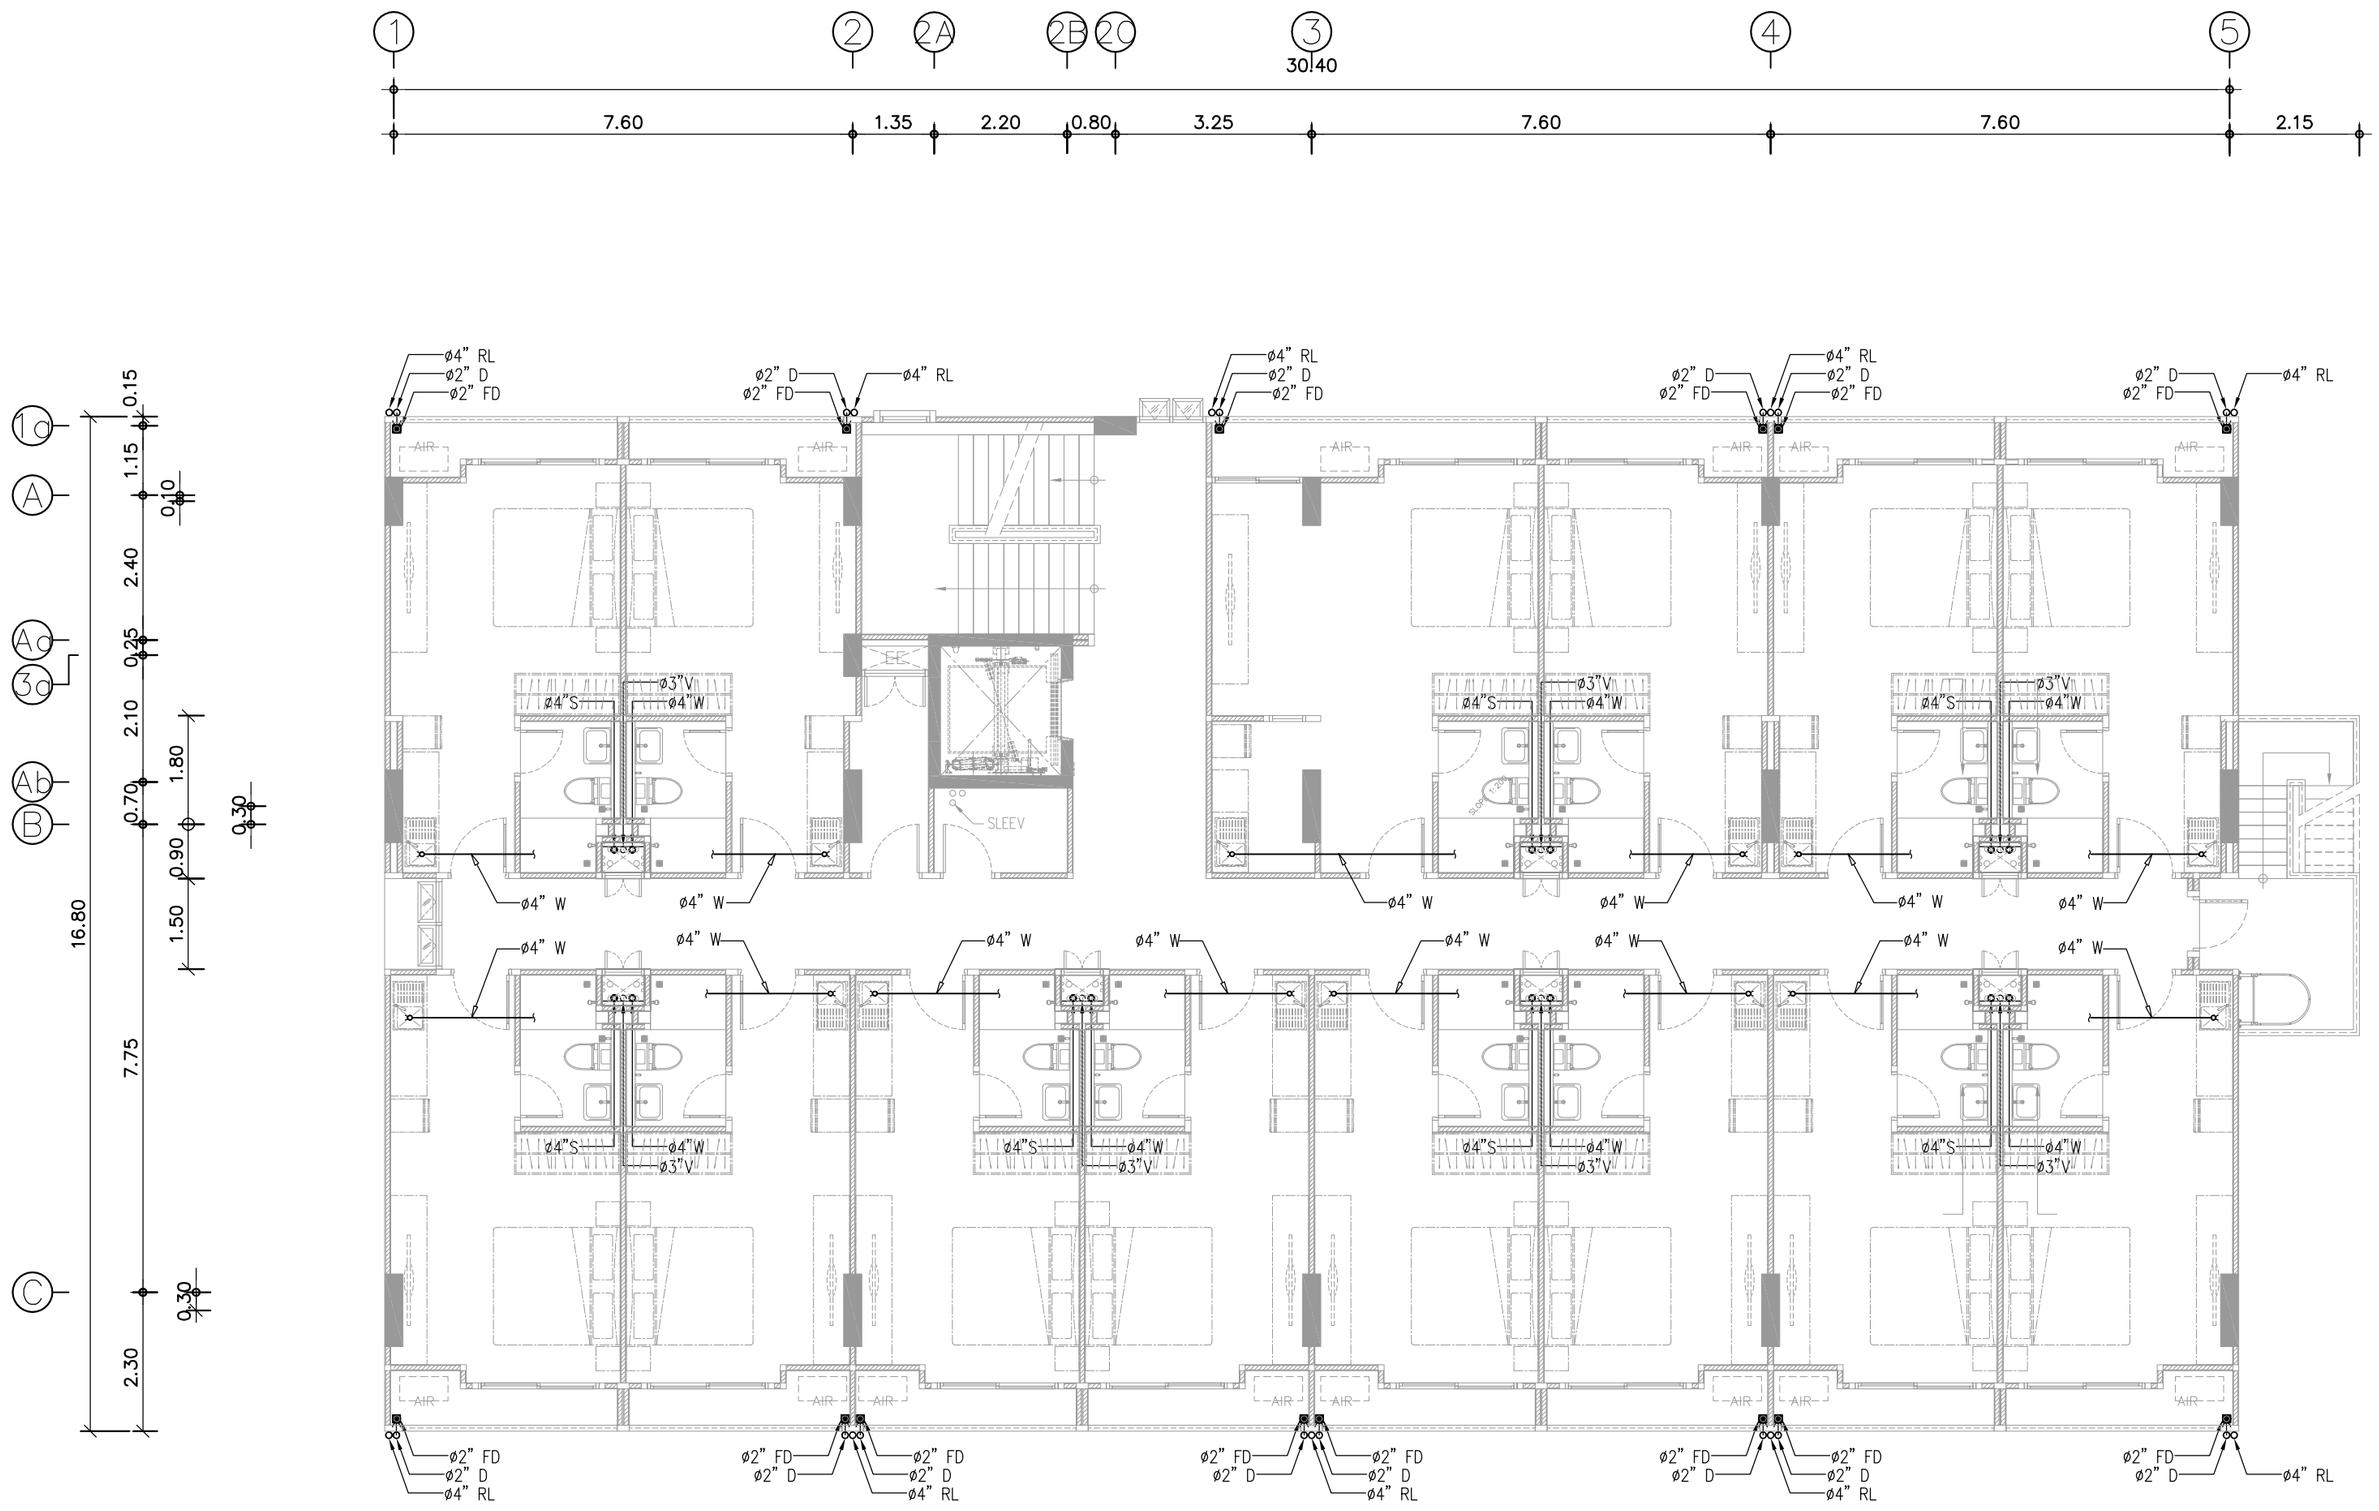

ผังระบบสุขาภิบาล (น้ำทิ้ง) ชั้น 6

SCALE 1:100

PROJECT NUMBER : VC2023-024

PROJECT

MACHI RESIDENCES

อาคารพักอาศัยรวม ค.ส.ล 7 ชั้น

OWNER

บริษัท ฤทธิกร ลิฟวิ่ง จำกัด

ARCHITECT :

อัคคะภัทร์ จิระอารีย์บุตร ส-สถ.3040

403 ซ.พัฒนาการ 50 พัฒนาการ

กรุงเทพมหานคร 10250

INTERIOR DESIGNER :

-

STRUCTURAL ENGINEER :

นายพงษ์ธวิทย์ คทาวุธเจริญกุล ลย.12291

ELECTRICAL ENGINEER :

นายภาคภูมิ คำพิทูรย์ ลฟก.5587

MECHANICAL ENGINEER :

SANITARY ENGINEER :

นส.อรวรรณ พลตรี ลส.134

DRAWING TITLE

ผังระบบสุขาภิบาล (น้ำทิ้ง) ชั้น 6

DRAWING FOR CONSTRUCTION

DRAW BY :	CHECKER :	REVISION :
Weerayuth L.	Akapatr C.	–

SCALE : 1 : 100

DRAWING NO. SN-15

DATE : 20-10-2024

FILE NAME :

JOB NO.

REVISION	DESCRIPTION

GERNERAL NOTE

DO NOT SCALE DRAWING ALL MEASUREMENT MUST BE

CHECKED AT THE SIDE BY THE CONTRACTOR

ALL DESIGN AND DRAWINGS ARE THE PROPERTY OF


MARCHTEN CO.,LTD

AND NOT BE USED WITH OUT THEIR WRITTEN PERMISSION

ARCHITECTURE / INTERIOR

บริษัท มาร์ชเทน จำกัด

403 ซ.พัฒนาการ 50 สวนหลวง กรุงเทพมหานคร 10250

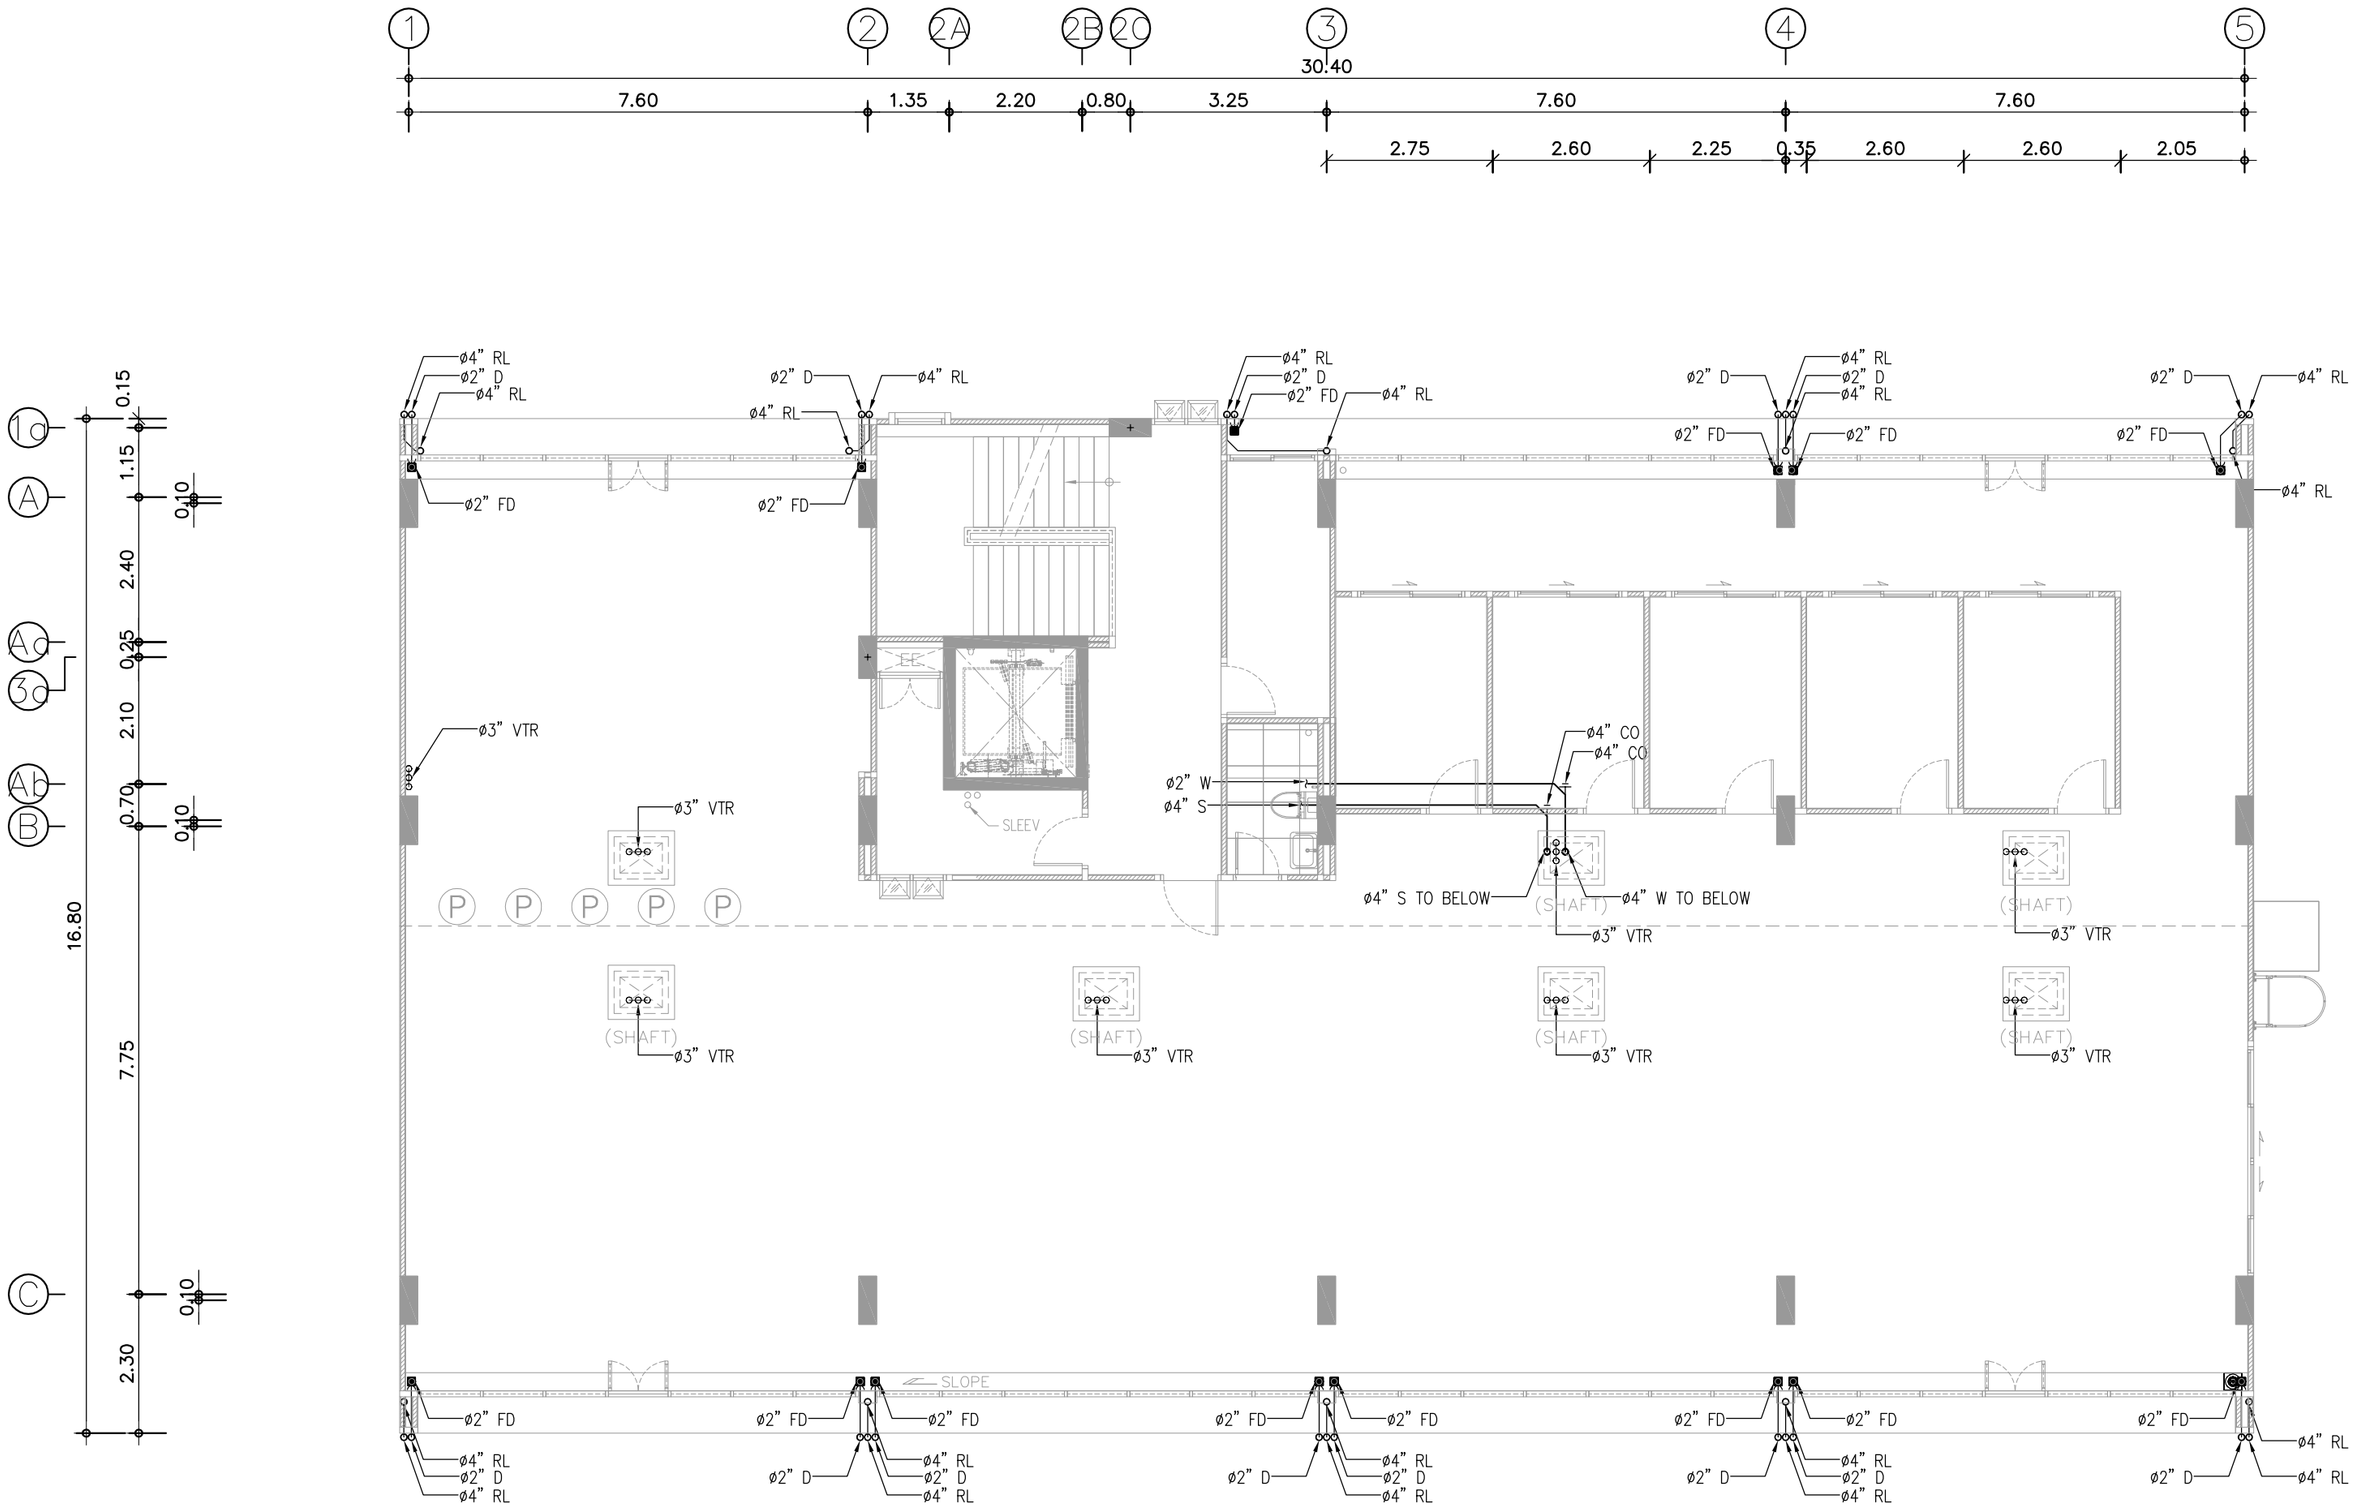

ผังระบบสุขาภิบาล (น้ำทิ้ง) ชั้นใต้หลังคา

SCALE 1:100

PROJECT NUMBER : VC2023-024

PROJECT

MACHI RESIDENCES

อาคารพักอาศัยรวม ค.ส.ล 7 ชั้น

OWNER

บริษัท ฤทธิกร ลิฟวิ่ง จำกัด

ARCHITECT :

อัคคะภัทร์ จิระอารียบุตร ส-สถ.3040

403 ซ.พัฒนาการ 50 พัฒนาการ

กรุงเทพมหานคร 10250

INTERIOR DESIGNER :

-

STRUCTURAL ENGINEER :

นายพงษ์ธวิทย์ คทาวุธเจริญกุล ลย.12291

ELECTRICAL ENGINEER :

นายภาคภูมิ คำพิทูรย์ ลฟก.5587

MECHANICAL ENGINEER :

SANITARY ENGINEER :

นส.อรวรรณ พลตรี ลส.134

DRAWING TITLE

ผังระบบสุขาภิบาล (น้ำทิ้ง) ชั้นใต้หลังคา

DRAWING FOR CONSTRUCTION

DRAW BY :	CHECKER :	REVISION :
Weerayuth L.	Akapatr C.	-

SCALE :	DRAWING NO.
1 : 100	SN-16
DATE : 20-10-2024	
FILE NAME :	JOB NO.

REVISION	DESCRIPTION

GERNERAL NOTE


DO NOT SCALE DRAWING ALL MEASUREMENT MUST BE **CHECKED AT THE SIDE BY THE CONTRACTOR**

ALL DESIGN AND DRAWINGS ARE THE PROPERTY OF MARCHTEN CO.,LTD **AND NOT BE USED WITH OUT THEIR WRITTEN PERMISSION**

ARCHITECTURE / INTERIOR

บริษัท มาร์ชเทน จำกัด

403 ซ.พัฒนาการ 50 สวนหลวง กรุงเทพมหานคร 10250

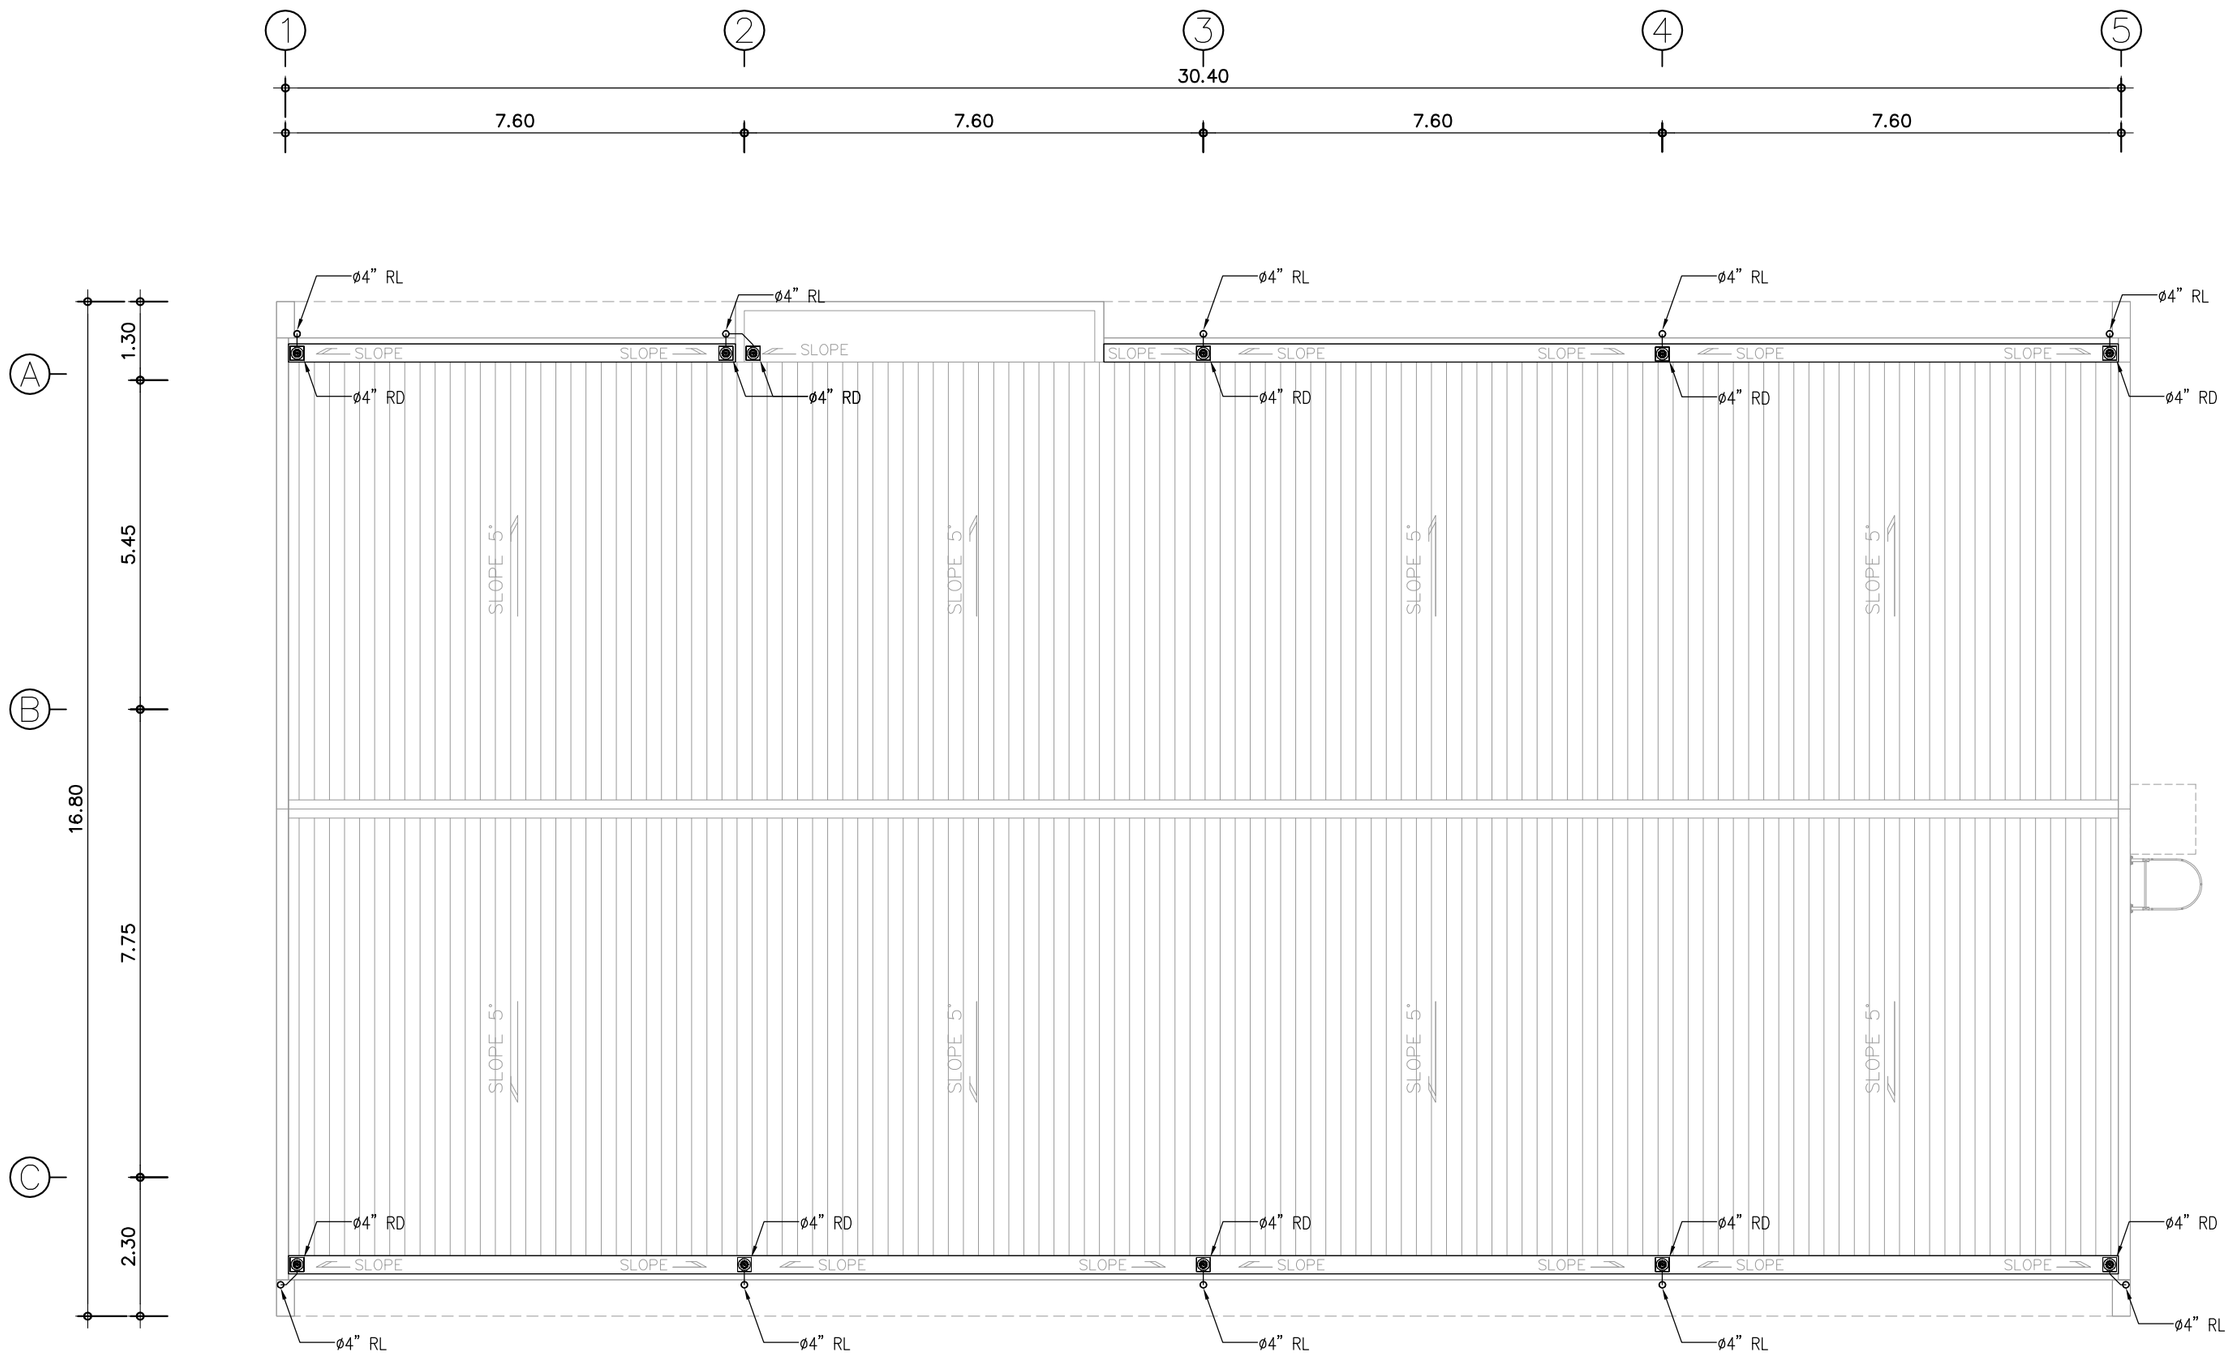

ผังระบบสุขาภิบาล หลังคา

SCALE 1:100

PROJECT NUMBER : VC2023-024

PROJECT

MACHI RESIDENCES

อาคารพักอาศัยรวม ค.ส.ล 7 ชั้น

OWNER

บริษัท ฤทธิกร ลิฟวิ่ง จำกัด

ARCHITECT :

อัคคะภัทร์ จิระอารียบุตร ส-สถ.3040

403 ซ.พัฒนาการ 50 พัฒนาการ

กรุงเทพมหานคร 10250

INTERIOR DESIGNER :

-

STRUCTURAL ENGINEER :

นายพงษ์ธวิทย์ คทาวุธเจริญกุล ลย.12291

ELECTRICAL ENGINEER :

นายภาคภูมิ คำพิทูรย์ ลฟก.5587

MECHANICAL ENGINEER :

SANITARY ENGINEER :

นส.อรวรรณ พลตรี ลส.134

DRAWING TITLE

ผังระบบสุขาภิบาล หลังคา

DRAWING FOR CONSTRUCTION

DRAW BY :	CHECKER :	REVISION :
Weerayuth L.	Akapatr C.	-


SCALE :	DRAWING NO.
1 : 100	SN-17
DATE : 20-10-2024	
FILE NAME :	JOB NO.

REVISION	DESCRIPTION


GERNERAL NOTE
DO NOT SCALE DRAWING ALL MEASUREMENT MUST BE
CHECKED AT THE SIDE BY THE CONTRACTOR
ALL DESIGN AND DRAWINGS ARE THE PROPERTY OF
MARCHTEN CO.,LTD
AND NOT BE USED WITH OUT THEIR WRITTEN PERMISSION

ARCHITECTURE / INTERIOR

บริษัท มาร์ชเทน จำกัด
403 ซ.พัฒนาการ 50 สวนหลวง กรุงเทพมหานคร 10250

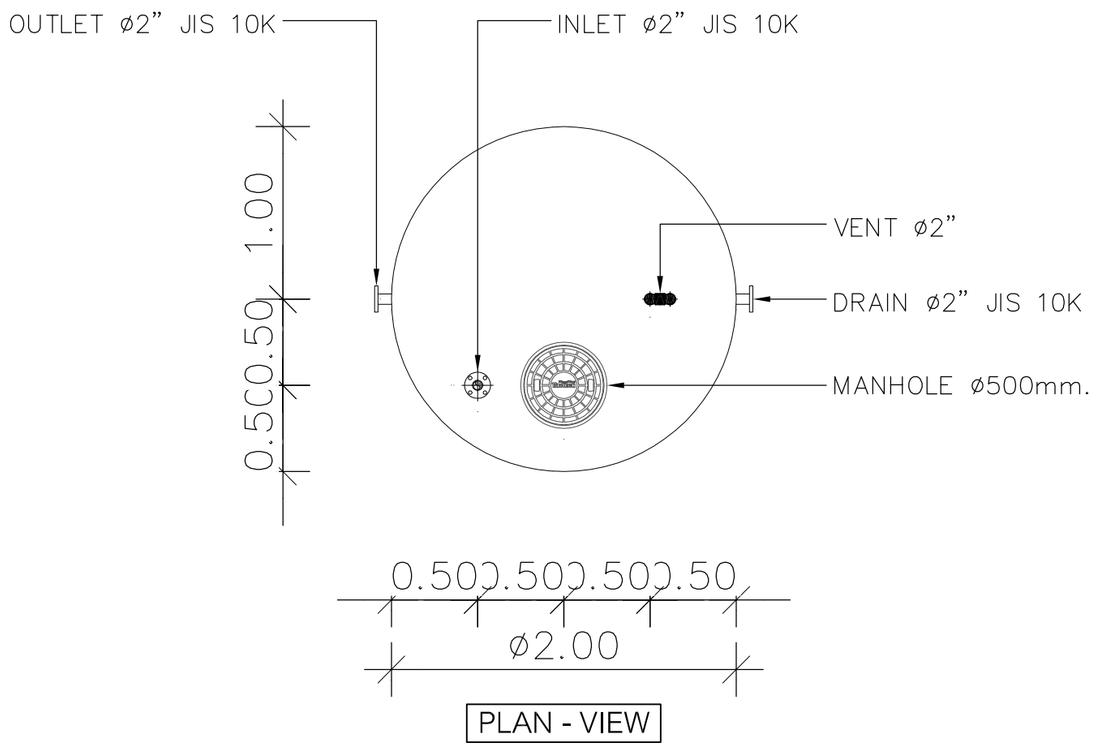

BIOTECH MODEL : F-50-H

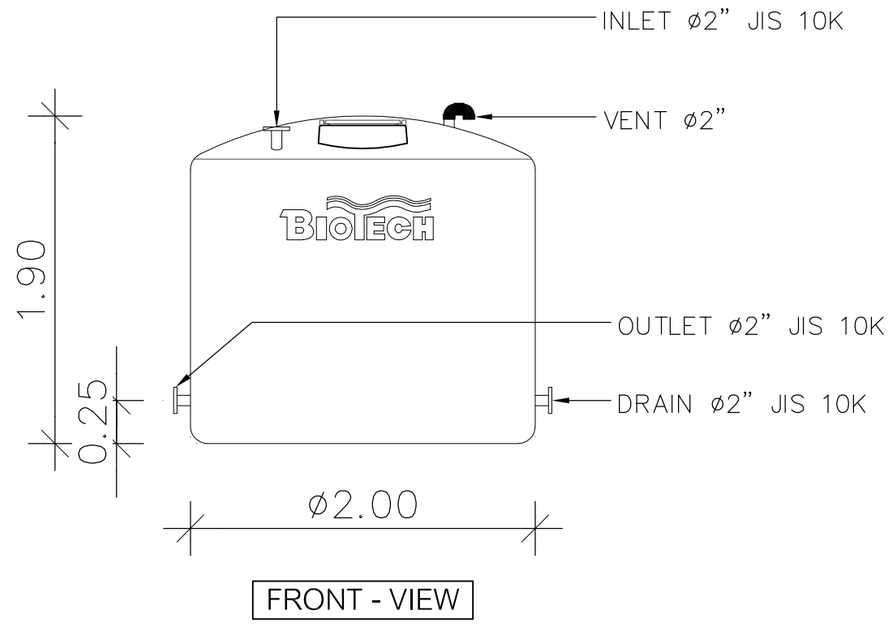

รายละเอียด : ถังเก็บน้ำทรงกระบอกแนวตั้ง รุ่น F-50-H

วัสดุ : ไฟเบอร์กล๊าสเสริมแรง (FRP)

ชนิดพันไขว้แนวเฉียง (HELICAL FILAMENT CROSS WINDING)


ขนาดถัง : เส้นผ่าศูนย์กลาง 2.0 เมตร สูง 1.9 เมตร ปริมาตรไม่น้อยกว่า 5 ลบ.ม.

ขนาดท่อ : ท่อเข้า 2นิ้ว ท่อออก 2นิ้ว ท่อระบายน้ำ2นิ้ว ท่อระบายอากาศ 2นิ้ว


ฝาถัง : ขนาด 500 มม.

แบบขยายถังสำรองน้ำประปา ขนาด 5 ลูกบาศก์เมตร

SCALE NTS.

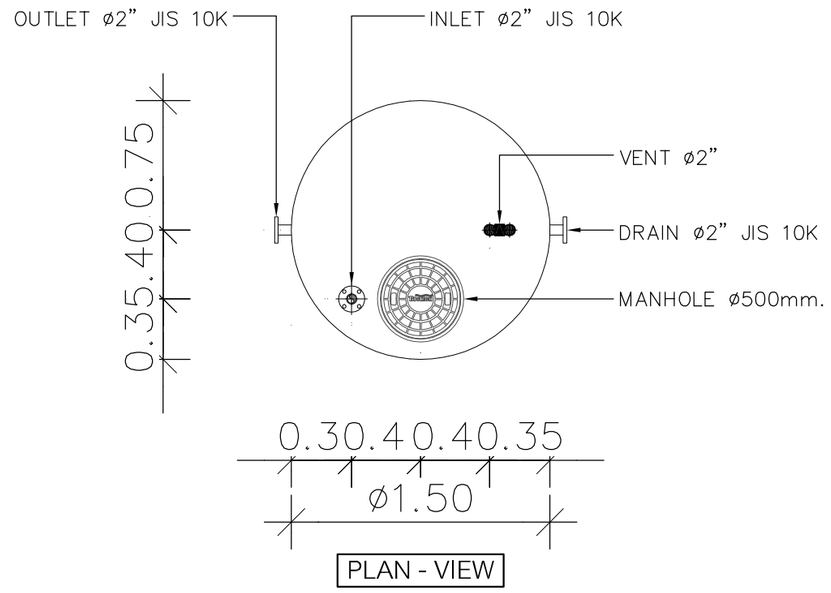

BIOTECH MODEL : F-30-H

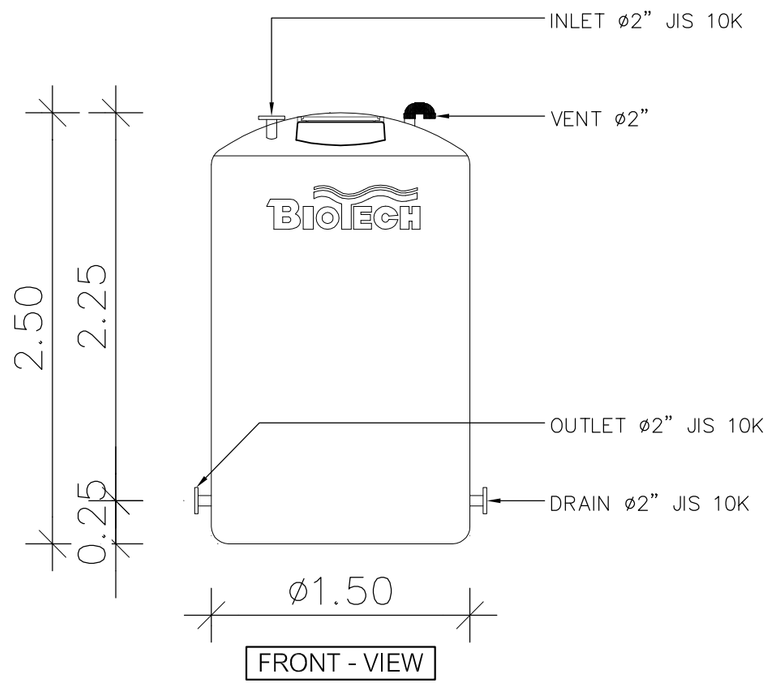

รายละเอียด : ถังเก็บน้ำทรงกระบอกแนวตั้ง รุ่น F-30-H

วัสดุ : ไฟเบอร์กล๊าสเสริมแรง (FRP)

ชนิดพันไขว้แนวเฉียง (HELICAL FILAMENT CROSS WINDING)

ขนาดถัง : เส้นผ่าศูนย์กลาง 1.5 เมตร สูง 2.5 เมตร ปริมาตรไม่น้อยกว่า 3.0 ลบ.ม.

ขนาดท่อ : ท่อเข้า 2นิ้ว ท่อออก 2นิ้ว ท่อระบายน้ำ 2นิ้ว ท่อระบายอากาศ 2นิ้ว

ฝาถัง : ขนาด 500 มม.

แบบขยายถังสำรองน้ำประปา ขนาด 3 ลูกบาศก์เมตร

SCALE NTS.

PROJECT NUMBER : VC2023-024

PROJECT

MACHI RESIDENCES

อาคารพักอาศัยรวม ค.ส.ล 7 ชั้น

OWNER

บริษัท ฤทธิกร ลิฟวิ่ง จำกัด

ARCHITECT :

อัคคะภัทร์ จิระอารียบุตร ส-สถ.3040

403 ซ.พัฒนาการ 50 พัฒนาการ

กรุงเทพมหานคร 10250

INTERIOR DESIGNER :

-

STRUCTURAL ENGINEER :

นายพงษ์ธวิทย์ คทาวุธเจริญกุล ลย.12291

ELECTRICAL ENGINEER :

นายภาคภูมิ คำพิทูรย์ ลฟก.5587

MECHANICAL ENGINEER :

SANITARY ENGINEER :

นส.อรวรรณ พลตรี ลส.134

DRAWING TITLE

แบบขยายถังสำรองน้ำประปา ขนาด 5 ลูกบาศก์เมตร

แบบขยายถังสำรองน้ำประปา ขนาด 3 ลูกบาศก์เมตร

DRAWING FOR CONSTRUCTION

DRAW BY :	CHECKER :	REVISION :
Weerayuth L.	Akapatr C.	–

SCALE :	DRAWING NO.
1 : 100	SN-18
DATE : 20-10-2024	
FILE NAME :	JOB NO.


REVISION	DESCRIPTION

GERNERAL NOTE
DO NOT SCALE DRAWING ALL MEASUREMENT MUST BE
CHECKED AT THE SIDE BY THE CONTRACTOR
ALL DESIGN AND DRAWINGS ARE THE PROPERTY OF
MARCHTEN CO.,LTD
AND NOT BE USED WITH OUT THEIR WRITTEN PERMISSION

ARCHITECTURE / INTERIOR


บริษัท มาร์ชเทน จำกัด

403 ซ.พัฒนาการ 50 สวนหลวง กรุงเทพมหานคร 10250

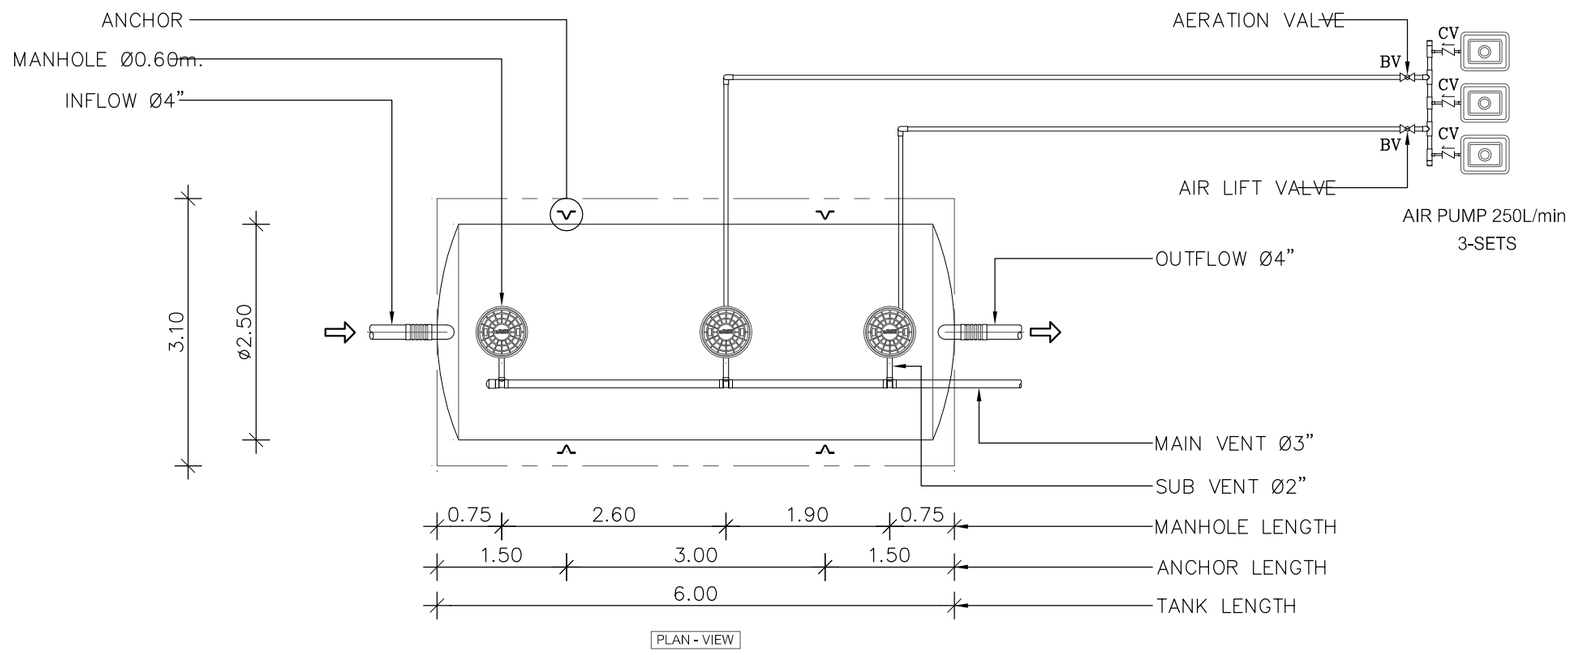


PLAN - VIEW


BIOTECH MODEL : CAB-25-D2.5

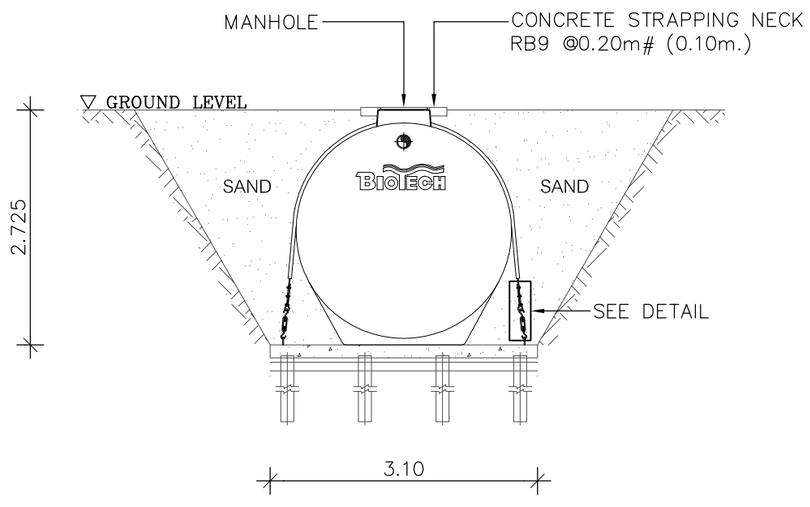


LEFT SIDE - VIEW

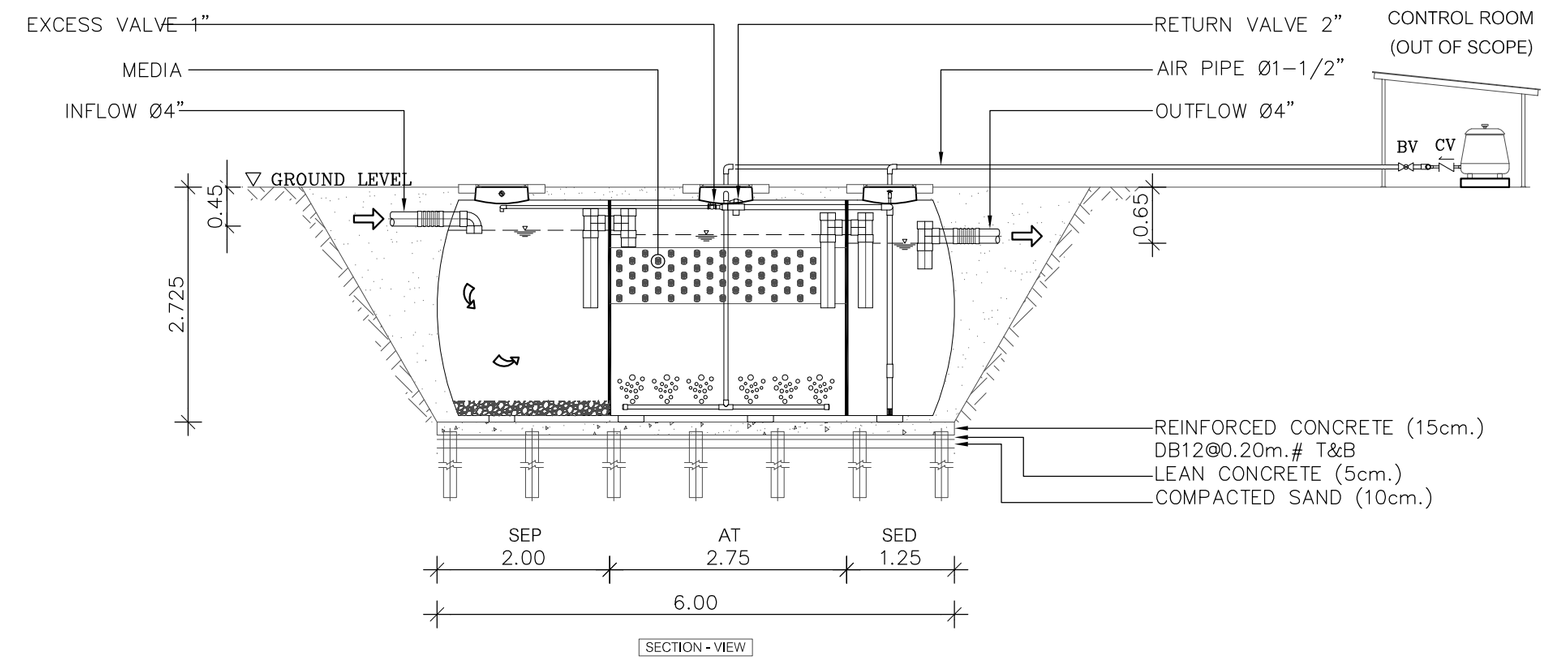


SECTION - VIEW

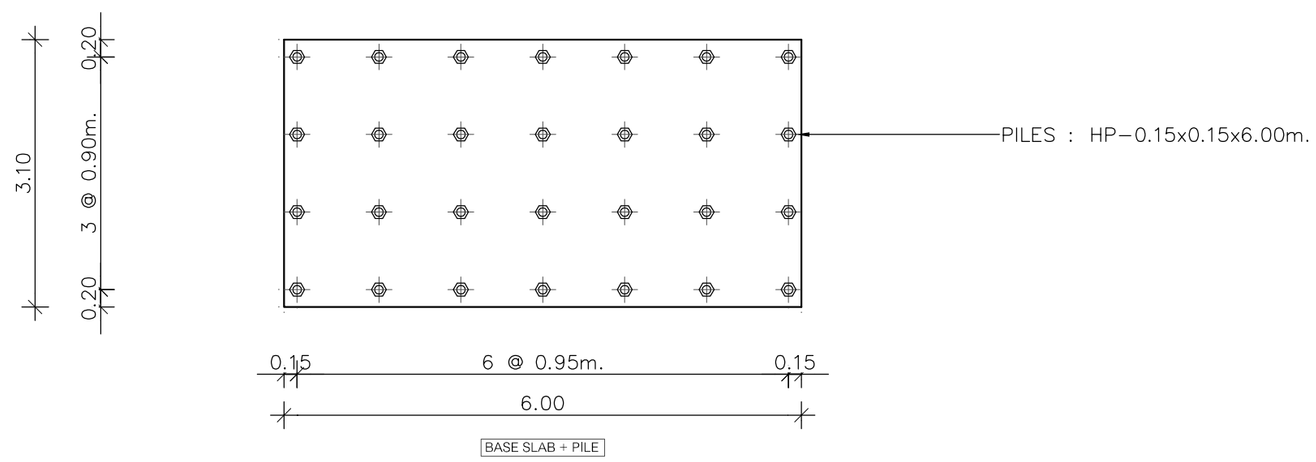

BASE SLAB + PILE

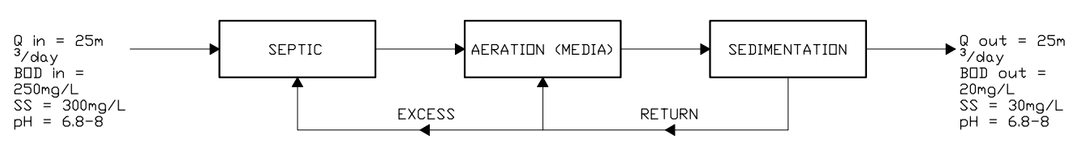

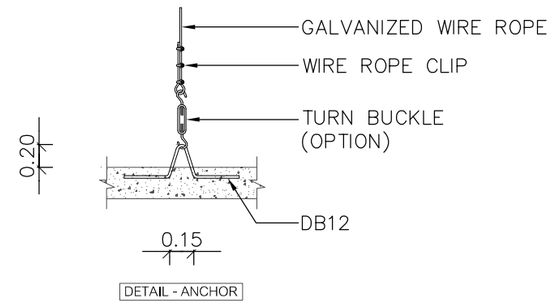

DETAIL - ANCHOR

BIOTECH MODEL : CAB-25-D2.5		
No.	ITEM	DETAIL
1	PROCESS	CONTACT AERATION BIOFILTER BOD IN < 250 mg/L, BOD OUT < 20 mg/L
2	RETURN&EXCESS SLUDGE	AIR LIFT PUMP
3	DIMENSION	Ø=2.5 m , L=6.0 m , H=2.725 m , THICKNESS 8 mm.
4	TANK VOLUME	28.25 m^3
5	MEDIA	BIO MEDIA , SURFACE AREA 105 sq.m./cu.m. (MEDIA VOLUME 6.37 m^3)
6	BODY	FIBERGLASS REINFORCE PLASTIC (FRP.) HELICAL FILAMENT CROSS WINDING TYPE , TOLERATED TO ACID/BASE CORROSION.
7	INFLOW , OUTFLOW , AIR PIPE	PVC.
8	MANHOLE COVER	ABS. Ø600mm. x 3
9	AIR PUMP	250 L/min , 1 phase (220V) , (3-DUTY)
10	SLING GALVANIZED WIRE ROPE	2 SETS (8 mm.)
11	STANDARD	ได้รับการรับรองมาตรฐานสากล ISO 9001 : 2015 ในงานการผลิต

Remark
1. Back fill with coarse sand only.
2. The foundation structure is just the installation guideline. The actual foundation use must be designed according to soil load condition at the site under control and consulting by civil engineers.
3. Install the tank to the cover to be at ground level. If necessary to install the tank below the soil level, the soil level over cover must not be more than 60 cm. in order to be able to open the cover for service.
4. The water is immediately added after tank installation.

แบบขยายถังบำบัดน้ำเสียสำเร็จรูป ขนาด 25 ลูกบาศก์เมตรต่อวัน

SCALE NTS.

PROJECT NUMBER : VC2023-024

PROJECT

MACHI RESIDENCES

อาคารพักอาศัยรวม ค.ส.ล 7 ชั้น

OWNER

บริษัท ฤทธิกร ลิฟวิ่ง จำกัด

ARCHITECT :

อัคคะภัทร์ จิระอารียบุตร ส-สถ.3040

403 ซ.พัฒนาการ 50 พัฒนาการ

กรุงเทพมหานคร 10250

INTERIOR DESIGNER :

-

STRUCTURAL ENGINEER :

นายพงษ์ธวิทย์ คทาวุธเจริญกุล ลย.12291

ELECTRICAL ENGINEER :

นายภาคภูมิ คำพิทูรย์ ลฟก.5587

MECHANICAL ENGINEER :

SANITARY ENGINEER :

พล.อรวรรณ พลตรี ลส.134

DRAWING TITLE

แบบขยายถังบำบัดน้ำเสียสำเร็จรูป

ขนาด 25 ลูกบาศก์เมตรต่อวัน

DRAWING FOR CONSTRUCTION


DRAW BY :	CHECKER :	REVISION :
Weerayuth L.	Akapatr C.	-

SCALE :	DRAWING NO.
1 : 100	SN-19
DATE : 20-10-2024	
FILE NAME :	JOB NO.


REVISION	DESCRIPTION

GERNERAL NOTE
DO NOT SCALE DRAWING ALL MEASUREMENT MUST BE
CHECKED AT THE SIDE BY THE CONTRACTOR
ALL DESIGN AND DRAWINGS ARE THE PROPERTY OF
MARCHTEN CO.,LTD
AND NOT BE USED WITH OUT THEIR WRITTEN PERMISSION

ARCHITECTURE / INTERIOR
บริษัท มาร์ชเทน จำกัด
403 ซ.พัฒนาการ 50 สวนหลวง กรุงเทพมหานคร 10250

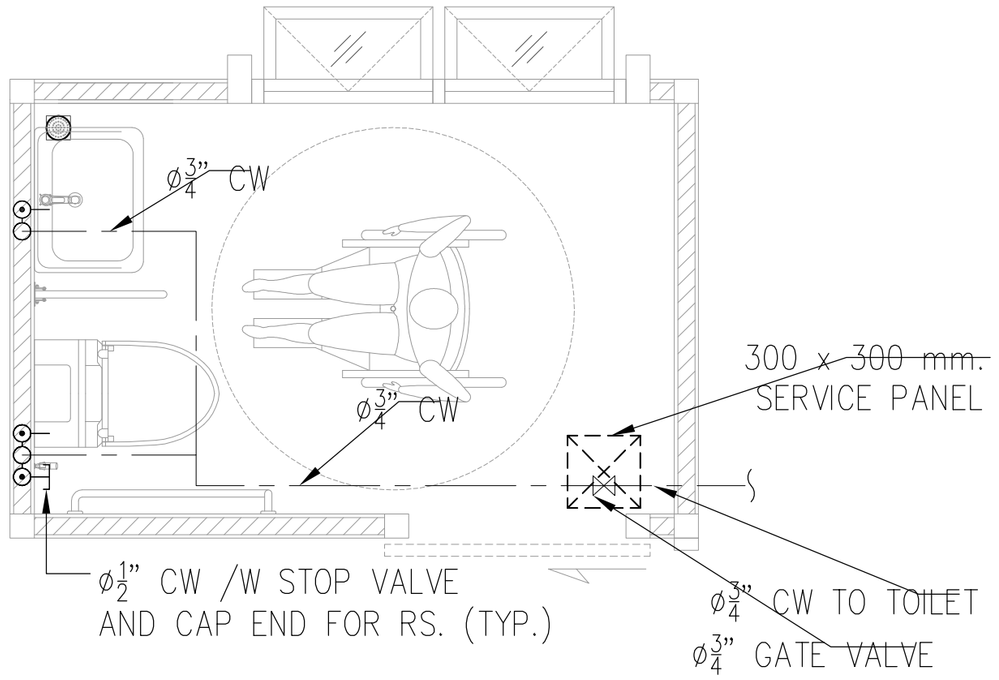


ผังระบบท่อน้ำประปา

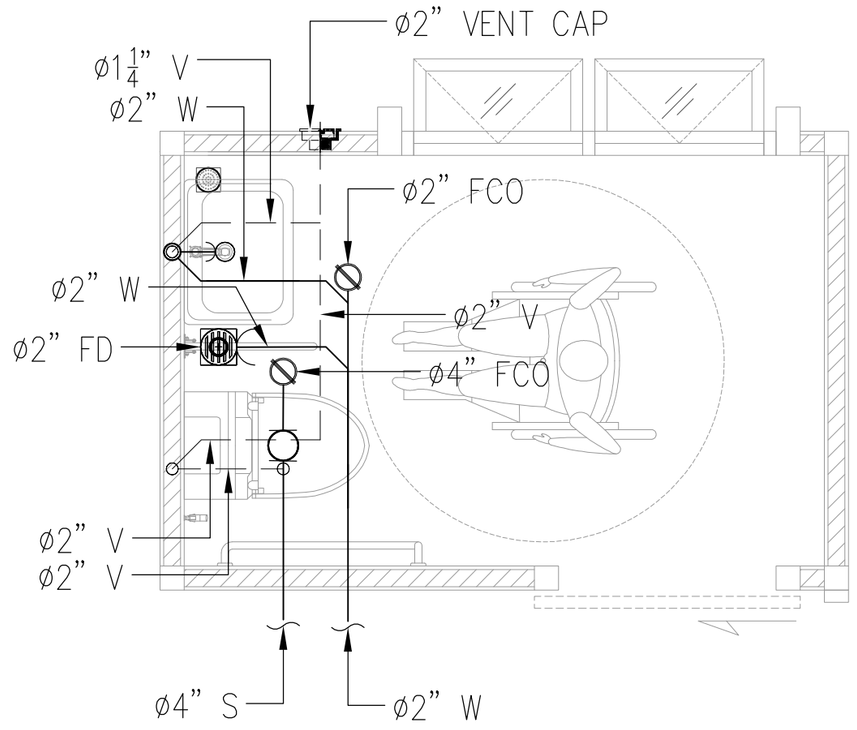


ผังระบบท่อน้ำโสโครก ท่อน้ำเสีย และท่อระบายอากาศ

แบบขยายห้องน้ำ WC-1

SCALE 1:25

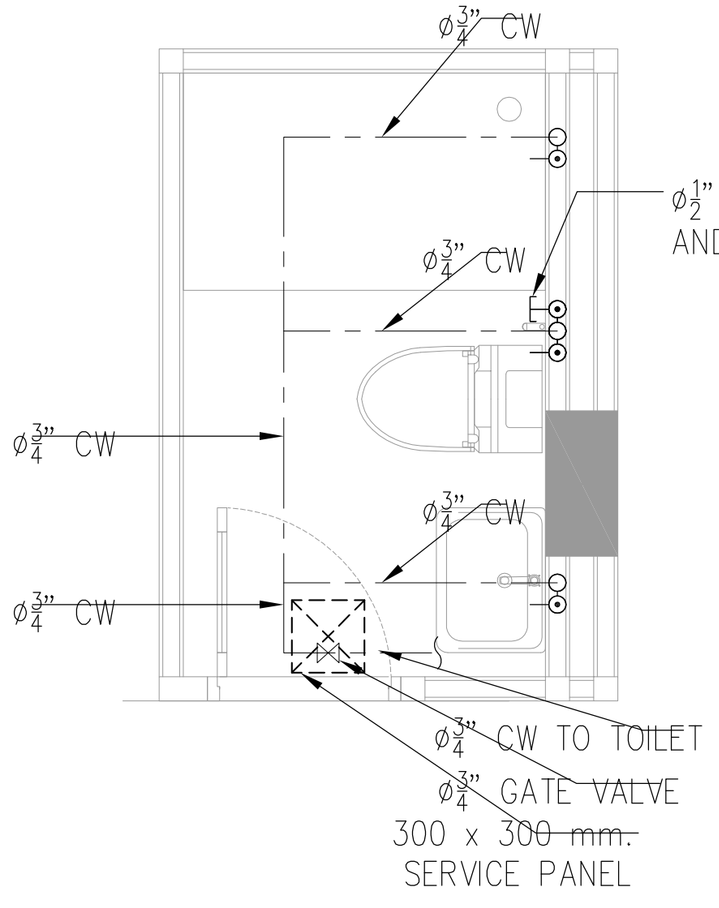

ผังระบบท่อน้ำประปา

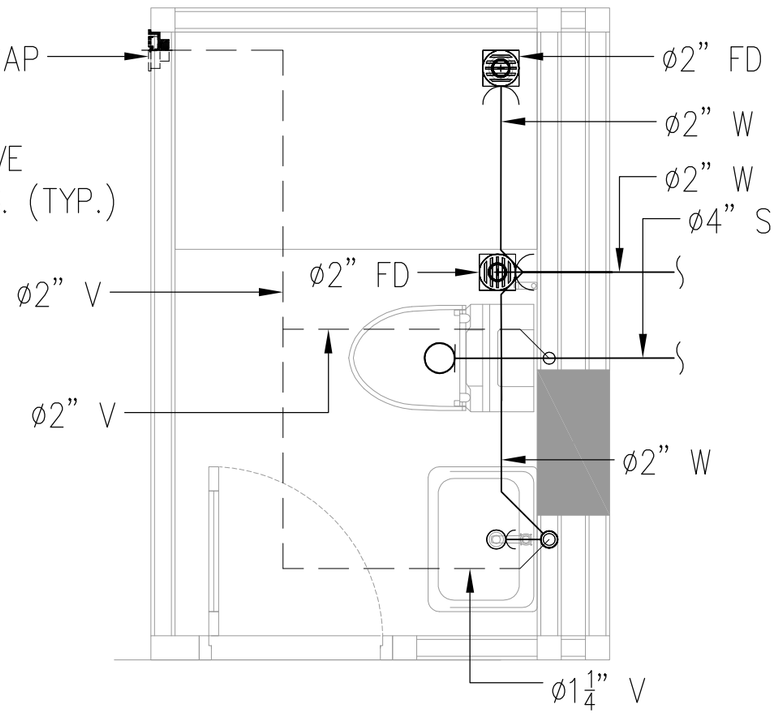

ผังระบบท่อน้ำโสโครก ท่อน้ำเสีย และท่อระบายอากาศ

แบบขยายห้องน้ำ WC-3

SCALE 1:25

PROJECT NUMBER : VC2023-024

PROJECT

MACHI RESIDENCES

อาคารพักอาศัยรวม ค.ส.ล 7 ชั้น

OWNER

บริษัท ฤทธิกร ลิฟวิ่ง จำกัด

ARCHITECT :

อัคคะภัทร์ จิระอารียบุตร ส-สถ.3040

403 ซ.พัฒนาการ 50 พัฒนาการ

กรุงเทพมหานคร 10250

INTERIOR DESIGNER :

-

STRUCTURAL ENGINEER :

นายพงษ์ธวิทย์ คทาวุธเจริญกุล ลย.12291

ELECTRICAL ENGINEER :

นายภาคภูมิ คำพิทูรย์ ลฟก.5587

MECHANICAL ENGINEER :

SANITARY ENGINEER :

นส.อรวรรณ พลตรี ลส.134

DRAWING TITLE

แบบขยายห้องน้ำ

DRAWING FOR CONSTRUCTION

DRAW BY :	CHECKER :	REVISION :
Weerayuth L.	Akapatr C.	-


SCALE :	DRAWING NO.
1 : 100	SN-20
DATE : 20-10-2024	
FILE NAME :	JOB NO.

REVISION	DESCRIPTION


GERNERAL NOTE
DO NOT SCALE DRAWING ALL MEASUREMENT MUST BE
CHECKED AT THE SIDE BY THE CONTRACTOR
ALL DESIGN AND DRAWINGS ARE THE PROPERTY OF
MARCHTEN CO.,LTD
AND NOT BE USED WITH OUT THEIR WRITTEN PERMISSION

ARCHITECTURE / INTERIOR


บริษัท มาร์ชเทน จำกัด
403 ซ.พัฒนาการ 50 สวนหลวง กรุงเทพมหานคร 10250

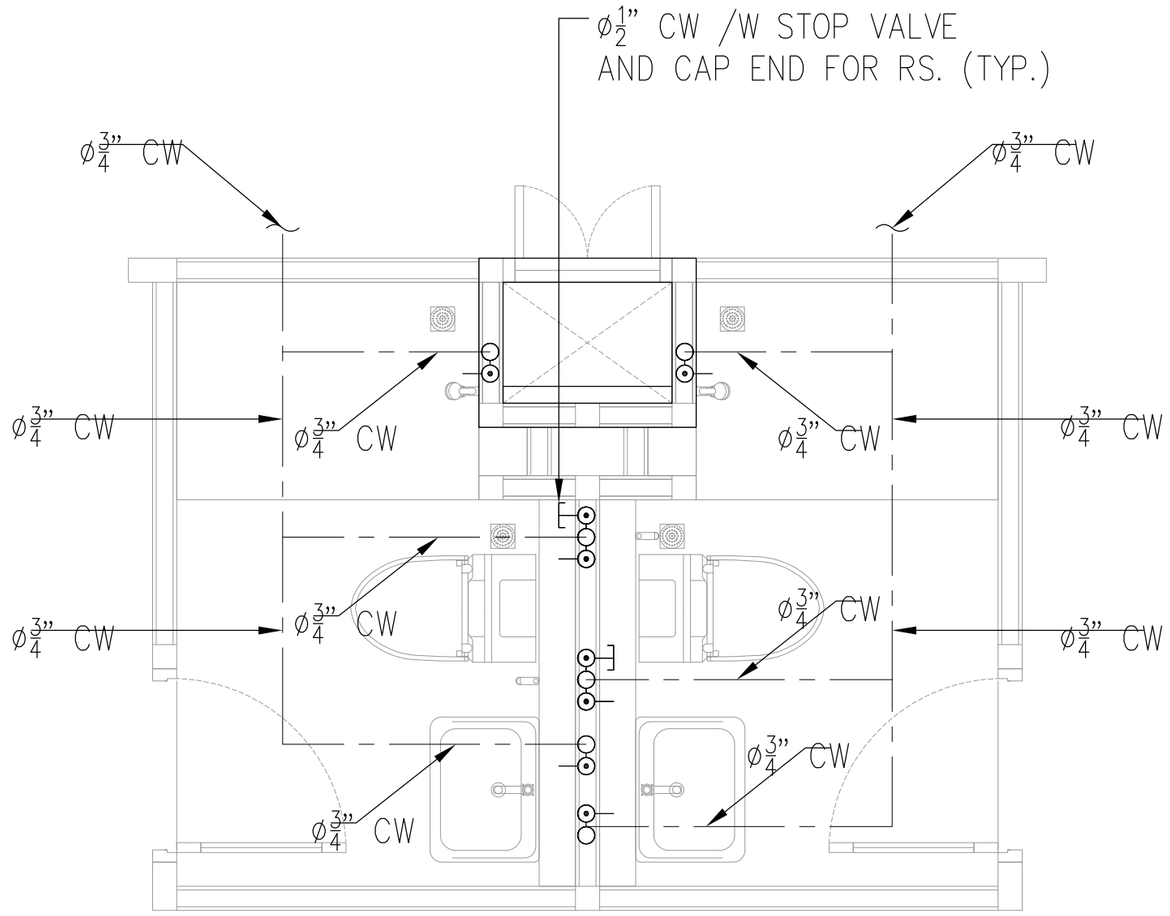

ผังระบบท่อน้ำประปา

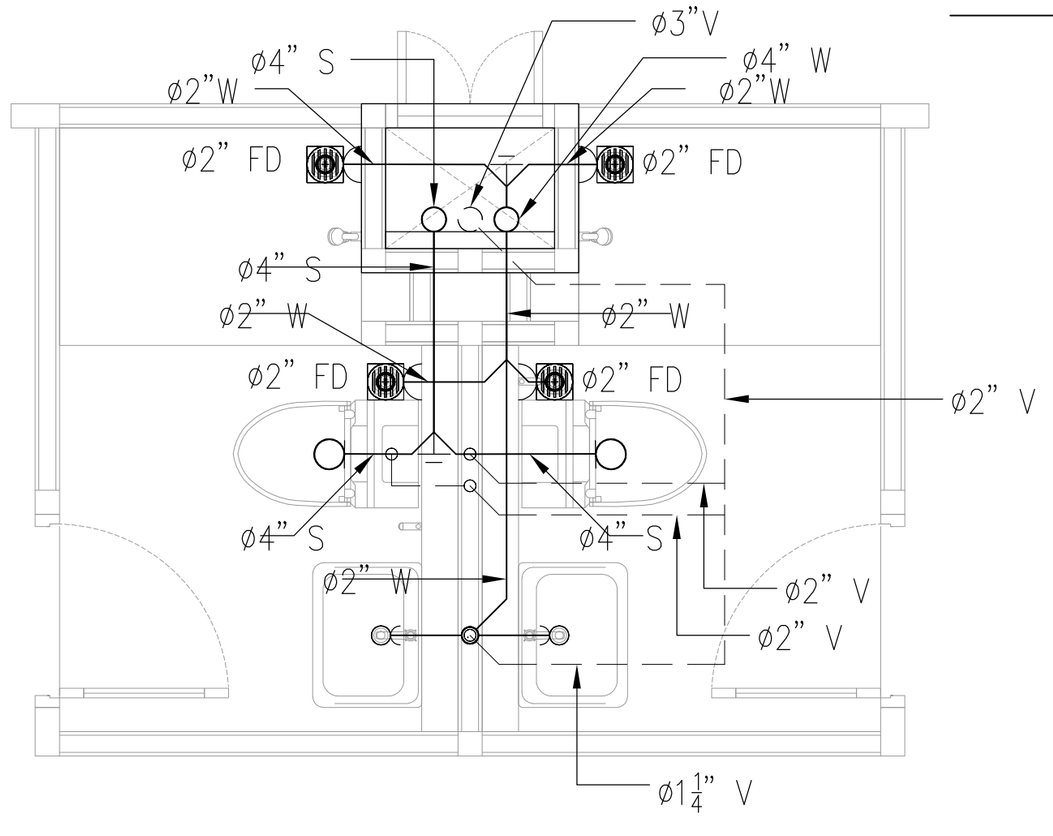

ผังระบบท่อน้ำโสโครก ท่อน้ำเสีย และท่อระบายอากาศ

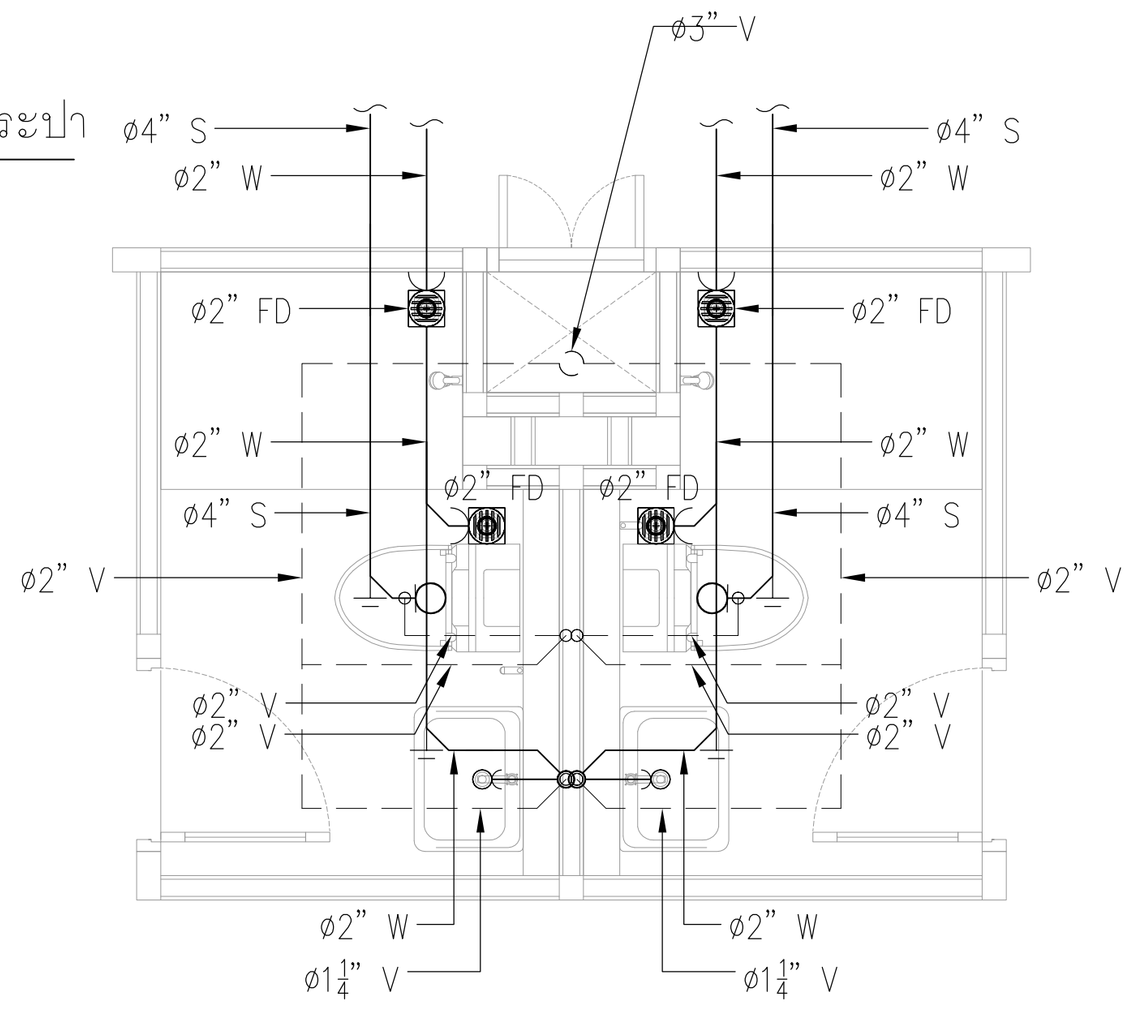

ผังระบบท่อน้ำโสโครก ท่อน้ำเสีย และท่อระบายอากาศ

แบบขยายห้องน้ำ WC-2

SCALE 1:25

PROJECT NUMBER : VC2023-024

PROJECT

MACHI RESIDENCES

อาคารพักอาศัยรวม ค.ส.ล 7 ชั้น

OWNER

บริษัท ฤทธิกร ลิฟวิ่ง จำกัด

ARCHITECT :

อัคคะภัทร์ จิระอารียบุตร ส-สถ.3040

403 ซ.พัฒนาการ 50 พัฒนาการ

กรุงเทพมหานคร 10250

INTERIOR DESIGNER :

-

STRUCTURAL ENGINEER :

นายพงษ์ธวิทย์ คทาวุธเจริญกุล ลย.12291

ELECTRICAL ENGINEER :

นายภาคภูมิ คำพิทูรย์ ลฟก.5587

MECHANICAL ENGINEER :

SANITARY ENGINEER :

นส.อรวรรณ พลตรี ลส.134

DRAWING TITLE

แบบขยายห้องน้ำ

DRAWING FOR CONSTRUCTION

DRAW BY :	CHECKER :	REVISION :
Weerayuth L.	Akapatr C.	–


SCALE : 1 : 100	DRAWING NO. SN-21
DATE : 20-10-2024	
FILE NAME :	JOB NO.

REVISION	DESCRIPTION

GERNERAL NOTE
DO NOT SCALE DRAWING ALL MEASUREMENT MUST BE
CHECKED AT THE SIDE BY THE CONTRACTOR
ALL DESIGN AND DRAWINGS ARE THE PROPERTY OF
MARCHTEN CO.,LTD.
AND NOT BE USED WITH OUT THEIR WRITTEN PERMISSION


ARCHITECTURE / INTERIOR

บริษัท มาร์ชเทน จำกัด
403 ซ.พัฒนาการ 50 สวนหลวง กรุงเทพมหานคร 10250

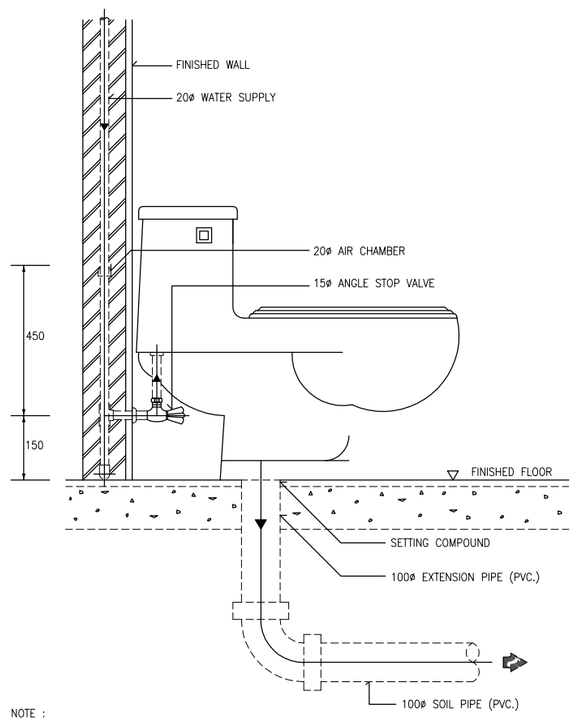


NOTE :
1. ALL EXPOSED PIPES AND FITTINGS SHALL BE CHROME-PLATED.
2. CHROME-PLATED ESCUTCHEON SHALL BE INSTALLED AT EVERY PIPES THAT PASS THROUGH WALL.

WATER CLOSET (ELEVATION)

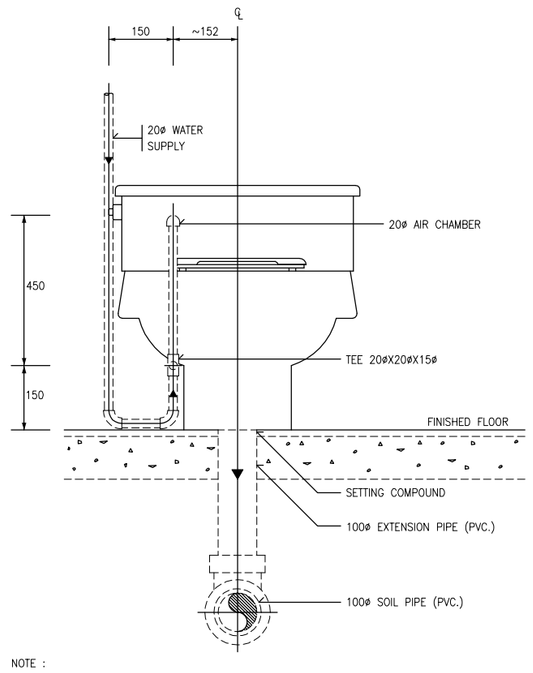


NOTE :
1. ALL EXPOSED PIPES AND FITTINGS SHALL BE CHROME-PLATED.
2. CHROME-PLATED ESCUTCHEON SHALL BE INSTALLED AT EVERY PIPES THAT PASS THROUGH WALL.

WATER CLOSET (FRONT VIEW)

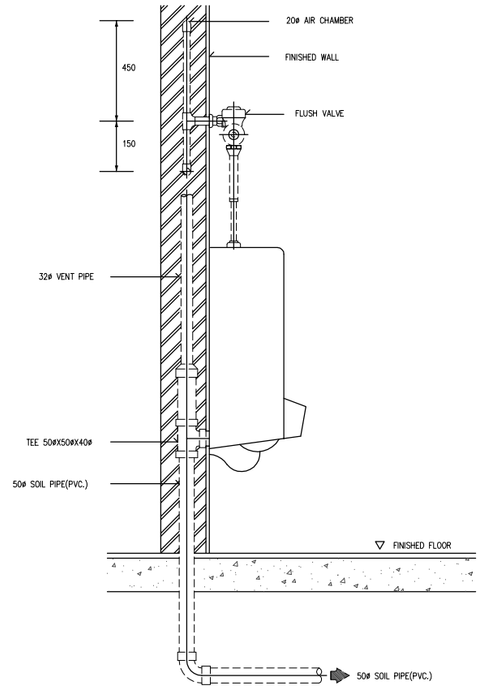


NOTE :
1. ALL EXPOSED PIPES AND FITTINGS SHALL BE CHROME-PLATE.
2. CHROME-PLATED ESCUTCHEON SHALL BE INSTALLED AT EVERY PIPES THAT PASS THROUGH WALL.

URINAL FLUSH VALVE (ELEVATION)

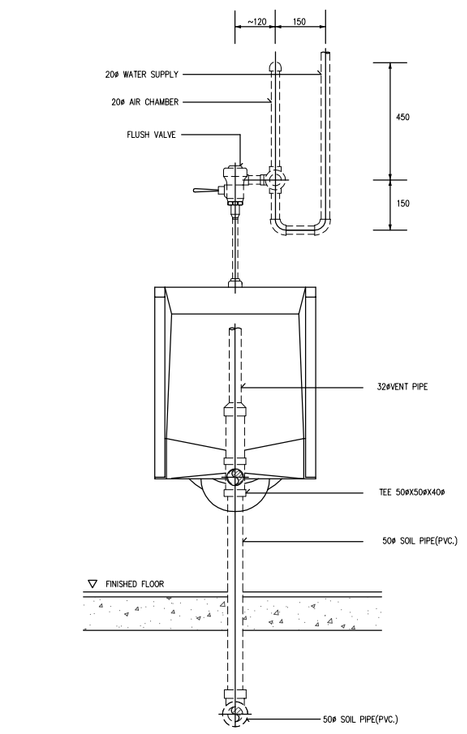


NOTE :
1. ALL EXPOSED PIPES AND FITTINGS SHALL BE CHROME-PLATE.
2. CHROME-PLATED ESCUTCHEON SHALL BE INSTALLED AT EVERY PIPES THAT PASS THROUGH WALL.

URINAL FLUSH VALVE (FRONT VIEW)

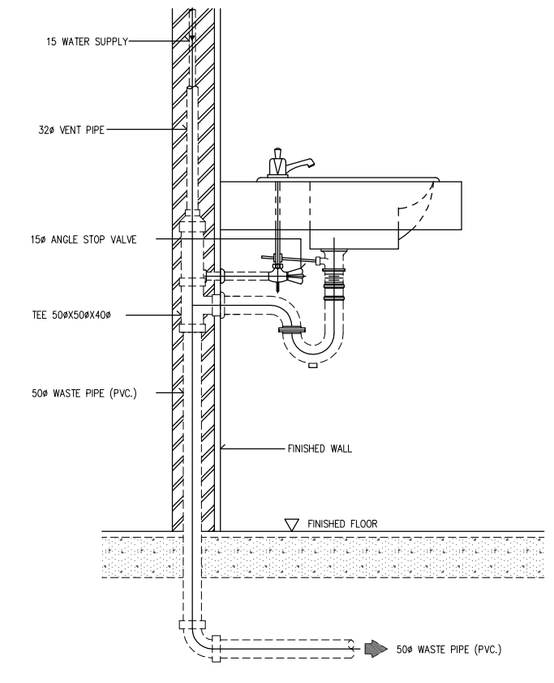


NOTE : 1. ALL EXPOSED PIPES AND FITTINGS SHALL BE CHROME-PLATED.
2. CHROME-PLATED ESCUTCHEON SHALL BE INSTALLED AT EVERY PIPES THAT PASS THROUGH WALL.

LAVATORY (ELEVATION)

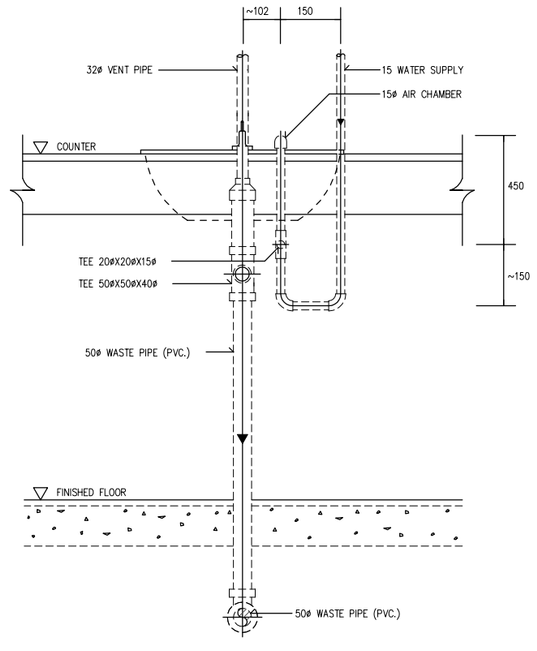


NOTE : 1. ALL EXPOSED PIPES AND FITTINGS SHALL BE CHROME-PLATED.
2. CHROME-PLATED ESCUTCHEON SHALL BE INSTALLED AT EVERY PIPES THAT PASS THROUGH WALL.

LAVATORY (FRONT VIEW)

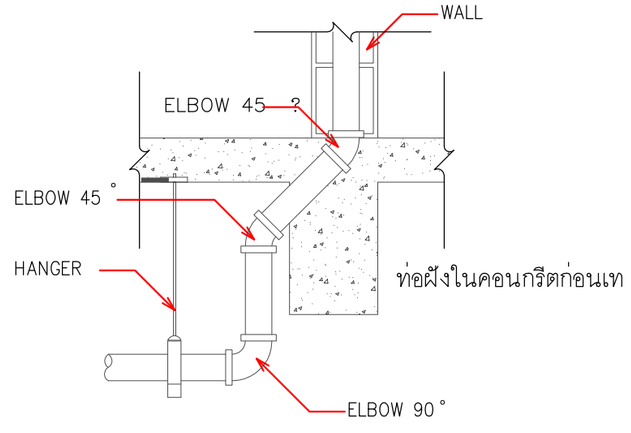

PIPE EMBED BEAM

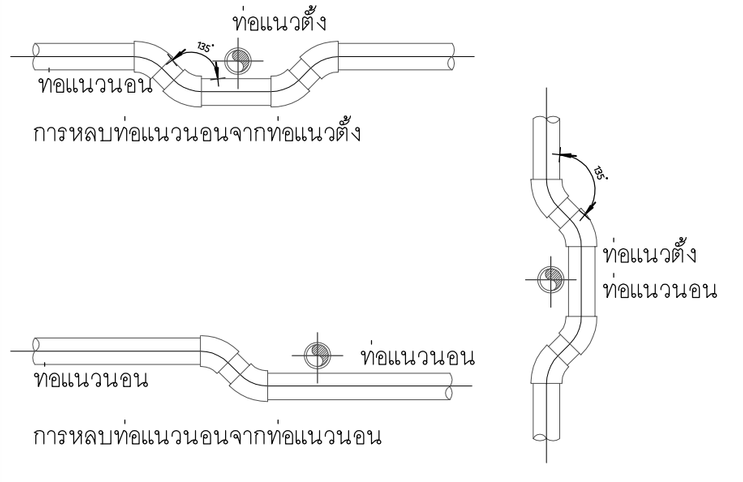

PIPE CROSS PIPE

PROJECT NUMBER : VC2023-024

PROJECT

MACHI RESIDENCES

อาคารพักอาศัยรวม ค.ส.ล 7 ชั้น

OWNER

บริษัท ฤทธิกร ลิฟวิ่ง จำกัด

ARCHITECT :

อัคคะภัทร์ จิระอารียบุตร ส-สถ.3040

403 ซ.พัฒนาการ 50 พัฒนาการ

กรุงเทพมหานคร 10250

INTERIOR DESIGNER :

-

STRUCTURAL ENGINEER :

นายพงษ์ธวิทย์ คทาวุธเจริญกุล ลย.12291

ELECTRICAL ENGINEER :

นายภาคภูมิ คำพิทรย์ ลฟท.5587

MECHANICAL ENGINEER :

SANITARY ENGINEER :

นส.อรวรรณ พลตรี ลส.134

DRAWING TITLE

แบบมาตรฐานงานวิศวกรรมสุขาภิบาล 1

DRAWING FOR CONSTRUCTION

DRAW BY :	CHECKER :	REVISION :
Weerayuth L.	Akapatr C.	-


SCALE : 1 : 100	DRAWING NO. SN-22
DATE : 20-10-2024	
FILE NAME :	JOB NO.

REVISION	DESCRIPTION


GERNERAL NOTE
DO NOT SCALE DRAWING ALL MEASUREMENT MUST BE
CHECKED AT THE SIDE BY THE CONTRACTOR
ALL DESIGN AND DRAWINGS ARE THE PROPERTY OF
MARCHTEN CO.,LTD
AND NOT BE USED WITH OUT THEIR WRITTEN PERMISSION

ARCHITECTURE / INTERIOR


บริษัท มาร์ชเทน จำกัด
403 ซ.พัฒนาการ 50 สวนหลวง กรุงเทพมหานคร 10250

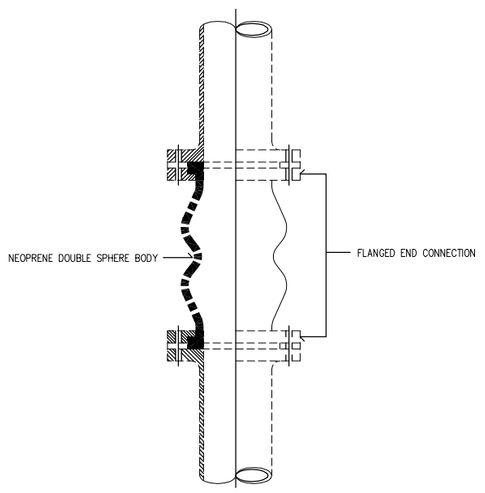


FLEXIBLE JOINT TYPE

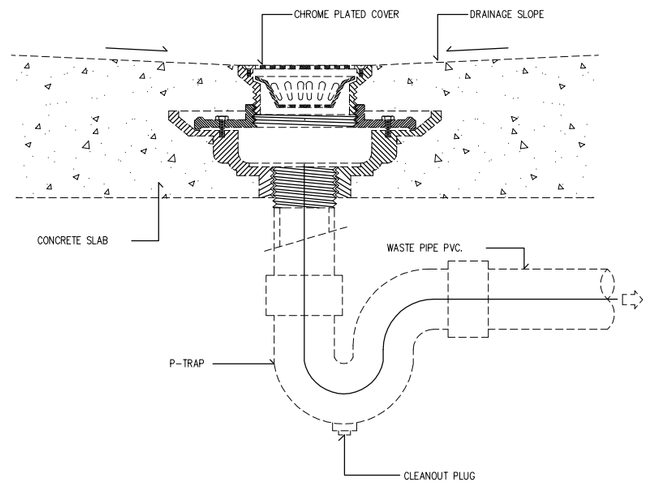


FLOOR DRAIN

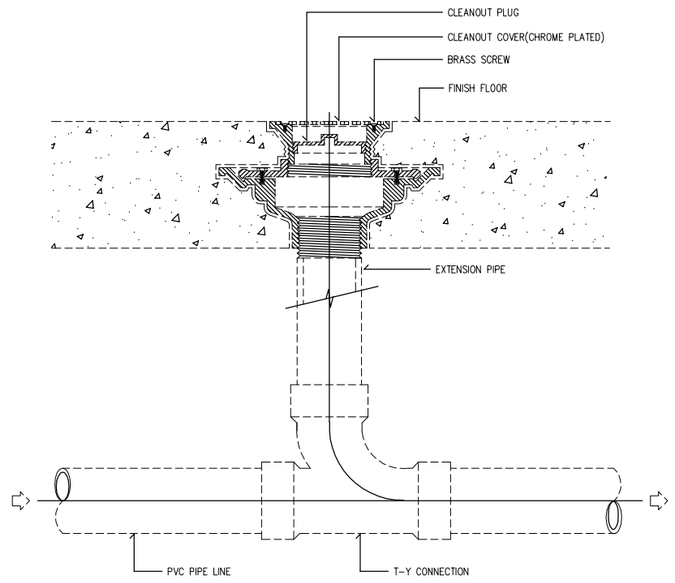


FLOOR CLEANOUT

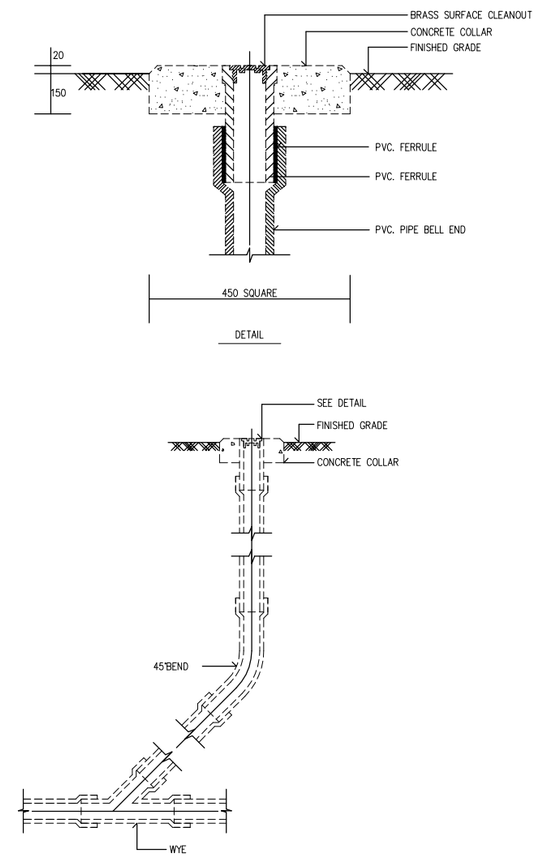


SURFACE CLEANOUT

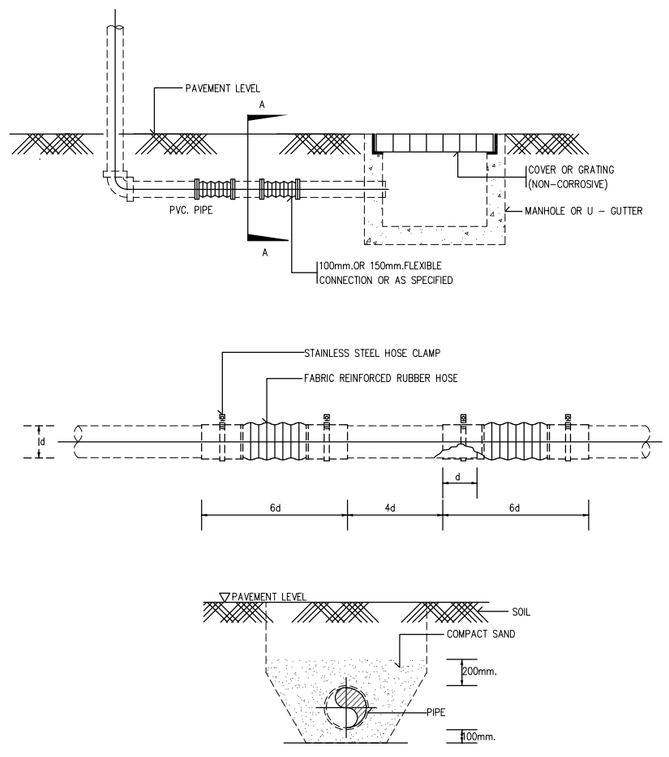

DRAINAGE FLEXIBLE CONNECTION

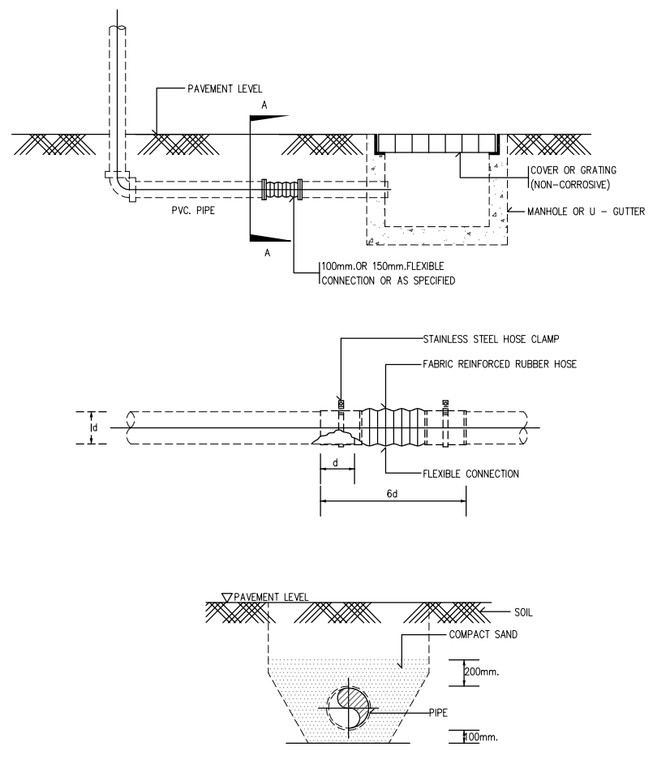


DRAINAGE FLEXIBLE CONNECTION

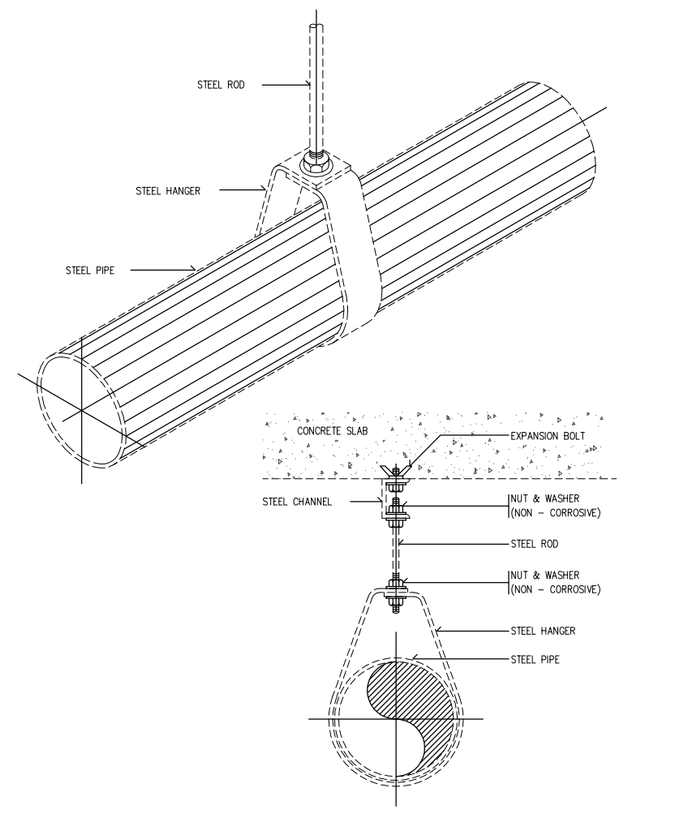

NOTE: ALL STEEL PARTS SHALL BE PAINTED WITH 2 COATS OF ANTI-RUST PAINT AND 1 COAT OF FINISHED PAINT OR AS SPECIFIED.

PIPE HANGER
FOR SIZE UP TO 50 mm (2"ø)

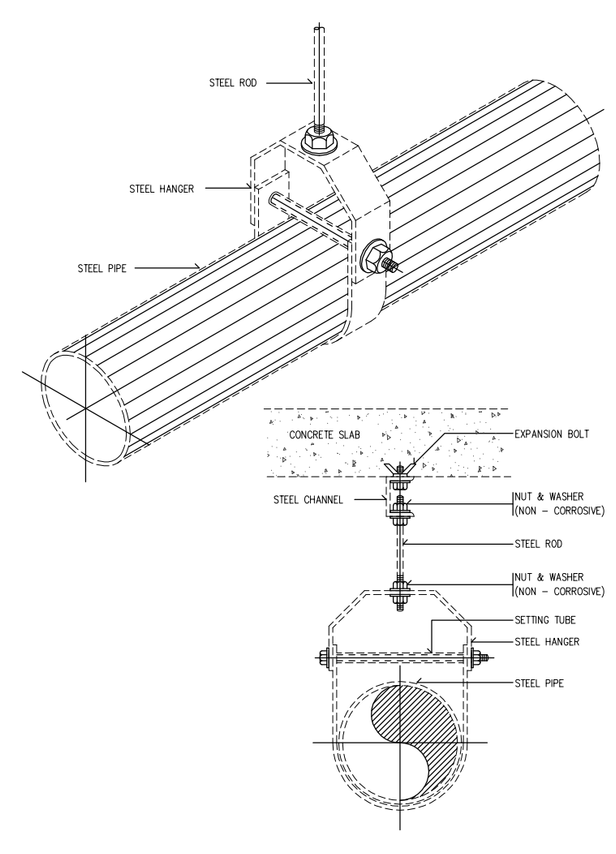

NOTE: ALL STEEL PARTS SHALL BE PAINTED WITH 2 COATS OF ANTI-RUST PAINT AND 1 COAT OF FINISHED PAINT OR AS SPECIFIED.

PIPE HANGER FOR
SIZE 65 mm (21/2"ø) AND LARGER

PROJECT NUMBER : VC2023-024

PROJECT

MACHI RESIDENCES

อาคารพักอาศัยรวม ค.ส.ล 7 ชั้น

OWNER

บริษัท ฤทธิกร ลิฟวิ่ง จำกัด

ARCHITECT :

อัคคะภัทร์ จิระอารียบุตร ส-สถ.3040

403 ซ.พัฒนาการ 50 พัฒนาการ

กรุงเทพมหานคร 10250

INTERIOR DESIGNER :

-

STRUCTURAL ENGINEER :

นายพงษ์ธวิทย์ คทาวุธเจริญกุล ลย.12291

ELECTRICAL ENGINEER :

นายภาคภูมิ คำพิทูรย์ ลฟก.5587

MECHANICAL ENGINEER :

SANITARY ENGINEER :

พล.อรวรรณ พลตรี ลส.134

DRAWING TITLE

แบบมาตรฐานงานวิศวกรรมสุขาภิบาล 2

DRAWING FOR CONSTRUCTION

DRAW BY :	CHECKER :	REVISION :
Weerayuth L.	Akapatr C.	-

SCALE :	DRAWING NO.
1 : 100	SN-23
DATE : 20-10-2024	
FILE NAME :	JOB NO.

REVISION	DESCRIPTION


GERNERAL NOTE


DO NOT SCALE DRAWING ALL MEASUREMENT MUST BE **CHECKED AT THE SIDE BY THE CONTRACTOR**

ALL DESIGN AND DRAWINGS ARE THE PROPERTY OF MARCHTEN CO.,LTD **AND NOT BE USED WITH OUT THEIR WRITTEN PERMISSION**

ARCHITECTURE / INTERIOR


บริษัท มาร์ชเทน จำกัด
403 ซ.พัฒนาการ 50 แขวนหลวง กรุงเทพมหานคร 10250

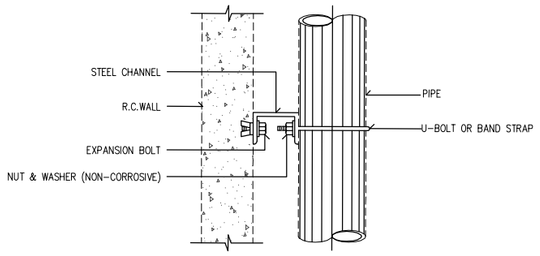


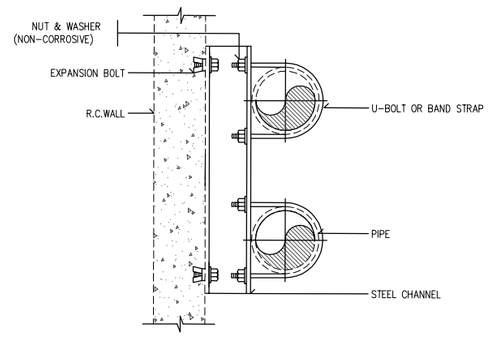

NOTE : ALL STEEL PARTS SHALL BE PAINTED WITH 2 COATS OF ANTI-RUST PAINT AND 1 COAT OF FINISHED PAINT OR AS SPECIFIED.


PIPE SUPPORT TO WALL

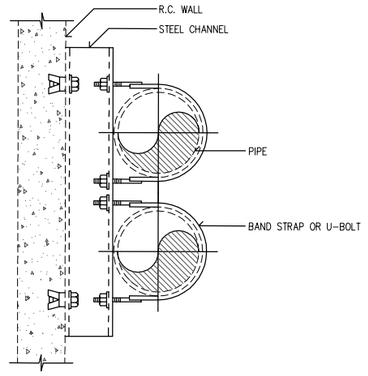


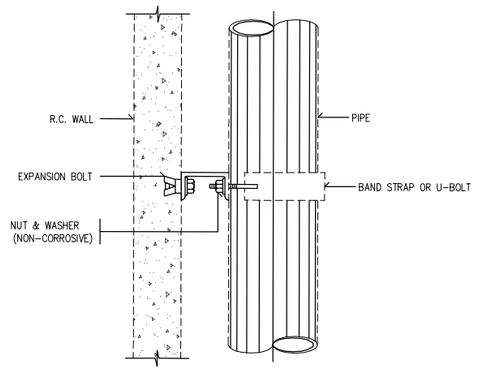

NOTE : 1. ALL STEEL PARTS SHALL BE PAINTED WITH 2 COATS OF ANTI-RUST PAINT AND 1 COAT OF FINISHED PAINT OR AS SPECIFIED.
2. A DIRT LEG AND BLOW-OFF VALVE SHALL BE PROVIDED ON EVERY RISERS


PIPE RISER

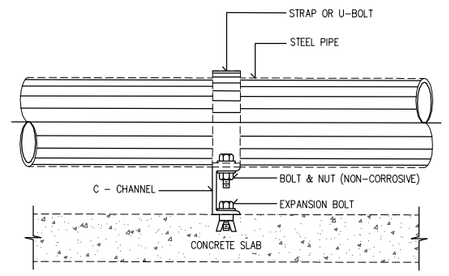

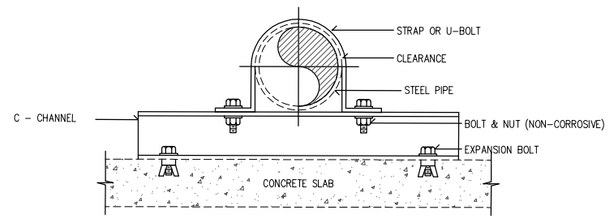


NOTE :
ALL STEEL PARTS SHALL BE PAINTED WITH 2 COATS OF ANTI-RUST PAINT AND 1 COAT OF FINISHED PAINT OR AS SPECIFIED.

PIPE SUPPORT TO FLOOR

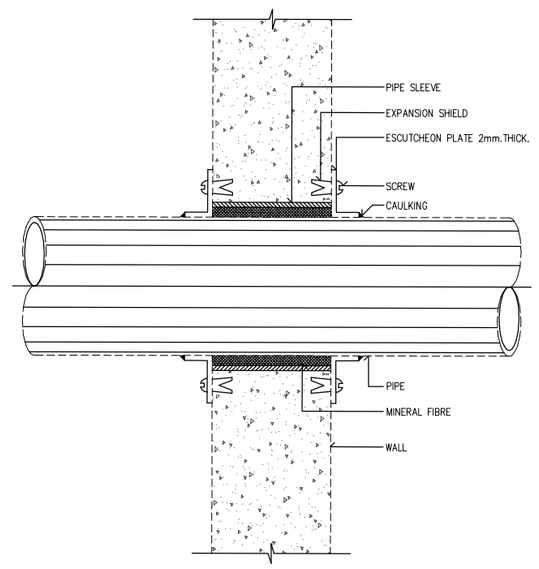


NOTE : ESCUTCHEON PLATE SEE SPECIFICATION

PIPE SLEEVE THROUGH INTERIOR WALL

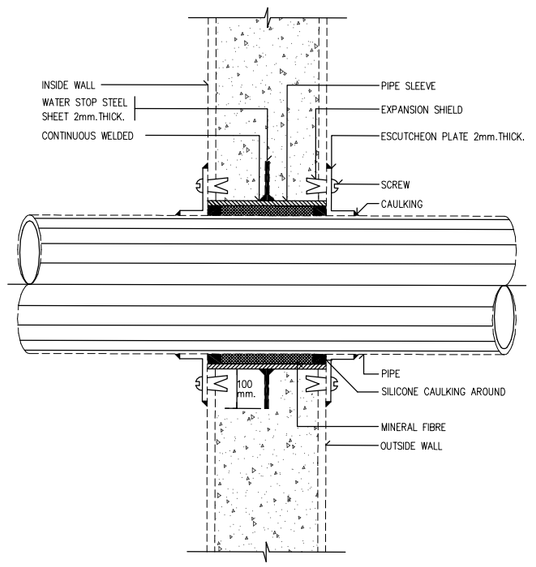


NOTE : ESCUTCHEON PLATE SEE SPECIFICATION

PIPE SLEEVE THROUGH OUTSIDE WALL

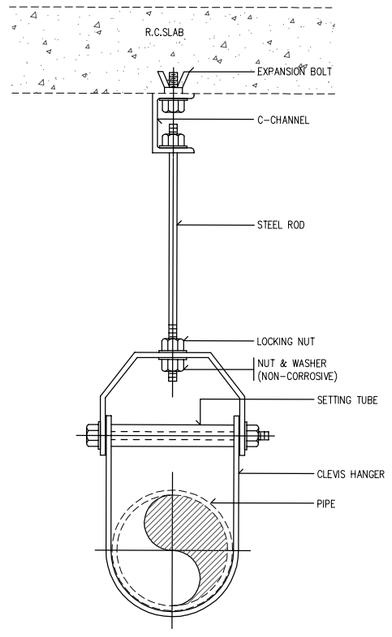


NOTE : ALL STEEL PARTS SHALL BE PAINTED WITH 2 COATS OF ANTI-RUST PAINT AND 1 COAT OF FINISHED PAINT OR AS SPECIFIED.

PIPE HANGER

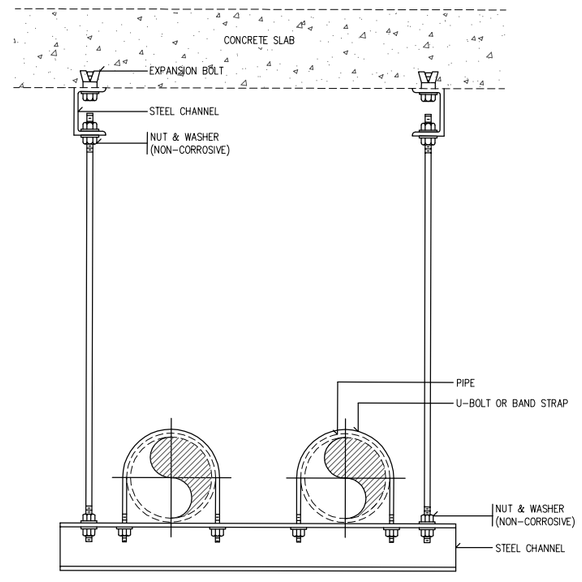

NOTE : ALL STEEL PARTS SHALL BE PAINTED WITH 2 COATS OF ANTI-RUST PAINT AND 1 COAT OF FINISHED PAINT OR AS SPECIFIED.

PIPE HANGER

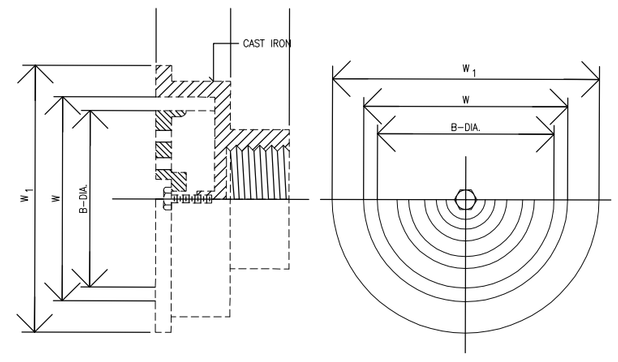

PIPE SIZE		B	H	H1	W	W1	FREE AREA
in.	in.	mm.	mm.	mm.	mm.	mm.	cm.2
1 1/2	40	105	27	28	121	140	114
2	50	105	27	28	121	140	114
2 1/2	65	105	27	36	132	145	136
3	80	156	27	35	182	200	260
4	100	165	30	40	181	198	257
6	150	184	35	45	220	237	380

AIR VENT CAP (VTA WALL TYPE)

PROJECT NUMBER : VC2023-024

PROJECT

MACHI RESIDENCES

อาคารพักอาศัยรวม ค.ส.ล 7 ชั้น

OWNER

บริษัท ฤทธิกร ลิฟวิ่ง จำกัด

ARCHITECT :

อัคคะภัทร์ จิระอารีย์บุตร ส-สถ.3040

403 ซ.พัฒนาการ 50 พัฒนาการ

กรุงเทพมหานคร 10250

INTERIOR DESIGNER :

-

STRUCTURAL ENGINEER :

นายพงษ์ธวิทย์ คทาวุธเจริญกุล ลย.12291

ELECTRICAL ENGINEER :

นายภาคภูมิ คำพิทรย์ ลฟก.5587

MECHANICAL ENGINEER :

SANITARY ENGINEER :

พล.อรวรรณ พลตรี ลส.134

DRAWING TITLE

แบบมาตรฐานงานวิศวกรรมสุขาภิบาล 3

DRAWING FOR CONSTRUCTION

DRAW BY :	CHECKER :	REVISION :
Weerayuth L.	Akapatr C.	–

SCALE :	DRAWING NO.
1 : 100	SN-24
DATE : 20-10-2024	
FILE NAME :	JOB NO.

REVISION	DESCRIPTION


GERNERAL NOTE

DO NOT SCALE DRAWING ALL MEASUREMENT MUST BE **CHECKED AT THE SIDE BY THE CONTRACTOR**


ALL DESIGN AND DRAWINGS ARE THE PROPERTY OF MARCHTEN CO.,LTD **AND NOT BE USED WITH OUT THEIR WRITTEN PERMISSION**

ARCHITECTURE / INTERIOR


บริษัท มาร์ชเทน จำกัด
403 ซ.พัฒนาการ 50 สวนหลวง กรุงเทพมหานคร 10250

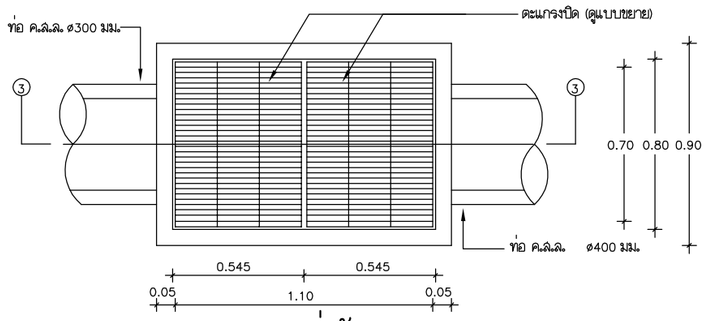


แบบขยายบ่อดักขยะ

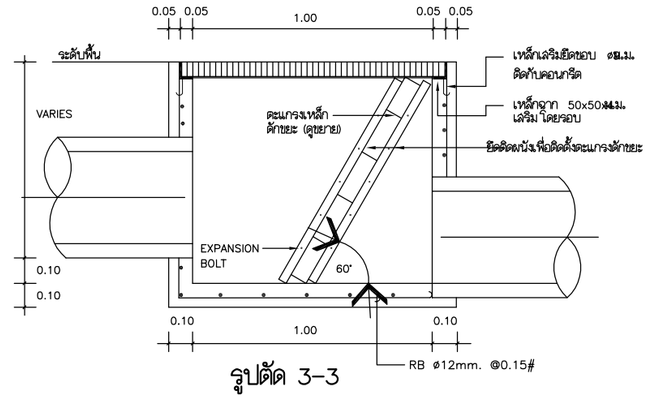


รูปตัด 3-3

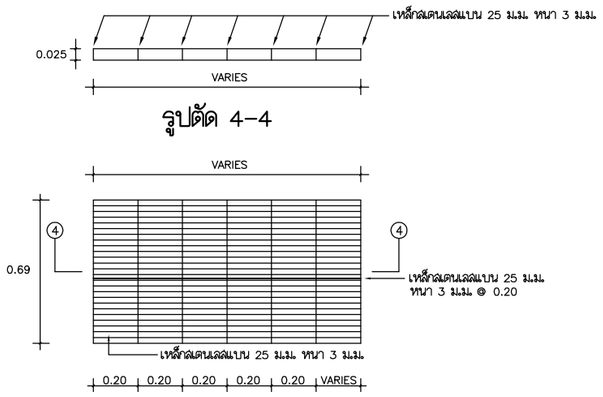


รูปตัด 1-1

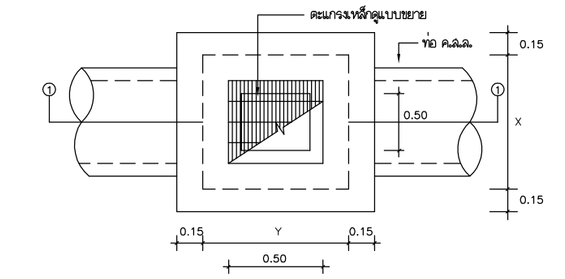


แบบขยายบ่อพักท่อระบายน้ำ ค.ส.ล. แบบที่1 (MH1)

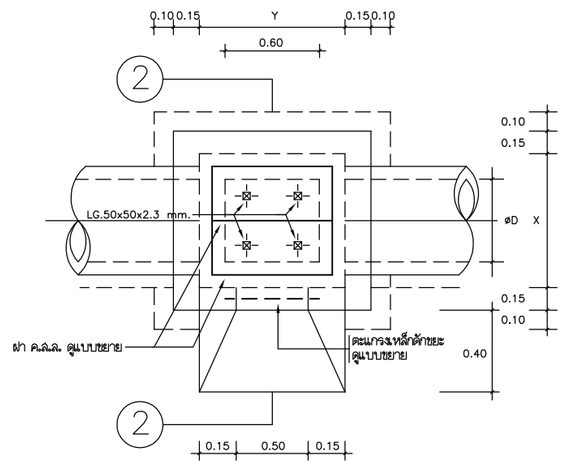

แบบขยายบ่อพักท่อระบายน้ำ ค.ส.ล. แบบที่2 (MH2)

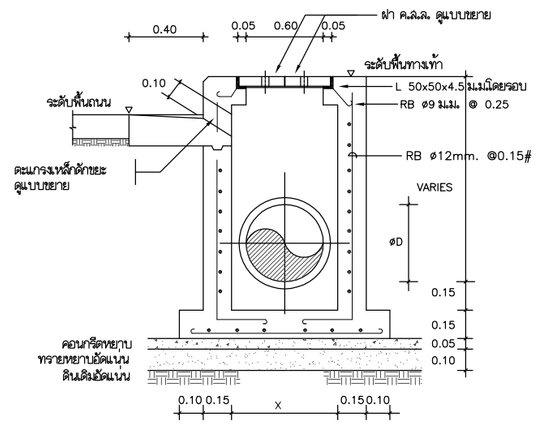

รูปตัด 2-2

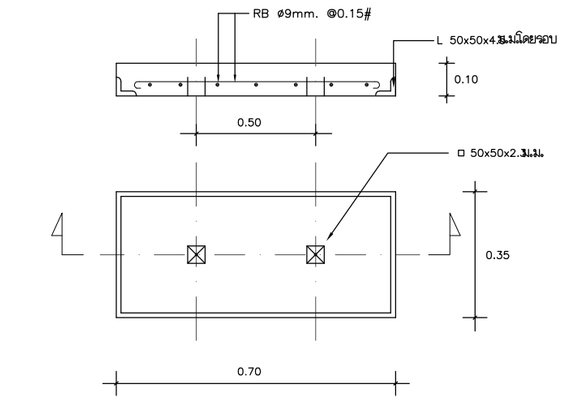

แบบขยายฝาบ่อพักท่อระบายน้ำ ค.ส.ล.

ขนาดเส้นผ่าศูนย์กลางท่อ (เมตร)	X (เมตร)	Y (เมตร)
0.20-0.30	0.50	0.50
0.40	0.60	0.60
0.50-0.60	0.80	0.80
0.80	1.00	1.00
1.00	1.30	1.00

รูปตัด 1-1